

FOUNDATION PLAN NOTES:

1. FINISH FLOOR ELEVATION = 0'-0". UNLESS NOTED OTHERWISE, REFER TO THE CIVIL DRAWINGS FOR ADDITIONAL INFORMATION.
2. REFER TO THE ARCHITECTURAL DRAWINGS FOR EXACT LOCATIONS OF FLOOR RECESSES, DROPS AND SLOPES NOT DIMENSIONED ON PLAN. REFER TO MECHANICAL, ELECTRICAL, AND PLUMBING DRAWINGS FOR LOCATION AND DIMENSIONS OF FLOOR PENETRATIONS NOT DIMENSIONED ON PLAN. CONTRACTOR TO COORDINATE.
3. CENTERLINES OF FOUNDATIONS NOT SPECIFICALLY LOCATED ON PLAN BY NOTE OR DIMENSION SHALL BE LOCATED AS FOLLOWS:
 - A. SUPPORTING FREESTANDING COLUMNS:
CENTERLINES OF COLUMN.
 - B. SUPPORTING GRADEBEAMS AND WALLS:
CENTERLINE OF GRADEBEAM OR WALL IN ONE DIRECTION. GRID OR AS NOTED IN OTHER DIRECTION. AT CORNER CONDITIONS:
CENTERLINES OF GRADEBEAMS OR WALLS.
 - C. COLUMNS EMBEDDED IN GRADEBEAMS OR WALLS (PILASTERS): CENTERLINES OF THE COLUMN.
4. REF. S5.0 FOR ADD'L SLAB-ON-GRADE INFORMATION
5.  = 8" CMU WALLS
6.  = 8" CMU SHEAR WALL



STEEL COLUMN NOTES:

DENOTES COLUMN MARK

STEEL COLUMN

CIP PLINTH

DENOTES BASEPLATE MARK

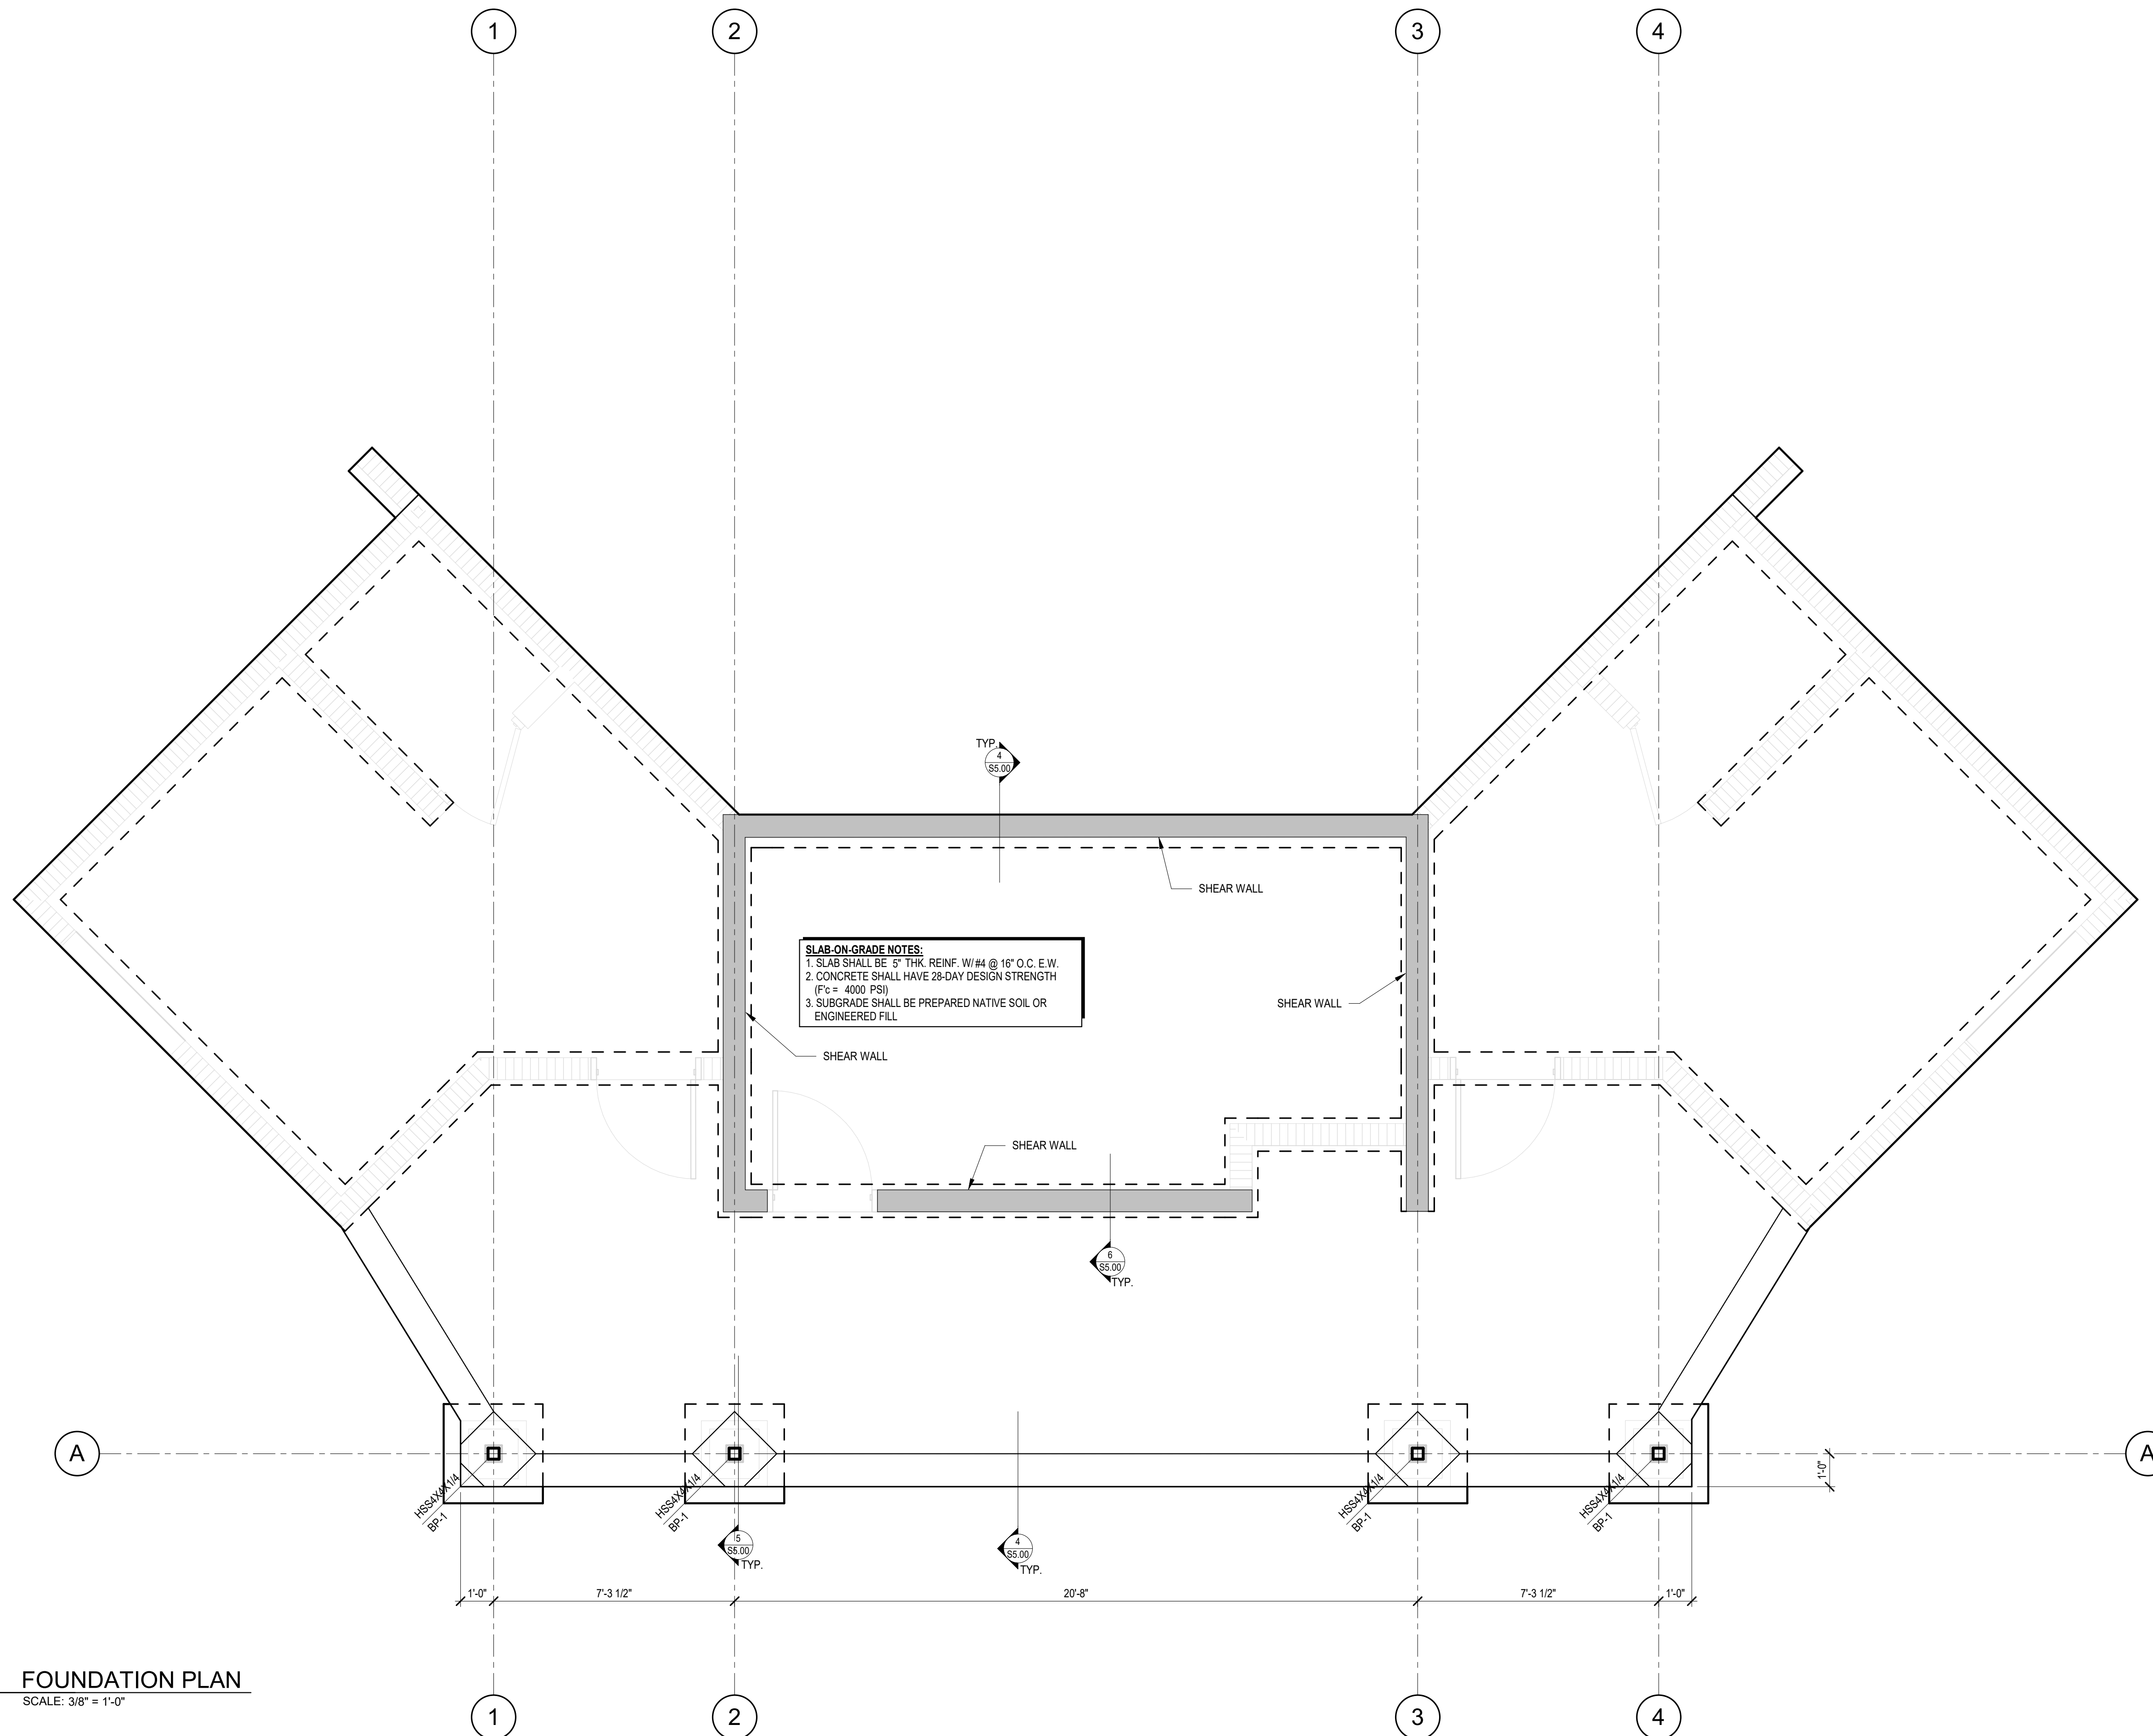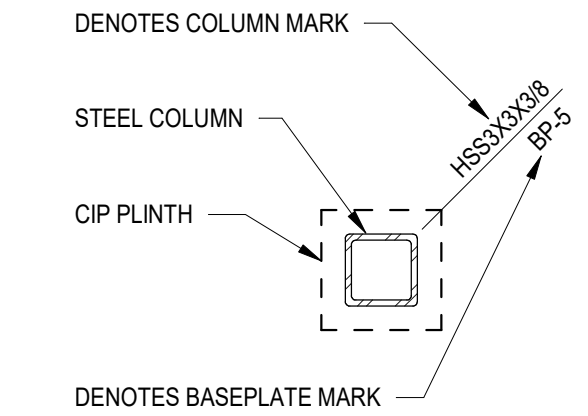

1 FOUNDATION PLAN

SCALE: 3/8" = 1'-0"



**CITY OF DADE CITY
PARK RESTROOMS**

37800 CHURCH AVENUE DADE CITY, FL 33525

[illegible]

PROJECT NO:

23005.001

DATE: 10/19/2023

DESIGNED BY: _____

DRAWN BY: _____

CHECKED BY: _____

DRAWING TITLE:

FOUNDATION PLAN

SHEET NO:

S1.00

PERMIT BID SET 10-19-2023