


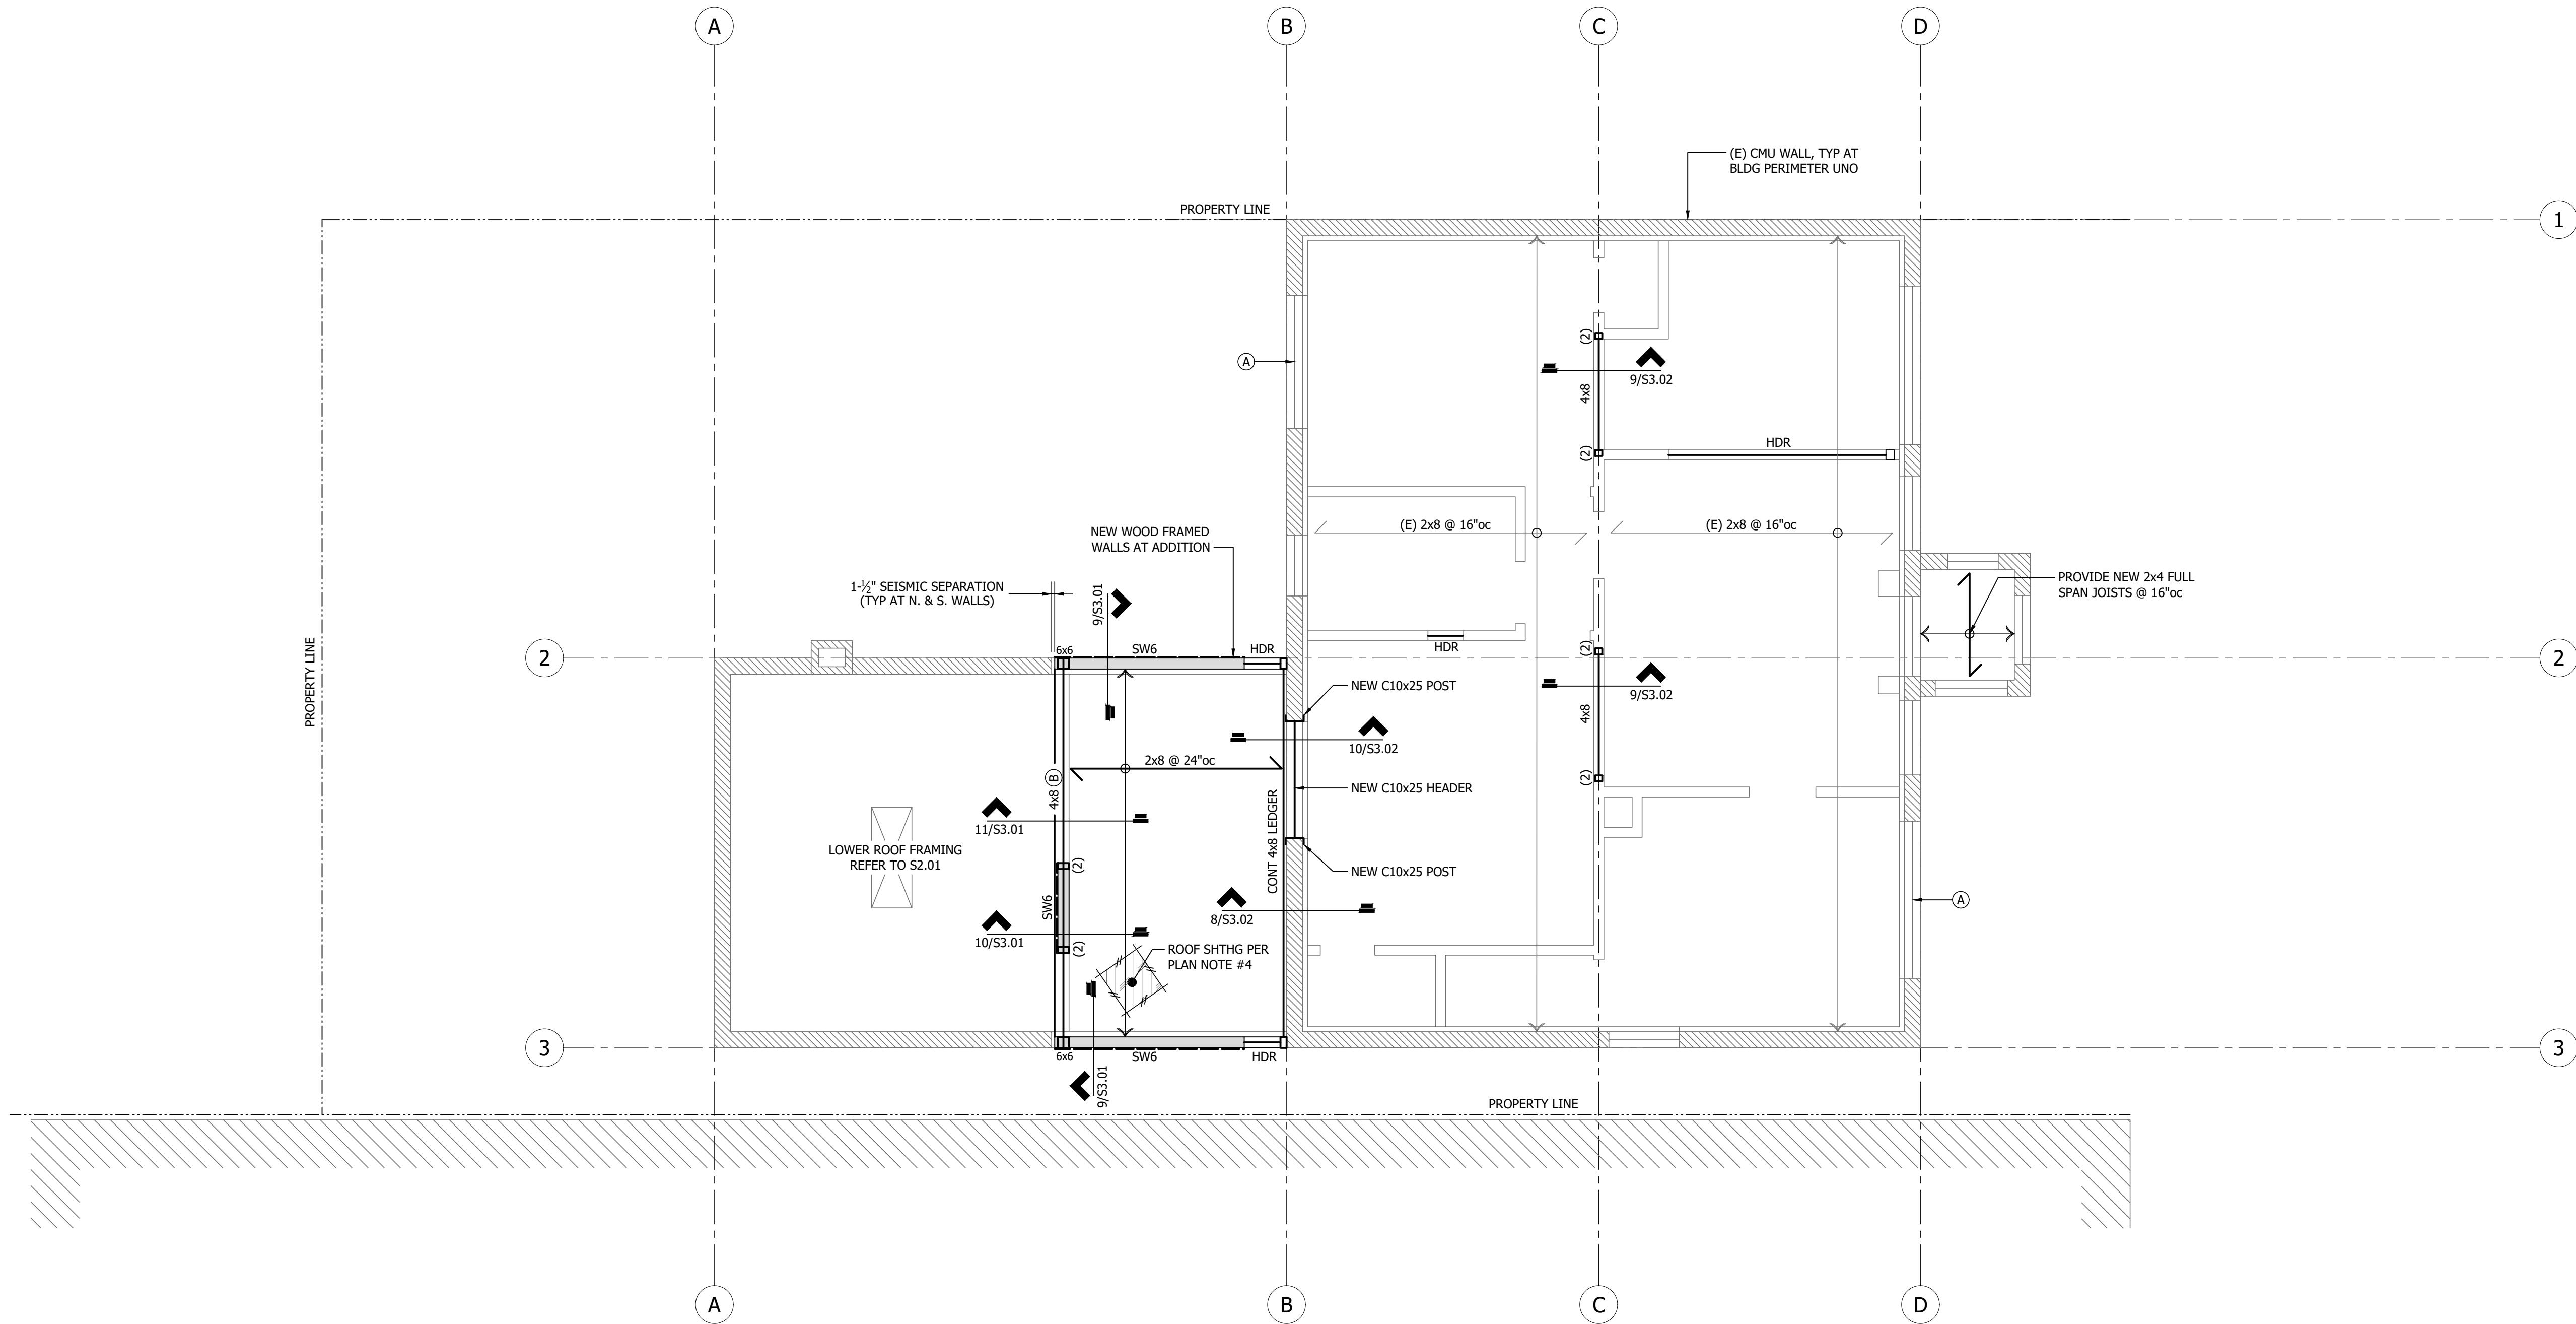

UPPER ROOF FRAMING PLAN


SCALE: 1/4" = 1'-0"

UPPER ROOF FRAMING PLAN NOTES

- REFER TO ARCHITECTURAL DRAWINGS FOR ALL DIMENSIONS, ROOF SLOPES & ANGLES.
- PLAN INDICATES FRAMING AT ROOF LEVEL AND WALLS/POSTS BELOW.
- EXISTING CONDITIONS ARE ASSUMED AND SHOULD BE VERIFIED BY THE CONTRACTOR. WHERE DISCOVERED CONDITIONS VARY FROM THOSE SHOWN ON PLANS, CONTRACTOR SHALL CONTACT THE ENGINEER BEFORE PROCEEDING WITH CONSTRUCTION.
- NEW ROOF SHEATHING SHALL BE 19/32" APA RATED SHEATHING (32/16). ATTACH SHEATHING WITH 8d NAILS @ 6"OC TO ALL FRAMED PANEL EDGES AND OVER SHEARWALLS, AND @ 12"OC TO ALL INTERMEDIATE/FIELD FRAMING. PLACE LONG DIRECTION OF PLYWOOD PERPENDICULAR TO JOIST FRAMING DIRECTION, STAGGER PANEL JOINTS.
- ALL BEAMS SHALL BE FLUSH FRAMED AND ALL HEADERS DROPPED, UNO. REFER TO GENERAL STRUCTURAL NOTES FOR ADDITIONAL CONNECTION MEMBER INFORMATION NOT SHOWN PER PLAN.
- PROVIDE SOLID BEARING UNDER ALL POINT LOADS ABOVE. TYPICAL HEADERS OVER DOOR AND WINDOW OPENINGS (**HDR**) SHALL BE 4x6 MIN EXTERIOR, (2)2x6 MIN INTERIOR. UNLESS NOTED OTHERWISE, PROVIDE (1) FULL HEIGHT (KING) STUD AND (2) BEARING (TRIMMER) STUD AT EACH END OF BEAM/HEADER. NAIL MULTIPLE STUDS TOGETHER PER GENERAL STRUCTURAL NOTES.
- PROVIDE SIMPSON HARDWARE PCZ/EPCZ COLUMN TO BEAM CONNECTIONS, TYPICAL UNO. REFER TO STRUCTURAL GENERAL NOTES FOR ADDITIONAL CONNECTION MEMBER INFORMATION.
- TYPICAL STUD WALLS SHALL BE 2x6 @ 16"oc AT EXTERIOR WALLS AND 2x4's OR 2x6's @ 16"oc AT INTERIOR WALLS PER ARCH DRAWINGS, UNLESS NOTED OTHERWISE.
- REFER TO GENERAL STRUCTURAL NOTES AND TYPICAL DETAILS FOR ADDITIONAL REQUIREMENTS.

LEGEND

- SWX SHEARWALL w/ DESIGNATION PER SHEARWALL SCHEDULE
- NEW WOOD WALL FRAMING BELOW
- EXISTING WOOD WALL FRAMING BELOW
- EXISTING CMU WALL BELOW
- (x) NUMBER OF BUILT-UP STUDS

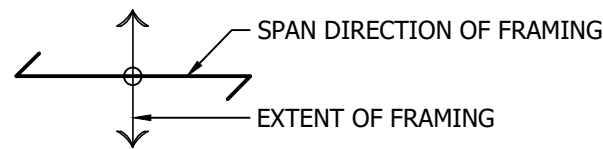

FOOTNOTES

- (A) REMOVE & REPLACE EXISTING STEEL LINTEL w/ 16x6x5/8 GALVANIZED ANGLE AS REQUIRED PER GENERAL STRUCTURAL NOTE #19, TYPICAL AT EAST & WEST WINDOW OPENINGS.
- (B) EXTEND 4x8 BEAM CONTINUOUS TO NORTH & SOUTH INTERSECTING WALLS

SUNDBERG
KENNEDY
LY-AU YOUNG
ARCHITECTS

1501 E MADISON, SUITE 205
SEATTLE WA 98122-4465
206.322.1130



ROICH
STRUCTURAL INC.

P.O. Box 38809 | Seattle, WA 98118
roichstructural.com | 206.745.2967

Official
Stamps:

Eng Family Homestead Renovation
611 8th Ave South, Seattle, WA 98104

FOR CONSTRUCTION

PERMIT SET

9/22/2023

UPPER ROOF FRAMING PLAN

2019

9/22/2023

RC

RC

Project number

Date

Project Manager

RC

RC

Drawn by

RC

Checked by

RC

S2.02

NTS

Scale