




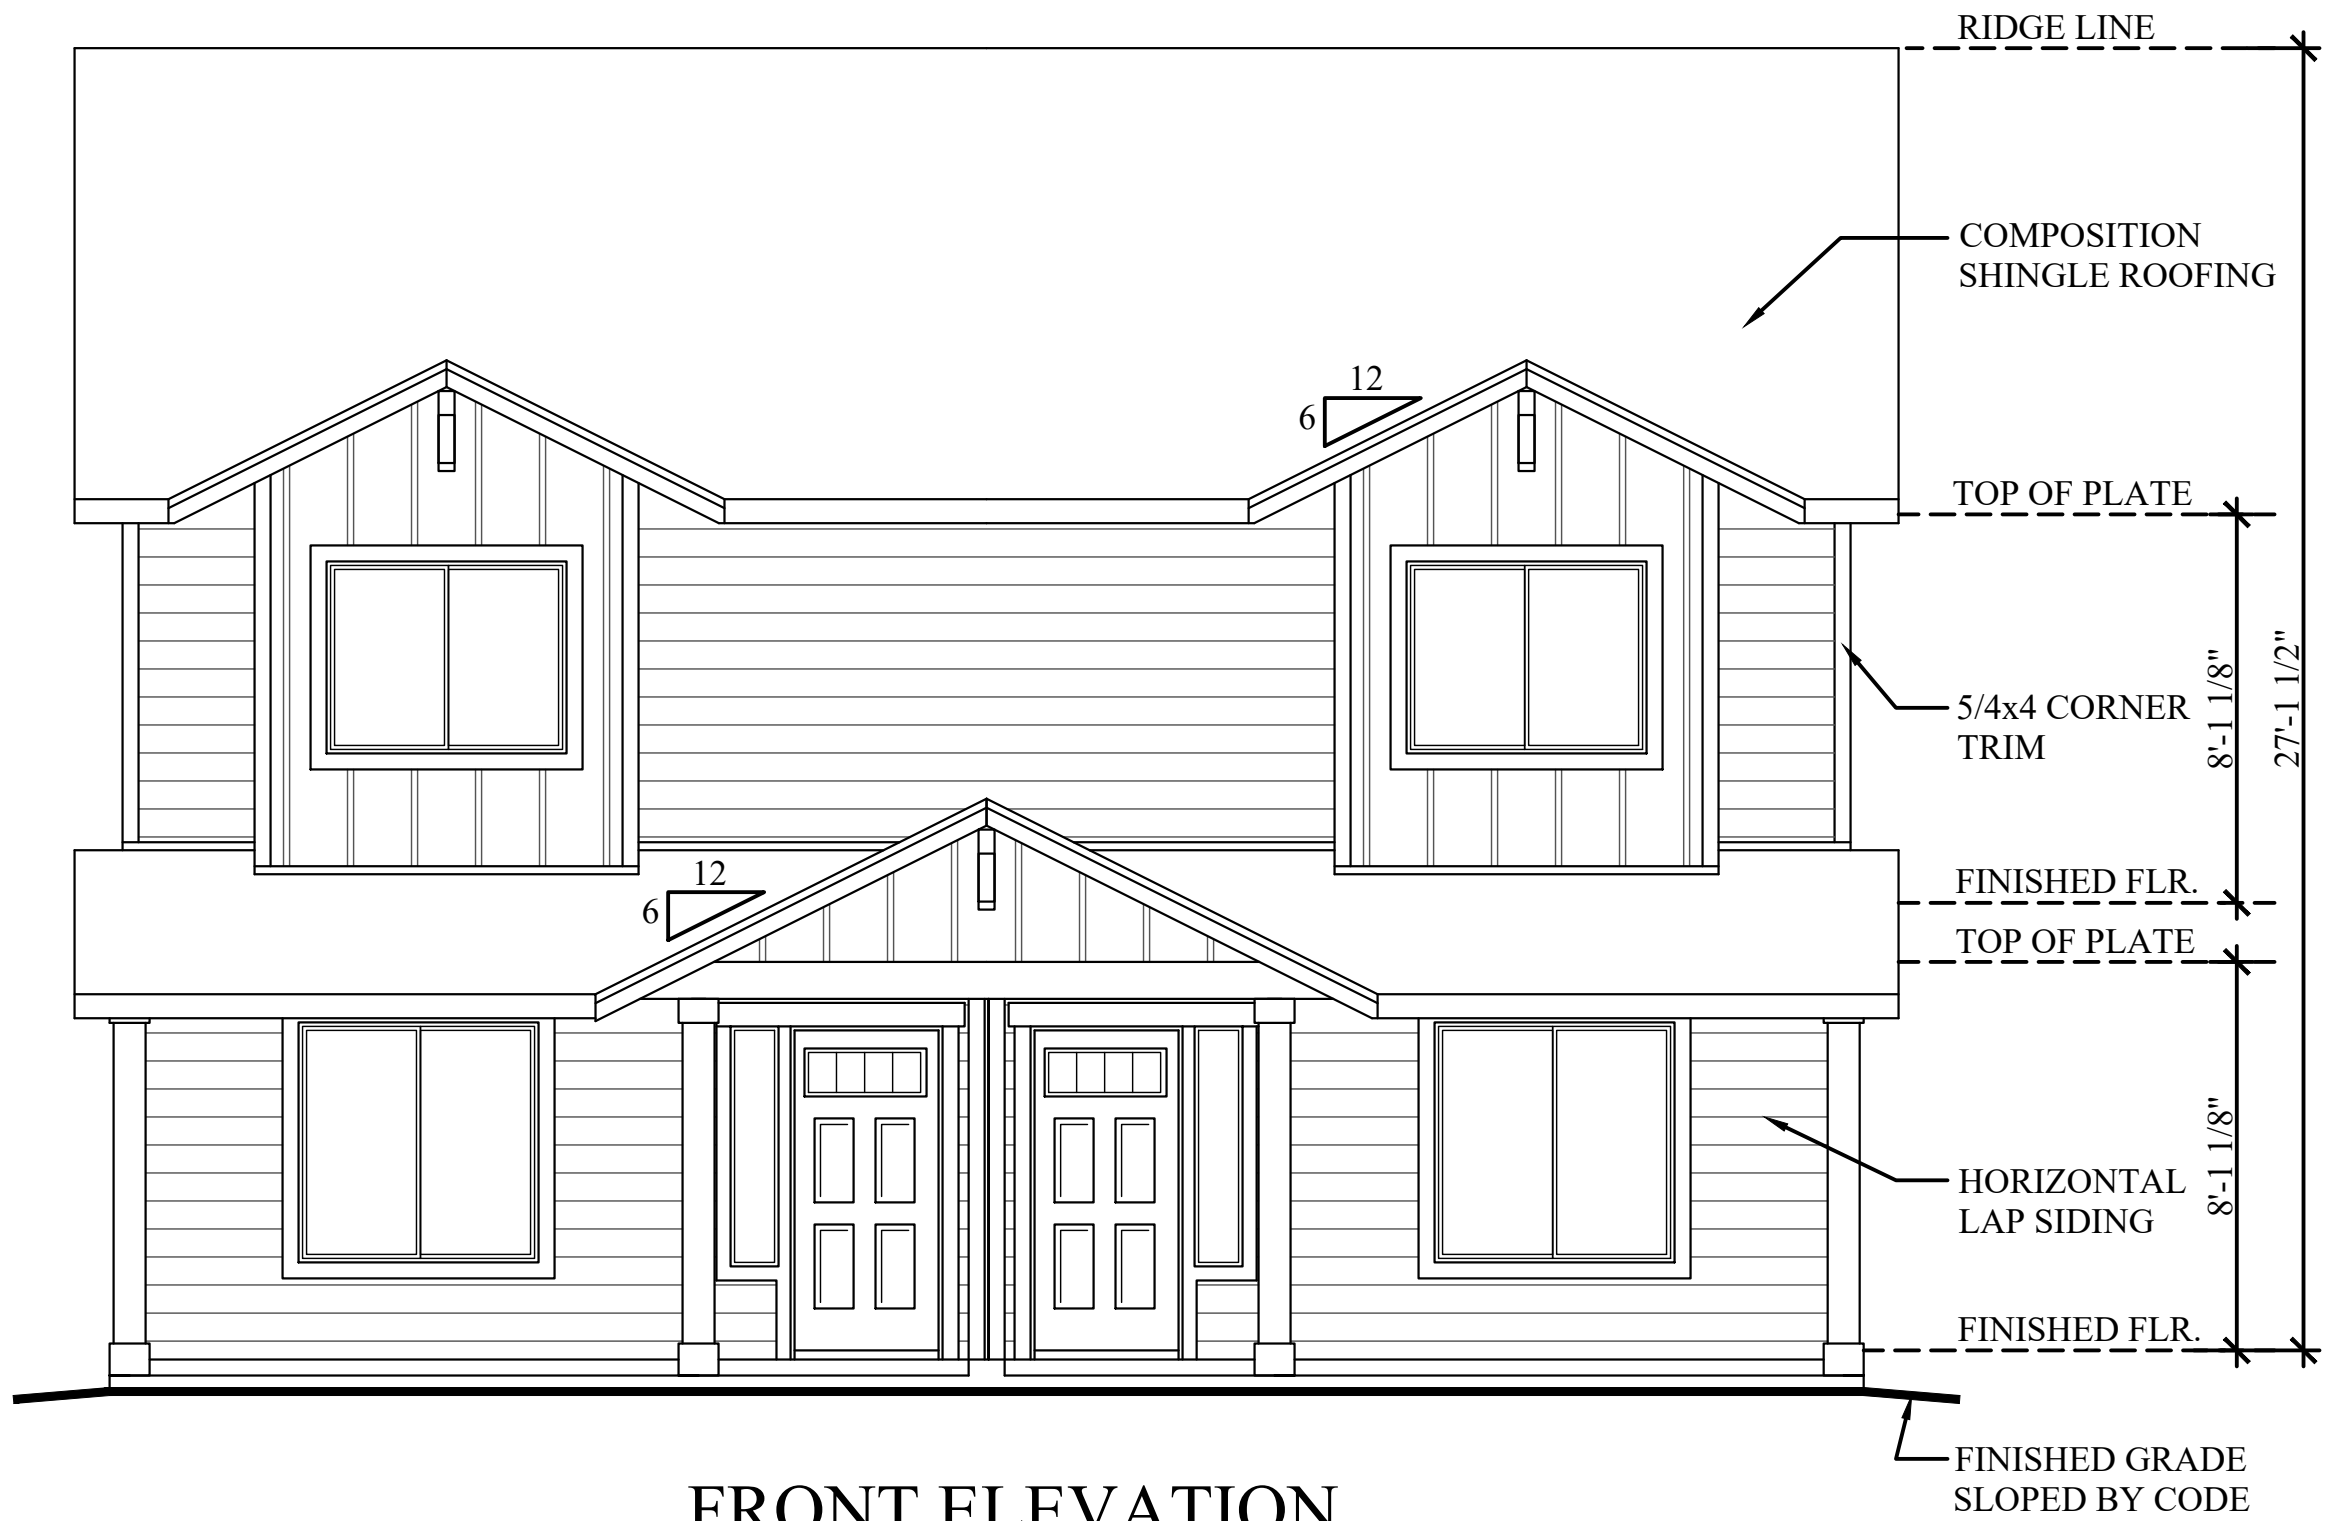


FRONT ELEVATION
1/4" = 1'-0"

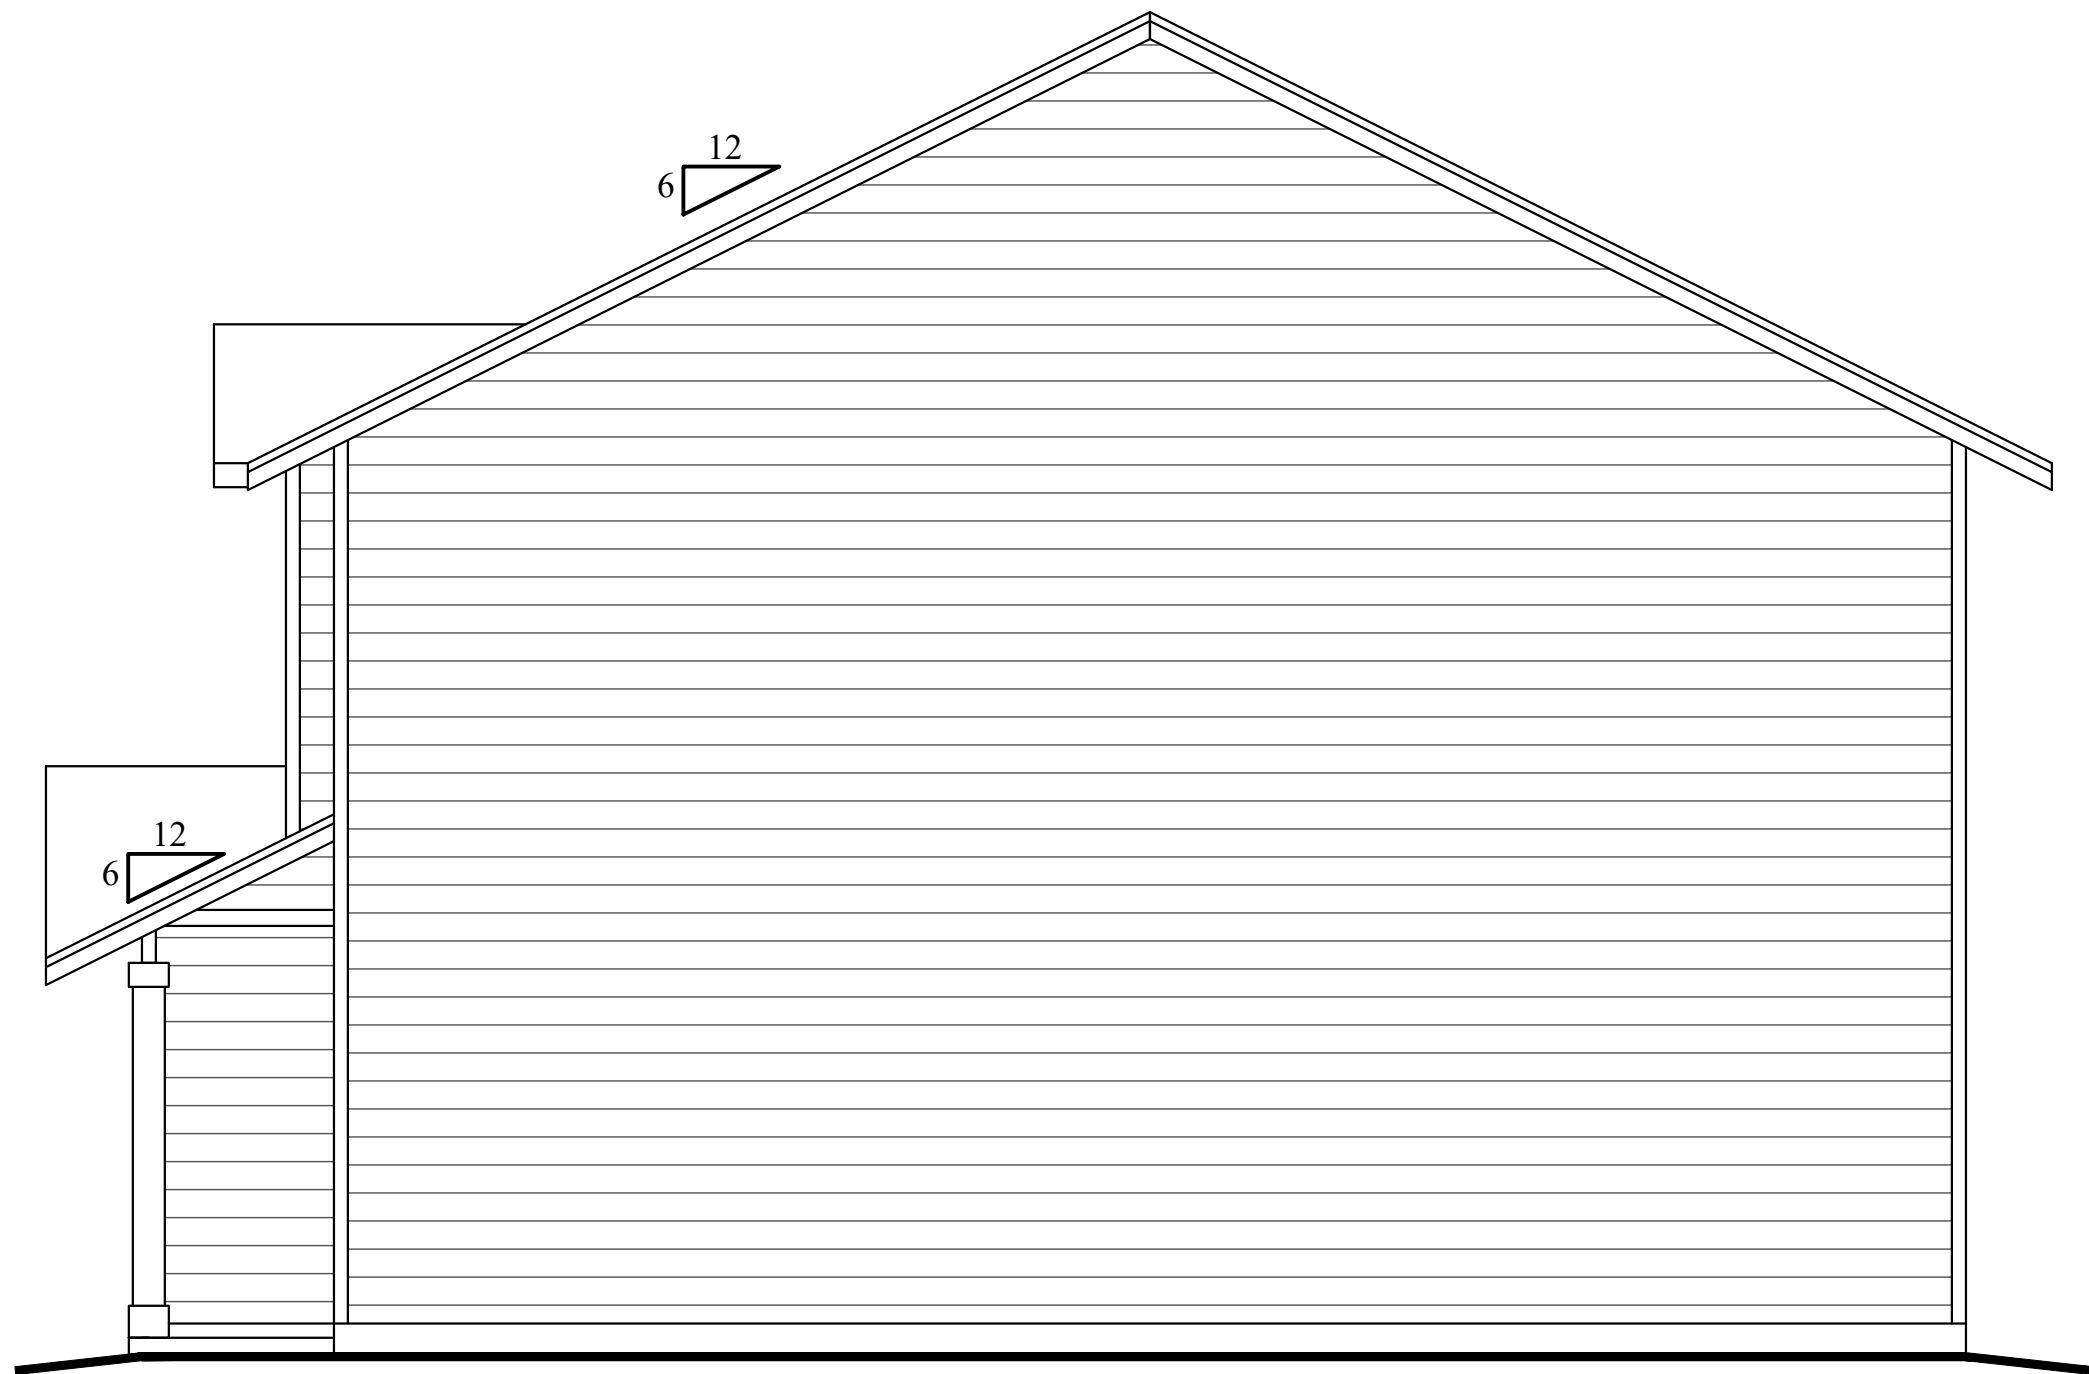

RIGHT ELEVATION
1/4" = 1'-0"

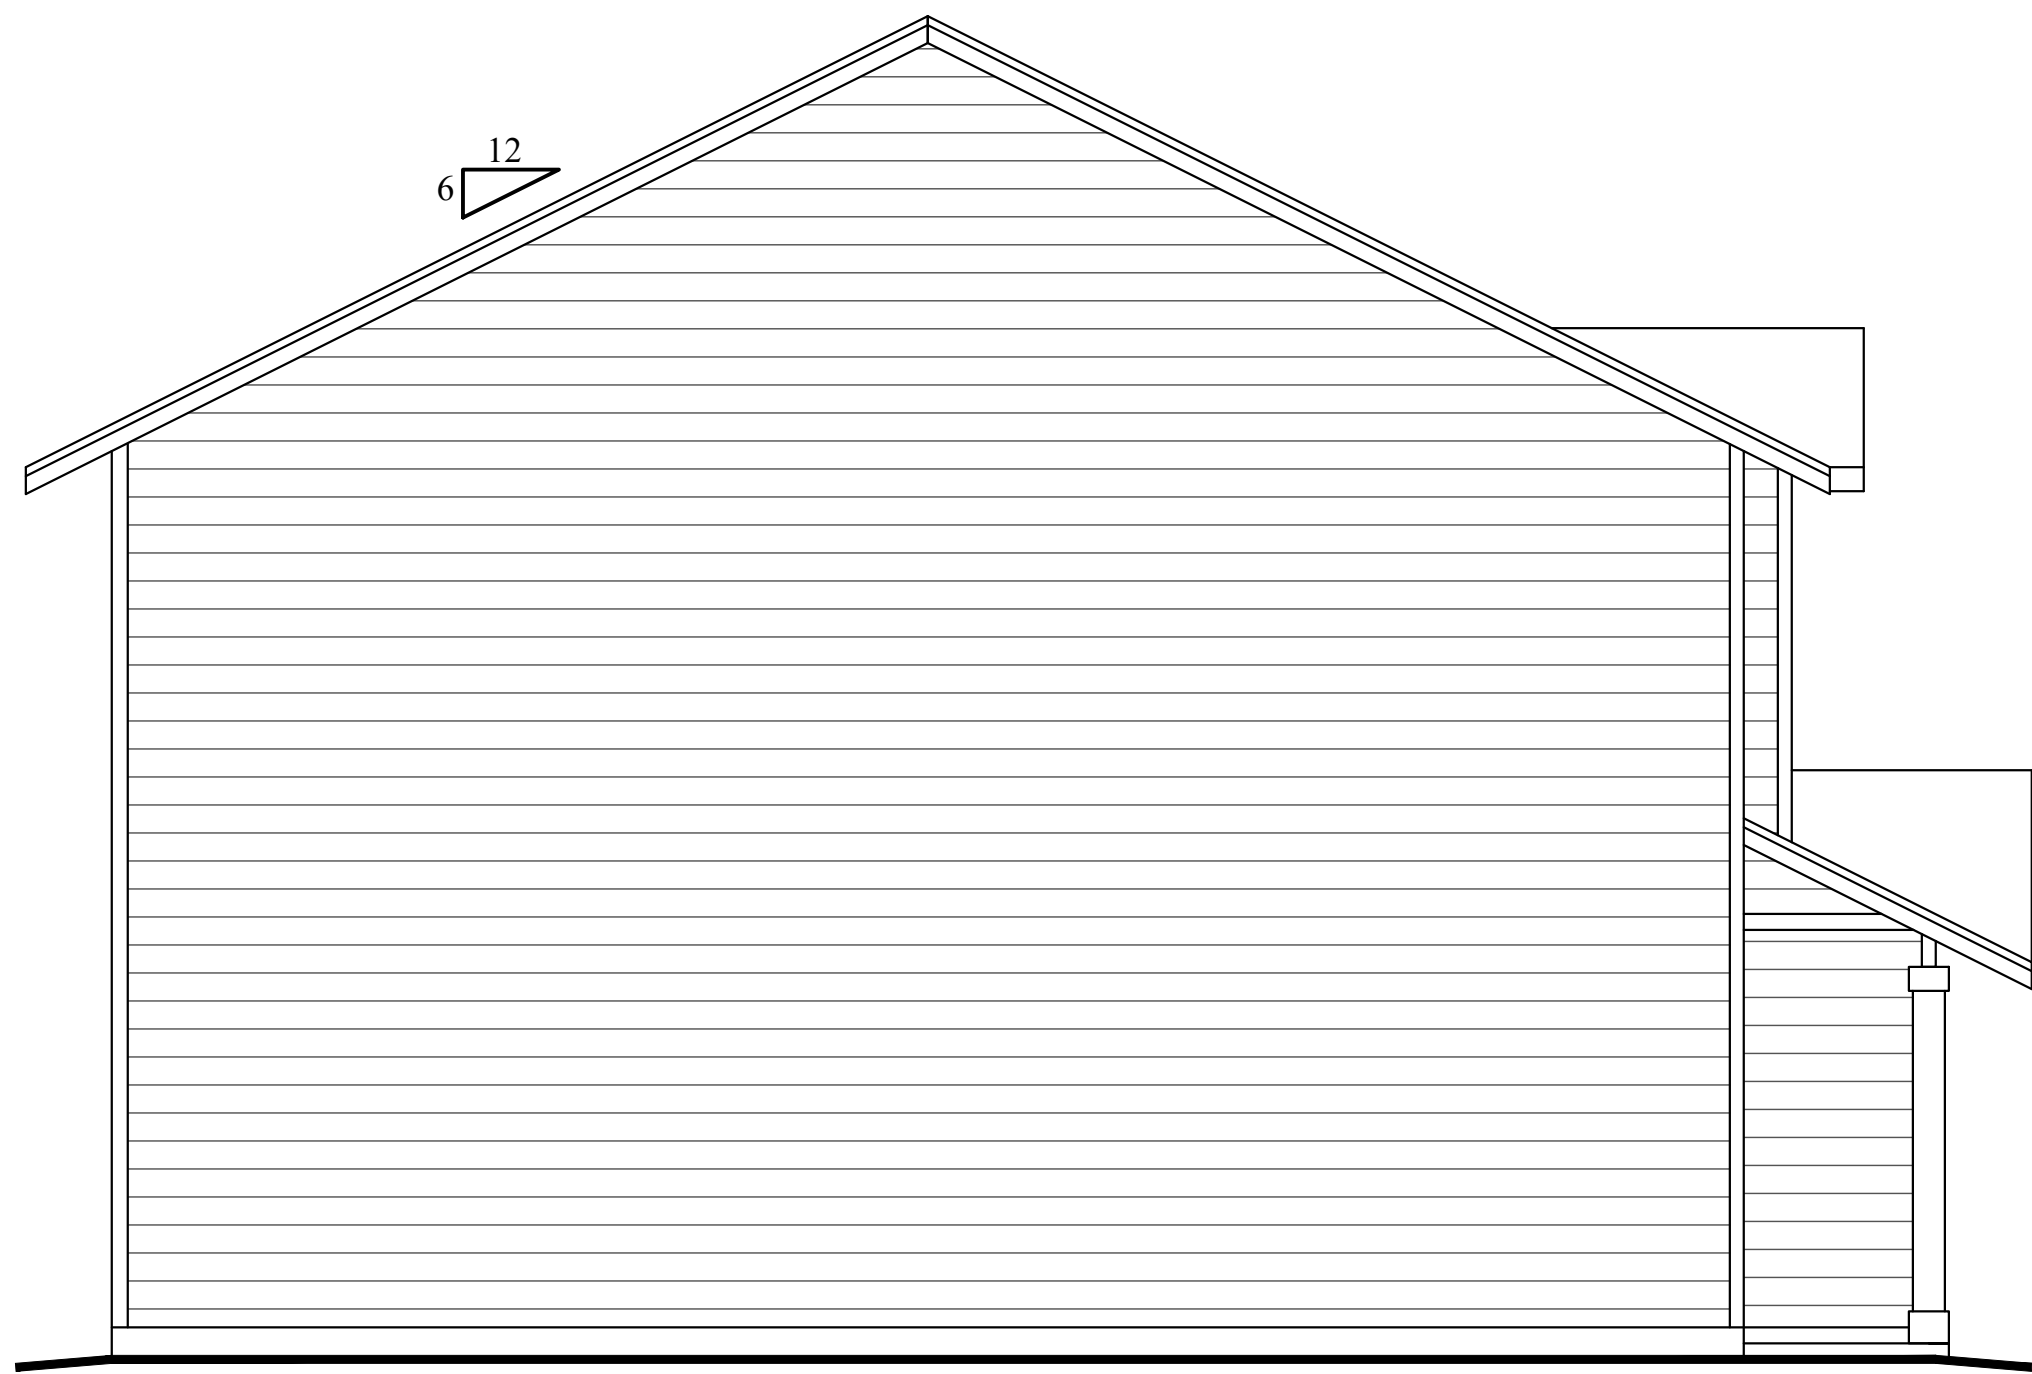

LEFT ELEVATION
1/4" = 1'-0"

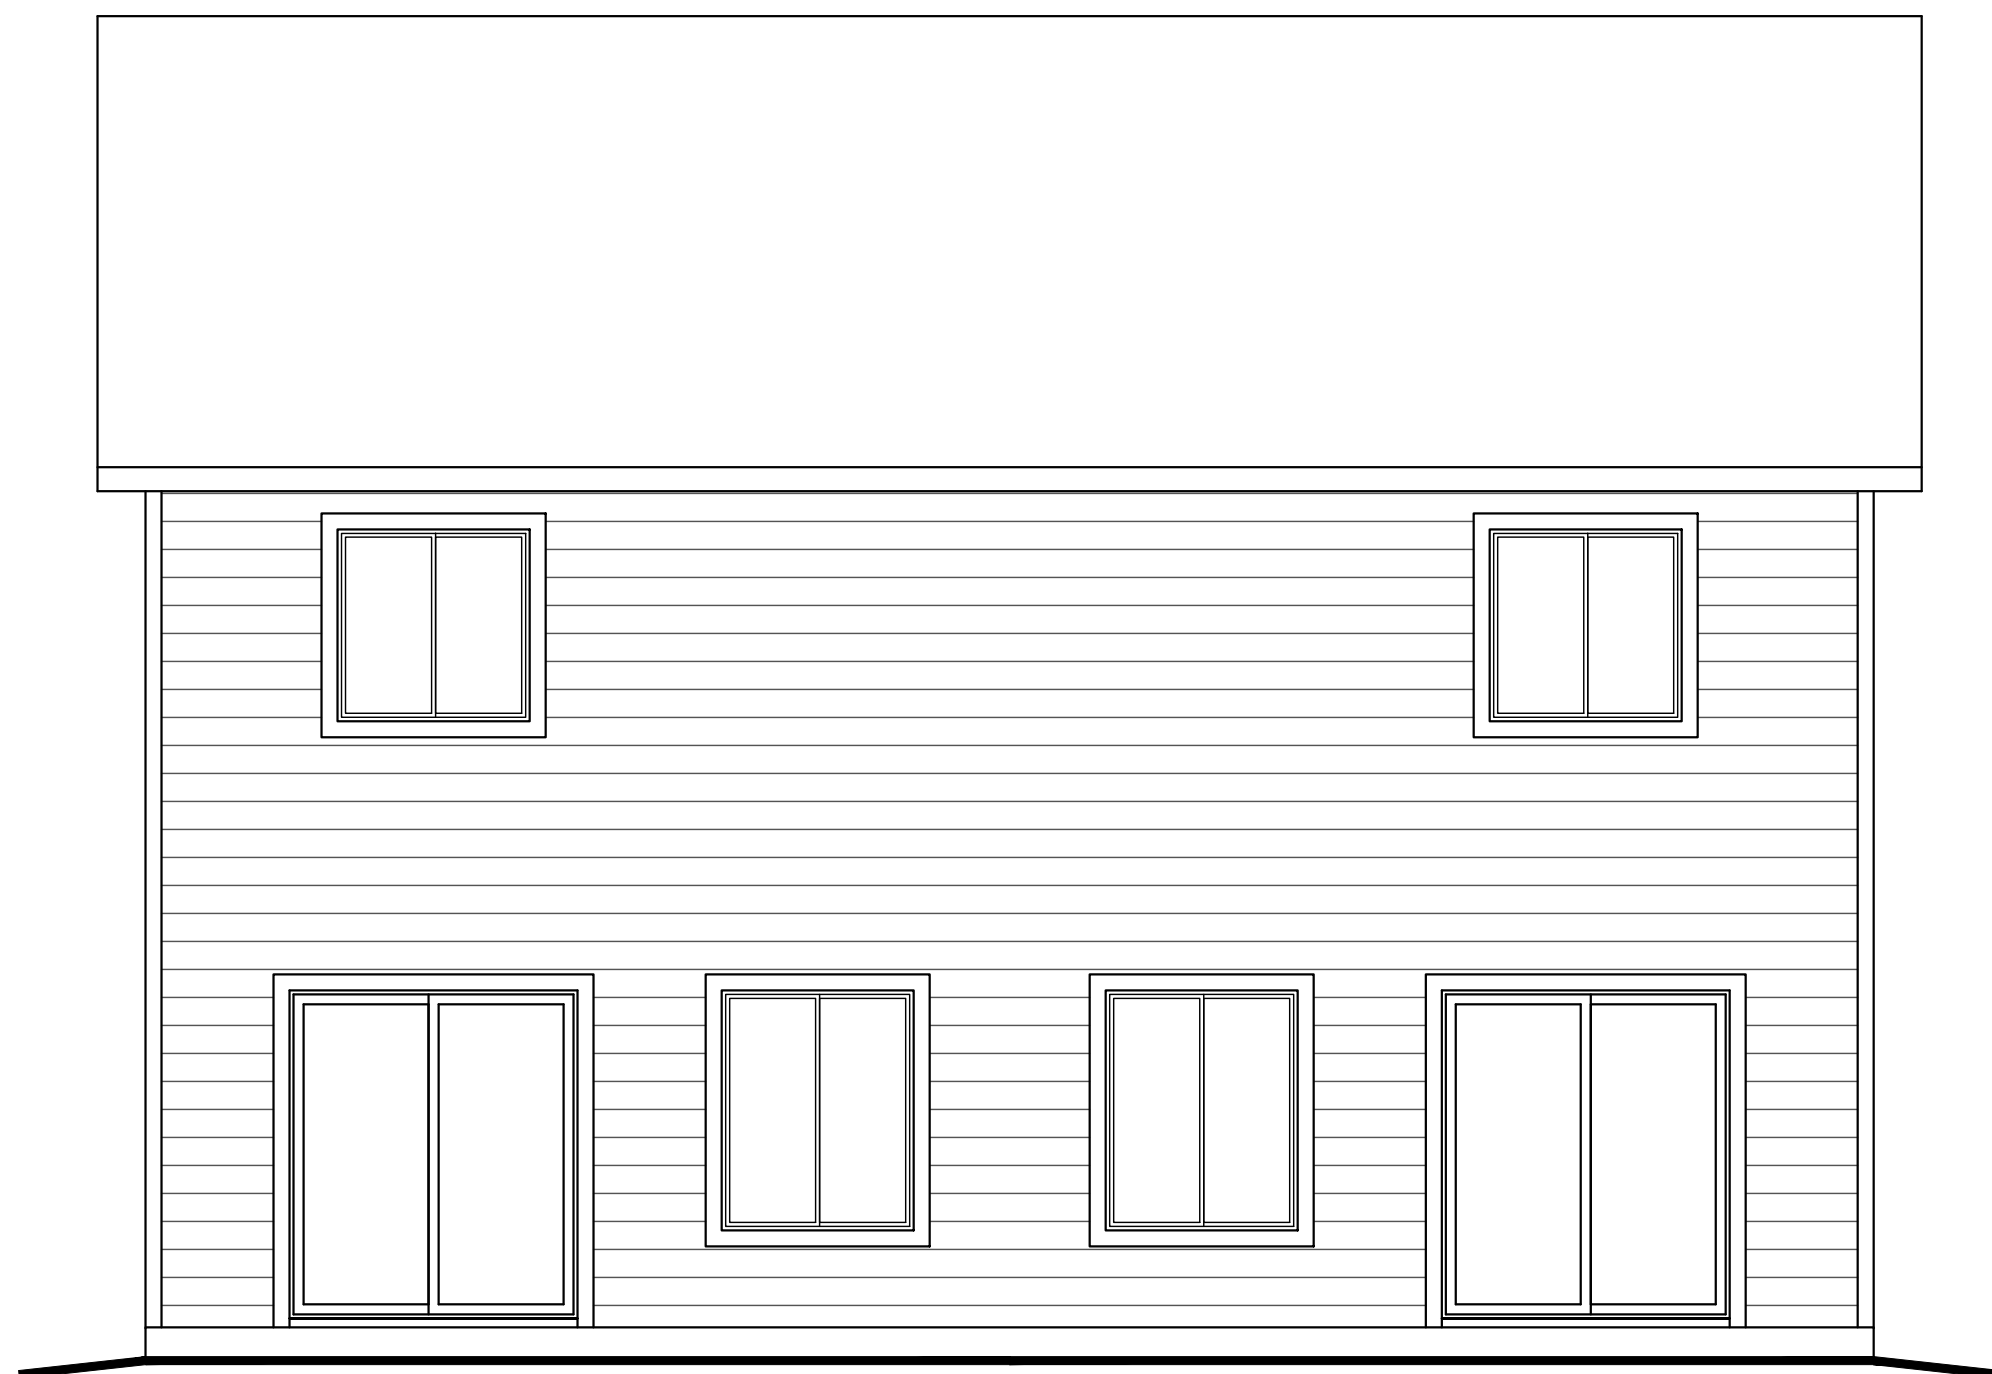

REAR ELEVATION
1/4" = 1'-0"

TRADITIONS ELEV. NOTES

EXTERIOR SIDING & TRIM SPECIFICATIONS

- 1) SIDING ON WALLS: HORIZONTAL LAP SIDING.
- 2) SIDING IN GABLES WHERE SHOWN ON PLANS (TYP. FRONT ONLY): PLAIN PANEL SIDING W/ VERTICAL BATTS AT 16" O.C. OR SHAKE SIDING W/ STAGGERED BOTTOM EDGE.
- 3) TRIM AT EXTERIOR CORNERS: 5/4x4 EACH WAY.
- 4) BELLY BAND AT THE BOTTOM OF DESIGNATED GABLES: 5/4x6 TRIM (METAL HEAD FLASHING TO MATCH).
- 5) LOOK-OUT BEAM AT PEAK OF DESIGNATED GABLE ENDS: 4x6 BEAM, 4x4 ANGLED BRACE, AND 2x4 BACK PLATE.
- 6) WINDOWS: 5/4x4 TRIM ALL SIDES. ON GROUPED WINDOWS THE VERTICAL CENTER MULLIONS WILL BE 5/4x8 RIPPED TO FIT THE WIDTH BETWEEN WINDOWS.
- 7) GARAGE AND FRONT ENTRY DOOR TRIM: 5/4x4 TRIM EACH SIDE AND 5/4x6 HEADER TRIM. HEADER TRIM OVERHANGS EACH SIDE 1 1/2". (DOES NOT APPLY TO OTHER EXTERIOR DOORS)
- 8) SOFFITED AREAS: PLAIN PANEL SIDING WITH 4-4x3 TRIM AT THE PERIMETER.
- 9) EXTERIOR BEAMS: DF#2 SIZED PER STRUCTURAL ENGINEER
- 10) POSTS TO BE 4x4 OR 6x6 PT POSTS PER STRUCTURAL ENGINEER
- 11) WRAPPED PORCH SUPPORT BEAM AND PILLARS: FRONT, BACK, BOTTOM (BETWEEN POSTS) AND EXPOSED ENDS OF THE SUPPORT BEAM TO BE COVERED WITH PLAIN (NO GROOVE) PANEL SIDING. PILLAR COVER TO TERMINATE AT THE BOTTOM 8" BELOW THE TOP OF THE ROUGH FLOOR ELEVATION OF THE HOME. THE OWNER WILL PROVIDE THE FRONT PORCH (WOOD DECK OR CONCRETE SLAB). BASE TRIM TO BE ADJUSTED AS NEEDED.

NOTE:
ALL SIDING IS TO BE CEMENT FIBER BOARD AND THEREFORE FIRE-RESISTANT PER THE MANUFACTURER'S SPECIFICATIONS.

NOTE:
EXTERIOR ELEVATIONS ARE DRAWN W/ ESTIMATED GRADES. ONCE SITE CLEARING & EXCAVATION IS COMPLETE, SOME ADJUSTMENTS MAY BE NECESSARY.

ADAIR HOMES INC.
© COPYRIGHT 2025



ADAIR HOMES, INC
4400 NE 77TH AVE
SUITE 100
VANCOUVER, WA 98662

HODSON #1 - 2386

GARAGE CONFIGURATION:
NONE

PLAN ORIENTATION:
STANDARD

COMMUNITY CODE / LOT#:
MEME-122

ELEVATIONS

2023 ORSC

SCALE: 1/4" = 1'-0"
DATE: 08/26/2025
DRAFTED BY: ES
REV:

PAGE:

A1