


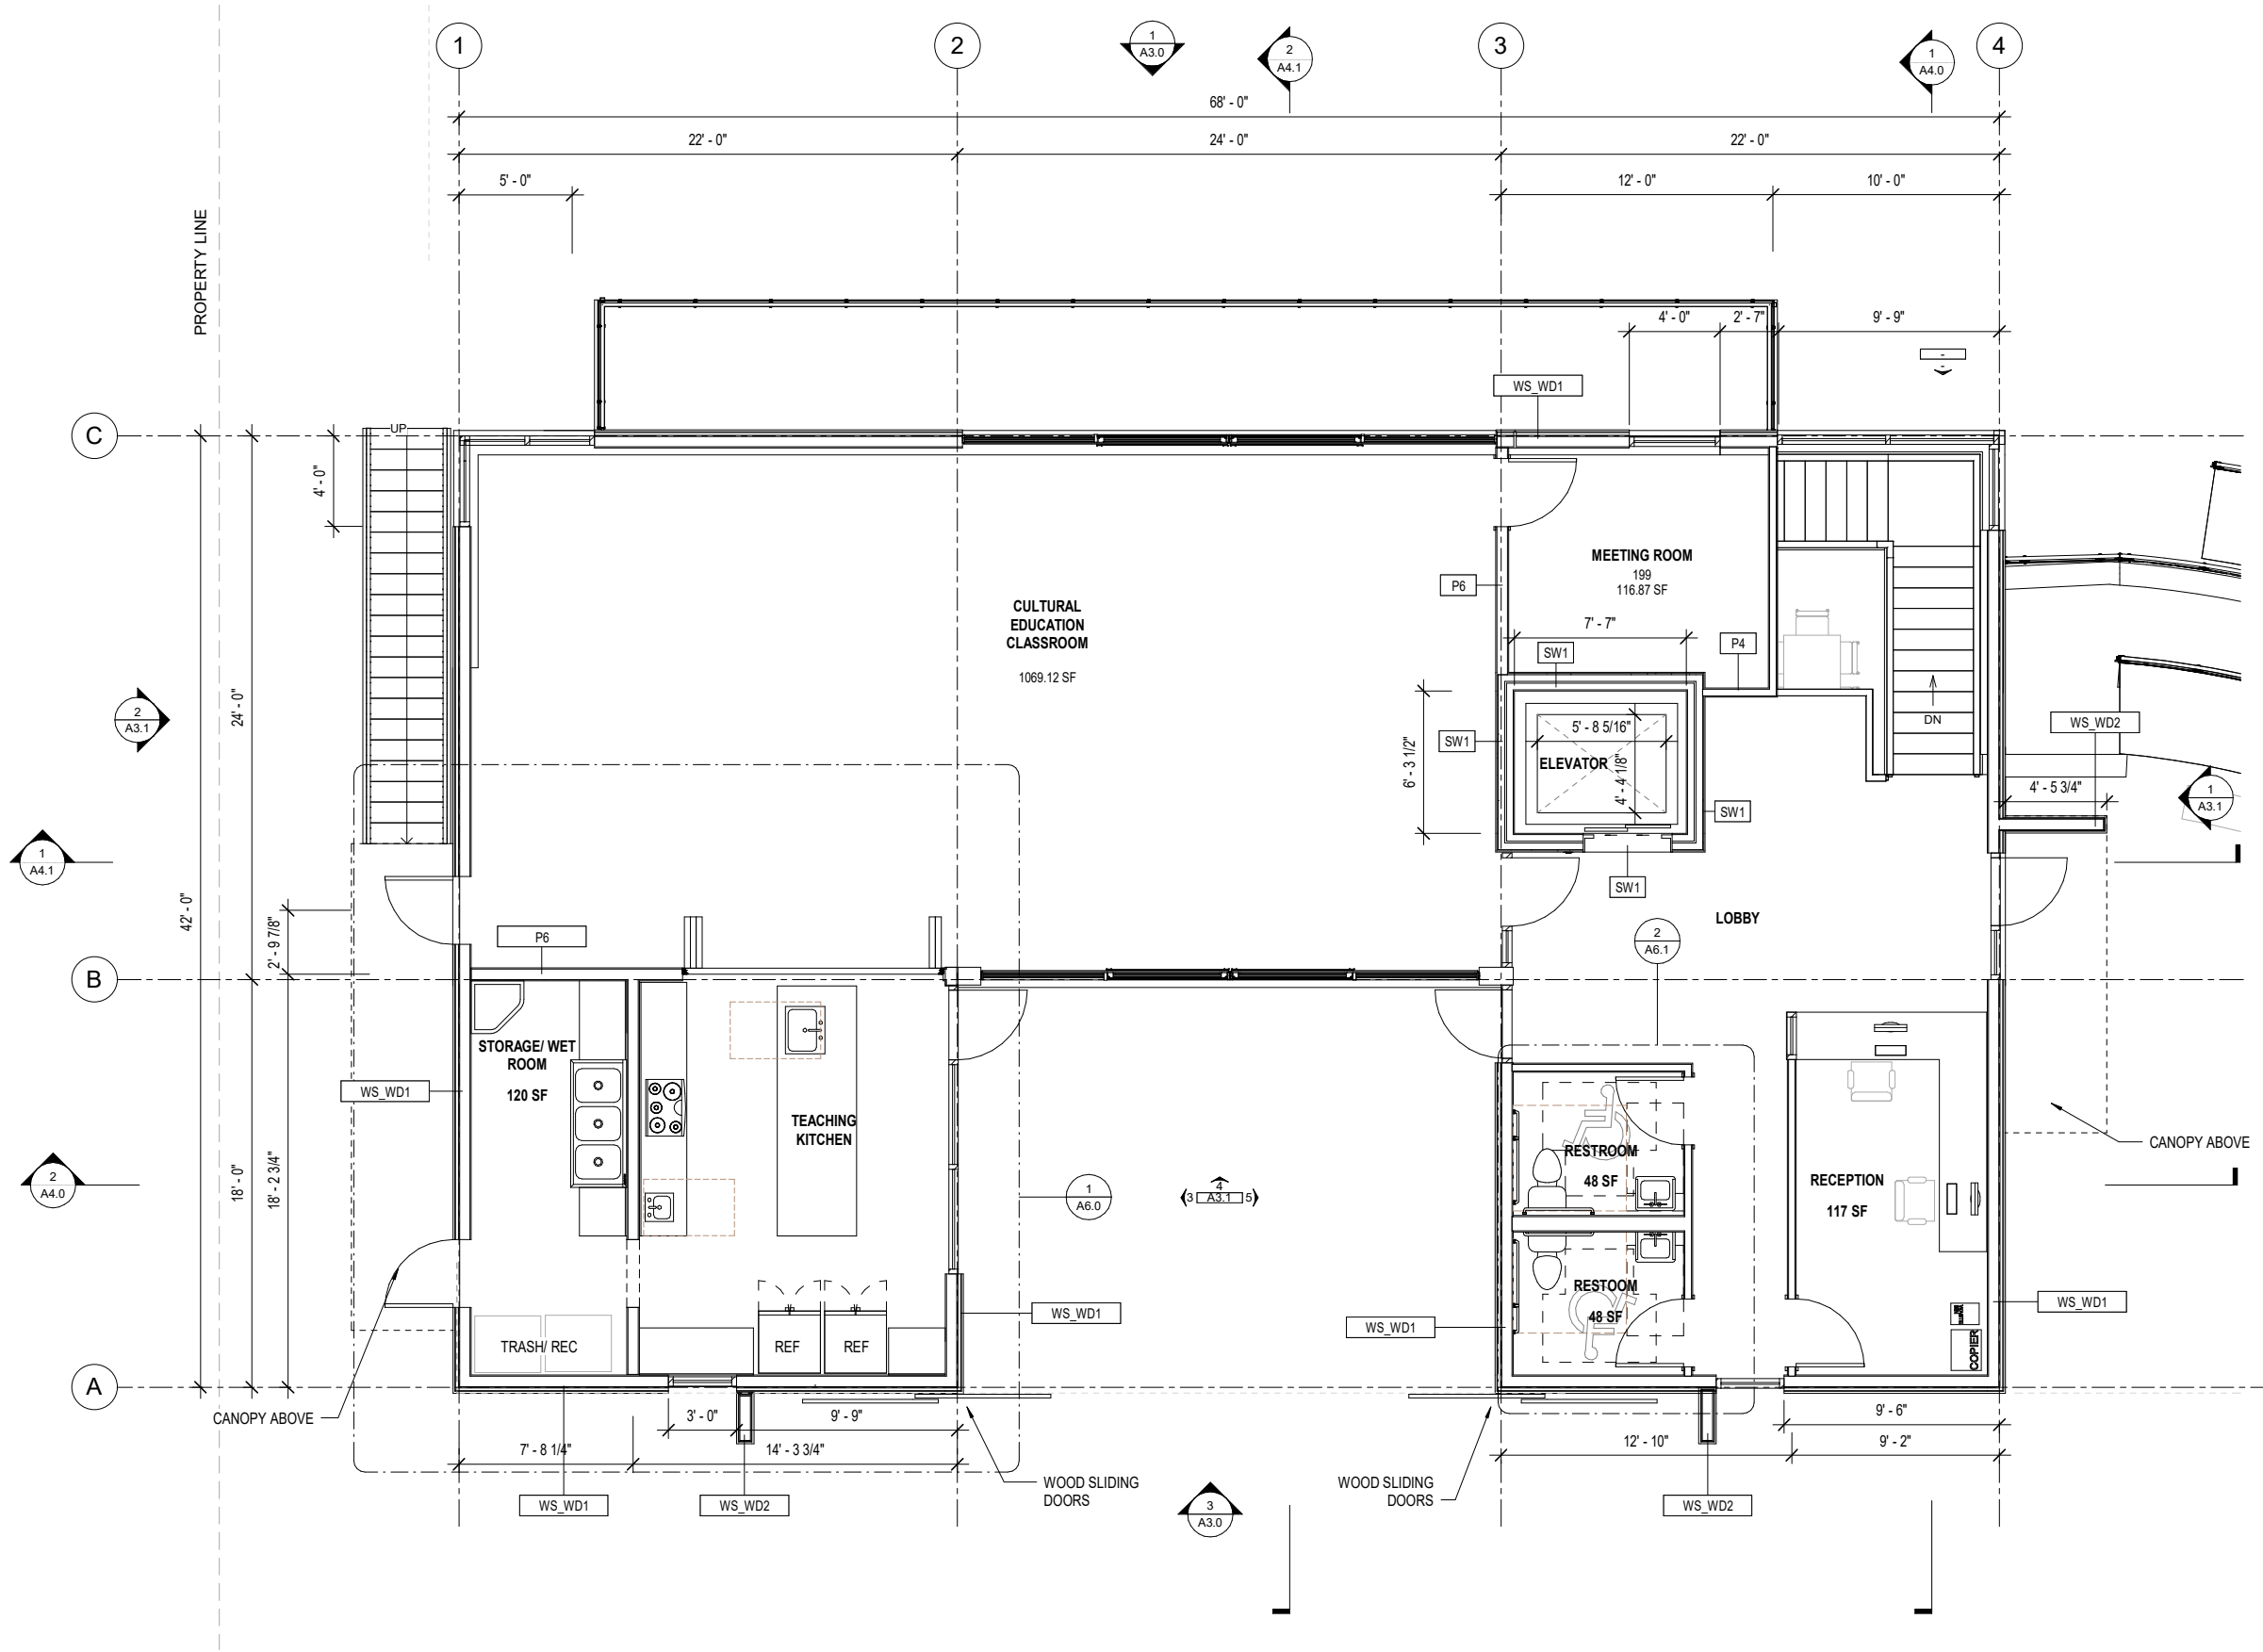

GENERAL NOTES:


1. CONTRACTOR SHALL FIELD VERIFY ACTUAL BUILDING CONDITIONS AND DIMENSIONS. WHERE DISCREPANCIES OR CONFLICTS ARE FOUND, NOTIFY ARCHITECT PRIOR TO COMMENCING WORK.
2. DO NOT SCALE OFF OF DRAWINGS.
3. DIMENSIONS ARE TO GRIDLINE, FACE OR CENTER OF FRAMING UNO.
4. STRUCTURAL ELEMENTS SHOWN IN ARCHITECTURAL DRAWINGS FOR REFERENCE ONLY. SEE STRUCTURAL DRAWINGS FOR ALL STRUCTURAL INFORMATION.
5. ALL PARTITIONS ARE TYPE P1-4, UNO.
6. WHERE DOOR OPENINGS ARE NOT DIMENSIONED, LOCATE DOOR OPENINGS TO ENSURE 3" MIN JAMB FRAMING.
7. DIMENSIONS LOCATING OPENINGS ARE TO CENTERLINE OF OPENING, UNO.
8. SEE ENLARGED PLANS FOR INFORMATION NOT SHOWN HERE.
9. THE MAJORITY OF ALL FFE ITEMS ARE OFOI AND ARE NOT IN CONTRACT, HOWEVER LIMITED ITEMS ARE SHOWN IN DRAWINGS FOR COORDINATION PURPOSES. SEE FFE SHEETS FOR GENERAL FFE INFORMATION AND FFE SHEETS AND PROJECT MANUAL FOR CFCl FFE INFORMATION.

SHEET NOTES:

1. #SPEC DESCRIPTION

LEGEND:

- STRUCTURAL FRAMING -
- SEE STRUCT

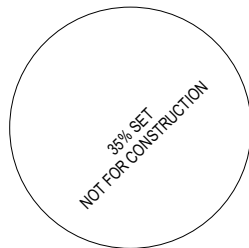

06/05/2023

NorthWind Architects, LLC

126 Seward St
Juneau, AK 99801
Ph #907.586.6150
www.northwindarch.com

1" ACTUAL
IF THE ABOVE DIMENSION DOES NOT MEASURE ONE INCH (1") EXACTLY, THIS DRAWING WILL HAVE BEEN ENLARGED OR REDUCED, AFFECTING ALL LABEL SCALES.

AYAYD Cultural Center
DOUGLAS INDIAN ASSOCIATION AND TRIBAL GOVERNMENT

SHEET TITLE:
**FLOOR PLAN -
LEVEL 1**

CHECKED	Approver	
DRAWN	Author	
issue	date	description

SHEET # **A2.1**

ISSUE DATE 06/05/2023