



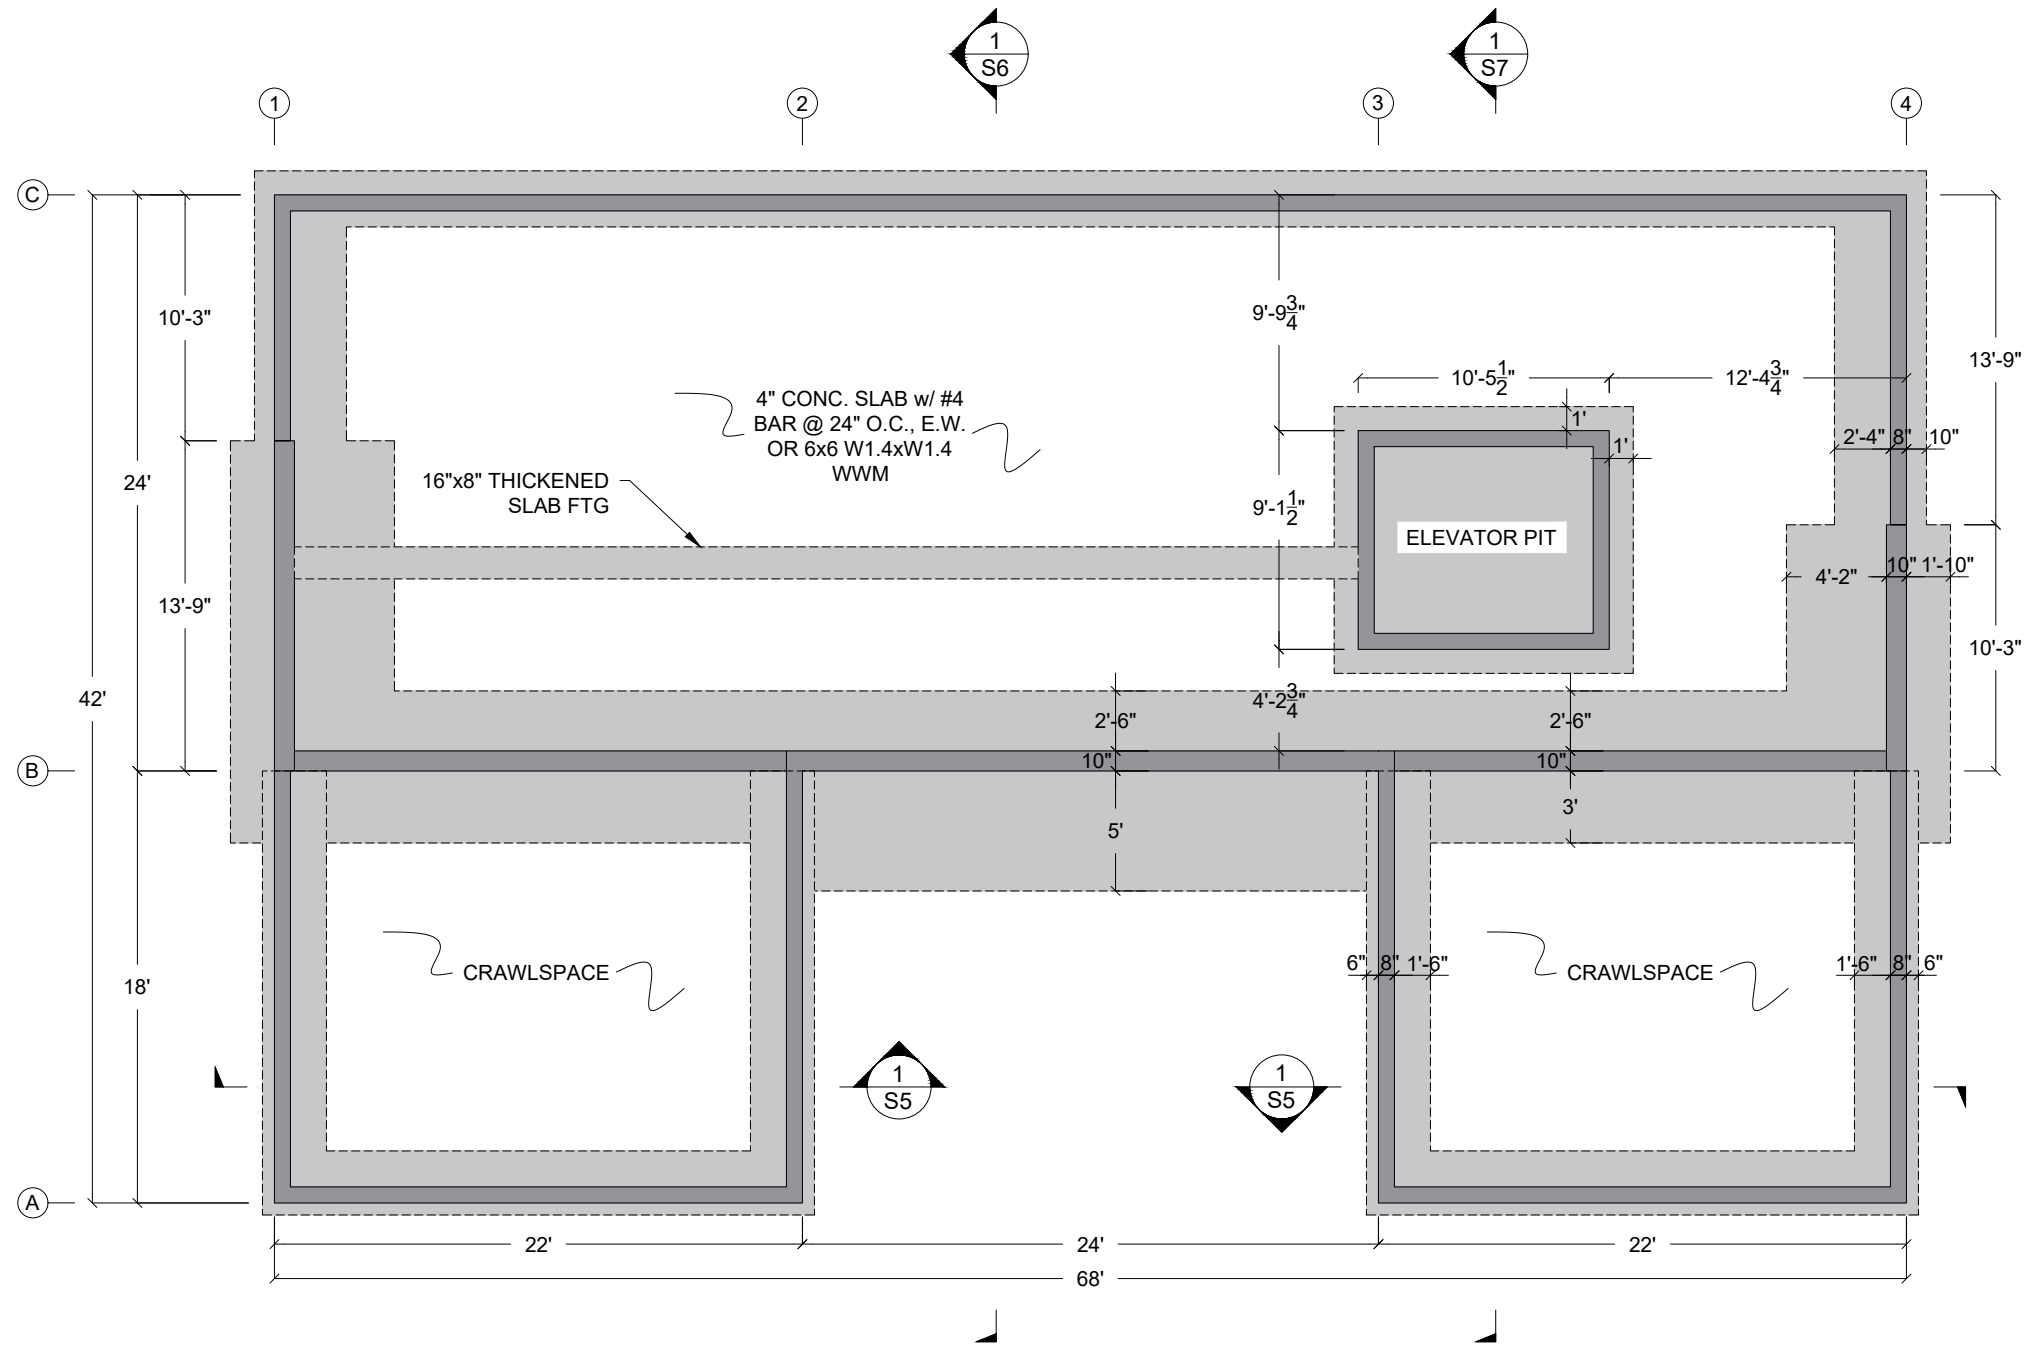

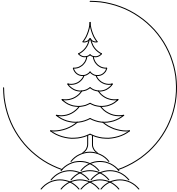

TIMBERLINE ENGINEERING
LLC

JUNEAU, ALASKA
907-635-1433
JAGRAVES77@GMAIL.COM

1" ACTUAL

IF THE ABOVE DIMENSION DOES NOT
MEASURE ONE INCH TO EXACTLY THIS
DRAWING WILL HAVE BEEN ENLARGED OR
REDUCED, AFFECTING ALL LABELED SCALES.

35% SUBMITTAL

DOUGLAS INDIAN ASSOCIATION AND
TRIBAL GOVERNMENT CULTURAL CENTER

DOUGLAS INDIAN ASSOCIATION AND TRIBAL GOVERNMENT
ST. ANN'S AVENUE, DOUGLAS, ALASKA

SHEET TITLE:
FOUNDATION PLAN

CHECKED	JG
DRAWN	JG

issue	date	description
-------	------	-------------

SHEET #
S2

1 FOUNDATION PLAN
1/4" = 1'-0"

