



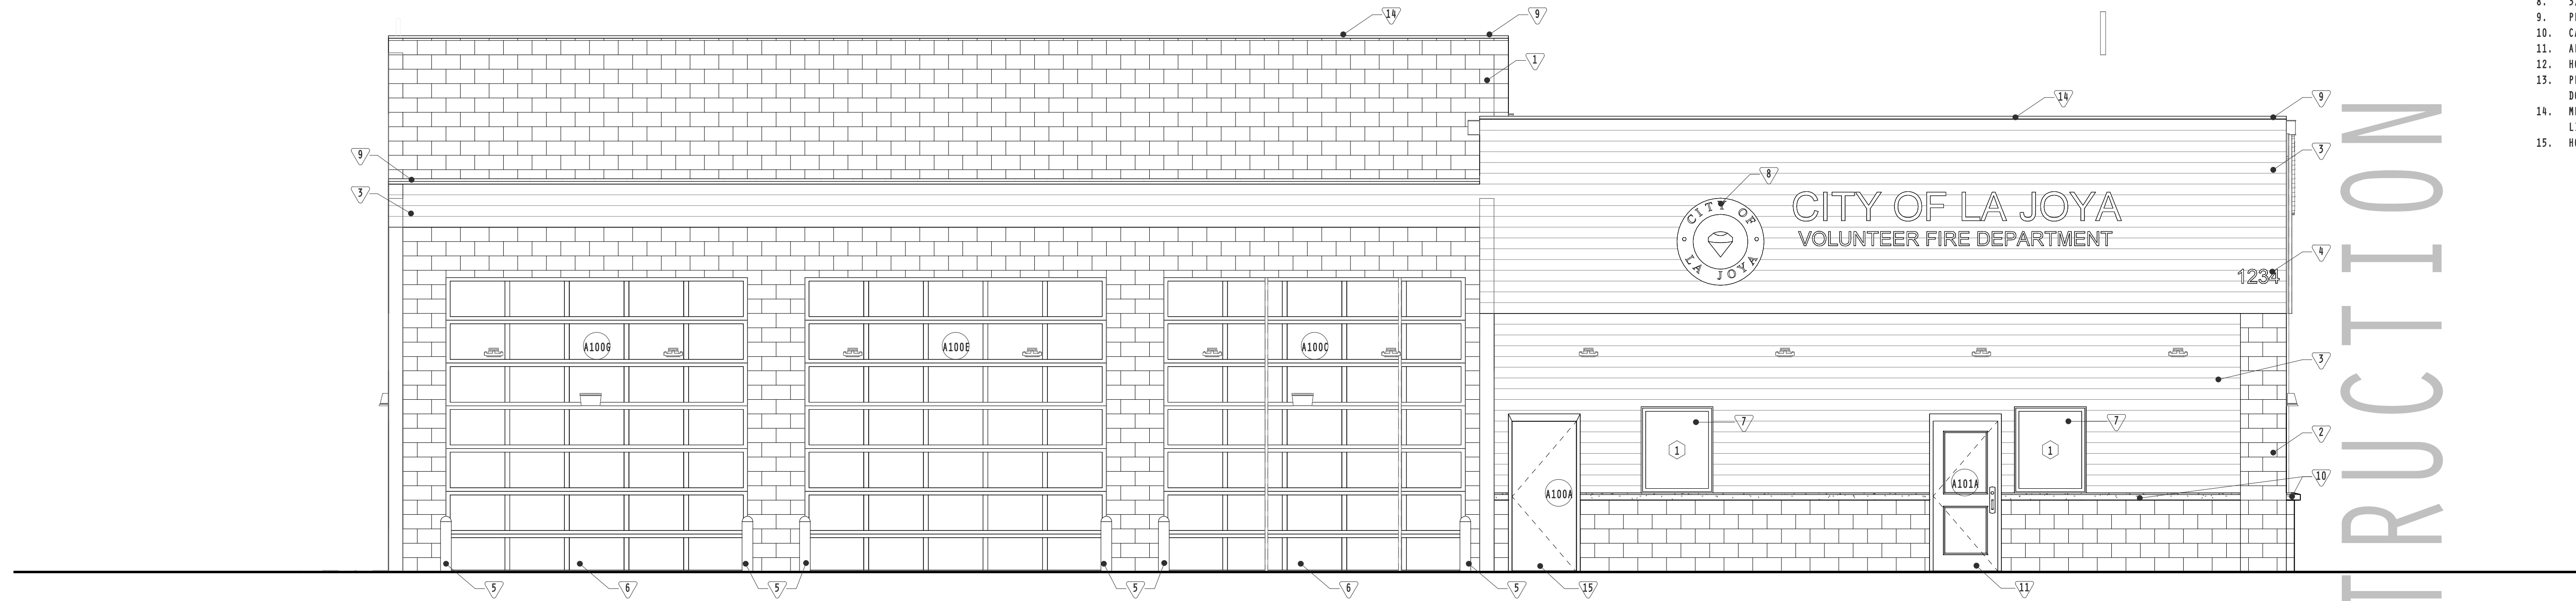


2 WEST ELEVATION
1/4" = 1'-0"

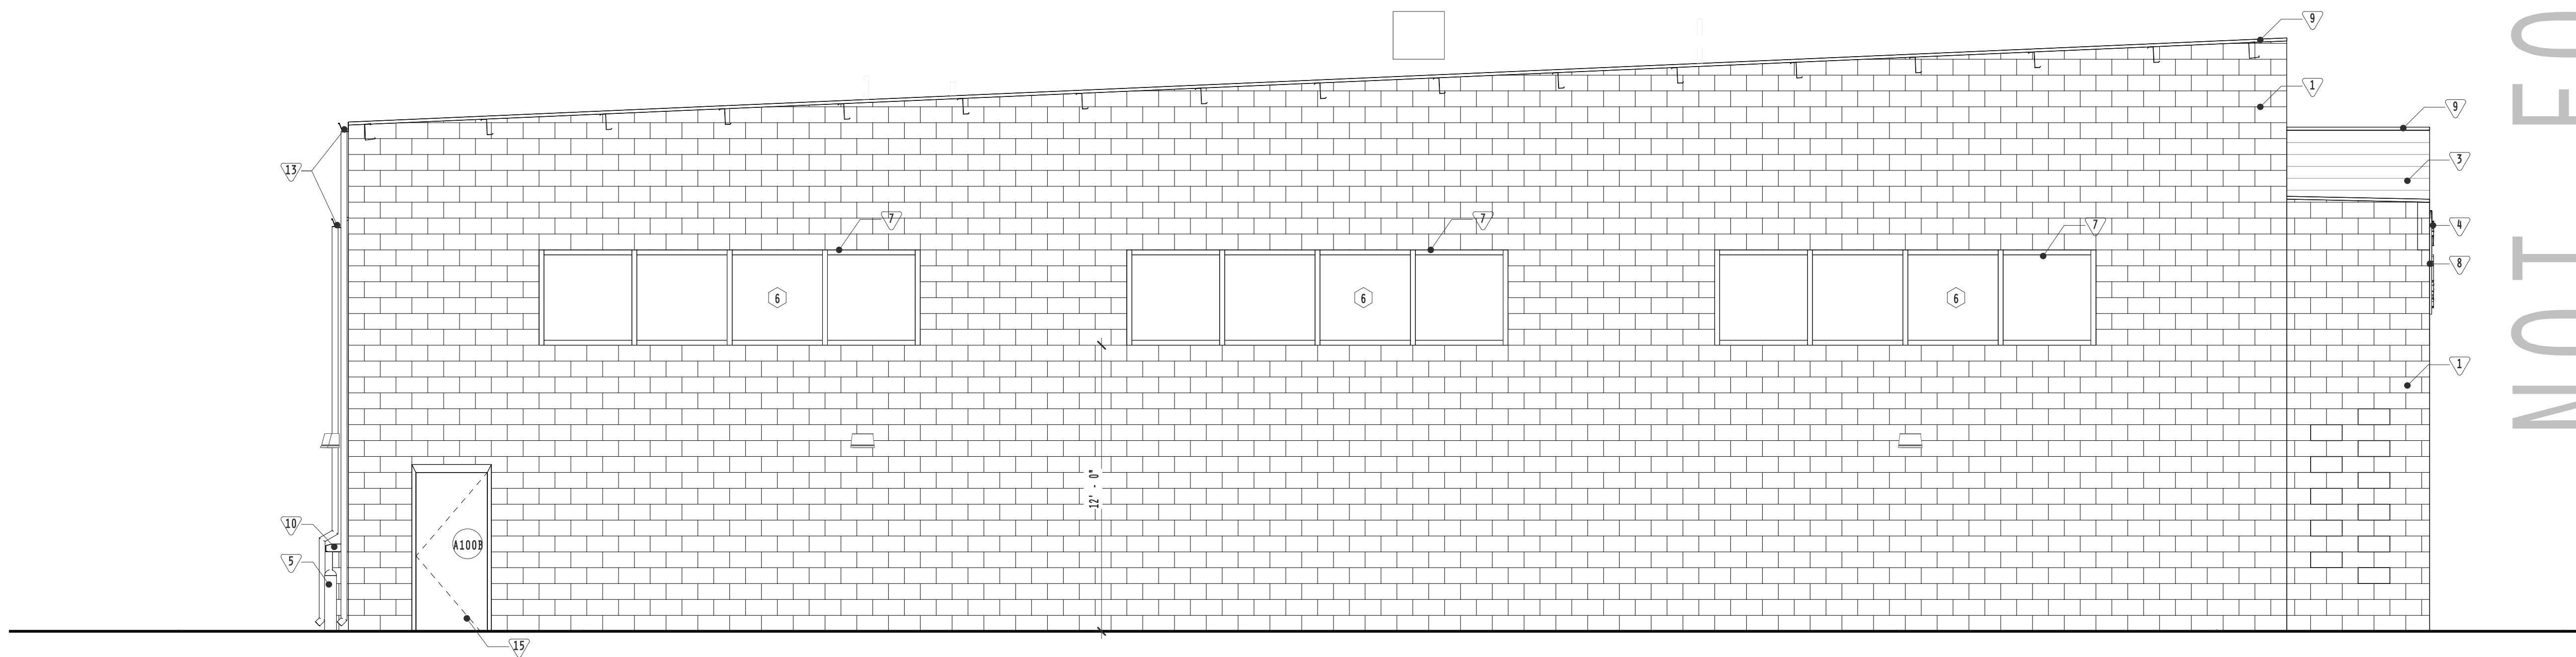

1 NORTH ELEVATION
1/4" = 1'-0"

SHEET KEYNOTES

- 8" CMU, INTEGRAL COLOR
- 4" CMU VENEER, INTEGRAL COLOR
- 1 1/2" METAL PANEL
- 8" AND 16" TALL 3/8" THICK ALUMINUM LETTERS
- 6" CONCRETE FILLED BOLLARDS, PTD.
- OVERHEAD DOORS AS SPEC.
- ALUMINUM WINDOW SYSTEM, AS SCHED.
- 3/8" PERFORATED ALUMINUM LOGO
- PRE-FINISHED EAVE TRIM.
- CAST STONE CAP
- ALUMINUM DOOR SYSTEM, AS SCHED.
- HOLLOW METAL DOOR SYSTEM, PTD.
- PRE-FINISHED GUTTERS AND DOWNSPOUTS
- METAL PANEL ROOFING SYSTEM WITH LINER INSULATION SYSTEM
- HOLLOW METAL DOOR SYSTEM, PTD.

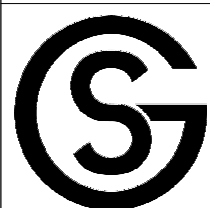No.	DESCRIPTION	DATE
		01.06.2023
	 SAM GARCIA ARCHITECT 1200 AUBURN AVE. SUITE 280 McALLEN, TX 78504 (956) 631 - 8327 INFO@SANGARCIAARCHITECT.COM	
	CITY OF LA JOYA FIRE STATION	
	701 E EXPRESSWAY 83 LA JOYA, TX 78560	
2022-016		01.06.2023
	EXTERIOR ELEVATIONS	
	A2.01	