
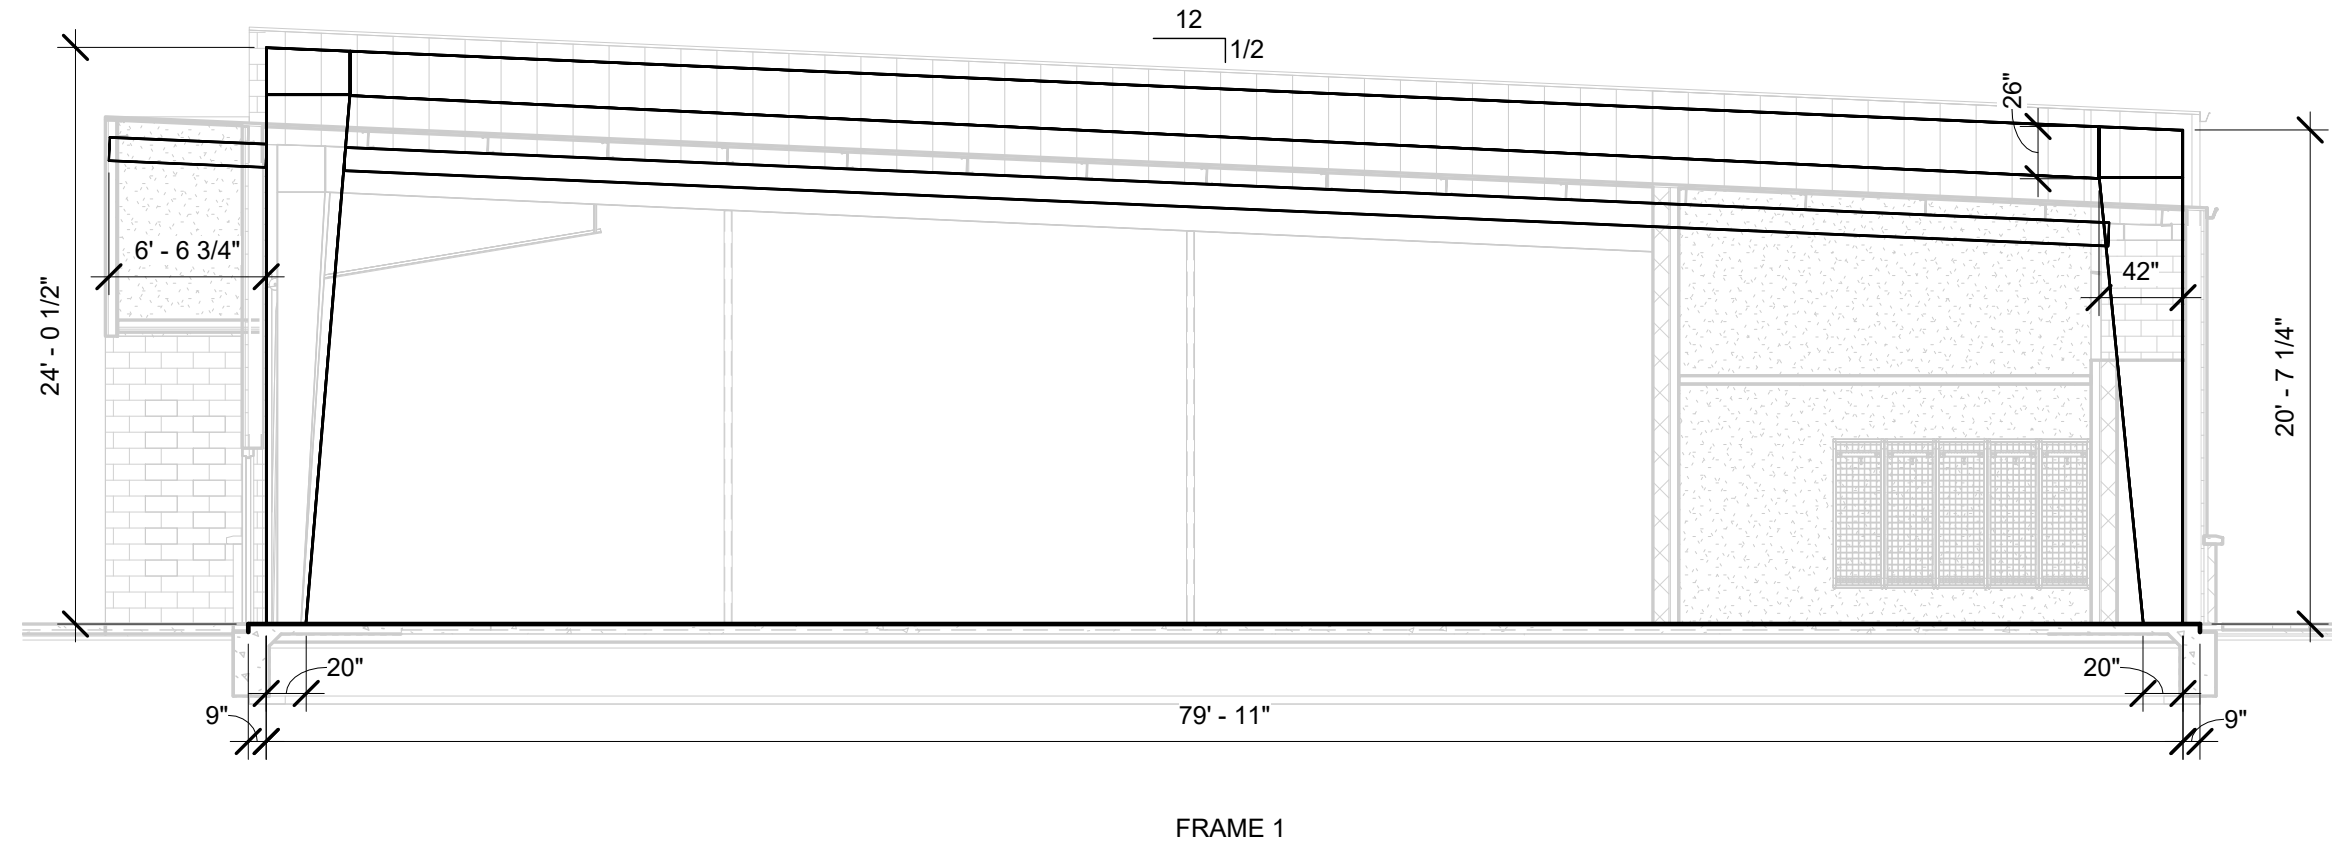


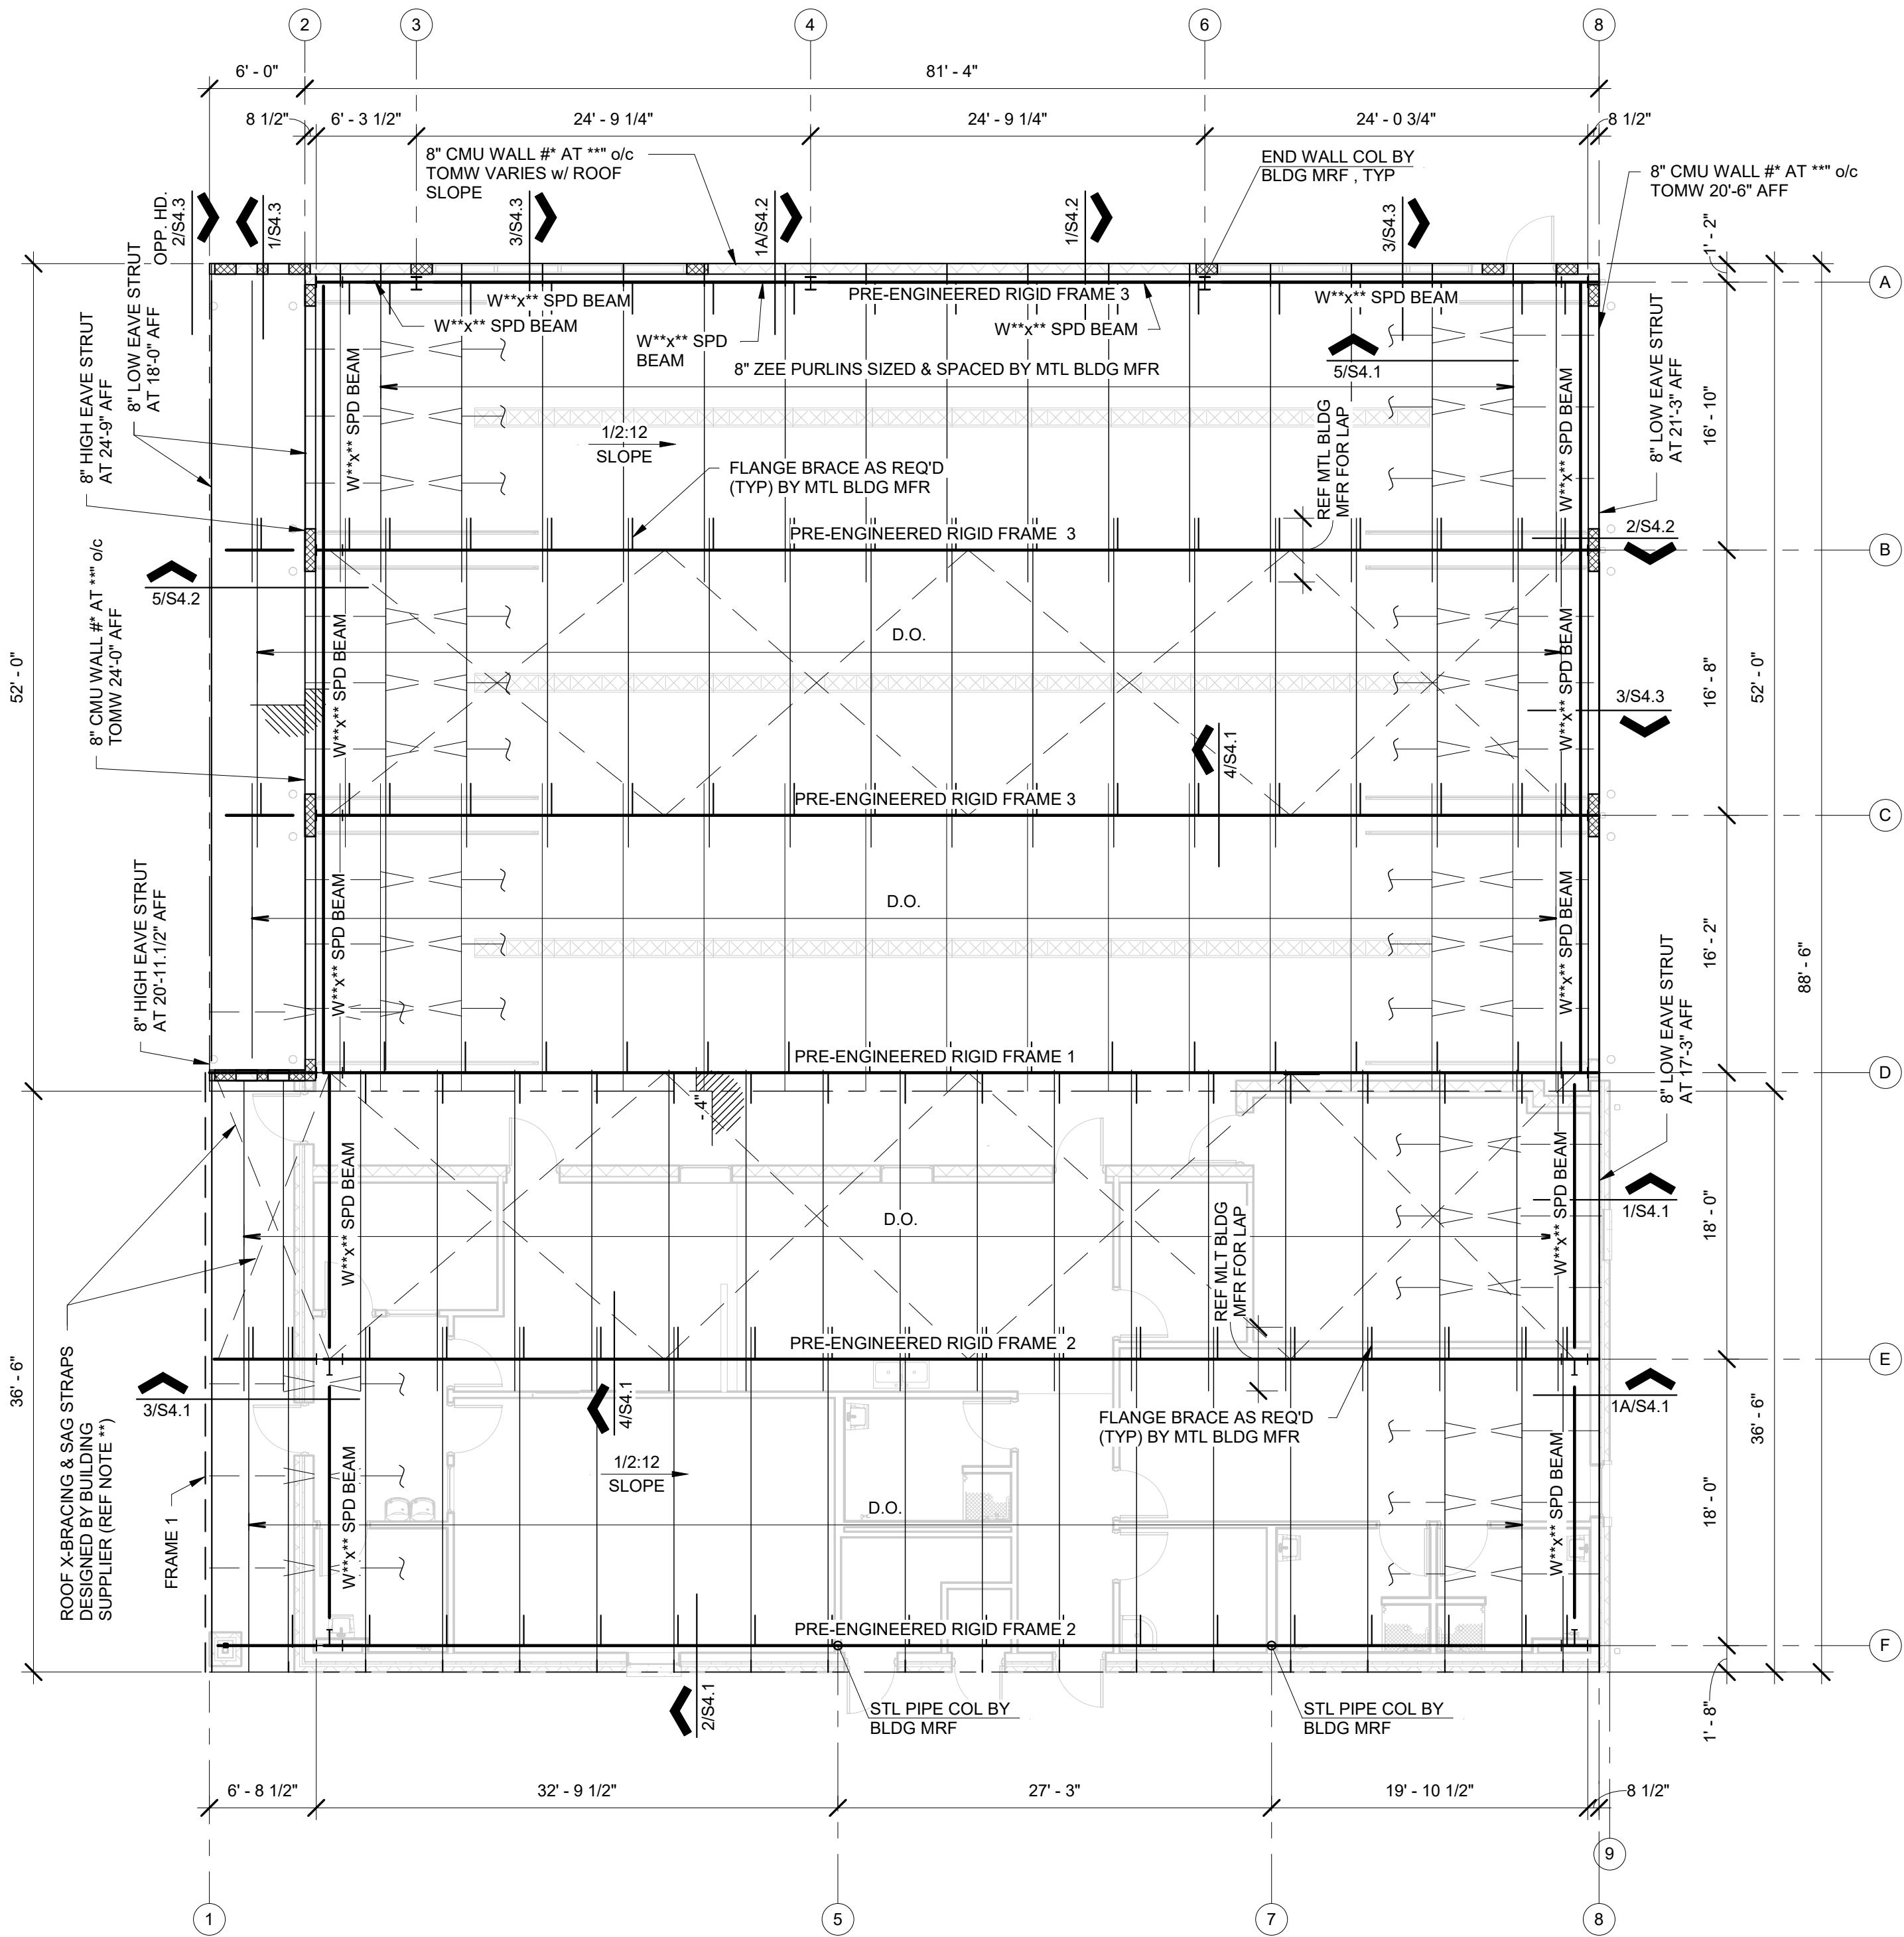

NOT FOR CONSTRUCTION

No.	DESCRIPTION	DATE
01-06-2023	SAM GARCIA ARCHITECT 200 S. 10th ST. SUITE 402 McAllen, TX 78501 (956) 631-6327 info@samgarciaarchitect.com	
CITY OF LA JOYA FIRE STATION		
Enter address here		
1205-05	01-06-2023	
SCHEMATIC ROOF FRAMING PLAN		
S3.1		

PRELIMINARY

THIS DOCUMENT IS RELEASED FOR THE PURPOSE OF INTERIM REVIEW UNDER THE AUTHORITY OF ROLANDO R. RUBIANO, P.E., 68369. IT IS NOT TO BE USED FOR CONSTRUCTION, BIDDING, OR PERMIT PURPOSES.

GREEN, RUBIANO & ASSOCIATES

CONSULTING STRUCTURAL ENGINEERS

1220 WEST HAWTHORN
MCKINNEY, TEXAS 75069
(956) 428-4481 (956) 428-0287 FAX
P.E. REGISTRATION # 64145