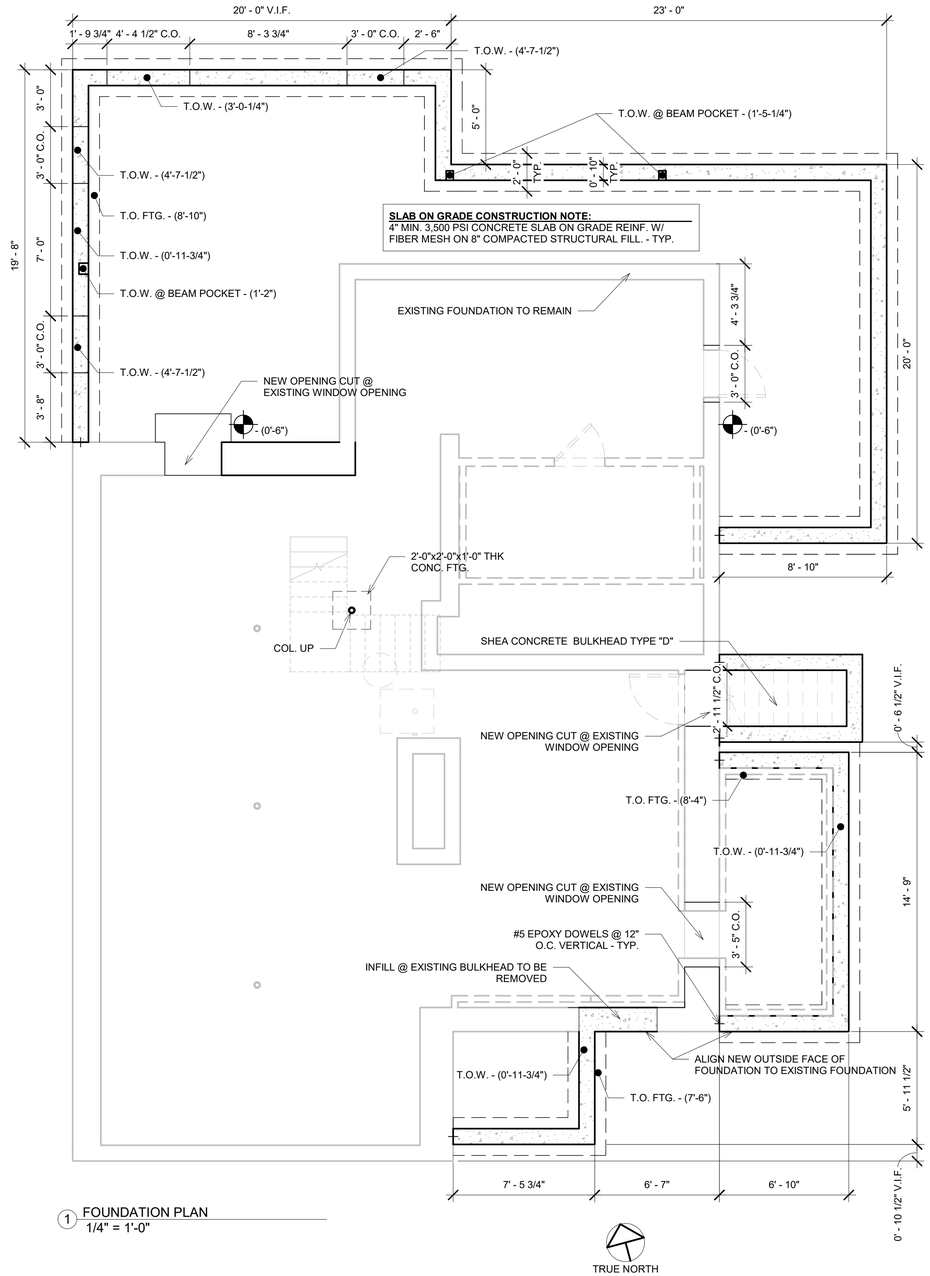


1 FOUNDATION PLAN
1/4" = 1'-0"

0' 2' 4' 8' 16'

KRAUS ASSOCIATES

66 CENTRAL STREET STE. 2
WELLESLEY, MA 02482
(781) 431-7400
WWW.KRAUSAB.COM

ALL RIGHTS RESERVED. NO USE OR REPRODUCTION OF THIS MATERIAL IS PERMITTED WITHOUT WRITTEN CONSENT.

DO NOT SCALE THE DRAWINGS. USE ALL DIMENSIONS SHOWN. VERIFY ALL DIMENSIONS ON SITE & NOTIFY ARCHITECT OF ANY DISCREPANCIES.

No.	Date	Description

PROJECT NAME:

PIGNATELLI RESIDENCE

11 SILVER HILL RD
WESTON, MA

REGISTERED ARCHITECT
CHARLES E. KRAUS
No. 10560
BOSTON
MASS.
COMMONWEALTH OF MASSACHUSETTS

DRAWING NAME:

FOUNDATION PLAN

DATE:	03.16.2023
PROJECT NO:	21031
SCALE:	1/4" = 1'-0"
DRAWN & CHECKED BY:	JJ/CK

DRAWING NO:

A3.1

2023.03.16 - PROGRESS SET