

DASHWOOD TRAILS

HOUSTON, HARRIS COUNTY, TEXAS

PROJECT INFORMATION

SITE DATA					
SITE ZONING:		(SEE CIVIL)			
SITE SIZE:		(SEE CIVIL)			
SITE DENSITY:		(SEE CIVIL)			
NO. OF PARKING SPACES:		(SEE CIVIL)			
BUILDING DATA					
DWELLING UNITS	LABEL	COMPLIANCE WITH	SQ FT	QTY	SUBTOTAL
1-BR UNIT	FHA	FHA	648	25	16,200 SF
1-BR UNIT	FHA/HV	FHA/HV	648	1	648 SF
1-BR UNIT	ADA	ADA	648	2	1,296 SF
2-BR UNIT	FHA	FHA	856	65	55,640 SF
2-BR UNIT	FHA/HV	FHA/HV	856	1	856 SF
2-BR UNIT	ADA	ADA	856	2	1,712 SF
3-BR UNIT	FHA	FHA	1064	1	1,064 SF
3-BR UNIT	ADA	ADA	1064	1	1,064 SF
DWELLING UNIT AREA:				98	78,480 SF
NON-DWELLING AREA:					25,500 SF
TOTAL BUILDING AREA:					103,980 SF
TOTAL RENTAL UNITS:		(98) TOTAL UNITS: (28) 1-BR UNITS, (68) 2-BR UNITS, (2) 3-BR UNITS			
CODES AND REGULATIONS					
BLDG. & RELATED CODES:		2021 IBC, 2021 IPC, 2021 IMC, 2021 IECC			
ELECT. CODE:		2020 NEC			
FIRE CODE:		2021 IFC			
ACCESSIBILITY:		ICC A117.1-2017; FAIR HOUSING AT UNITS AND AT COMMON AREAS; ADA 2010 AT UNITS AND PUBLIC USE AREAS & 2012 TEXAS ACCESSIBILITY STANDARDS INCLUDING IBC SECTION 102.2; TAS SECTION 1.1			
AGENCY:		TDHCA STATE POLICIES AND GUIDELINES			
MISC.:		ALL APPLICABLE FEDERAL, STATE, LOCAL CODES, LAWS AND ORDINANCES			
BUILDING CODE DATA					
USE GROUP:		R-2 (DWELLING UNITS, CORRIDORS, STAIRS, COMMUNITY ROOM, MAILBOXES AREA, FOYER / WAITING AREA, KITCHENETTE, FITNESS ROOM, LAUNDRY & ELEVATOR); A-3 (OTHER COMMON AREAS); UNSEPARATED MIXED USE			
CONSTRUCTION TYPE:		5A (RESIDENTIAL)			
EXT. WALL CONSTRUCTION:		1-HR RATED EXTERIOR WALLS			
OTHER CONSTRUCTION:		1-HR RATED UNIT SEPARATION WALLS, ROOF/CEILING, FLOOR/CEILING, BEAMS, COLUMNS, CORRIDOR WALLS; 2-HR RATED STAIR SHAFT & ELEVATOR SHAFT; 2-HR RATED FIREWALL; 1 1/2 HR RATED HORIZONTAL EXIT; UNRATED INTERIOR WALLS AND COMMON AREA INTERIOR WALLS.			
ALLOW. AREA PER FLOOR AREA:		R-2 = 12,000 SF			
AREA ADJUSTMENTS:		FRONTAGE INCREASE R-2 = 12,000(100-25) X 30/30 = 9,000 SF/FLOOR INCREASE = 21,000 SF/ FLOOR TOTAL ALLOWABLE FOR R-2 PER FLOOR AREA			
ACTUAL AREA PER FLOOR:		1ST FLOOR = 17,594 SF LEFT SIDE & 8,494 SF RIGHT SIDE OF FIRE WALL; 2ND FLOOR = 17,470 SF LEFT SIDE & 8,494 SF RIGHT SIDE OF FIRE WALL; 3RD FLOOR = 17,470 SF LEFT SIDE & 8,494 SF RIGHT SIDE OF FIRE WALL; 4TH FLOOR = 17,470 SF LEFT SIDE & 8,494 SF RIGHT SIDE OF FIRE WALL			
ALLOW. HEIGHT & FLOORS:		R-2 = 60'-0", 4 STORIES			
HEIGHT ADJUSTMENTS:		NONE REQUIRED, NONE TAKEN			
ACTUAL HEIGHT & FLOORS:		55'-3 1/8", 4 STORIES			
SPRINKLER SYSTEM:		NFPA 13R DESIGNED AND INSTALLED BY ACCREDITED FIRE PROTECTION SYSTEM DESIGNER AND INSTALLER. PROTECTION SHALL INCLUDE ALL AREAS AS APPLICABLE BY LOCAL AND STATE CODES. COORDINATE WITH GC/OWNER REGARDING THE INSTALLATION OF THE WET/DRY FIRE SUPPRESSION SYSTEM FOR UNCONDITIONED FREEZE PROTECTION PER O.O CODE DATA, PROVIDE FLEXIBLE DRY HEADS AT BALCONIES, PROVIDE FREEZE PROTECTED SOFFITS ON THE TOP FLOOR PER O.O CODE DATA INFORMATION. THIS COORDINATION SHOULD BE INCLUDED IN THE BASE BID.			


INDEX TO DRAWINGS

Sheet Number	Sheet Name	Sheet Issue Date	Current Revision Date	Current Revision Description
1 - COVER SHEET	COVER SHEET	25 OCT 2024	25 OCT 2024	ISSUE SET
2 - CIVIL SHEETS (BY CARLSON CONSULTING ENGINEERS, INC.)	CIVIL SHEETS SUBMITTED UNDER SEPARATE COVER	25 OCT 2024	25 OCT 2024	ISSUE SET
3 - STRUCTURAL SHEETS (BY CROCKETT ENGINEERING CONSULTANTS)				
S100	GENERAL STRUCTURAL DATA	25 OCT 2024	25 OCT 2024	ISSUE SET
S200	FOUNDATION PLAN	25 OCT 2024	25 OCT 2024	ISSUE SET
S201	FOUNDATION PLAN	25 OCT 2024	25 OCT 2024	ISSUE SET
S210	FOUNDATION DETAILS	25 OCT 2024	25 OCT 2024	ISSUE SET
S211	FOUNDATION DETAILS	25 OCT 2024	25 OCT 2024	ISSUE SET
S300	2ND FLOOR FRAMING PLAN	25 OCT 2024	25 OCT 2024	ISSUE SET
S300A	SHEAR WALL PLAN	25 OCT 2024	25 OCT 2024	ISSUE SET
S301	2ND FLOOR FRAMING PLAN	25 OCT 2024	25 OCT 2024	ISSUE SET
S301A	SHEAR WALL PLAN	25 OCT 2024	25 OCT 2024	ISSUE SET
S400	3RD FLOOR FRAMING PLAN	25 OCT 2024	25 OCT 2024	ISSUE SET
S401	3RD FLOOR FRAMING PLAN	25 OCT 2024	25 OCT 2024	ISSUE SET
S500	4TH FLOOR FRAMING PLAN	25 OCT 2024	25 OCT 2024	ISSUE SET
S501	4TH FLOOR FRAMING PLAN	25 OCT 2024	25 OCT 2024	ISSUE SET
S610	FLOOR FRAMING DETAILS	25 OCT 2024	25 OCT 2024	ISSUE SET
S611	FLOOR FRAMING DETAILS	25 OCT 2024	25 OCT 2024	ISSUE SET
S600	ROOF FRAMING PLAN	25 OCT 2024	25 OCT 2024	ISSUE SET
S601	ROOF FRAMING PLAN	25 OCT 2024	25 OCT 2024	ISSUE SET
S610	ROOF FRAMING DETAILS	25 OCT 2024	25 OCT 2024	ISSUE SET
S611	ROOF FRAMING DETAILS	25 OCT 2024	25 OCT 2024	ISSUE SET
S612	ROOF FRAMING DETAILS	25 OCT 2024	25 OCT 2024	ISSUE SET
4 - ARCHITECTURAL SITE				
AS1.0	ARCHITECTURAL SITE PLAN	25 OCT 2024	25 OCT 2024	ISSUE SET
ASD1.0	ARCHITECTURAL SITE DETAILS	25 OCT 2024	25 OCT 2024	ISSUE SET
5 - ARCHITECTURAL				
A1.0	FIRST FLOOR EAST SIDE BUILDING PLAN	25 OCT 2024	25 OCT 2024	ISSUE SET
A1.1	FIRST FLOOR WEST SIDE BUILDING PLAN	25 OCT 2024	25 OCT 2024	ISSUE SET
A1.2	SECOND FLOOR EAST SIDE BUILDING PLAN	25 OCT 2024	25 OCT 2024	ISSUE SET
A1.3	SECOND FLOOR WEST SIDE BUILDING PLAN	25 OCT 2024	25 OCT 2024	ISSUE SET
A1.4	THIRD FLOOR EAST SIDE BUILDING PLAN	25 OCT 2024	25 OCT 2024	ISSUE SET
A1.5	THIRD FLOOR WEST SIDE BUILDING PLAN	25 OCT 2024	25 OCT 2024	ISSUE SET
A1.6	FOURTH FLOOR EAST SIDE BUILDING PLAN	25 OCT 2024	25 OCT 2024	ISSUE SET
A1.7	FOURTH FLOOR WEST SIDE BUILDING PLAN	25 OCT 2024	25 OCT 2024	ISSUE SET
A1.8	1-BR UNIT DIMENSION PLANS, DOOR SCHEDULE, WALL TYPES & NOTES	25 OCT 2024	25 OCT 2024	ISSUE SET
A1.9	2-BR & 3-BR UNIT DIMENSION PLANS	25 OCT 2024	25 OCT 2024	ISSUE SET
A1.10	FIRST FLOOR COMMON AREA DIMENSION PLANS	25 OCT 2024	25 OCT 2024	ISSUE SET
A1.11	SECOND FLOOR COMMON AREA DIMENSION PLANS	25 OCT 2024	25 OCT 2024	ISSUE SET
A1.12	THIRD FLOOR COMMON AREA DIMENSION PLANS	25 OCT 2024	25 OCT 2024	ISSUE SET
A1.13	FOURTH FLOOR COMMON AREA DIMENSION PLANS	25 OCT 2024	25 OCT 2024	ISSUE SET
A1.14	1-BR UNIT ACCESSIBILITY PLANS	25 OCT 2024	25 OCT 2024	ISSUE SET
A1.15	2-BR & 3-BR UNIT ACCESSIBILITY PLANS	25 OCT 2024	25 OCT 2024	ISSUE SET
A1.16	FIRST FLOOR COMMON AREA ACCESSIBILITY PLANS	25 OCT 2024	25 OCT 2024	ISSUE SET
A1.17	SECOND FLOOR COMMON AREA ACCESSIBILITY PLANS	25 OCT 2024	25 OCT 2024	ISSUE SET
A1.18	THIRD & FOURTH FLOOR COMMON AREA ACCESSIBILITY PLANS	25 OCT 2024	25 OCT 2024	ISSUE SET
A2.0	BUILDING LEFT SIDE ROOF PLAN, DETAILS AND NOTES	25 OCT 2024	25 OCT 2024	ISSUE SET
A2.1	BUILDING RIGHT SIDE ROOF PLAN	25 OCT 2024	25 OCT 2024	ISSUE SET
A3.0	EXTERIOR ELEVATIONS	25 OCT 2024	25 OCT 2024	ISSUE SET
A3.1	EXTERIOR ELEVATIONS	25 OCT 2024	25 OCT 2024	ISSUE SET
A3.2	EXTERIOR ELEVATIONS	25 OCT 2024	25 OCT 2024	ISSUE SET
A4.0	WALL SECTIONS	25 OCT 2024	25 OCT 2024	ISSUE SET
A4.1	WALL SECTIONS	25 OCT 2024	25 OCT 2024	ISSUE SET
A4.2	WALL SECTIONS	25 OCT 2024	25 OCT 2024	ISSUE SET
A4.3	ELEVATOR WALL SECTIONS	25 OCT 2024	25 OCT 2024	ISSUE SET
A4.4	FRAMING DETAILS	25 OCT 2024	25 OCT 2024	ISSUE SET
A4.5	FLASHING DETAILS	25 OCT 2024	25 OCT 2024	ISSUE SET
A4.6	STAIR DETAILS	25 OCT 2024	25 OCT 2024	ISSUE SET
A5.0	FIRE RATED ASSEMBLIES	25 OCT 2024	25 OCT 2024	ISSUE SET
A5.1	FIRE RATED ASSEMBLIES	25 OCT 2024	25 OCT 2024	ISSUE SET
A5.2	FIRE RATED ASSEMBLIES	25 OCT 2024	25 OCT 2024	ISSUE SET
A5.3	FIRE RATED ASSEMBLIES	25 OCT 2024	25 OCT 2024	ISSUE SET
A5.4	FIRE RATED ASSEMBLIES	25 OCT 2024	25 OCT 2024	ISSUE SET

Sheet Number	Sheet Name	Sheet Issue Date	Current Revision Date	Current Revision Description
A6.0	1-BR UNIT FINISH PLANS, FINISH SCHEDULE & NOTES	25 OCT 2024	25 OCT 2024	ISSUE SET
A6.1	2-BR & 3-BR UNIT FINISH PLANS	25 OCT 2024	25 OCT 2024	ISSUE SET
A6.2	FIRST FLOOR COMMON AREA FINISH PLANS	25 OCT 2024	25 OCT 2024	ISSUE SET
A6.3	SECOND FLOOR COMMON AREA FINISH PLANS	25 OCT 2024	25 OCT 2024	ISSUE SET
A6.4	THIRD & FOURTH FLOOR COMMON AREA FINISH PLANS	25 OCT 2024	25 OCT 2024	ISSUE SET
A7.0	INTERIOR ELEVATIONS NOTES AND DETAILS	25 OCT 2024	25 OCT 2024	ISSUE SET
A7.1	ELECTRICAL MOUNTING HEIGHT ELEVATIONS	25 OCT 2024	25 OCT 2024	ISSUE SET
A7.2	1-BR UNIT INTERIOR ELEVATIONS	25 OCT 2024	25 OCT 2024	ISSUE SET
A7.3	2-BR UNIT INTERIOR ELEVATIONS & INTERIOR SIGNAGE DETAIL	25 OCT 2024	25 OCT 2024	ISSUE SET
A7.4	3-BR UNIT INTERIOR ELEVATIONS	25 OCT 2024	25 OCT 2024	ISSUE SET
A7.5	COMMON AREA INTERIOR ELEVATIONS	25 OCT 2024	25 OCT 2024	ISSUE SET
LS1.0	FIRST & SECOND FLOOR LIFE SAFETY PLANS	25 OCT 2024	25 OCT 2024	ISSUE SET
LS1.1	THIRD & FOURTH FLOOR LIFE SAFETY PLANS	25 OCT 2024	25 OCT 2024	ISSUE SET
6 - MECHANICAL, PLUMBING, ELECTRICAL (BY MALICOAT-WINSLOW ENGINEERS)				
ME1	MEP SITE PLAN	25 OCT 2024	25 OCT 2024	ISSUE SET
ME2	SCHEDULES	25 OCT 2024	25 OCT 2024	ISSUE SET
ME3	DETAILS	25 OCT 2024	25 OCT 2024	ISSUE SET
ME4	IECC CONTROL REQUIREMENTS	25 OCT 2024	25 OCT 2024	ISSUE SET
M1	1ST FLOOR E PLUMBING PLAN	25 OCT 2024	25 OCT 2024	ISSUE SET
M2	1ST FLOOR W PLUMBING PLAN	25 OCT 2024	25 OCT 2024	ISSUE SET
M3	2ND FLOOR E PLUMBING PLAN	25 OCT 2024	25 OCT 2024	ISSUE SET
M4	2ND FLOOR W PLUMBING PLAN	25 OCT 2024	25 OCT 2024	ISSUE SET
M5	3RD FLOOR E PLUMBING PLAN	25 OCT 2024	25 OCT 2024	ISSUE SET
M6	3RD FLOOR W PLUMBING PLAN	25 OCT 2024	25 OCT 2024	ISSUE SET
M7	4TH FLOOR E PLUMBING PLAN	25 OCT 2024	25 OCT 2024	ISSUE SET
M8	4TH FLOOR W PLUMBING PLAN	25 OCT 2024	25 OCT 2024	ISSUE SET
M9	1ST FLOOR E HVAC PLAN	25 OCT 2024	25 OCT 2024	ISSUE SET
M10	1ST FLOOR W HVAC PLAN	25 OCT 2024	25 OCT 2024	ISSUE SET
M11	2ND FLOOR E HVAC PLAN	25 OCT 2024	25 OCT 2024	ISSUE SET
M12	2ND FLOOR W HVAC PLAN	25 OCT 2024	25 OCT 2024	ISSUE SET
M13	3RD FLOOR E HVAC PLAN	25 OCT 2024	25 OCT 2024	ISSUE SET
M14	3RD FLOOR W HVAC PLAN	25 OCT 2024	25 OCT 2024	ISSUE SET
M15	4TH FLOOR E HVAC PLAN	25 OCT 2024	25 OCT 2024	ISSUE SET
M16	4TH FLOOR W HVAC PLAN	25 OCT 2024	25 OCT 2024	ISSUE SET
M17	3BR APT PLUMBING PLANS	25 OCT 2024	25 OCT 2024	ISSUE SET
M18	2-BR APT PLUMBING PLANS	25 OCT 2024	25 OCT 2024	ISSUE SET
M19	3BR APT HVAC PLANS	25 OCT 2024	25 OCT 2024	ISSUE SET
M20	2-BR APT HVAC PLANS	25 OCT 2024	25 OCT 2024	ISSUE SET
E1	1ST FLOOR E POWER PLAN	25 OCT 2024	25 OCT 2024	ISSUE SET
E2	1ST FLOOR W POWER PLAN	25 OCT 2024	25 OCT 2024	ISSUE SET
E3	2ND FLOOR E POWER PLAN	25 OCT 2024	25 OCT 2024	ISSUE SET
E4	2ND FLOOR W POWER PLAN	25 OCT 2024	25 OCT 2024	ISSUE SET
E5	3RD FLOOR E POWER PLAN	25 OCT 2024	25 OCT 2024	ISSUE SET
E6	3RD FLOOR W POWER PLAN	25 OCT 2024	25 OCT 2024	ISSUE SET
E7	4TH FLOOR E POWER PLAN	25 OCT 2024	25 OCT 2024	ISSUE SET
E8	4TH FLOOR W POWER PLAN	25 OCT 2024	25 OCT 2024	ISSUE SET
E9	1ST FLOOR E LIGHTING PLAN	25 OCT 2024	25 OCT 2024	ISSUE SET
E10	1ST FLOOR W LIGHTING PLAN	25 OCT 2024	25 OCT 2024	ISSUE SET
E11	2ND FLOOR E LIGHTING PLAN	25 OCT 2024	25 OCT 2024	ISSUE SET
E12	2ND FLOOR W LIGHTING PLAN	25 OCT 2024	25 OCT 2024	ISSUE SET
E13	3RD FLOOR E LIGHTING PLAN	25 OCT 2024	25 OCT 2024	ISSUE SET
E14	3RD FLOOR W LIGHTING PLAN	25 OCT 2024	25 OCT 2024	ISSUE SET
E15	4TH FLOOR E LIGHTING PLAN	25 OCT 2024	25 OCT 2024	ISSUE SET
E16	4TH FLOOR W LIGHTING PLAN	25 OCT 2024	25 OCT 2024	ISSUE SET
E17	3BR APT POWER PLANS	25 OCT 2024	25 OCT 2024	ISSUE SET
E18	2-BR APT POWER PLANS	25 OCT 2024	25 OCT 2024	ISSUE SET
E19	3BR APT LIGHTING PLANS	25 OCT 2024	25 OCT 2024	ISSUE SET
E20	2-BR APT LIGHTING PLANS	25 OCT 2024	25 OCT 2024	ISSUE SET
E21	ELECTRICAL RISER DIAGRAM	25 OCT 2024	25 OCT 2024	ISSUE SET
FA1	1ST FLOOR E FIRE ALARM PLAN	25 OCT 2024	25 OCT 2024	ISSUE SET
FA2	1ST FLOOR W FIRE ALARM PLAN	25 OCT 2024	25 OCT 2024	ISSUE SET
FA3	2ND FLOOR E FIRE ALARM PLAN	25 OCT 2024	25 OCT 2024	ISSUE SET
FA4	2ND FLOOR W FIRE ALARM PLAN	25 OCT 2024	25 OCT 2024	ISSUE SET
FA5	3RD FLOOR E FIRE ALARM PLAN	25 OCT 2024	25 OCT 2024	ISSUE SET
FA6	3RD FLOOR W FIRE ALARM PLAN	25 OCT 2024	25 OCT 2024	ISSUE SET
FA7	4TH FLOOR E FIRE ALARM PLAN	25 OCT 2024	25 OCT 2024	ISSUE SET
FA8	4TH FLOOR W FIRE ALARM PLAN	25 OCT 2024	25 OCT 2024	ISSUE SET

ARCHITECT'S JOB NO. 4809
TDHCA & PROJECT #24-221

PROJECT LOCATION MAP

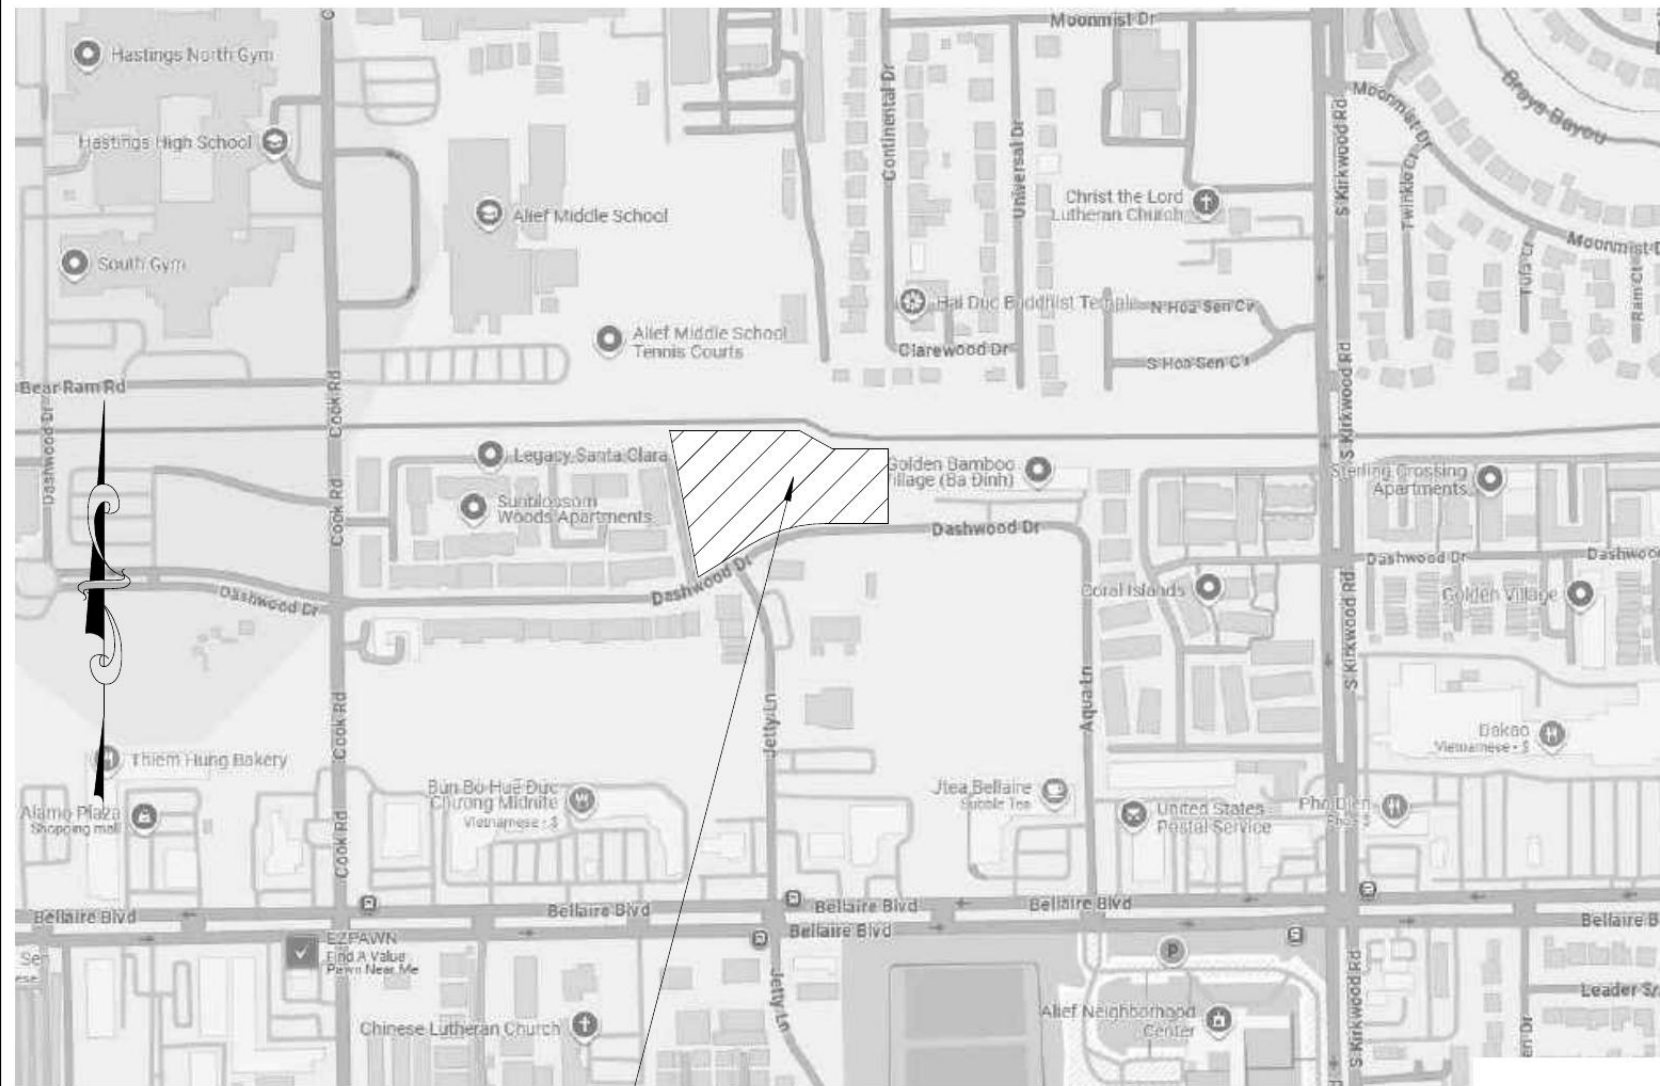

SIGNATURE AREAS


NOTE: PROJECT CONSTRUCTION MUST BE IN COMPLIANCE WITH ALL APPLICABLE CODES, OF LAWS, AND REGULATIONS AS ENUMERATED ELSEWHERE IN THE PLANS AND SPECIFICATION

ARCHITECT: WALLACE ARCHITECTS, LLC
302 CAMPUSVIEW DRIVE SUITE 208, COLUMBIA, MO 65201
BY: _____ DATE: _____

OWNER: DASHWOOD TRAILS, LP
3556 S. CULPEPPER CIRCLE, SUITE 4, SPRINGFIELD, MO 65804
BY: _____ DATE: _____

CONTRACTOR: HAMILTON BUILDERS CONTRACTING, LLC
3556 S. CULPEPPER CIRCLE, SUITE 4, SPRINGFIELD, MO 65804
BY: _____ DATE: _____

TDHCA REPRESENTATIVE:
221 EAST 11TH STREET, AUSTIN, TX 78701-2410
BY: _____ DATE: _____

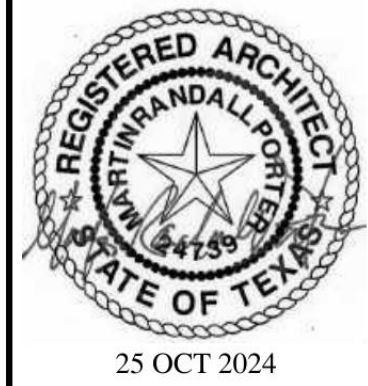

DASHWOOD TRAILS
HOUSTON, HARRIS COUNTY, TEXAS

