

KIRKLAND NOTES

- A). REINSTALL ANY AND ALL REMOVED ROW SIGNS PER CITY STANDARDS.
- B). A 2-INCH ASPHALT STREET OVERLAY WILL BE REQUIRED WHERE MORE THAN THREE UTILITY TRENCH CROSSINGS OCCUR WITHIN 150 LINEAR FT OF STREET LENGTH OR WHERE UTILITY TRENCHES PARALLEL THE STREET CENTERLINE. GRINDING OF THE EXISTING ASPHALT TO BLEND IN THE OVERLAY WILL BE REQUIRED ALONG ALL MATCH LINES.
- C). REMOVE AND REPLACE ANY EXISTING DAMAGED SIDEWALK OR CRACKED CURB AND GUTTER.
- D). UNDERGROUND ALL NEW AND EXISTING ON-SITE TRANSMISSION LINES FROM THE BUILDING TO THE POINT OF ORIGIN AT THE PRIMARY/DISTRIBUTION LINES FOR THE UTILITIES.
- E). ADJUST ANY EXISTING UTILITY WHICH MAY CONFLICT WITH STREET OR UTILITY IMPROVEMENTS.
- F). ANY WALKWAY ADJACENT TO AN AREA WITH A DROP OF OVER 30" WILL REQUIRE GUARD RAIL PROTECTION PER DETAIL CK-R.51.
- G). ALL BACK FILL ON NE MARKET ST SHALL BE CONTROL DENSITY FILL (CDF).
- H). ABANDON EXISTING WATER SERVICE AT THE MAIN.

GEOTECHNICAL ENGINEERING REPORT

SEE REPORT BY GEOTECHNICAL CONSULTANTS FOR ALL RECOMMENDATIONS RELATED TO FOUNDATION, SOLDIER PILE WALL AND DRAINAGE, UNDERSLAB DRAINAGE, ETC.

DEWATERING & BAKER TANK

GENERAL CONTRACTOR & OWNER SHOULD READ CITY POLICY E-1 BEFORE PROJECT EXCAVATION BEGINS. A DEWATERING PERMIT ALLOWING DISCHARGE TO CITY SEWER OR POTENTIAL NEED FOR A SETTLING TANK (BAKER TANK OR EQUAL) SHOULD BE ANTICIPATED BY CONTRACTOR.

DISCHARGE TO CITY STORM REQUIRES TDU BELOW 25 ntu. ANY DISCHARGE ABOVE 25 REQUIRES DISCHARGE TO SEWER SYSTEM AND PERMIT FROM KING COUNTY.

FOLLOWING IS BAKER TANK CONTACT:
BAKER TANKS
6100 - 238th St. SE
Woodinville, WA 98072
Phone: (425) 487-6503
Or 1-800-225-3712
www.bakercorp.com

- 3) Before discharging to the sanitary sewer:
- Notify the City of Kirkland, Public Works Inspector at (425) 587-3800.
 - All projects (except Single Family Infill) must obtain permit authorization from the King County Industrial Waste Program (206-263-3000). More information is available at the website listed below.


Single family infill projects may discharge to sanitary sewer without a permit from King County Industrial Waste Program as long as the discharge is less than 7 mg/L of suspended solids.

EROSION CONTROL LEGEND

LIMITS OF DISTURBANCE	
FILTER FABRIC FENCE (SILT FENCE)	CK E.03 (SF) — x — x —
STABILIZED CONSTRUCTION ENTRANCE	CK E.01 (CE) [Symbol]
CATCH BASIN INLET PROTECTION	CK E.08 (IP) [Symbol]
TREE PROTECTION FENCING	CK R.49 (TP) — o — o — o —
CHECK DAM	(CD) [Symbol]
STRAW WATTLES	CK E.10 (SW) USE AS NEEDED
PLASTIC COVERING	(PC) COVER EXPOSED AREAS WITHIN KIRKLAND TIME LIMIT
COMPOST SOCK	(CS) SEDIMENT CONTROL OPTION RECOMMENDED IN LIEU OF SILT FENCE
COMPOST BERM	(CB) SEDIMENT CONTROL OPTION RECOMMENDED IN LIEU OF SILT FENCE

EROSION CONTROL NOTES & DETAILS

SEE SHEET C1.1

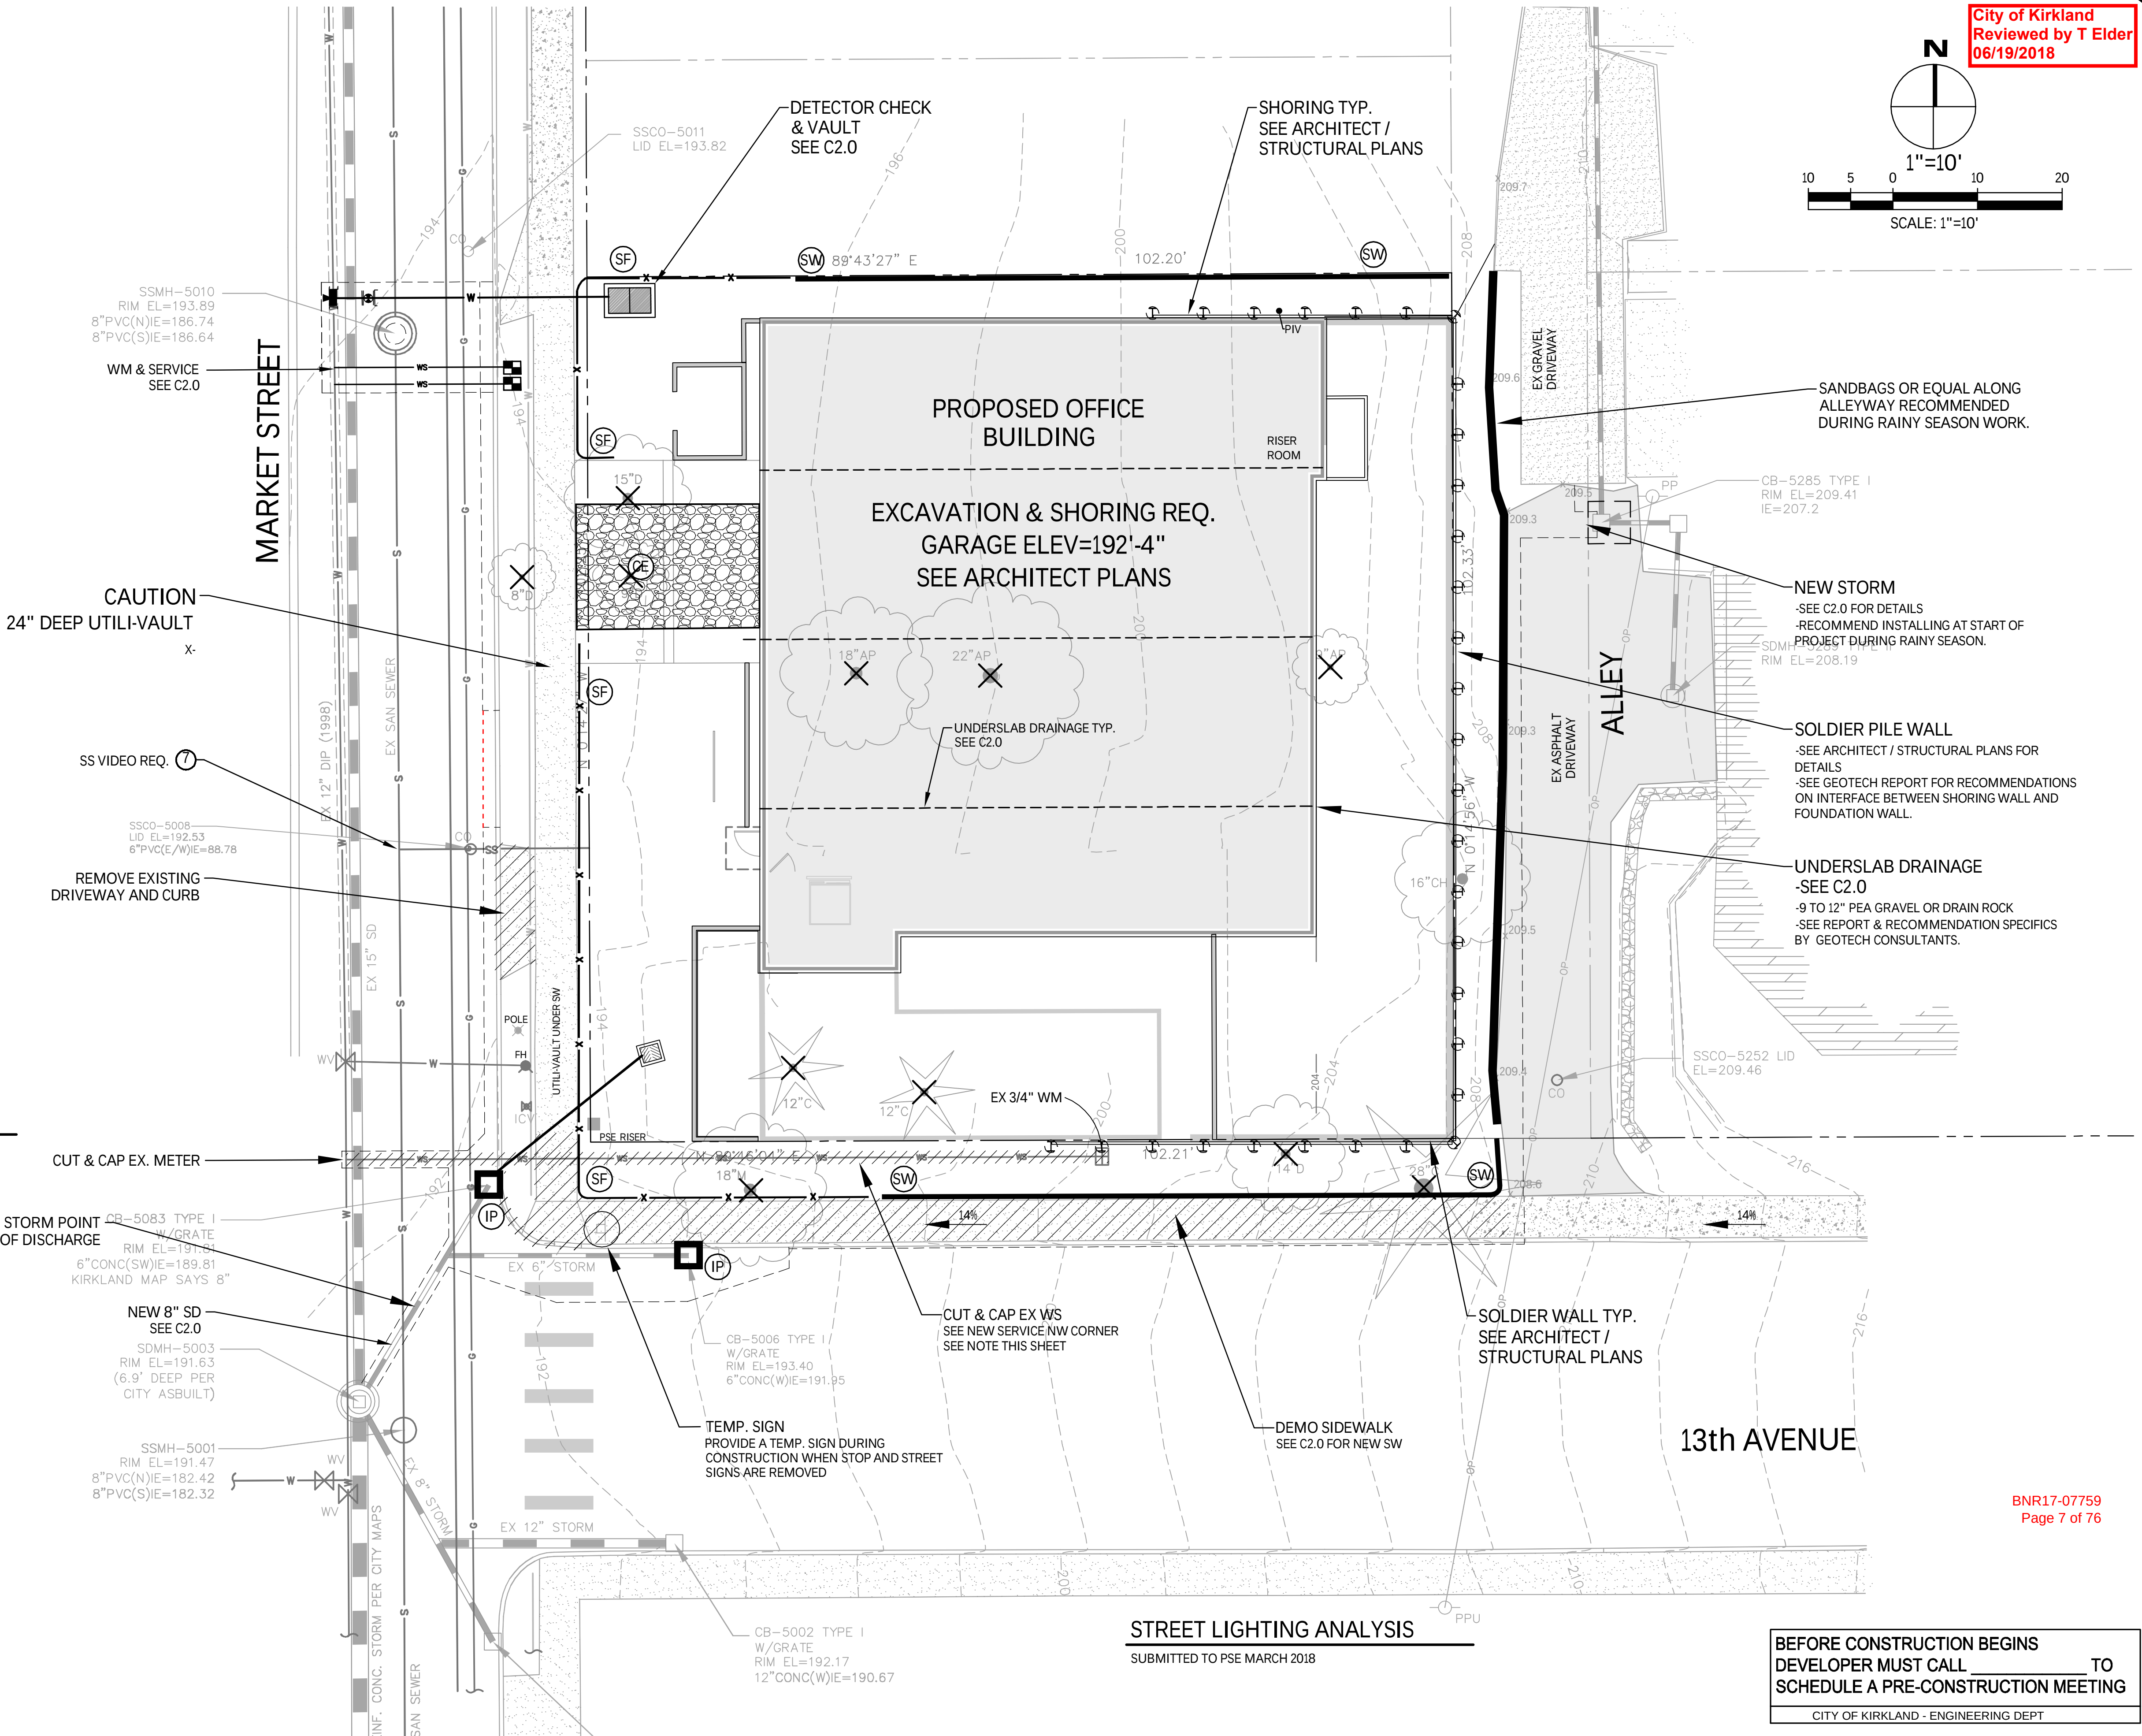

STREET LIGHTING ANALYSIS

SUBMITTED TO PSE MARCH 2018

BEFORE CONSTRUCTION BEGINS
DEVELOPER MUST CALL _____ TO
SCHEDULE A PRE-CONSTRUCTION MEETING

CITY OF KIRKLAND - ENGINEERING DEPT


NO.	DATE	BY	REVISIONS

APPLICANT



THIS DEVELOPMENT SHALL BE CONSTRUCTED IN ACCORDANCE WITH THE 2017 CITY OF KIRKLAND STANDARD SPECIFICATIONS AND DETAILS.

DATE:	May 25, 2018
JOB#:	1599
DRAFTED:	CH DESIGN: DE
DIGITAL SIGNATURE	

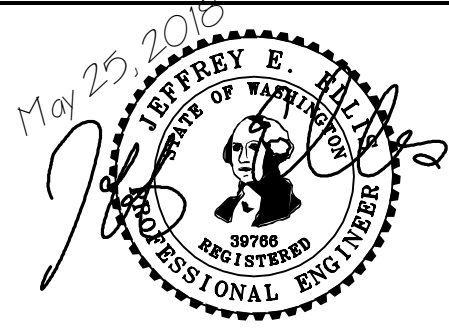

CIVIL ENGINEERING SOLUTIONS

102 NW CANAL STREET
PHONE: 206.930.0342
SEATTLE, WA 98107
DUFFY@CESOLUTIONS.US

TEMPORARY EROSION & SEDIMENT CONTROL

1302 MARKET STREET OFFICE
1302 MARKET STREET, KIRKLAND 98033

DRAWING NO:

C1.0

APN 388580-4140
BNR17-07759

BNR17-07759
Page 7 of 76