

BUILDING 500 EXTERIOR CANOPY SHELTER

HORRY-GEORGETOWN TECHNICAL COLLEGE
4003 SOUTH FRASER STREET
GEORGETOWN, SC 29440


SOUTH CAROLINA STATE PROJECT NUMBER
H59-N269-CB HGTC BLDG. 500 EXTERIOR RENOVATION



SYMBOLS LEGEND

DRAWING TITLE DRAWING I.D. NUMBER 1 FLOOR PLAN SCALE: 3/16" = 1'-0"	DETAIL (ENLARGEMENT) DRAWING I.D. NUMBER 1 A13 AREA TO BE ENLARGED SHEET NUMBER
BUILDING SECTION DRAWING I.D. NUMBER SHEET NUMBER 1 A2.13	BUILDING SECTION DRAWING I.D. NUMBER SHEET NUMBER 1 A2.13
WALL SECTION DRAWING I.D. NUMBER SHEET NUMBER 1 A1.22	WALL SECTION DRAWING I.D. NUMBER SHEET NUMBER 1 A1.22
1 COLUMN REFERENCE NUMBER COLUMN CENTER LINE	A COLUMN REFERENCE NUMBER COLUMN CENTER LINE
ELEVATION SECTION I.D. NUMBER SHEET NUMBER 1 A1.22	ELEVATION HEIGHT LEVEL REFERENCE LEVEL ELEVATION HEIGHT
REVISIONS ADDENDUM NUMBER REVISED AREA	ROOM NUMBER ROOM NAME ROOM NUMBER SQUARE FOOTAGE VESTIBULE
CEILING HEIGHT CEILING HEIGHT ABOVE FINISHED FLOOR 9'-6"	DOOR NUMBER DOOR NUMBER DESIGNATION 1
KEYED NOTES KEYED NOTE DESIGNATION 1	WINDOW NUMBER WINDOW NUMBER DESIGNATION A
FINISH MATERIAL FINISH DESIGNATION, TRIM ONLY COMMENTS, IF APPLICABLE P-1	NORTH ARROW TRUE PROJECT NORTH
INTERIOR ELEVATION TAG ELEVATION NOTATION DETAIL NUMBER DIRECTION OF ELEVATION REFERENCE DRAWING NUMBER A3.33	TOILET ACCESSORIES ACCESSORY NUMBER DESIGNATION PD7
FIRE EXTINGUISHER WALL HUNG	EQUIPMENT NUMBER ACCESSORY NUMBER DESIGNATION AH-12
	WITH CABINET

VICINITY MAP

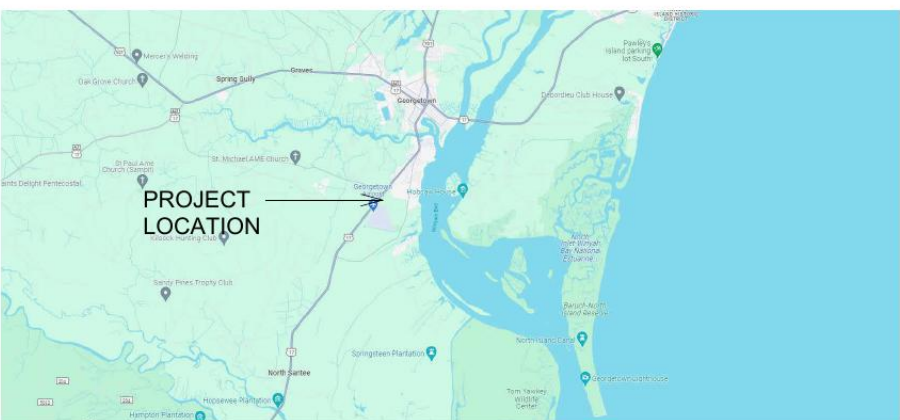

CONTACT LIST

OWNERS
CLIENT NAME: DIANNA CECALA / KEVIN BROWN
ORGANIZATION NAME: HORRY-GEORGETOWN TECH COLLEGE, BUILDING 500
ORGANIZATION ADDRESS: 2050 HWY 501 EAST, CONWAY SC 29526
TELEPHONE: 803-651-7900
EMAIL: DIANNA.CECALA@HGTC.EDU
KEVIN.BROWN@HGTC.EDU

ARCHITECT & STRUCTURAL ENGINEER
EARTHWORKS GROUP, INC.
ATTN: STEVE STRICKLAND / CHARLES MILLONZI
11655 HWY 707
MURRELLS INLET, SC 29576
TELEPHONE: 843-651-7900
EMAIL: STRICKLAND@EARTHWORKSGROUP.COM
CMILLONZI@EARTHWORKSGROUP.COM

ELECTRICAL \ HVAC \ PLUMBING ENGINEER
EARTHWORKS GROUP, INC.
ATTN: CHRIS J. HAMMEL, P.E.
7410 S HIGHWAY 1, SUITE 104
PORT ST. LUCIE, FL 34952
TELEPHONE: 888-451-7788
EMAIL: CHAMMEL@EARTHWORKSGROUP.COM

EARTHWORKS

planning and design consultants

11655 HIGHWAY 707, MURRELLS INLET, SC 29576
843.651.7900 / www.earthworksgroup.com

ISSUED ONLY FOR:	ACCEPTANCE BY:
☐ SCHEMATIC DESIGN APPROVAL	1st Owner: _____
☒ DESIGN DEVELOPMENT APPROVAL	Date: _____
☐ CONSTRUCTION DOCUMENTS APPROVAL	2nd Owner: _____
☐ STRUCTURAL DESIGN APPROVAL	Date: _____
☐ M-E-P DESIGN APPROVAL	

BUILDING CODES UTILIZED

2021 INTERNATIONAL BUILDING CODE
2021 INTERNATIONAL EXISTING BUILDING CODE
2021 INTERNATIONAL MECHANICAL CODE
2021 INTERNATIONAL FIRE CODE
2021 INTERNATIONAL PLUMBING CODE
2021 INTERNATIONAL FUEL GAS CODE
2021 NATIONAL ELECTRIC CODE
2021 INTERNATIONAL ENERGY CONSERVATION CODE
2021 ICC A117.1 ACCESSIBILITY CODE
NFPA STANDARDS
(AS ADOPTED BY THE OFFICE OF STATE FIRE MARSHAL)

ABBREVIATIONS

A.D.A.	AMERICANS WITH DISABILITIES ACT
A.F.F.	ABOVE FINISHED FLOOR
A/C	AIR CONDITIONING
ALUM.	ALUMINUM
BLDG.	BUILDING
C/C	CENTER TO CENTER
CL	CENTER LINE
CMU	CONCRETE MASONRY UNIT
D.F.	DRINKING FOUNTAIN
DIA.	DIAMETER
DWG.	DRAWING
E.I.F.S.	EXTERIOR INSULATION FINISH SYSTEM ELECTRICAL
ELEC.	ELECTRIC WATER COOLER
EWV	ELECTRIC WATER HEATER
EWI	FLOOR DRAIN
F.D.	FIRE EXTINGUISHER
F.F.	FINISH FLOOR
FIN.FLR.	GENERAL CONTRACTOR
G.C.	GALLONS PER HOUR
G.P.H.	GROUND FAULT INTERCEPT CIRCUIT
G.F.I.C.	GYPSUM BOARD
GYP.BD.	HEATING VENTILATION AND AIR
HVAC	CONDITIONING
IBC	INTERNATIONAL BUILDING CODE
MFR.	MANUFACTURER
MIN.	MINIMUM
MTL.	METAL
N.I.C.	NOT IN CONTRACT
N.T.S.	NOT TO SCALE
N/A	NOT APPLICABLE
#	NUMBER
O.C.	ON CENTER
P.E.	PHOTO-ELECTRIC
PLBG.	PLUMBING
PLYWD.	PLYWOOD
PVC	POLY-VINYL CHLORIDE
R.D.	ROOF DRAIN
R.O.	ROUGH OPENING
R.R.	RESTROOM
RTU	ROOF TOP UNIT
S/S	STAINLESS STEEL
SPECS.	SPECIFICATIONS
SS	SANITARY SEWER
ST.	STORM DRAIN
TYP.	TYPICAL
U.L.	UNDERWRITERS LABORATORIES
U.N.O.	UNLESS NOTED OTHERWISE
V.C.T.	VINYL COMPOSITE TILE
VTR	VENT THROUGH ROOF
W.C.	WATER CLOSET
W.H.	WATER HEATER
W/	WITH
WC	WATER CLOSET

INDEX OF DRAWINGS

G1.01	PROJECT COVERSHEET
G1.02	SPECIAL INSPECTIONS
G1.03	LIFE SAFETY PLAN / CODE REVIEW
C1.01	EXISTING CONDITIONS
A1.01	EXISTING FLOOR PLAN
A1.02	PROPOSED FLOOR PLAN
A1.03	PROPOSED FOUNDATION PLAN
A1.04	PROPOSED ROOF PLAN
A2.01	EXISTING EXTERIOR ELEVATIONS
A2.02	PROPOSED EXTERIOR ELEVATIONS
A3.01	BUILDING SECTIONS
A3.02	BUILDING SECTIONS
A6.01	DOOR SCHEDULE & DETAILS
P1.01	PLUMBING PLAN
E1.01	ELECTRICAL PLAN
S1.01	FOUNDATION PLAN
S2.01	STRUCTURAL DETAILS
S3.01	STRUCTURAL NOTES