



46226
PROJECT VICINITY




PROJECT LOCATION

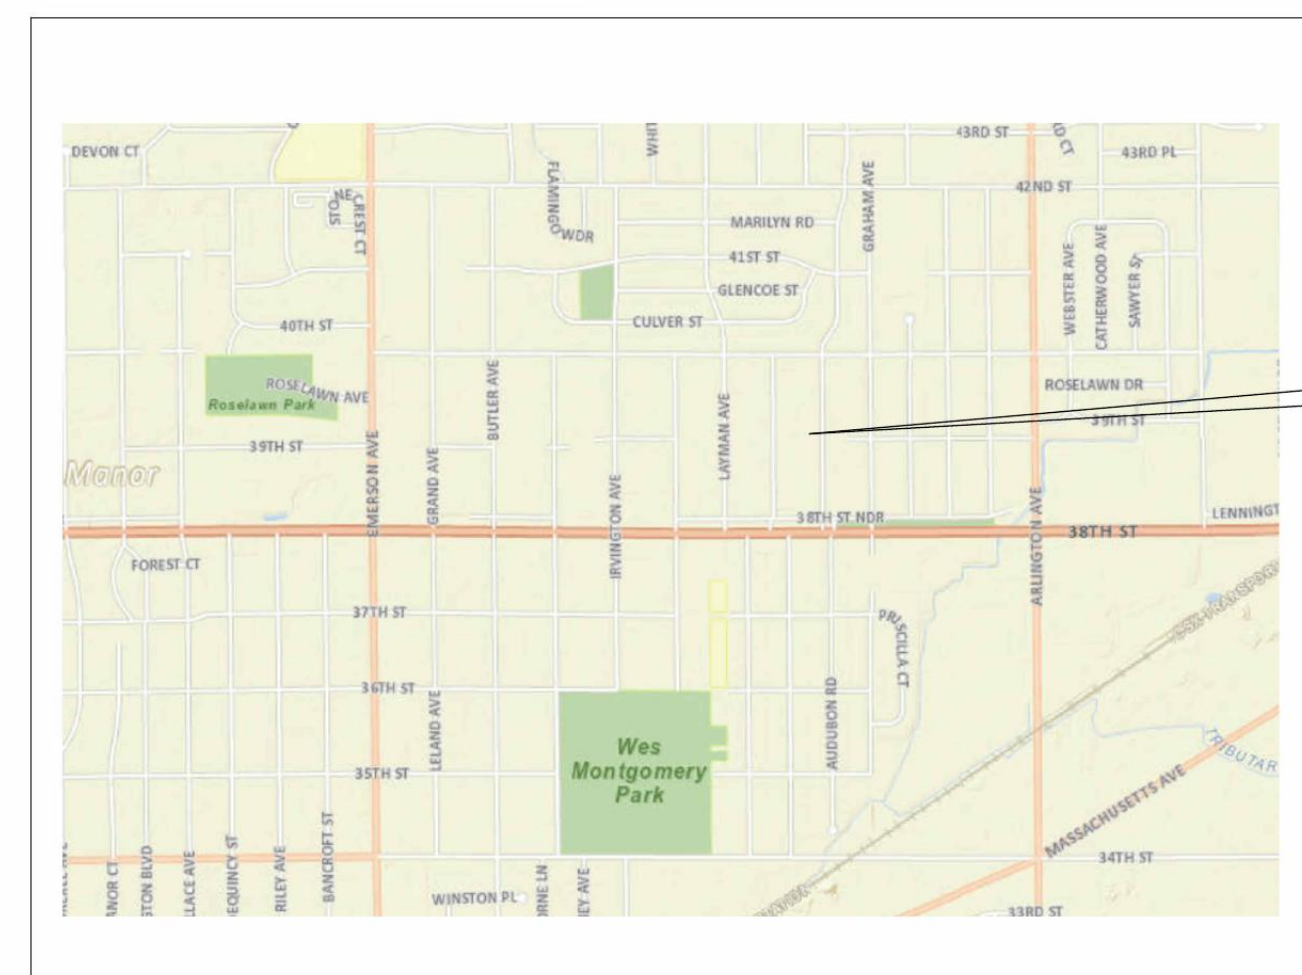

DRAWING SYMBOLS LEGEND

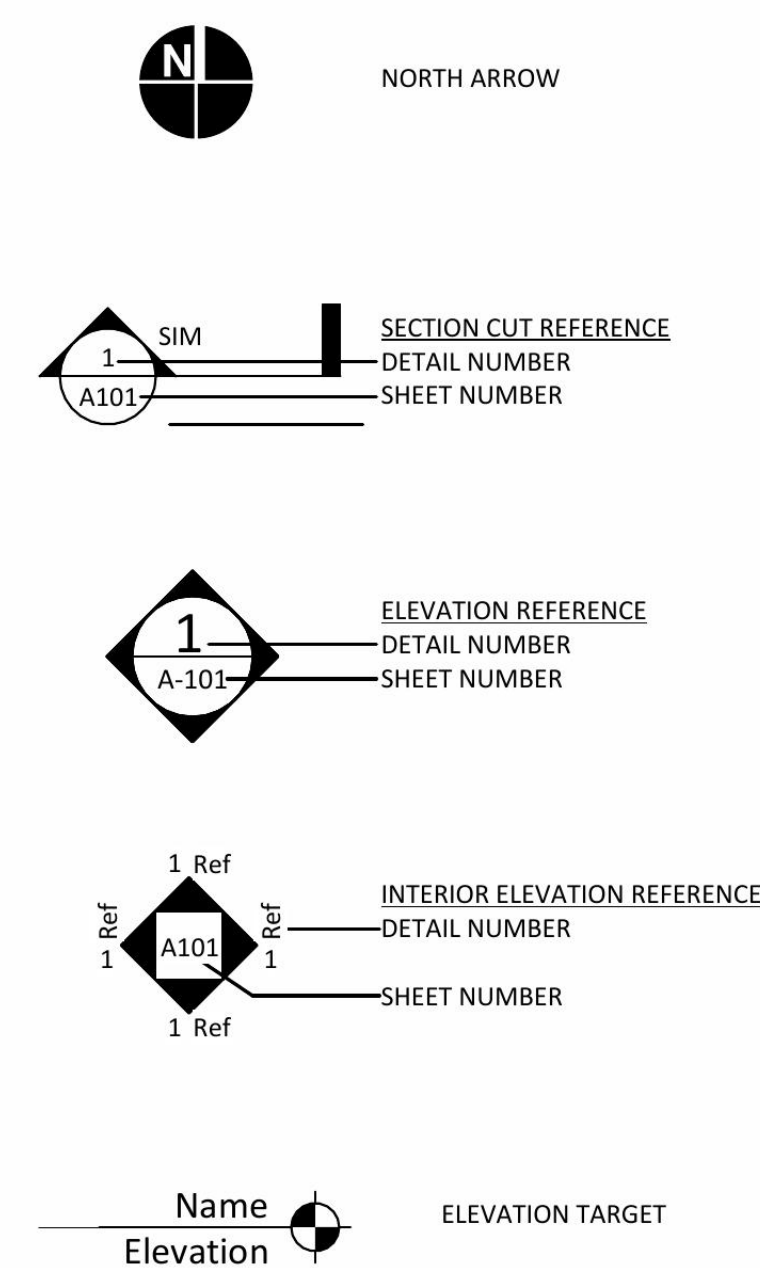

MATERIAL SYMBOLS LEGEND

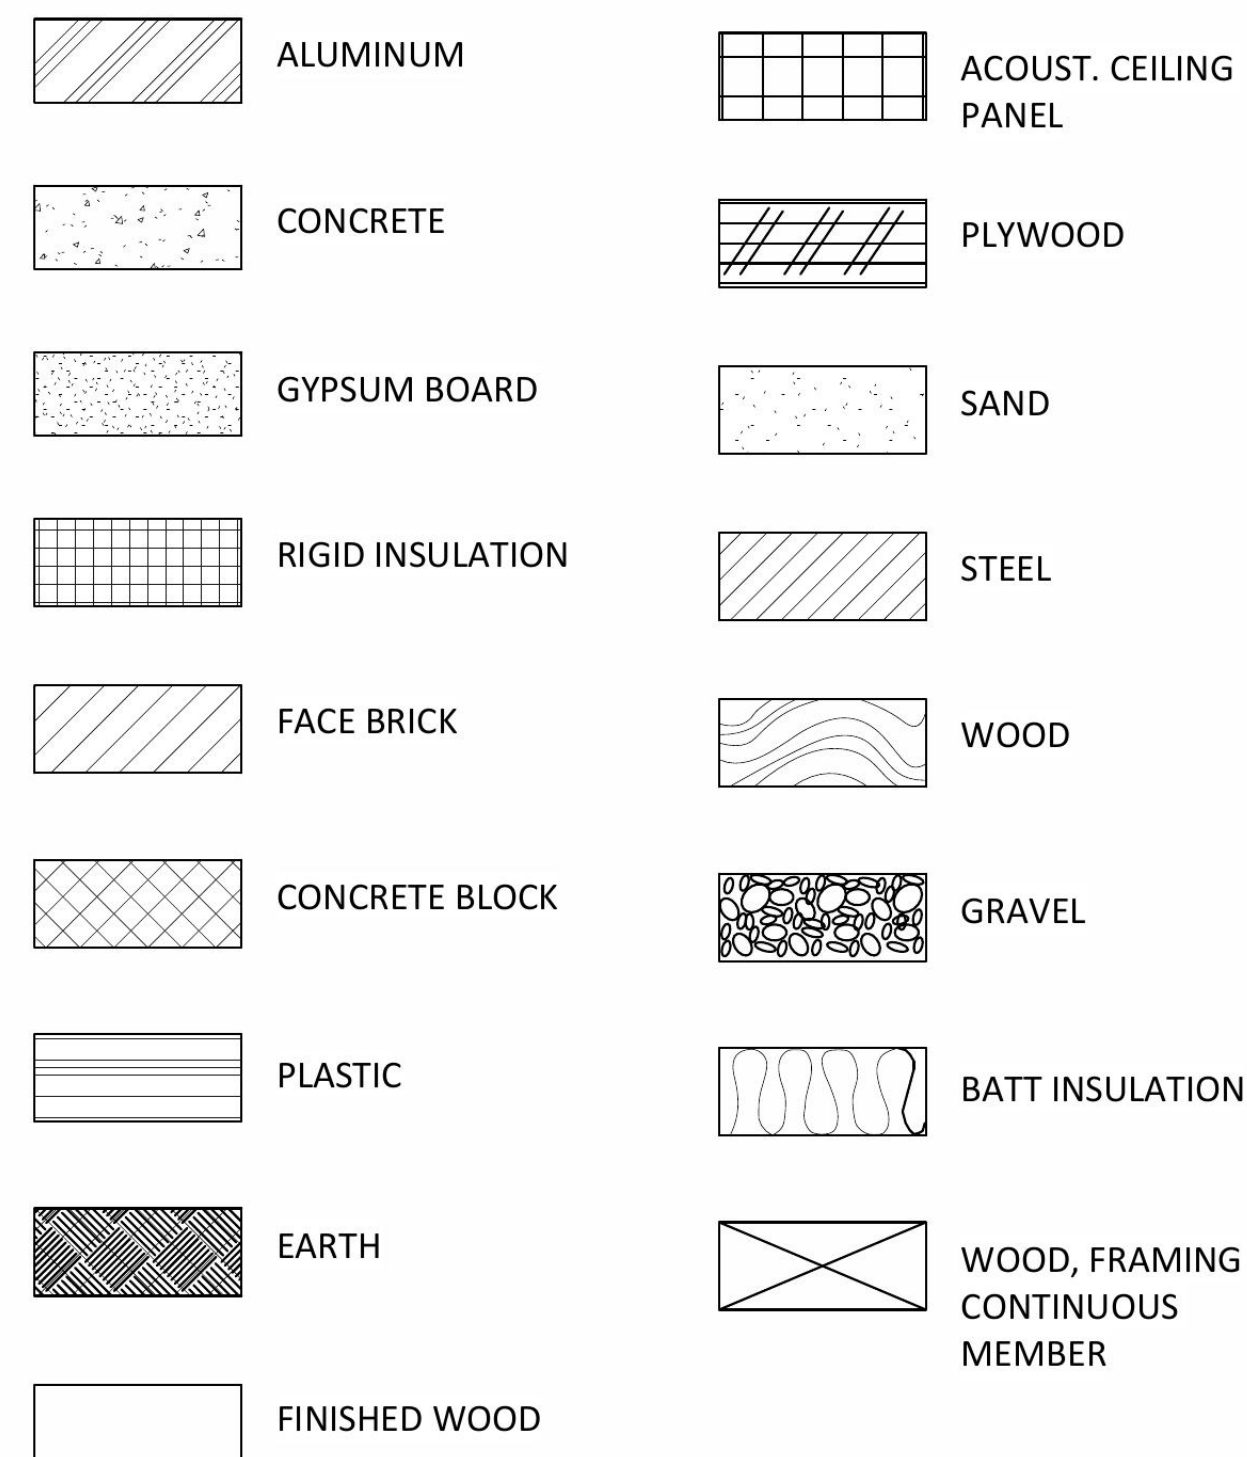

CODE SUMMARY

2020 INDIANA RESIDENTIAL CODE

DESIGN WIND SPEED	90
SEISMIC ZONE	B

LAND ZONING

D5

**TABLE R301.4 MINIMUM UNIFORMLY
DISTRIBUTED LIVE LOADS**

ATTICS - NONACCESSIBLE	0 PSF
BALCONIES - EXTERIOR	60 PSF
DECKS	60 PSF
GARAGES	50 PSF
ROOMS OTHER THAN SLEEPING ROOMS	40 PSF
SLEEPING ROOMS	30 PSF
GUARDS & HANDRAILS	200 SF
CONCENTRATED LOAD	
STAIRS	40 PSF
W/300 PSF CONCENTRATED LOAD	

EMERGENCY ESCAPE AND RESCUE OPENINGS

EVERY SLEEPING ROOM SHALL HAVE AT LEAST ONE
OPENABLE EMERGENCY ESCAPE AND RESCUE
OPENING

SMOKE ALARMS

REQUIRED SMOKE ALARM LOCATIONS:
LIVING AREA
ALL BEDROOMS OR SLEEPING AREAS
ON THE CEILING OF THE UPPER
LEVEL NEAR THE TOP OR ABOVE EACH STAIRWAY

BUILDING GROSS S.F.

1ST FLOOR	1,520 G.S.F
TOTAL	1,520 G.S.F

SHEET INDEX

<u>SD</u>	<u>DD</u>	<u>CD</u>	<u>REV</u>		
1 - General					
•				G-000	COVER SHEET
•				G-002	ARCHITECTURAL GENERAL NOTES AND ABBREVIATIONS
4 - Architectural					
				A-100	SITE/ROOF & FOUNDATION PLAN
				A-101	1ST FLOOR
				A-102	REFLECTED CEILING PLAN
				A-200	BUILDING ELEVATIONS
				A-300	BUILDING SECTIONS



BID SET

3 BED_2 BATH

3852 N AUDUBON RD, INDIANAPOLIS, IN 46226