


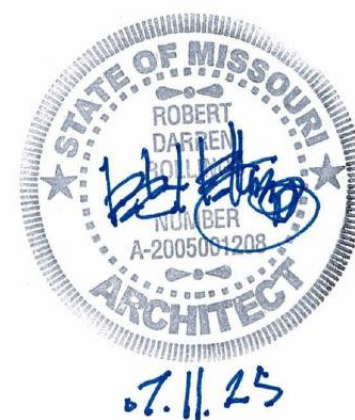

Robert D. Rollings 2005001208, Certificate of Authority # A-2006003870



Robert Rollings
Architects, LLC
208 S. Lowme
SEDALIA, MO 65201
PHONE: 660 829 9751
FAX: 660 829 9752



**J-SQUARED
ENGINEERING**
2400 BLUFF CREEK DR. STE. 101
COLUMBIA, MO 65201
573.234.4492 phone
www.j-squaredeng.com



Broadfoot Engineering, LLC
30277 Carpenter Road
Sedalia, MO 65301
Phone: 660-619-7001
broadfooteng@yahoo.com

**CROCKETT
ENGINEERING CONSULTANTS**
1000 W. Nifong Blvd., Bldg. 1,
Columbia, Missouri 65202
(573) 447-0292
www.crockettengineering.com
Crockett Engineering Consultants, LLC
Missouri Certificate of Authority
#2000151304

OFFICE OF ADMINISTRATION
DIVISION OF FACILITIES
MANAGEMENT DESIGN AND
CONSTRUCTION

DIRECTOR'S HOUSE

MISSOURI STATE
FAIRGROUNDS
2503 W. 16TH ST
SEDALIA, MO 65301

PROJECT # F2402-01

SITE # 1501


ASSET # 3511501149

DESIGN TEAM:

NOTE:	
THESE DRAWINGS, ALONG WITH THE PROJECT SPECIFICATIONS, REPRESENT A UNIFIED SET OF CONSTRUCTION DOCUMENTS. ALL BIDDERS SHALL BE RESPONSIBLE FOR FAMILIARIZING THEMSELVES WITH ALL DRAWINGS IN THIS SET, REGARDLESS OF SHEET NUMBER AND DISCIPLINE, AND SHALL BE RESPONSIBLE FOR COORDINATING THEIR WORK WITH THE WORK OF OTHER TRADES. ANY APPARENT DISCREPANCIES BETWEEN DRAWINGS OR BETWEEN THE DRAWINGS AND SPECIFICATIONS SHALL BE BROUGHT TO THE ATTENTION OF THE ARCHITECT PRIOR TO BIDDING.	
DO NOT BID FROM PARTIAL SETS OF BID DOCUMENTS.	
BY SUBMITTING A BID, BIDDERS REPRESENT THAT THEY HAVE VISITED THE SITE, BECOME FAMILIAR WITH THE BID DOCUMENTS IN THEIR ENTIRETY AND WITH LOCAL CONDITIONS UNDER WHICH THE WORKS IS TO BE PERFORMED AND HAVE CORRELATED THE BIDDER'S PERSONAL OBSERVATIONS WITH THE REQUIREMENTS OF THE CONTRACT DOCUMENTS.	



3	G-002	PROJECT LOCATION 1 1/2" = 1'-0"
---	-------	------------------------------------

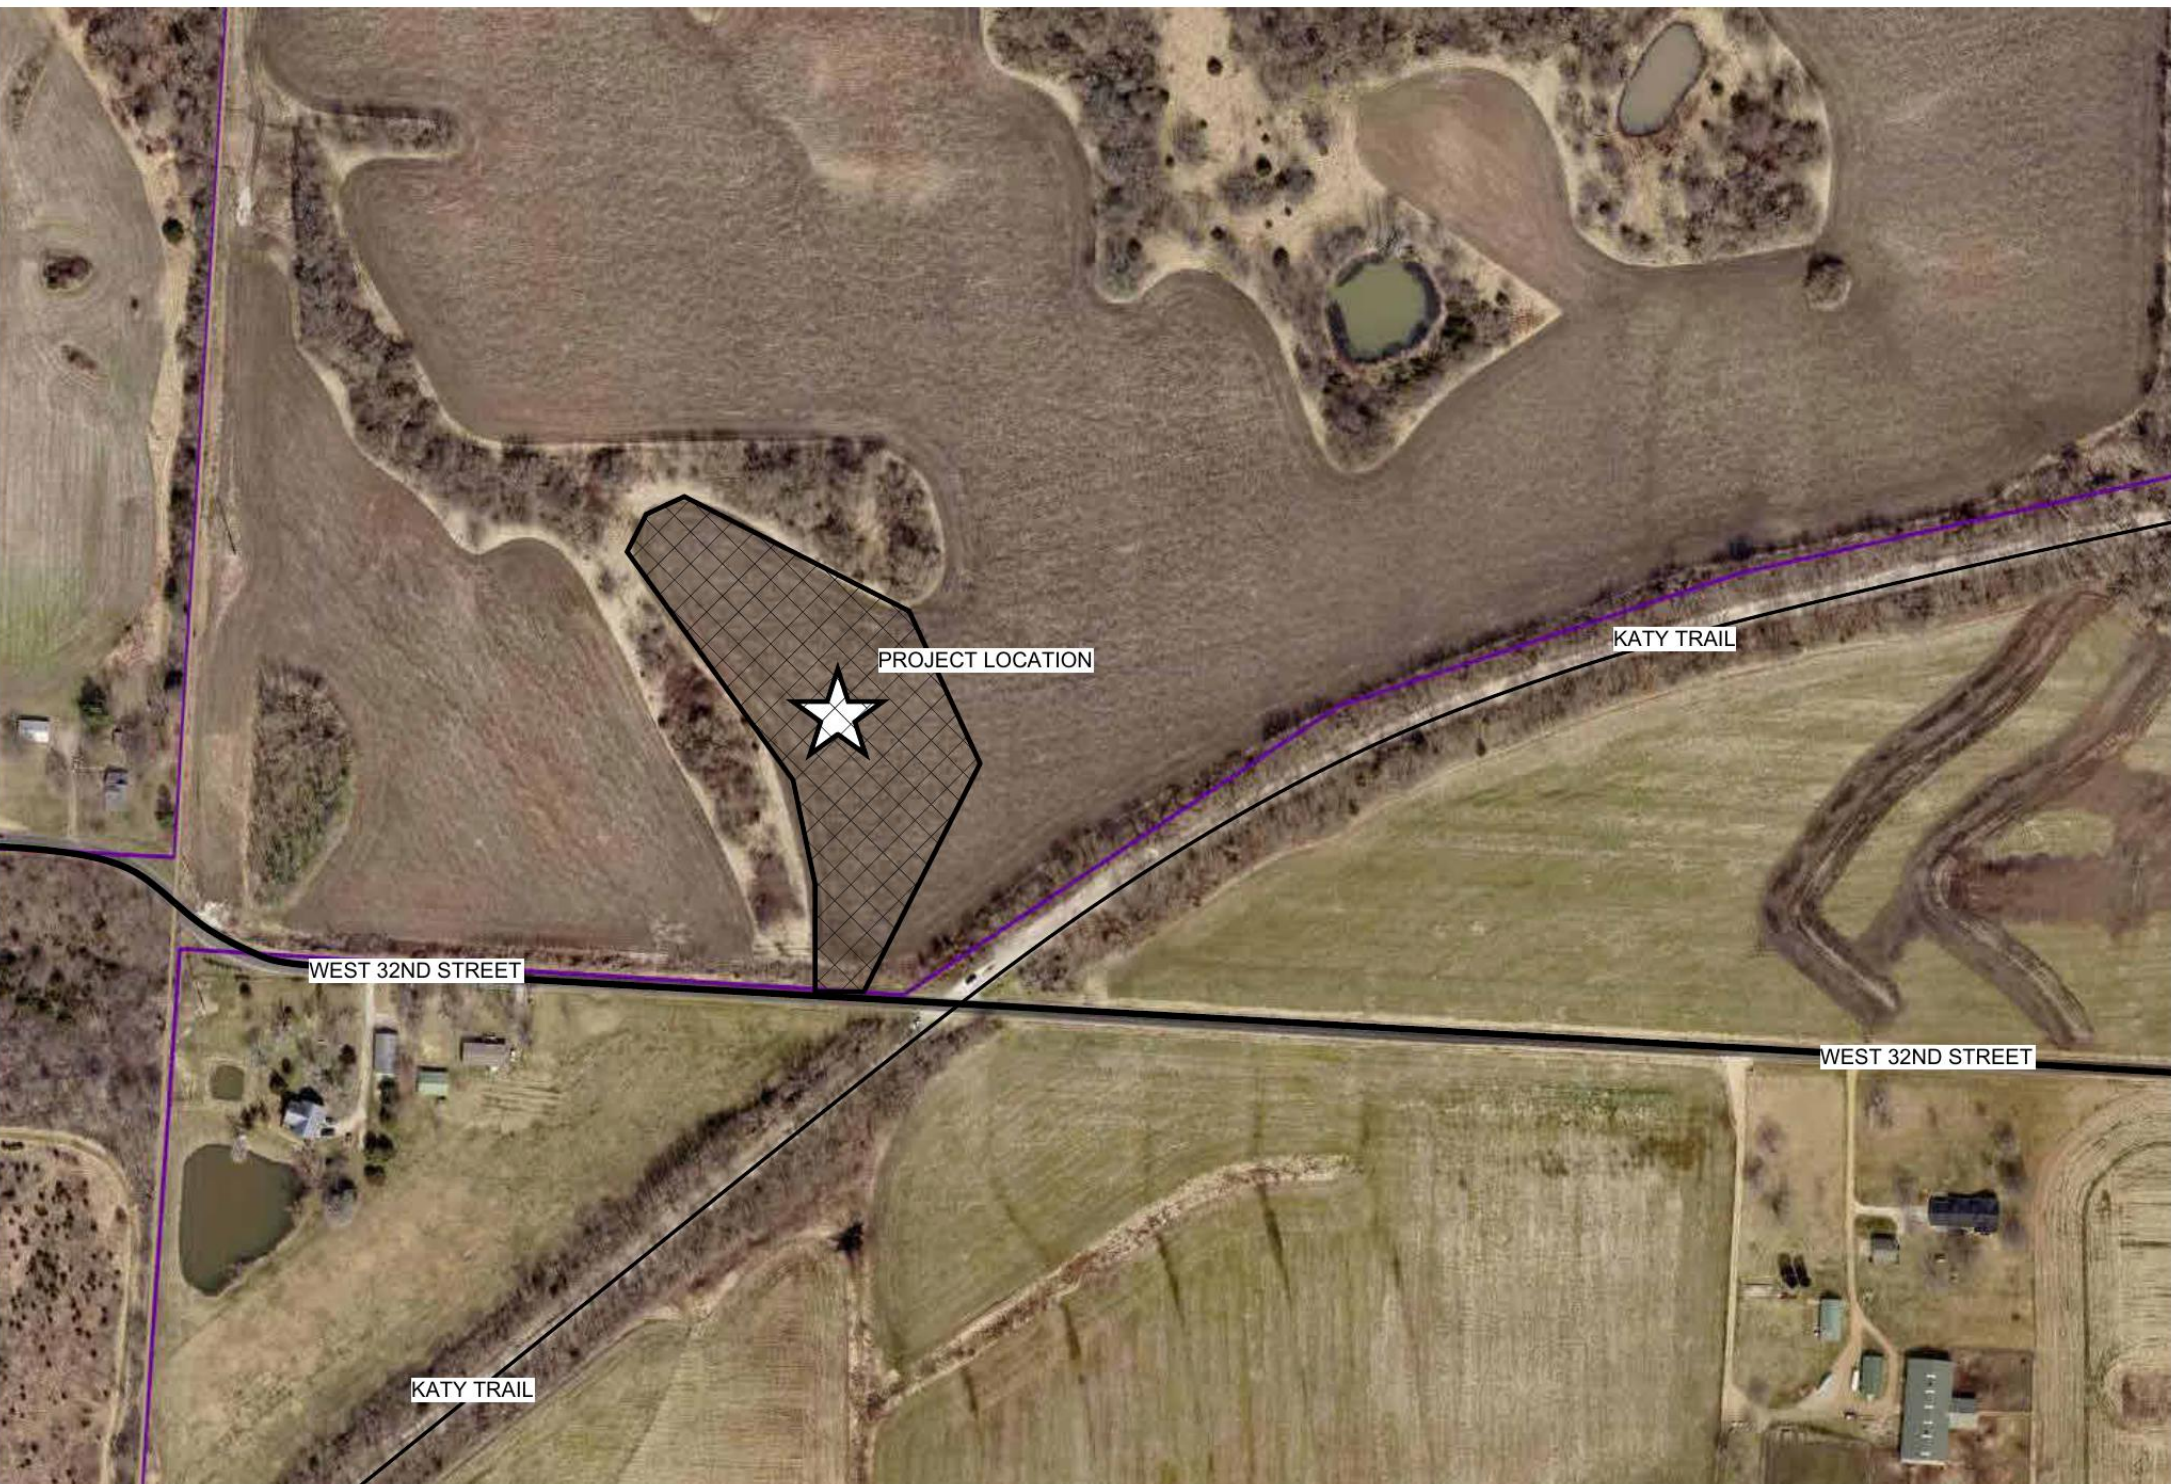

A-101	
DISCIPLINE	SHEET IN SERIES
G GENERAL	0 GENERAL INFORMATION
C CIVIL	1 PLANS
D DEMOLITION	2 EXTERIOR ELEVATIONS
S STRUCTURAL	3 BUILDING SECTIONS
A ARCHITECTURAL	4 LARGE SCALE VIEWS
Q EQUIPMENT	5 DETAILS
M MECHANICAL	6 SCHEDULES & DIAGRAMS
FG FUEL GAS	7 REFLECTED CEILING PLANS
P PLUMBING	8 STAIRS AND ELEVATORS
E ELECTRICAL	9 3D REPRESENTATIONS

4	SHEET NAMING CONVENTION
A1.01	SHEET NAMES DO NOT DEFINE LIMITS OF WORK

DRAWING NUMBER	4	SHEET NAME WHERE DRAWING IS FOUND
EXTERIOR ELEVATION	A2.01	101
INTERIOR ELEVATION	A3.01	B
BUILDING SECTION OR DETAIL SECTION	A3.01	G
DETAILED SECTION OR PLAN CALL-OUT	A4.01	6
FIRE EXTINGUISHER CABINET	F.E.C.	C.J.
		CONTROL JOINT

SHEET ORDER	SHEET NUMBER	SHEET NAME
1	G-001	COVER
2	G-002	GENERAL INFORMATION
3	C-001	CIVIL COVER SHEET
4	C-100	EXISTING CONDITIONS & DEMOLITION PLAN
5	C-101	OVERVIEW SITE LAYOUT PLAN
6	C-102	SITE LAYOUT & UTILITY PLAN
7	C-103	GRADING & DRAINAGE PLAN
8	C-501	DETAILS
9	C-502	DETAILS
10	S-100	STRUCTURAL COVER SHEET
11	S-101	FOUNDATION PLAN & DETAILS
12	S-102	FOUNDATION PLAN DETAILS
13	S-103	FRAMING PLAN & DETAILS
14	S-104	FRAMING PLAN DETAILS
15	A-101	FLOOR PLANS
16	A-102	DIMENSION PLANS
17	A-103	REFERENCE PLANS
18	A-104	ROOF PLAN & REFLECTED CEILING PLAN
19	A-201	EXTERIOR ELEVATIONS
20	A-301	BUILDING SECTIONS
21	A-401	WALL SECTIONS
22	A-402	WALL SECTIONS
23	A-403	INTERIOR ELEVATIONS
24	A-404	INTERIOR ELEVATIONS
25	A-501	TYPICAL DETAILS
26	A-601	DOOR - WINDOW & FINISH SCHEDULE
27	MEP1	MECHANICAL-ELECTRICAL-PLUMBING COVER SHEET
28	MEP2	SITE PLAN
29	M-101	HVAC PLAN
30	M-501	HVAC DETAILS & SCHEDULES
31	EP-101	POWER PLAN
32	EL-101	LIGHTING PLAN
33	E-501	ELECTRICAL DETAILS & SCHEDULES
34	PS-101	SANITARY SEWER PLAN
35	PW-101	WATER & GAS PLAN
36	P-501	PLUMBING DETAILS & SCHEDULES

DESIGN TEAM:

ARCHITECT:
ROBERT ROLLINGS ARCHITECTS, LLC
1806 WEST BROADWAY
SEDALIA, MO 65301
660.829.9751 FAX: 660.829.9752

MECHANICAL / ELECTRICAL ENGINEER:
J-SQUARED ENGINEERING
2400 BLUFF CREEK DR. SUITE 101
COLUMBIA, MO 65203
573.234.4492

STRUCTURAL ENGINEER:
CROCKETT ENGINEERING
1000 W. NIFONG BLVD. BLDG. 1
COLUMBIA, MO 65202
573.447.0292

CIVIL ENGINEER:
BROADFOOT ENGINEERING, LLC
30277 CARPENTER ROAD
SEDALIA, MO 65301
660.619.7001