


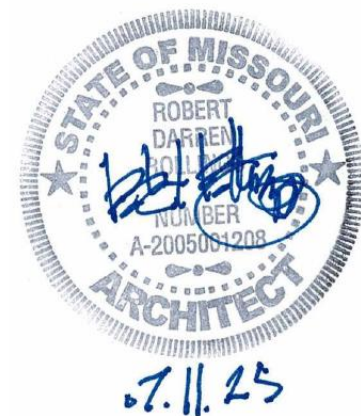

Robert D. Rollings 2005001208, Certificate of Authority # A-2006003870



Robert Rollings
Architects, LLC
208 S. Lowme
SEDALIA, MO 65201
PHONE: 660 829 9751
FAX: 660 829 9752



**J-SQUARED
ENGINEERING**

2400 BLUFF CREEK DR. STE. 101
COLUMBIA, MO 65201
573.234.4492 phone
www.j-squaredeng.com



Broadfoot Engineering, LLC

30277 Carpenter Road
Sedalia, MO 65301
Phone: 660-619-7001
broadfooteng@yahoo.com

**CROCKETT
ENGINEERING CONSULTANTS**

1000 W. Nifong Blvd., Bldg. 1,
Columbia, Missouri 65202
(573) 447-0292
www.crockettengineering.com
Crockett Engineering Consultants, LLC
Missouri Certificate of Authority
#2000151304

OFFICE OF ADMINISTRATION
DIVISION OF FACILITIES
MANAGEMENT DESIGN AND
CONSTRUCTION

DIRECTOR'S HOUSE

MISSOURI STATE
FAIRGROUNDS
2503 W. 16TH ST
SEDALIA, MO 65301

PROJECT # F2402-01


SITE # 1501


ASSET # 3511501149

DESIGN TEAM:

NOTE:
THESE DRAWINGS, ALONG WITH THE PROJECT SPECIFICATIONS, REPRESENT A UNIFIED SET OF CONSTRUCTION DOCUMENTS. ALL BIDDERS SHALL BE RESPONSIBLE FOR FAMILIARIZING THEMSELVES WITH ALL DRAWINGS IN THIS SET, REGARDLESS OF SHEET NUMBER AND DISCIPLINE, AND SHALL BE RESPONSIBLE FOR COORDINATING THEIR WORK WITH THE WORK OF OTHER TRADES. ANY APPARENT DISCREPANCIES BETWEEN DRAWINGS OR BETWEEN THE DRAWINGS AND SPECIFICATIONS SHALL BE BROUGHT TO THE ATTENTION OF THE ARCHITECT PRIOR TO BIDDING.
DO NOT BID FROM PARTIAL SETS OF BID DOCUMENTS.
BY SUBMITTING A BID, BIDDERS REPRESENT THAT THEY HAVE VISITED THE SITE, BECOME FAMILIAR WITH THE BID DOCUMENTS IN THEIR ENTIRETY AND WITH LOCAL CONDITIONS UNDER WHICH THE WORKS IS TO BE PERFORMED AND HAVE CORRELATED THE BIDDER'S PERSONAL OBSERVATIONS WITH THE REQUIREMENTS OF THE CONTRACT DOCUMENTS.

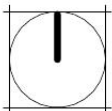



	3	PROJECT LOCATION
G-002	1 1/2" = 1'-0"	

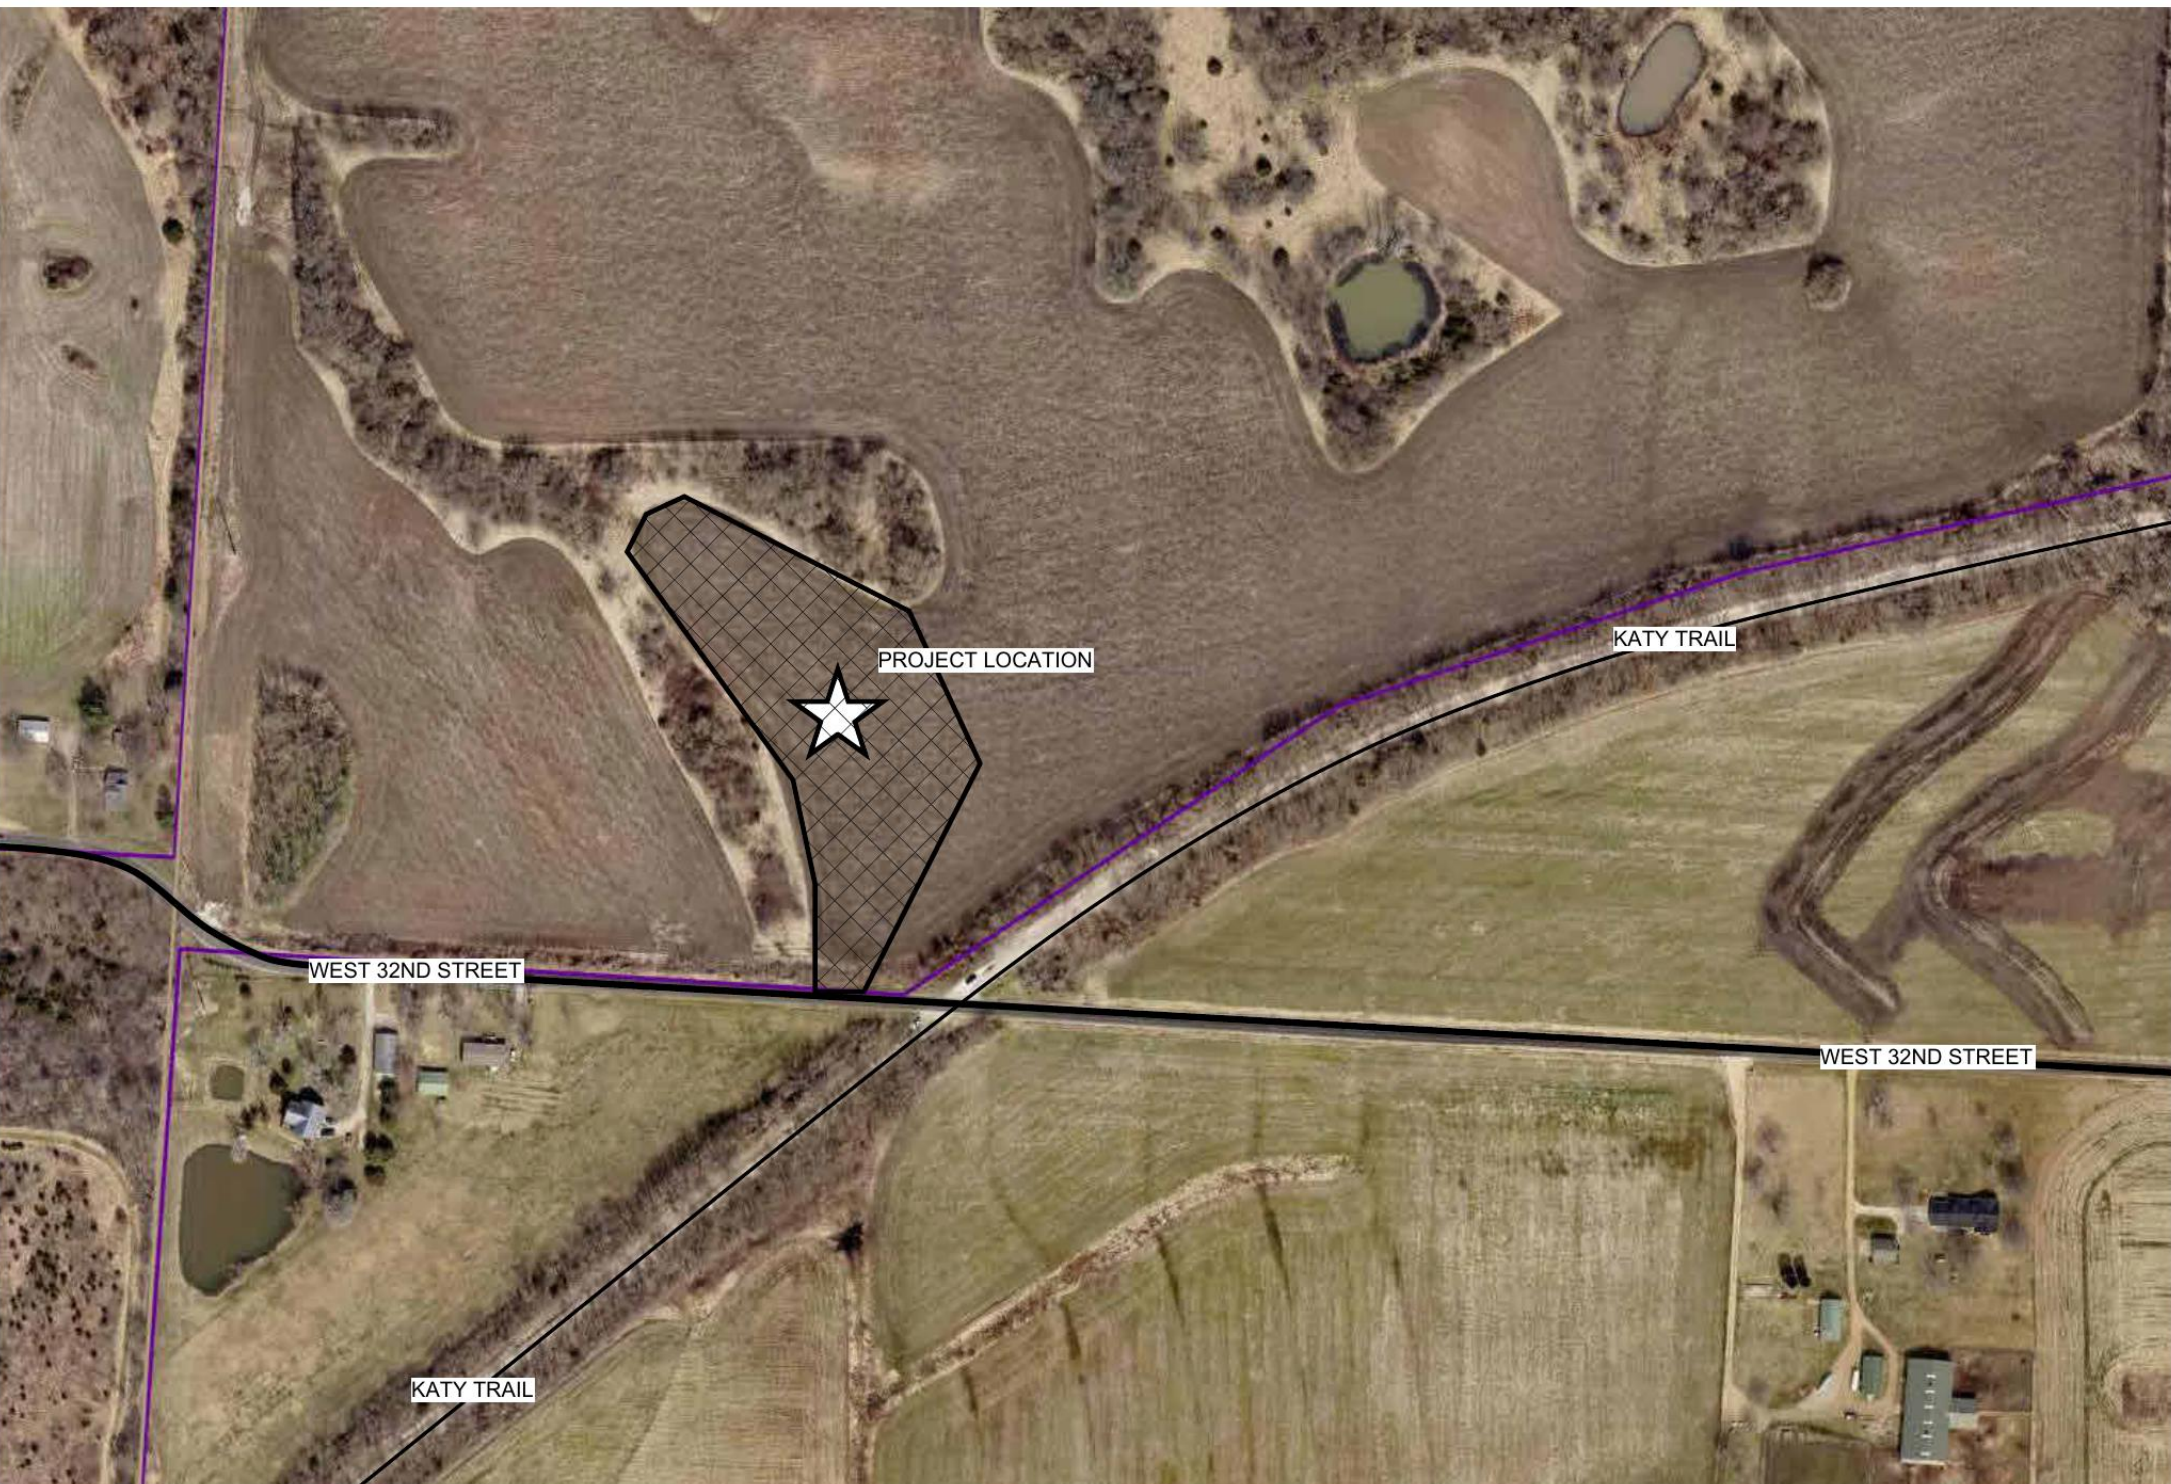

A-101

DISCIPLINE	SHEET IN SERIES
G GENERAL	0 GENERAL INFORMATION
C CIVIL	1 PLANS
D DEMOLITION	2 EXTERIOR ELEVATIONS
S STRUCTURAL	3 BUILDING SECTIONS
A ARCHITECTURAL	4 LARGE SCALE VIEWS
Q EQUIPMENT	5 DETAILS
M MECHANICAL	6 SCHEDULES & DIAGRAMS
FG FUEL GAS	7 REFLECTED CEILING PLANS
P PLUMBING	8 STAIRS AND ELEVATORS
E ELECTRICAL	9 3D REPRESENTATIONS

4	SHEET NAMING CONVENTION
A1.01	SHEET NAMES DO NOT DEFINE LIMITS OF WORK

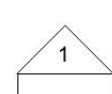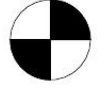DRAWING NUMBER	4	SHEET NAME WHERE DRAWING IS FOUND
	A1.01	
EXTERIOR ELEVATION		OFFICE T01
	A2.01	ROOM/SPACE NAME AND REF. NUMBER
	101	DOOR NUMBER
INTERIOR ELEVATION		B
	A3.01	WINDOW TYPE
BUILDING SECTION OR DETAIL SECTION		G
	A3.01	KEYED NOTE
	6	EQUIPMENT NUMBER
		SPOT ELEVATION OR FLOOR ELEVATION
DETAILED SECTION OR PLAN CALL-OUT		PLAN NORTH
	A4.01	
FIRE EXTINGUISHER CABINET	F.E.C.	C.J.
		CONTROL JOINT

DESIGN TEAM:

ARCHITECT:
ROBERT ROLLINGS ARCHITECTS, LLC
1806 WEST BROADWAY
SEDALIA, MO 65301
660.829.9751 FAX: 660.829.9752
MECHANICAL / ELECTRICAL ENGINEER:
J-SQUARED ENGINEERING
2400 BLUFF CREEK DR. SUITE 101
COLUMBIA, MO 65203
573.234.4492
STRUCTURAL ENGINEER:
CROCKETT ENGINEERING
1000 W. NIFONG BLVD. BLDG. 1
COLUMBIA, MO 65202
573.447.0292
CIVIL ENGINEER:
BROADFOOT ENGINEERING, LLC
30277 CARPENTER ROAD
SEDALIA, MO 65301
660.619.7001