


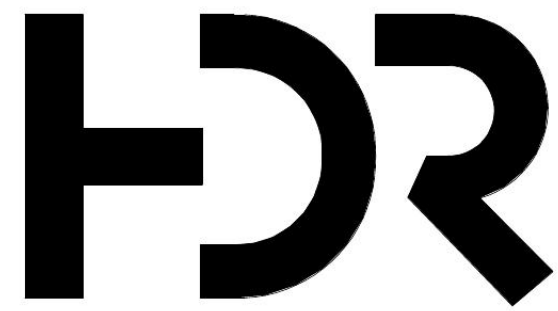

HDR Architecture
1917 S 67th Street
Omaha, NE 68106

Project Number | 10373227


Construction Documents 11/13/2023

Elkhorn Storage Building No.1

OPPD Elkhorn Center
1101 N 180th St
Omaha, NE 68022

OPPD

Elkhorn Service Center
1101 N 180th St
Omaha, NE 68022

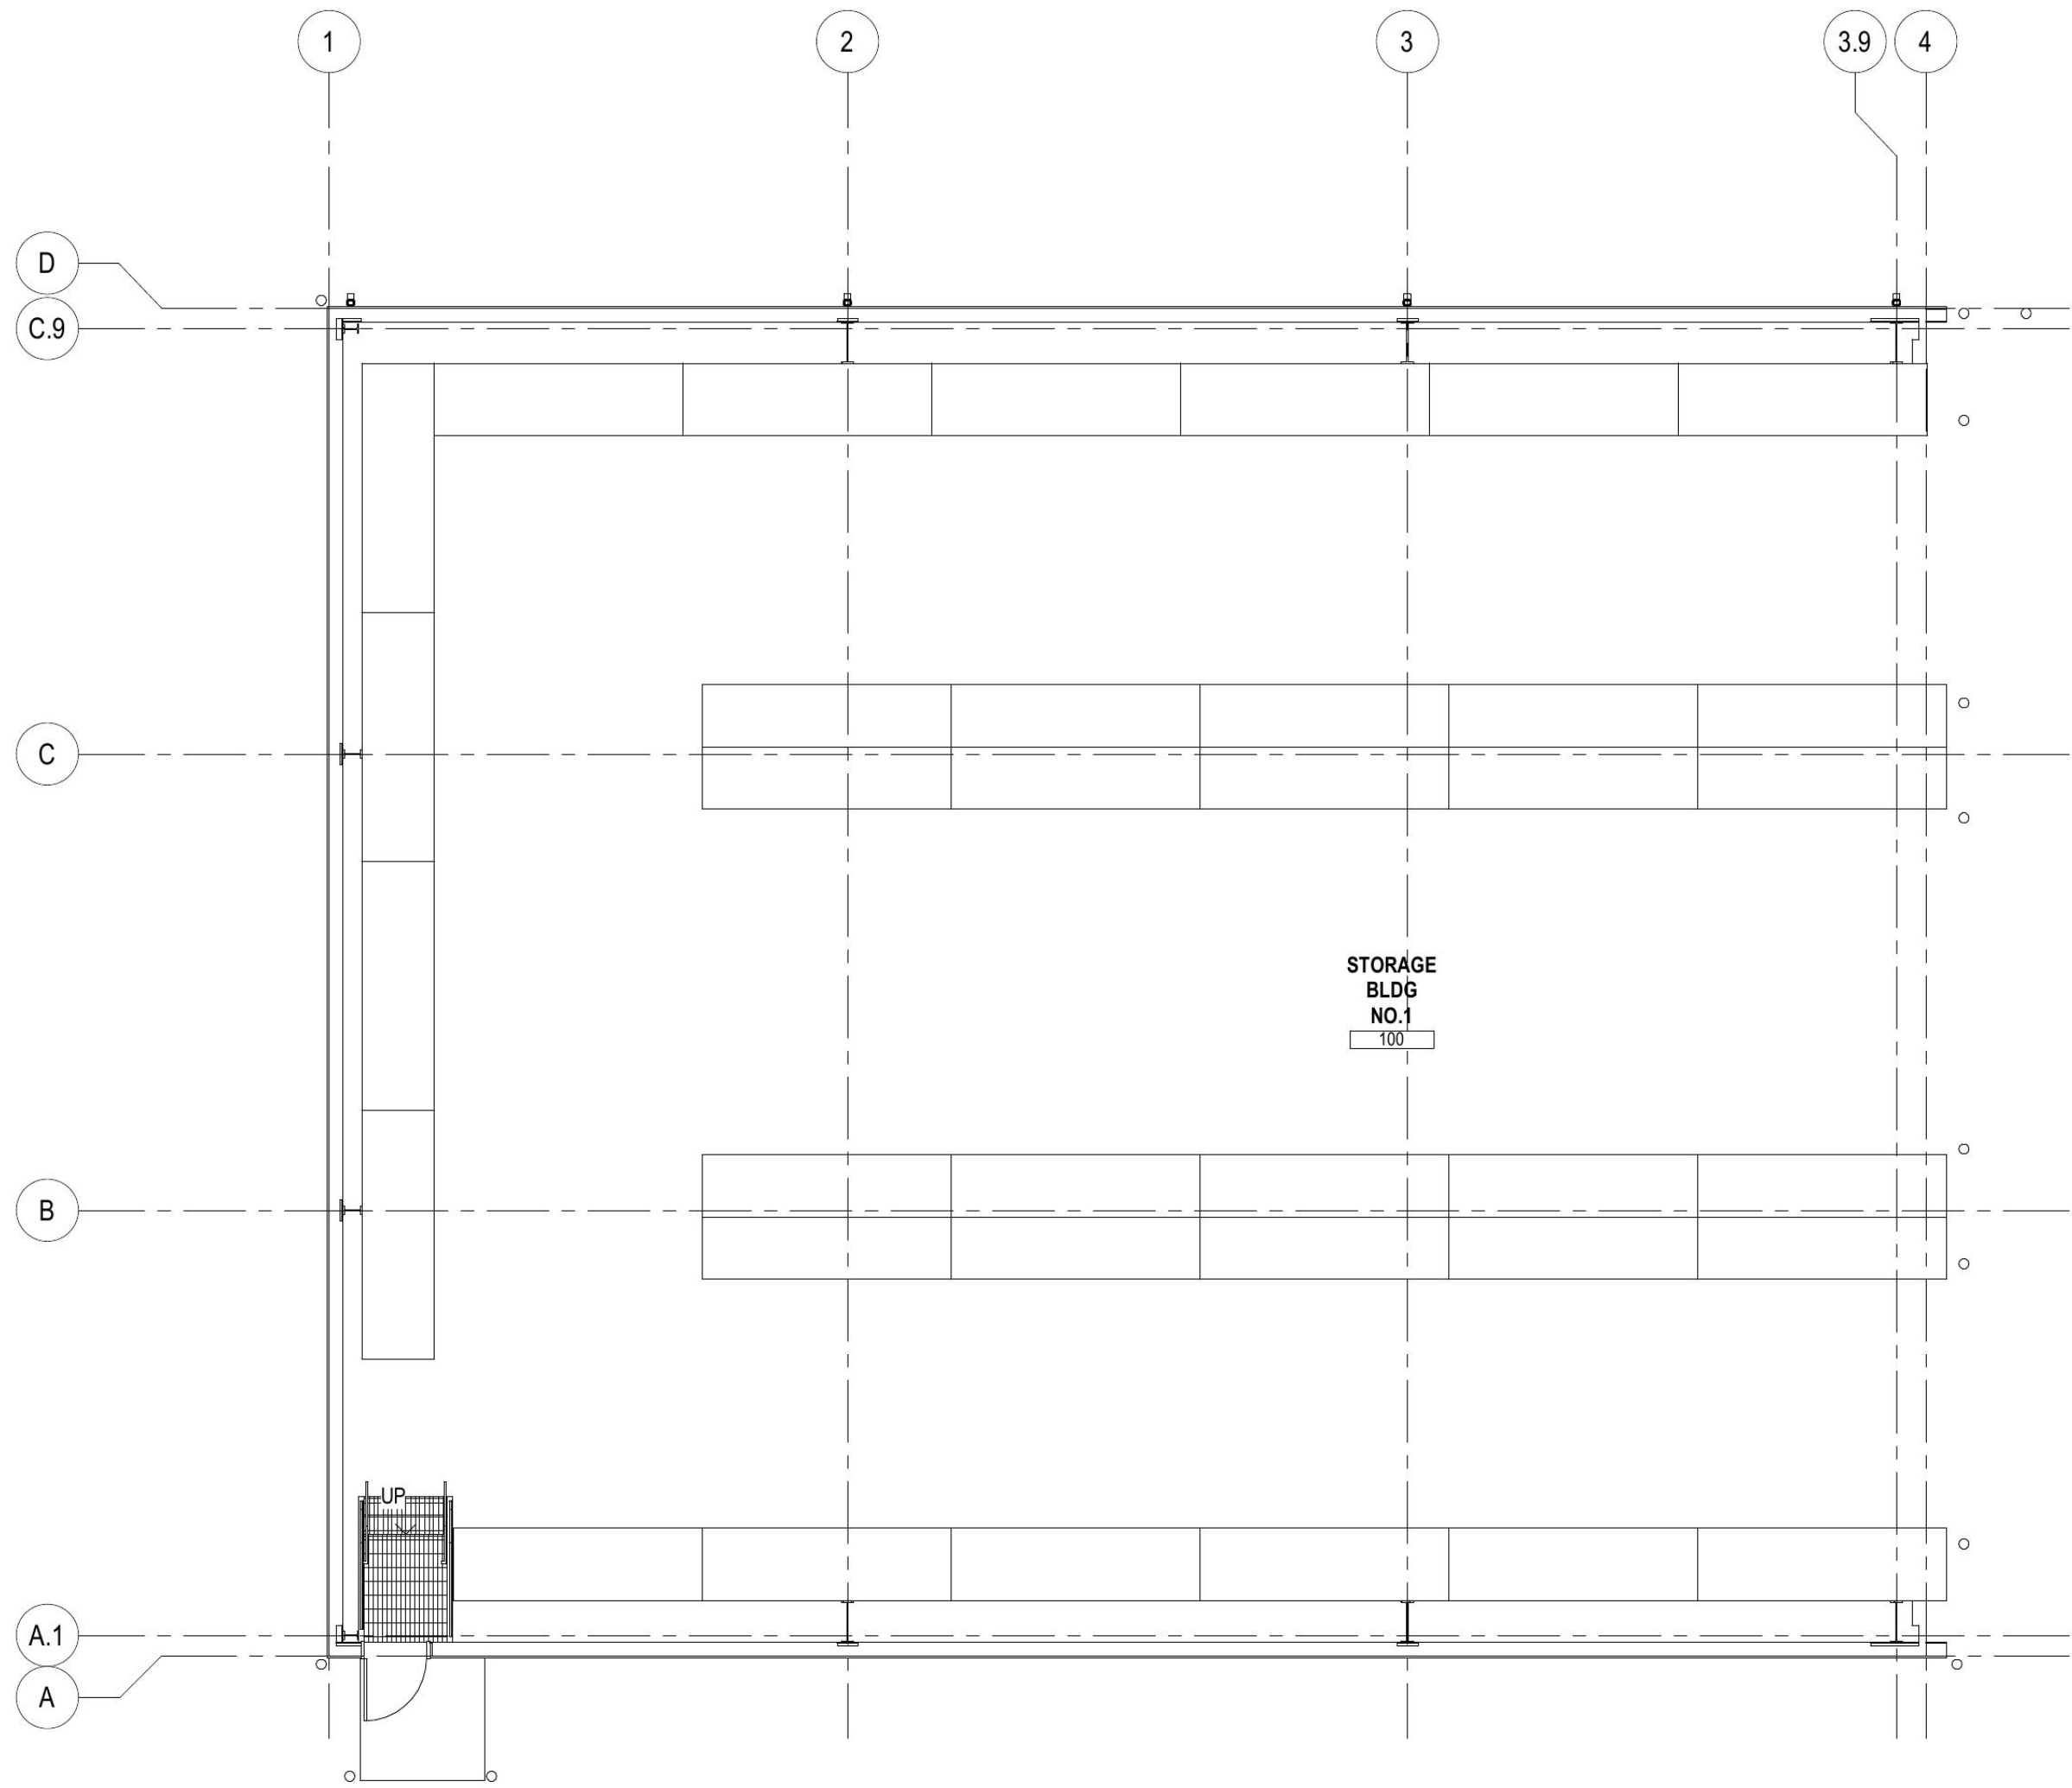

1 LIFE SAFETY PLAN

1/8" = 1'-0"

BUILDING OCCUPANT LOAD


A	B	C	D	E	E	F	G	H	I		
Floor Level	Total Floor Area	Occupancy Classification and Use Designation (IBC 302.1)				Area Square Footage	Occupant Loads (IBC 1004)				
							Function of Space (IBC Table 1004.5)	Occupant Load Factor (IBC Table 1004.5)	Occupant Load Factor (Actual and Hidden)	Occupant Load Factor (Override)	Occupant Load
		Use Designation	Occupancy Classification	Use Type (Hide Column Not Used)	Use Type (Manual) (Hide Column Not Used)						
	Measure	Select			Input	Input	Input	Selected	Input	(F/H)	
		Group S-2	Storage		Storage	5,088	Accessory storage areas, mechanical equipment room	300 gross	300	17	
Totals	5,088	Total Floor Area = Area Square Footages > 0				5,088				17	

NOTE: BUILDING IS NORMALLY UNOCCUPIED. RESTROOMS ARE NOT REQUIRED TO BE PROVIDED, PER IBC 2902.3.3 AND OMAHA PLUMBING CODE (CH 49). EMPLOYEE RESTROOMS ARE PROVIDED IN NEARBY, REGULARLY OCCUPIED MAIN ELKHORN CENTER BUILDING.

LIFE SAFETY LEGEND

Area Name	NAME OF AREA/SPACE
Business	FUNCTION OF SPACE (IBC TABLE 1004.5)
15,000 SF	SQUARE FOOTAGE OF AREA/SPACE
Load Factor 150	LOAD FACTOR (IBC TABLE 1004.1.2)
Calc Occ: 100	CALCULATED OCCUPANT LOAD PER AREA/SPACE (IBC 1004)
DOOR	EGRESS COMPONENT - OCCUPANT LOAD AND WIDTH (IN INCHES)
Clear Width: 33"	ACTUAL CLEAR WIDTH PROVIDED
Max Occ: 165	MAXIMUM ALLOWED OCCUPANT LOAD PER EXIT (IBC 1005.3)
Req Width: 28"	REQUIRED MINIMUM WIDTH PER OCCUPANCY (IBC 1005.3)
Calc Occ: 140	CALCULATED OCCUPANT LOAD PER EXIT (IBC 1004)
STAIR	EGRESS STAIR - OCCUPANT LOAD AND WIDTH (IN INCHES)
Clear Width: 44"	ACTUAL CLEAR WIDTH PROVIDED
Max Occ: 146	MAXIMUM ALLOWED OCCUPANT LOAD PER STAIR (IBC 1005.3)
Req Width: 28"	REQUIRED MINIMUM WIDTH PER OCCUPANCY (IBC 1005.3)
Calc Occ: 93	CALCULATED OCCUPANT LOAD PER STAIR (IBC 1004)
185'-6"	TRAVEL DISTANCE: LONGEST ROUTE TO AN EXIT (MAXIMUM PER SPACE/AREA SHOWN) (IBC 1017.2)
55'-6"	COMMON PATH: DISTANCE TRAVELED BEFORE AN EXIT PATH IS CHOSEN (MAXIMUM PER SPACE/ AREA SHOWN) (IBC 1006.2)

ELKHORN CENTER SITE PLAN

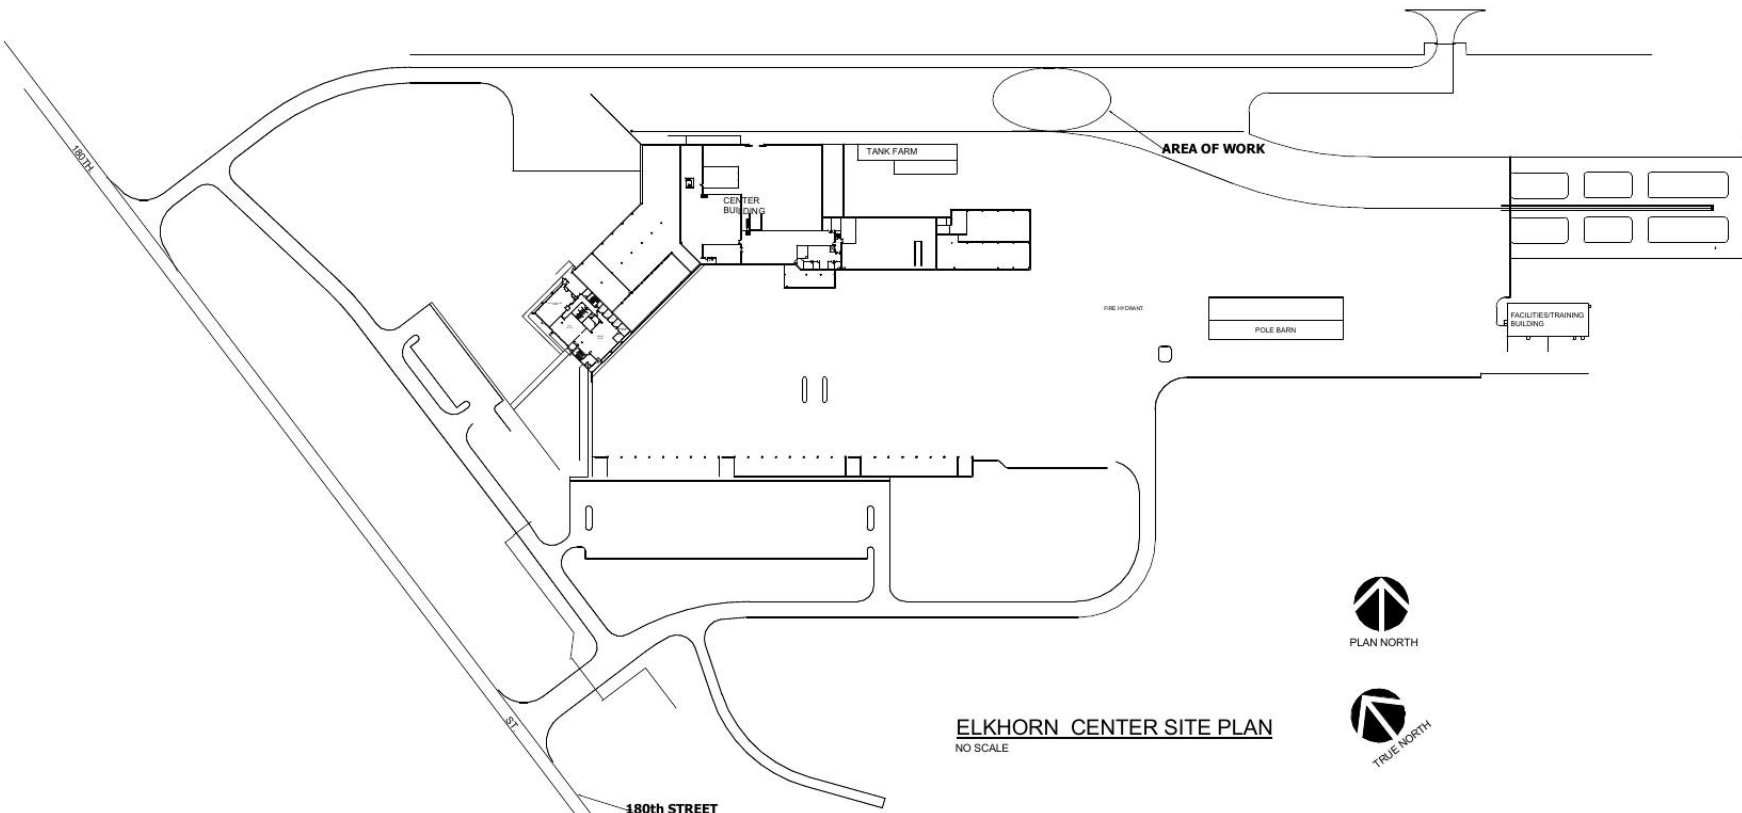

BUILDING INFORMATION

- ADDRESS: 1101 N 180th Street...
- ZONING DISTRICT: G1
- OCCUPANCY: Group S-1: Low Hazard Storage
- CONSTRUCTION TYPE: Type 2B - NonCombustible (Table 601)
- SPRINKLERED: Not Sprinklered
- BUILDING HEIGHT: 32'-0" Top of Steel Level 01 Elevation
- BUILDING AREAS: Allowable... 20'-6" (19.5' SLR - Base Flood Elevation)
Total Building Area (Occupied) 5,088 GSF
- Building Areas by Level: Level 01: 5,088 GSF
- PARKING: Not Applicable; Parking existing.

APPLICABLE BUILDING CODES

THIS PROJECT HAS BEEN DESIGNED UNDER THE REQUIREMENTS OF THE APPLICABLE CODES BELOW

- BUILDING: 2018 INTERNATIONAL BUILDING CODE, NFPA 101
- OTHER: NFPA 10
- ENERGY: 2018 INTERNATIONAL ENERGY CONSERVATION CODE
- MECHANICAL: 2012 INTERNATIONAL MECHANICAL CODE
- PLUMBING: 2018 OMAHA PLUMBING CODE
- ELECTRICAL: 2017 NFPA 70 (NATIONAL ELECTRICAL CODE)
- FIRE: 2012 INTERNATIONAL FIRE CODE WITH AMENDMENTS, 2012 NFPA 1 PREVENTION
- ACCESSIBILITY: 2010 ADA SAD & 2009 ICC A117.1

APPLICABLE EGRESS REQUIREMENTS

BASED ON: Type 2B - NonCombustible (Table 601) - Group S-1 - Not Sprinklered

- MAXIMUM ALLOWABLE TRAVEL DISTANCE: 300 FEET
Per IBC Table 1017.1
- COMMON PATH OF EGRESS TRAVEL: 100 FEET
Per IBC Table 1006.2.1
- MAXIMUM ALLOWABLE DEAD-END DISTANCE: 20 FEET
Per IBC 1020.4
- ALLOWABLE EGRESS COMPONENT CAPACITY: 165 @ 33 INCH DOOR
Per IBC 1005.3.1 0.2 Inches/Occupant 330 @ 66 INCH DOOR
- ALLOWABLE EGRESS STAIR CAPACITY: 146 @ 44 INCH STAIR
Per IBC 1005.3.2 0.3 Inches/Occupant

GENERAL LIFE SAFETY NOTES

- Structure is to be utilized for yard storage and will be typically unoccupied.
-
-
-
-
-