


COMPLY WITH REQUIREMENTS OF THE LOCAL GOVERNING AUTHORITY FOR ENTRANCE APRON FROM STREET. PROVIDE SMOOTH TRANSITION BETWEEN NEW PAVEMENT AND EXISTING.

DO NOT BIND OR EXTRACT SETS OF BINDING DOCUMENTS

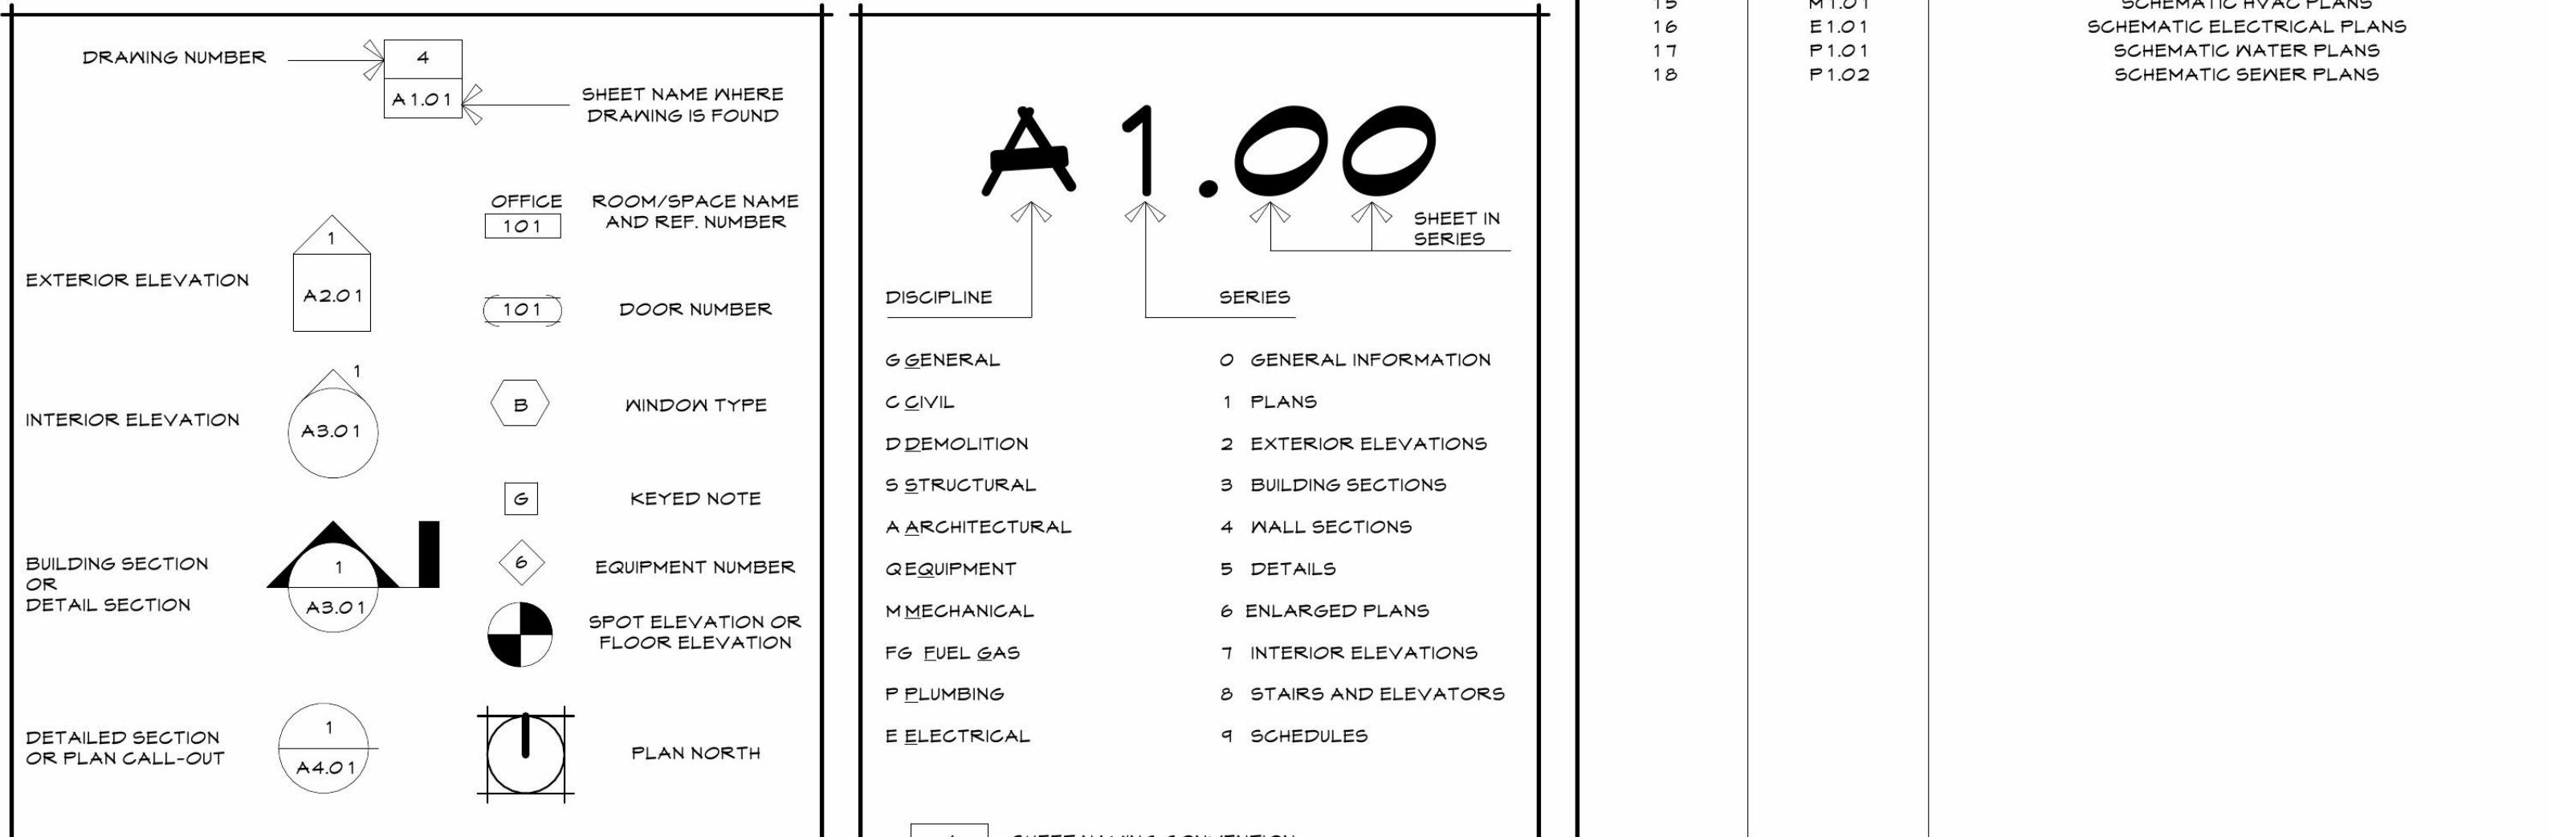

ROBERT D. ROLLINGS 2008001208
 CERTIFICATE OF AUTHORITY
 TO OFFER ARCHITECTURAL
 SERVICES,
 ROBERT ROLLINGS ARCHITECTS, LLC
 SERIAL # A-200800850-D

ISSUE/REVISION	DATE	NO.
CONSTRUCTION SET	2/9/2023	