

HOUSING ASSISTANCE PROGRAM - WOODBURRY RESIDENCE

STRUCTURAL ENGINEER



Service Beyond Design

ARCHITECTURE + ENGINEERING

License No. AR102538 License No. CA30900

DESIGN CRITERIA


FLORIDA BUILDING CODE-
RESIDENTIAL
8TH EDITION (2023)


TO THE BEST OF THI DESIGN PORFESSIONAL'S KNOWLEDGE, THESE PLANS AND SPECIFICATIONS COMPLY WITH THE APPLICABLE MINIMUM BUILDING CODES AND THE APlicable FIRE SAFETY STANDARDS AS DETERMINED BY THE LOCAL AUTHORITY IN ACCORDANCE WITH CHAPTER 553 AND 633 OF THE FLORIDA STATUTES AND MEET OR EXCEED THE REQUIREMENTS OF THE FLORIDA BUILDING CODE-RESIDENTIAL 8TH EDITION (2023), AS DEVELOPED AND MAINTANIED BY THE FLORIDA BUILDING COMMISSION, AND ADMINISTERED AND ENFOCED BY LOCAL JURISDICTIONS.

LOT INFORMATION

COMMUNITY:
LOT: PARCEL ID: 2571-013-003
ADDRESS: 826 NW 6TH AVE., FL 34475
COUNTY: OCALA
WIND SPEED: 130
EXPOSURE: C

SITE MAP

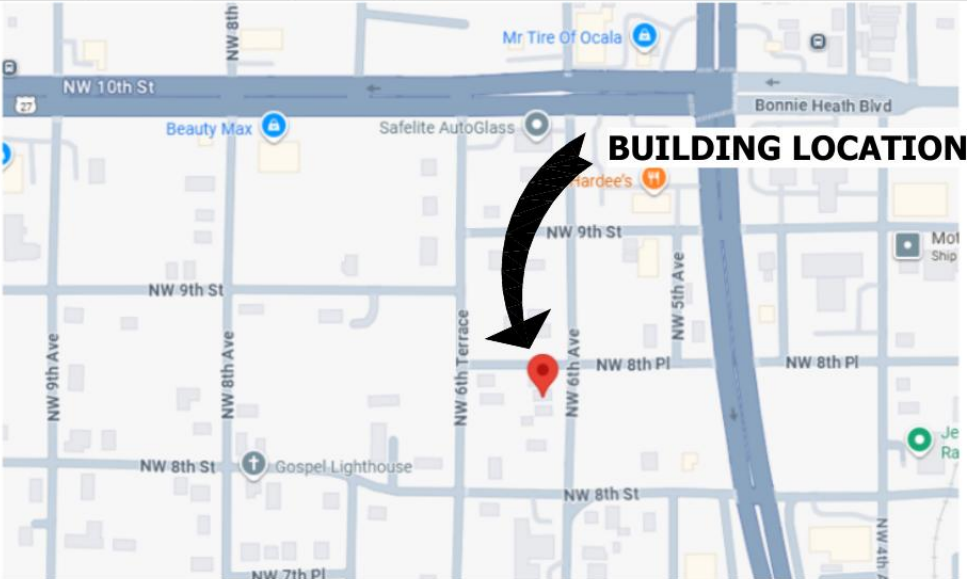

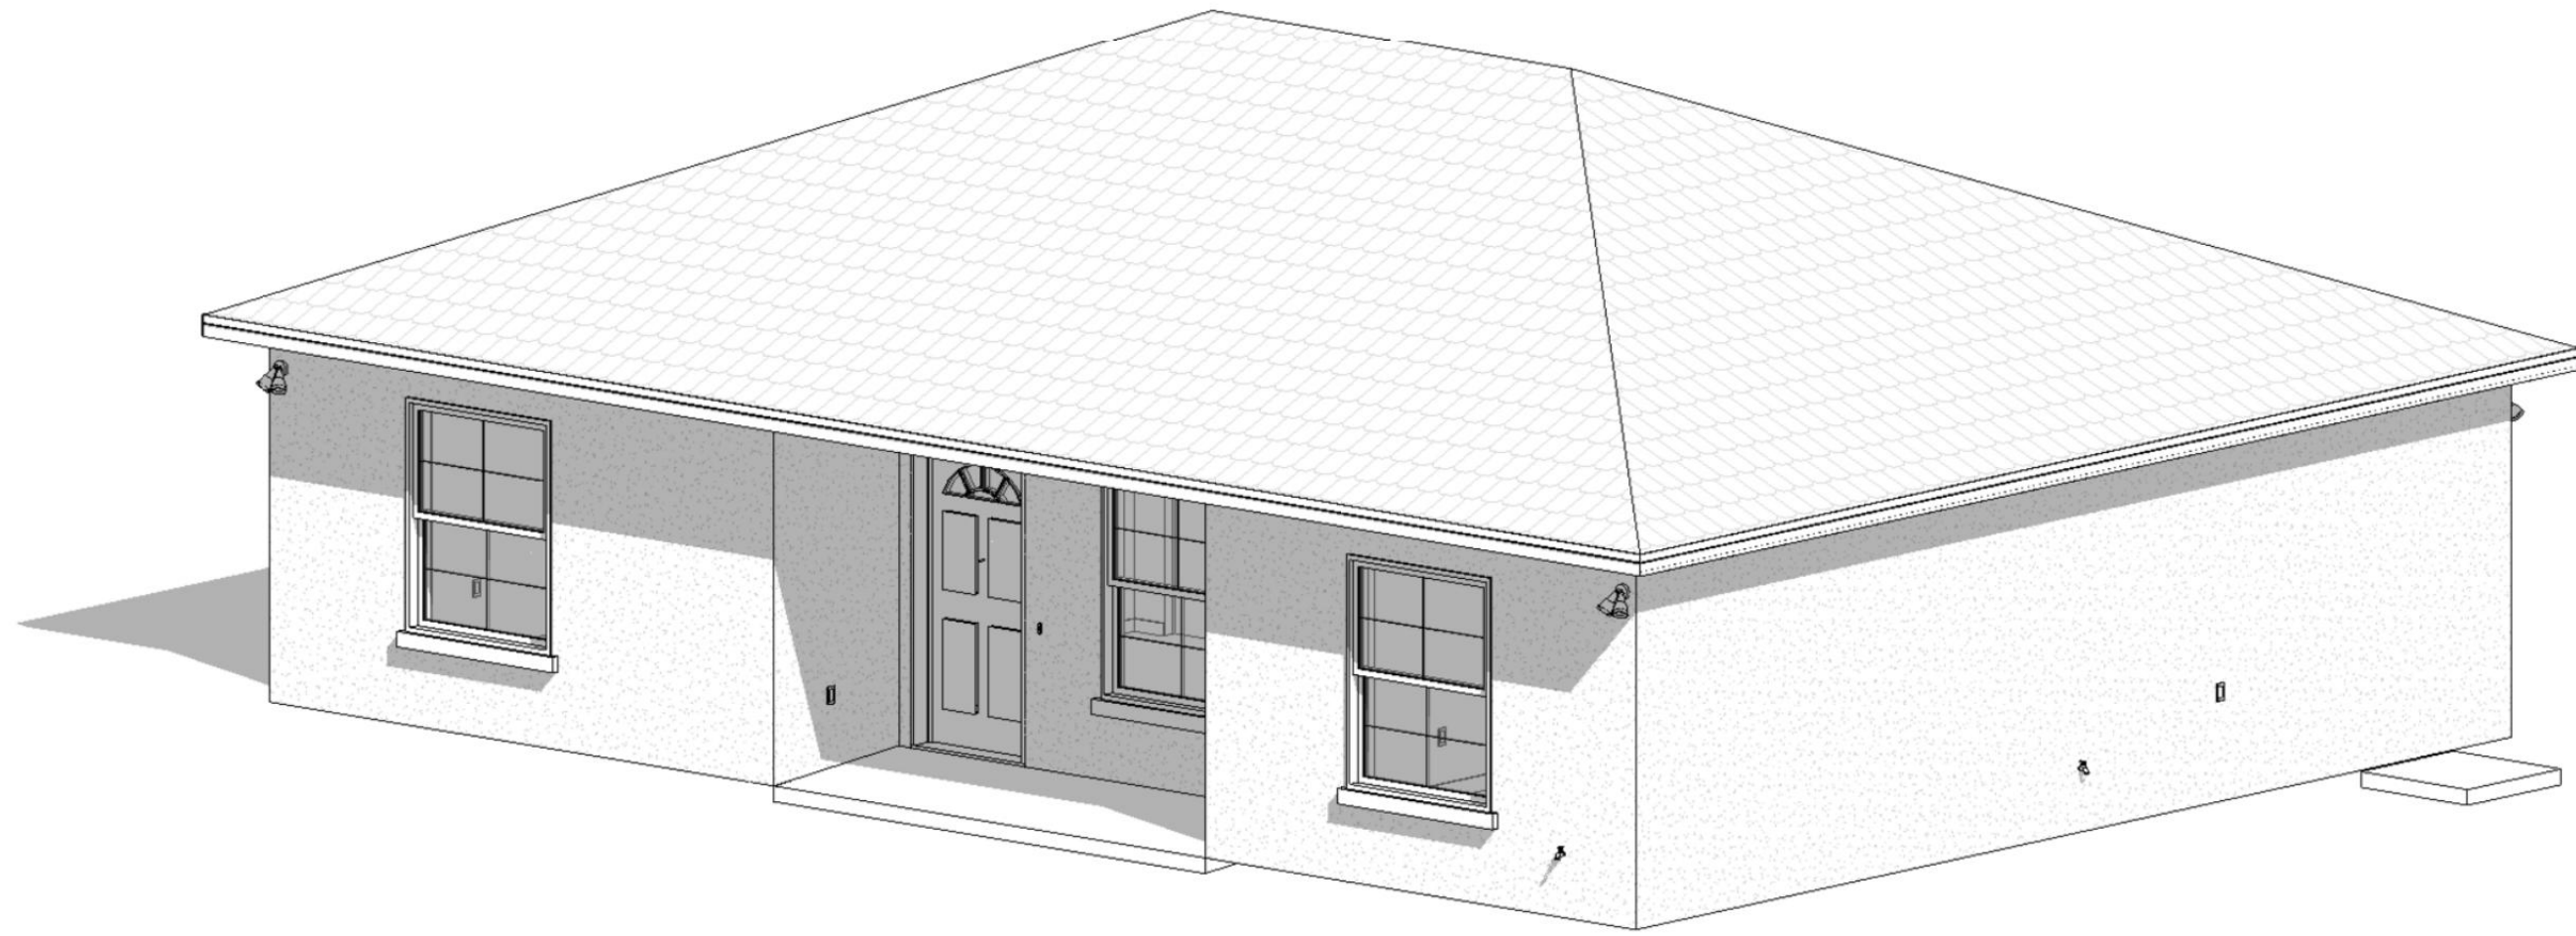

SHEET SCHEDULE			
REV. NO.	SHEET NAME	REVISION	REV. DATE
3. GENERAL			
A-001	COVER SHEET		
A-002	GENERAL NOTES		
4. ARCHITECTURAL			
A-101	ARCHITECTURAL SITE PLAN		
A-102	FIRST LEVEL FLOORPLAN		
A-103	ROOF PLAN		
A-201	EXTERIOR ELEVATIONS		
A-202	EXTERIOR ELEVATIONS		
A-203	EXTERIOR ISOMETRIC		
A-301	BUILDING SECTIONS		
AD-01	ARQUITECTURAL DETAILS		
AD-02	ARQUITECTURAL DETAILS - ROOF		
AD-03	ARQUITECTURAL DETAILS - DOOR / WINDOW		
AD-04	ARQUITECTURAL DETAILS - WINDOW FLASHING		
AD-05	ARCHITECTURAL DETAILS - DOOR FLASHING		
AD-06	ARQUITECTURAL DETAILS		
5. ELECTRICAL			
E-101	FIRST FLOOR ELECTRICAL PLAN		
6. STRUCTURAL			
S001	STRUCTURAL NOTES		
S002	STRUCTURAL NOTES		
S101	FOUNDATION PLAN		
S102	ROOF FRAMING PLAN		
S103	LINTEL SCHEDULE		
SD100	GENERAL DETAILS		
SD101	GENERAL DETAILS		
SD200	FOUNDATION DETAILS - S.O.G.		
SD201	FRAMING DETAILS - ROOF		

AREA SCHEDULE	
Name	Area
LIVABLE AREA	1016 SF
NON-LIVABLE AREA	48 SF
TOTAL	1064 SF

THE ELECTRONIC SEAL
PLACED ON THESE
DOCUMENTS DOES NOT
APPLY TO THE
FOLLOWING PAGES:
E101 AND E102



ARCHITECTURE
ENGINEERING
1230 Oakley Seaver Drive, Suite 100
Clermont, Florida 34711
888.850.FFAE (3323)
www.forefront.com
AR102538-CA30900

ISSUE - REVISION LOG

MARK.	DATE	DESCRIPTION

ASSISTANCE PROGRAM -
DBURRY RESIDENCE
826 NW 6TH AVE., Ocala, FL 34475

COVER SHEET