


Austin, TX 78704

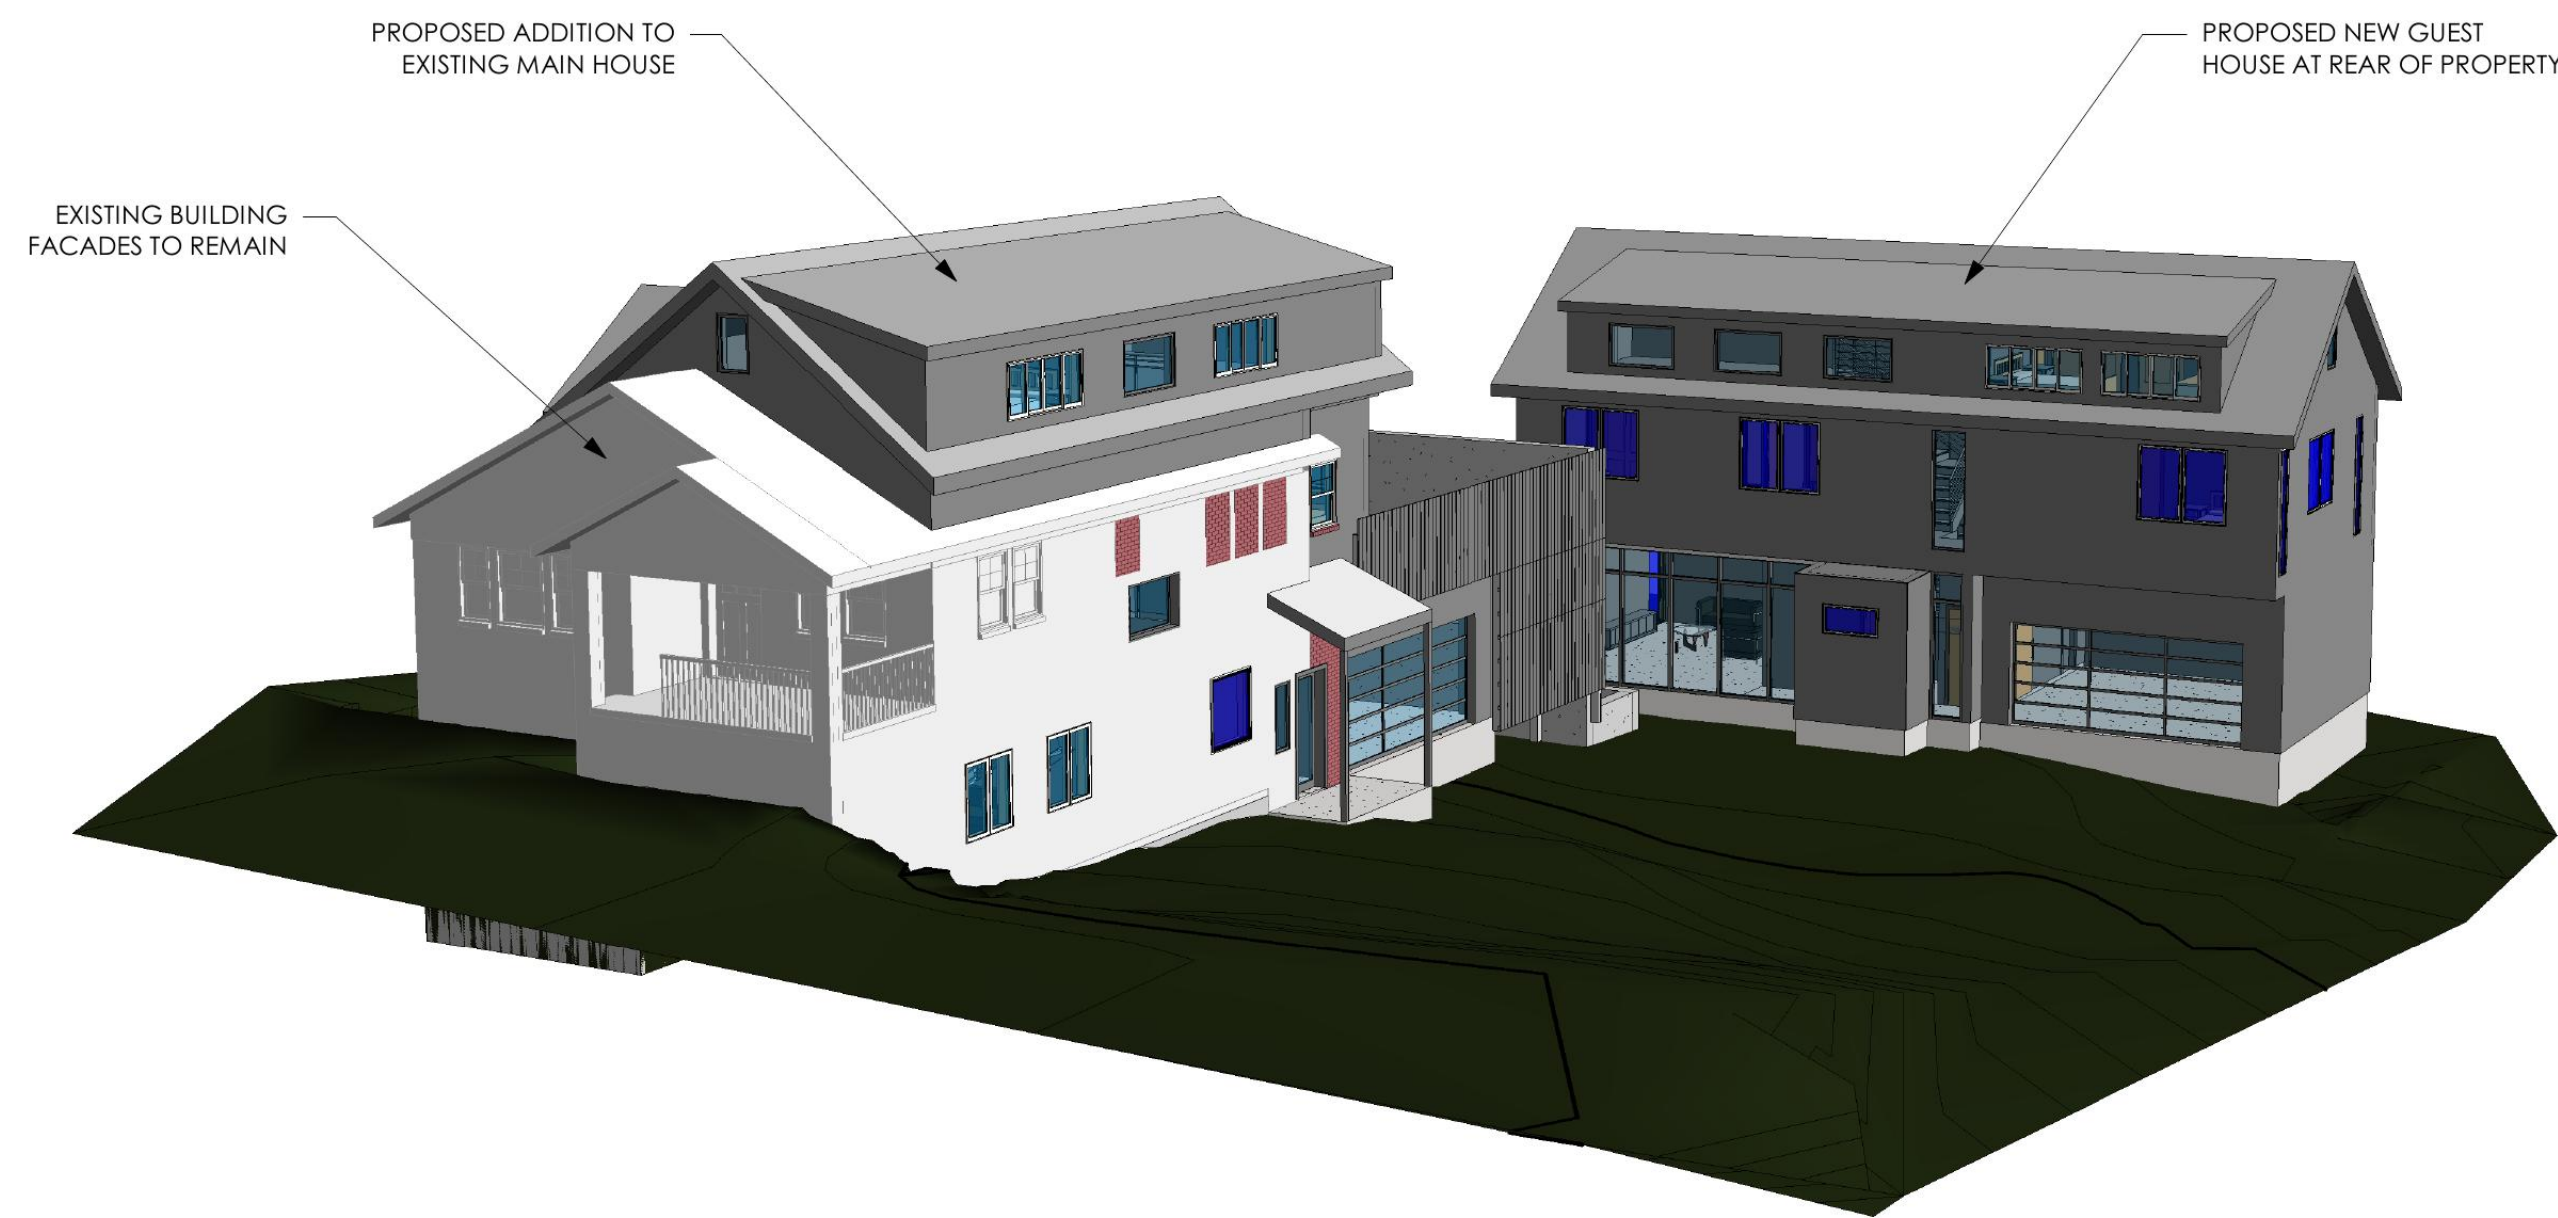

DRAWING LIST:

ARCHITECTURAL

A001

COVER SHEET

X

X

A002

SPECIFICATIONS

A101

SITE PLAN & TREE PROTECTION DETAILS

X

A102

TREE IMPACT SITE PLAN

A109

FOUNDATION PLAN - SITE

A110

FOUNDATION PLAN A

A111

FOUNDATION PLAN B

A113

FIRST FLOOR PLAN - OVERVIEW

A114

FIRST FLOOR PLAN - MAIN HOUSE

X

A115

SECOND FLOOR PLAN - MAIN HOUSE

X

A116

ATTIC FLOOR PLAN - MAIN HOUSE

X

A117

FIRST FLOOR PLAN & RCP - GUEST HOUSE

X

A118

SECOND FLOOR PLAN & RCP - GUEST HOUSE

X

A119

ATTIC FLOOR PLAN & RCP - GUEST HOUSE

X

A120

FIRST FLOOR REFLECTED CEILING PLAN - MAIN

A121

SECOND FLOOR REFLECTED CEILING PLAN - MAIN

A122

ATTIC FLOOR REFLECTED CEILING PLAN - MAIN

A131

ROOF PLAN

X

A132

SOFFIT PLAN

A201

EXTERIOR ELEVATIONS - SITE/ZONING

X

A202

EXTERIOR ELEVATIONS - SITE/ZONING

X

A203

EXTERIOR ELEVATIONS - MAIN HOUSE

X

A204

EXTERIOR ELEVATIONS - GUEST HOUSE

X

A301

BUILDING SECTIONS

X

A302

BUILDING SECTIONS

X

A303

BUILDING SECTIONS

X

A304

BUILDING SECTIONS

X

A305

BUILDING SECTIONS

X

A306

BUILDING SECTIONS

X

A311

DETAILED WALL SECTIONS

X

A312

DETAILED WALL SECTIONS

X

A313

DETAILED WALL SECTIONS

X

A411

INTERIOR ELEVATIONS

X

A412

INTERIOR ELEVATIONS

X

A413

INTERIOR ELEVATIONS

X

A414

INTERIOR ELEVATIONS

X

A415

INTERIOR ELEVATIONS

X

A416

INTERIOR ELEVATIONS

X

A501

EXTERIOR PLAN DETAILS

A502

EXTERIOR SECTION DETAILS AT SLAB

A503

EXTERIOR SECTION DETAILS AT ROOF

A504

EXTERIOR SECTION DETAILS AT ROOF

A601

GLAZING SCHEDULE

A602

DOOR SCHEDULES

A603

APPLIANCE / UTILITY / PLUMBING SCHEDULES

STRUCTURAL

S1

FOUNDATION REINFORCEMENT - ENTRY & GUESTS

X

S1.1

FOUNDATION REINFORCEMENT - LIVING & KITCHEN

X

S1.2

FOUNDATION REINFORCEMENT - BEDROOM SUITE

X

S2

FOUNDATION LAYOUT - ENTRY & GUESTS

X

S2.1

FOUNDATION LAYOUT - LIVING & KITCHEN

X

S2.2

FOUNDATION LAYOUT - BEDROOM SUITE

X

S3

FOUNDATION DETAILS

X

S4

LEVEL 1 CEILING FRAMING PLAN - ENTRY & GUESTS

X

S4.1

LEVEL 1 CEILING FRAMING PLAN - LIVING & KITCHEN

X

S4.2

LEVEL 1 CEILING FRAMING PLAN - BEDROOM SUITE

X

S5

LEVEL 1 DROPPED CEILING PLAN - ENTRY & GUESTS

X

S5.1

LEVEL 1 DROPPED CEILING PLAN - BEDROOM SUITE

X

S6

CLERESTORY CEILING FRAMING PLAN

X

S7

OVERLAY PLAN

X

S8

ROOF FRAMING PLAN - ENTRY & GUESTS

X

S8.1

ROOF FRAMING PLAN - LIVING & KITCHEN

X

S8.2

ROOF FRAMING PLAN - BEDROOM SUITE

X

S9

LEVEL 1 LATERAL BRACING PLAN - ENTRY & GUESTS

X

S9.1

LEVEL 1 LATERAL BRACING PLAN - LIVING & KITCHEN

X

S9.2

LEVEL 1 LATERAL BRACING PLAN - BEDROOM SUITE

X

S10

CLERESTORY LATERAL BRACING PLAN

X

S11

FRAMING NOTES

X

S12

FRAMING DETAILS

X

S13

FRAMING DETAILS

X

S14

FRAMING DETAILS

X

S15

FRAMING DETAILS

X

S16

FRAMING DETAILS

X

S17

FRAMING DETAILS

X

SUBCHAPTER F:

XXXXX