


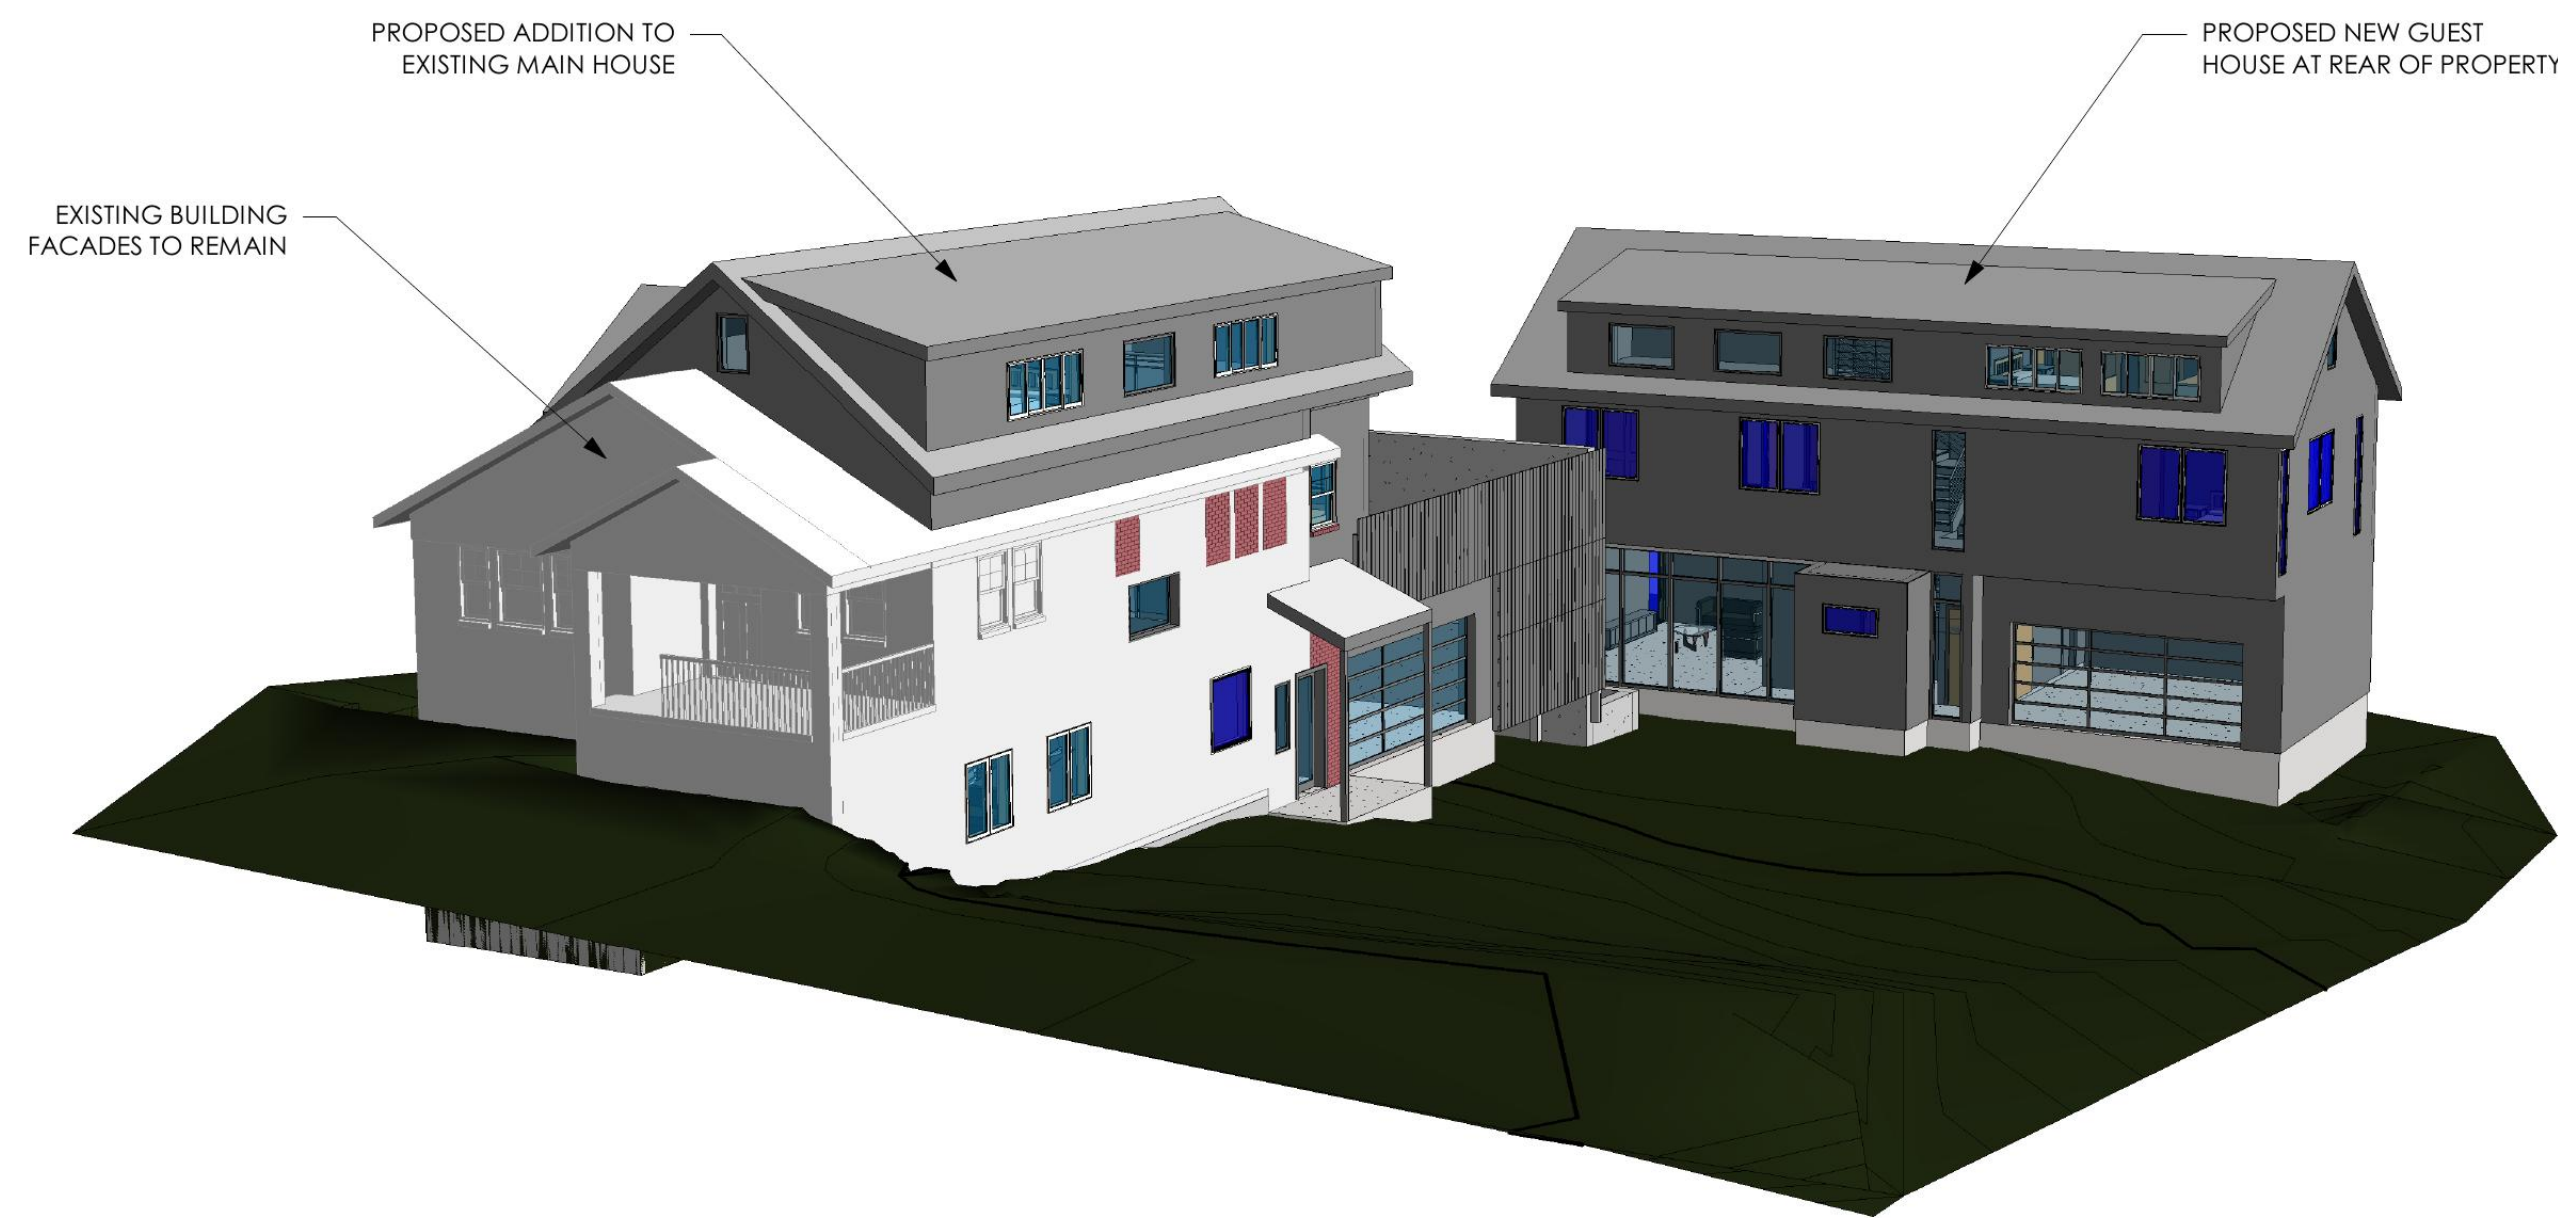

DRAWING LIST:

ARCHITECTURAL

A001

COVER SHEET

X

X

A002

SPECIFICATIONS

A101

SITE PLAN & TREE PROTECTION DETAILS

X

A102

TREE IMPACT SITE PLAN

A109

FOUNDATION PLAN - SITE

A110

FOUNDATION PLAN A

A111

FOUNDATION PLAN B

A113

FIRST FLOOR PLAN - OVERVIEW

A114

FIRST FLOOR PLAN - MAIN HOUSE

X

A115

SECOND FLOOR PLAN - MAIN HOUSE

X

A116

ATTIC FLOOR PLAN - MAIN HOUSE

X

A117

FIRST FLOOR PLAN & RCP - GUEST HOUSE

X

A118

SECOND FLOOR PLAN & RCP - GUEST HOUSE

X

A119

ATTIC FLOOR PLAN & RCP - GUEST HOUSE

X

A120

FIRST FLOOR REFLECTED CEILING PLAN - MAIN

A121

SECOND FLOOR REFLECTED CEILING PLAN - MAIN

A122

ATTIC FLOOR REFLECTED CEILING PLAN - MAIN

A131

ROOF PLAN

X

A132

SOFFIT PLAN

A201

EXTERIOR ELEVATIONS - SITE/ZONING

X

A202

EXTERIOR ELEVATIONS - SITE/ZONING

X

A203

EXTERIOR ELEVATIONS - MAIN HOUSE

X

A204

EXTERIOR ELEVATIONS - GUEST HOUSE

X

A301

BUILDING SECTIONS

X

A302

BUILDING SECTIONS

X

A303

BUILDING SECTIONS

X

A304

BUILDING SECTIONS

X

A305

BUILDING SECTIONS

X

A306

BUILDING SECTIONS

X

A311

DETAILED WALL SECTIONS

X

A312

DETAILED WALL SECTIONS

X

A313

DETAILED WALL SECTIONS

X

A411

INTERIOR ELEVATIONS

X

A412

INTERIOR ELEVATIONS

X

A413

INTERIOR ELEVATIONS

X

A414

INTERIOR ELEVATIONS

X

A415

INTERIOR ELEVATIONS

X

A416

INTERIOR ELEVATIONS

X

A501

EXTERIOR PLAN DETAILS

A502

EXTERIOR SECTION DETAILS AT SLAB

A503

EXTERIOR SECTION DETAILS AT ROOF

A504

EXTERIOR SECTION DETAILS AT ROOF

A601

GLAZING SCHEDULE

A602

DOOR SCHEDULES

A603

APPLIANCE / UTILITY / PLUMBING SCHEDULES

STRUCTURAL

S1

FOUNDATION REINFORCEMENT - ENTRY & GUESTS

X

S1.1

FOUNDATION REINFORCEMENT - LIVING & KITCHEN

X

S1.2

FOUNDATION REINFORCEMENT - BEDROOM SUITE

X

S2

FOUNDATION LAYOUT - ENTRY & GUESTS

X

S2.1

FOUNDATION LAYOUT - LIVING & KITCHEN

X

S2.2

FOUNDATION LAYOUT - BEDROOM SUITE

X

S3

FOUNDATION DETAILS

X

S4

LEVEL 1 CEILING FRAMING PLAN - ENTRY & GUESTS

X

S4.1

LEVEL 1 CEILING FRAMING PLAN - LIVING & KITCHEN

X

S4.2

LEVEL 1 CEILING FRAMING PLAN - BEDROOM SUITE

X

S5

LEVEL 1 DROPPED CEILING PLAN - ENTRY & GUESTS

X

S5.1

LEVEL 1 DROPPED CEILING PLAN - BEDROOM SUITE

X

S6

CLERESTORY CEILING FRAMING PLAN

X

S7

OVERLAY PLAN

X

S8

ROOF FRAMING PLAN - ENTRY & GUESTS

X

S8.1

ROOF FRAMING PLAN - LIVING & KITCHEN

X

S8.2

ROOF FRAMING PLAN - BEDROOM SUITE

X

S9

LEVEL 1 LATERAL BRACING PLAN - ENTRY & GUESTS

X

S9.1

LEVEL 1 LATERAL BRACING PLAN - LIVING & KITCHEN

X

S9.2

LEVEL 1 LATERAL BRACING PLAN - BEDROOM SUITE

X

S10

CLERESTORY LATERAL BRACING PLAN

X

S11

FRAMING NOTES

X

S12

FRAMING DETAILS

X

S13

FRAMING DETAILS

X

S14

FRAMING DETAILS

X

S15

FRAMING DETAILS

X

S16

FRAMING DETAILS

X

S17

FRAMING DETAILS

X

SUBCHAPTER F:

XXXXX

BUILDING & PROPERTY INFORMATION:

LEGAL DESCRIPTION:

LOT 8 AND NORTH 30 FEET OF LOT 7, BLOCK 31, TRAVIS HEIGHTS, A SUBDIVISION RECORDED IN VOLUME 3, PAGE 15, PLAT RECORDS OF TRAVIS COUNTY, TEXAS

NEIGHBORHOOD PLAN:

SOUTH RIVER CITY; TRAVIS HEIGHTS-SWISHER

OWNER:

SAL & DAWN MIRRAN

ADDRESS:

1509 TRAVIS HEIGHTS BLVD., AUSTIN, TX 78704

ZONING:

SF-3-NP

JURISDICTION:

AUSTIN FULL PURPOSE

FLOODPLAIN:

NO

WATERSHED:

HRP1: HARPER'S BRANCH

EXISTING USE:

SINGLE-FAMILY RESIDENTIAL

PROPOSED USE:

SINGLE-FAMILY RESIDENTIAL

SITE SQUARE FOOTAGE:

11,085.20 SQ FT

APPLICABLE CODE:

2021 IRC

GROSS FLOOR AREA: (As defined by subchapter f, Section 3.3)

EXISTING

NEW

EXEMPTION

TOTAL

BLDG 1

BLDG 2

BLDG 1

BLDG 2

1ST FLOOR:

1,121 SF

-----

971 SF

834 SF

-----

1,805 SF

2ND FLOOR:

1,211 SF

-----

1,262 SF

1,290 SF

-----

2,552 SF

3RD FLOOR:

-----

-----

-----

-----

-----

0

15+ CLG:

-----

-----

-----

-----

-----

0

GROUND PORCH/PATIO:

131

-----

152

-----

-283

0

BASEMENT:

-----

-----

-----

-----

-----

0

ATTIC:

-----

-----

741 SF

883 SF

-1,624SF

0

ATTACHED CARPORT

-----

-----

471 SF

-----

-450 SF

21 SF

DETACHED GARAGE/CARPORT

305 SF

-----

447 SF

-450 SF

0

CONDITIONED AREA:

2,974 SF

3,007 SF

GROSS FLOOR AREA:

4,378 SF

LOT AREA:

11,085.2 SF

TOTAL FLOOR AREA RATIO:

39.49%

TOTAL ALLOWABLE FLOOR AREA: (Maximum allowable by subchapter "F", Article 2, Section 2.1)

4,434.08 SF

SITE IMPERVIOUS COVERAGE:

SITE TOTAL SF:

11,085.20

45% ALLOWED:

X 45% = 4,988.34

BUILDING 1 COVERAGE

1,830 SF

BUILDING 2 COVERAGE

1,342.5 SF

DRIVEWAY

1,359 SF

CONCRETE PAVERS

213 SF

POOL COPING & RETAINING

92 SF

WOOD DECK (50%)

138 X .5 = 69 SF

TOTAL:

4,905.5 SF (44.25%)

MAXIMUM ALLOWED:

4,988.34 SF (45.0%)

BUILDING COVERAGE:

SITE TOTAL SF:

11,085.20

EXISTING BUILDING COVERAGE:

1,647 SF

FINAL BUILDING COVERAGE:

3,172.5 SF (28.62%)