

DEFERRED PERMIT SUBMITTALS

REFERENCE SECTION 01 31 16 - DELEGATED DESIGN PROCEDURES
DIVISION 03 - SECTION 03 38 00 - POST-TENSIONED CONCRETE
DIVISION 06 - SECTION 06 17 33 - WOOD JOISTS
DIVISION 06 - SECTION 06 17 33 - SHOP-FABRICATED WOOD TRUSSES
DIVISION 05 - SECTION 05 73 00 - DECORATIVE METAL RAILINGS AND ATTACHMENTS
DIVISION 05 - SECTION 05 73 00 - ALUMINUM FRAMED STOREFRONTS
DIVISION 23 - MECHANICAL ATTACHMENT OF ROOF CURBS & EQUIPMENT TO ROOF STRUCTURE
DIVISIONS 22, 23 & 26 - SEISMIC BRACING OF MEP EQUIPMENT


SEPARATE PERMIT SUBMITTALS

DIVISION 08 - KNOX BOX (TO BE OBTAINED FROM FIRE MARSHAL'S OFFICE)
DIVISION 10 - OCCUPANT LOAD SIGNS (TO BE OBTAINED FROM FIRE MARSHAL'S OFFICE)
DIVISION 21 - FIRE SUPPRESSION SYSTEM
DIVISION 22 - PLUMBING TRADE PERMIT
DIVISION 26 - ELECTRICAL TRADE PERMIT
DIVISION 28 - FIRE DETECTION AND ALARM
DEMOLITION PERMIT
TENANT IMPROVEMENTS


DISCLAIMER

THE WRITTEN AGREEMENT, DRAWINGS, SPECIFICATIONS AND ANY ADDENDA COMPRISE THE CONTRACT FOR THIS PROJECT. THEY SHALL BE TREATED AS ONE ENTITY, EQUALLY, WITHOUT PRIORITY, ITEMS, ELEMENTS, FIXTURES, SYSTEMS AND EQUIPMENT SHOWN SHALL BE FURNISHED AND INSTALLED EVEN THOUGH TYPICALLY SHOWN ELSEWHERE. THEREFORE IT IS THE RESPONSIBILITY OF THE CONTRACTOR TO READ AND COMPREHEND ALL THESE DOCUMENTS IN ORDER TO COMPLETE THE WORK. IF A CONTRACTOR CHOOSES TO NOT THOROUGHLY REVIEW THE ENTIRE SET OF CONTRACT DOCUMENTS, THEY DO SO AT THEIR OWN RISK AND AGREE TO FURNISH & INSTALL ALL ITEMS NOTED ABOVE AT NO ADDITIONAL COST OR DELAY TO THE OWNER. (THE ONLY EXCEPTION TO THIS IS THAT THE SPECIFICATIONS SHALL TAKE PRECEDENCE OVER GENERAL NOTES ON THIS SHEET.)

GENERAL SITE PLAN - NTS

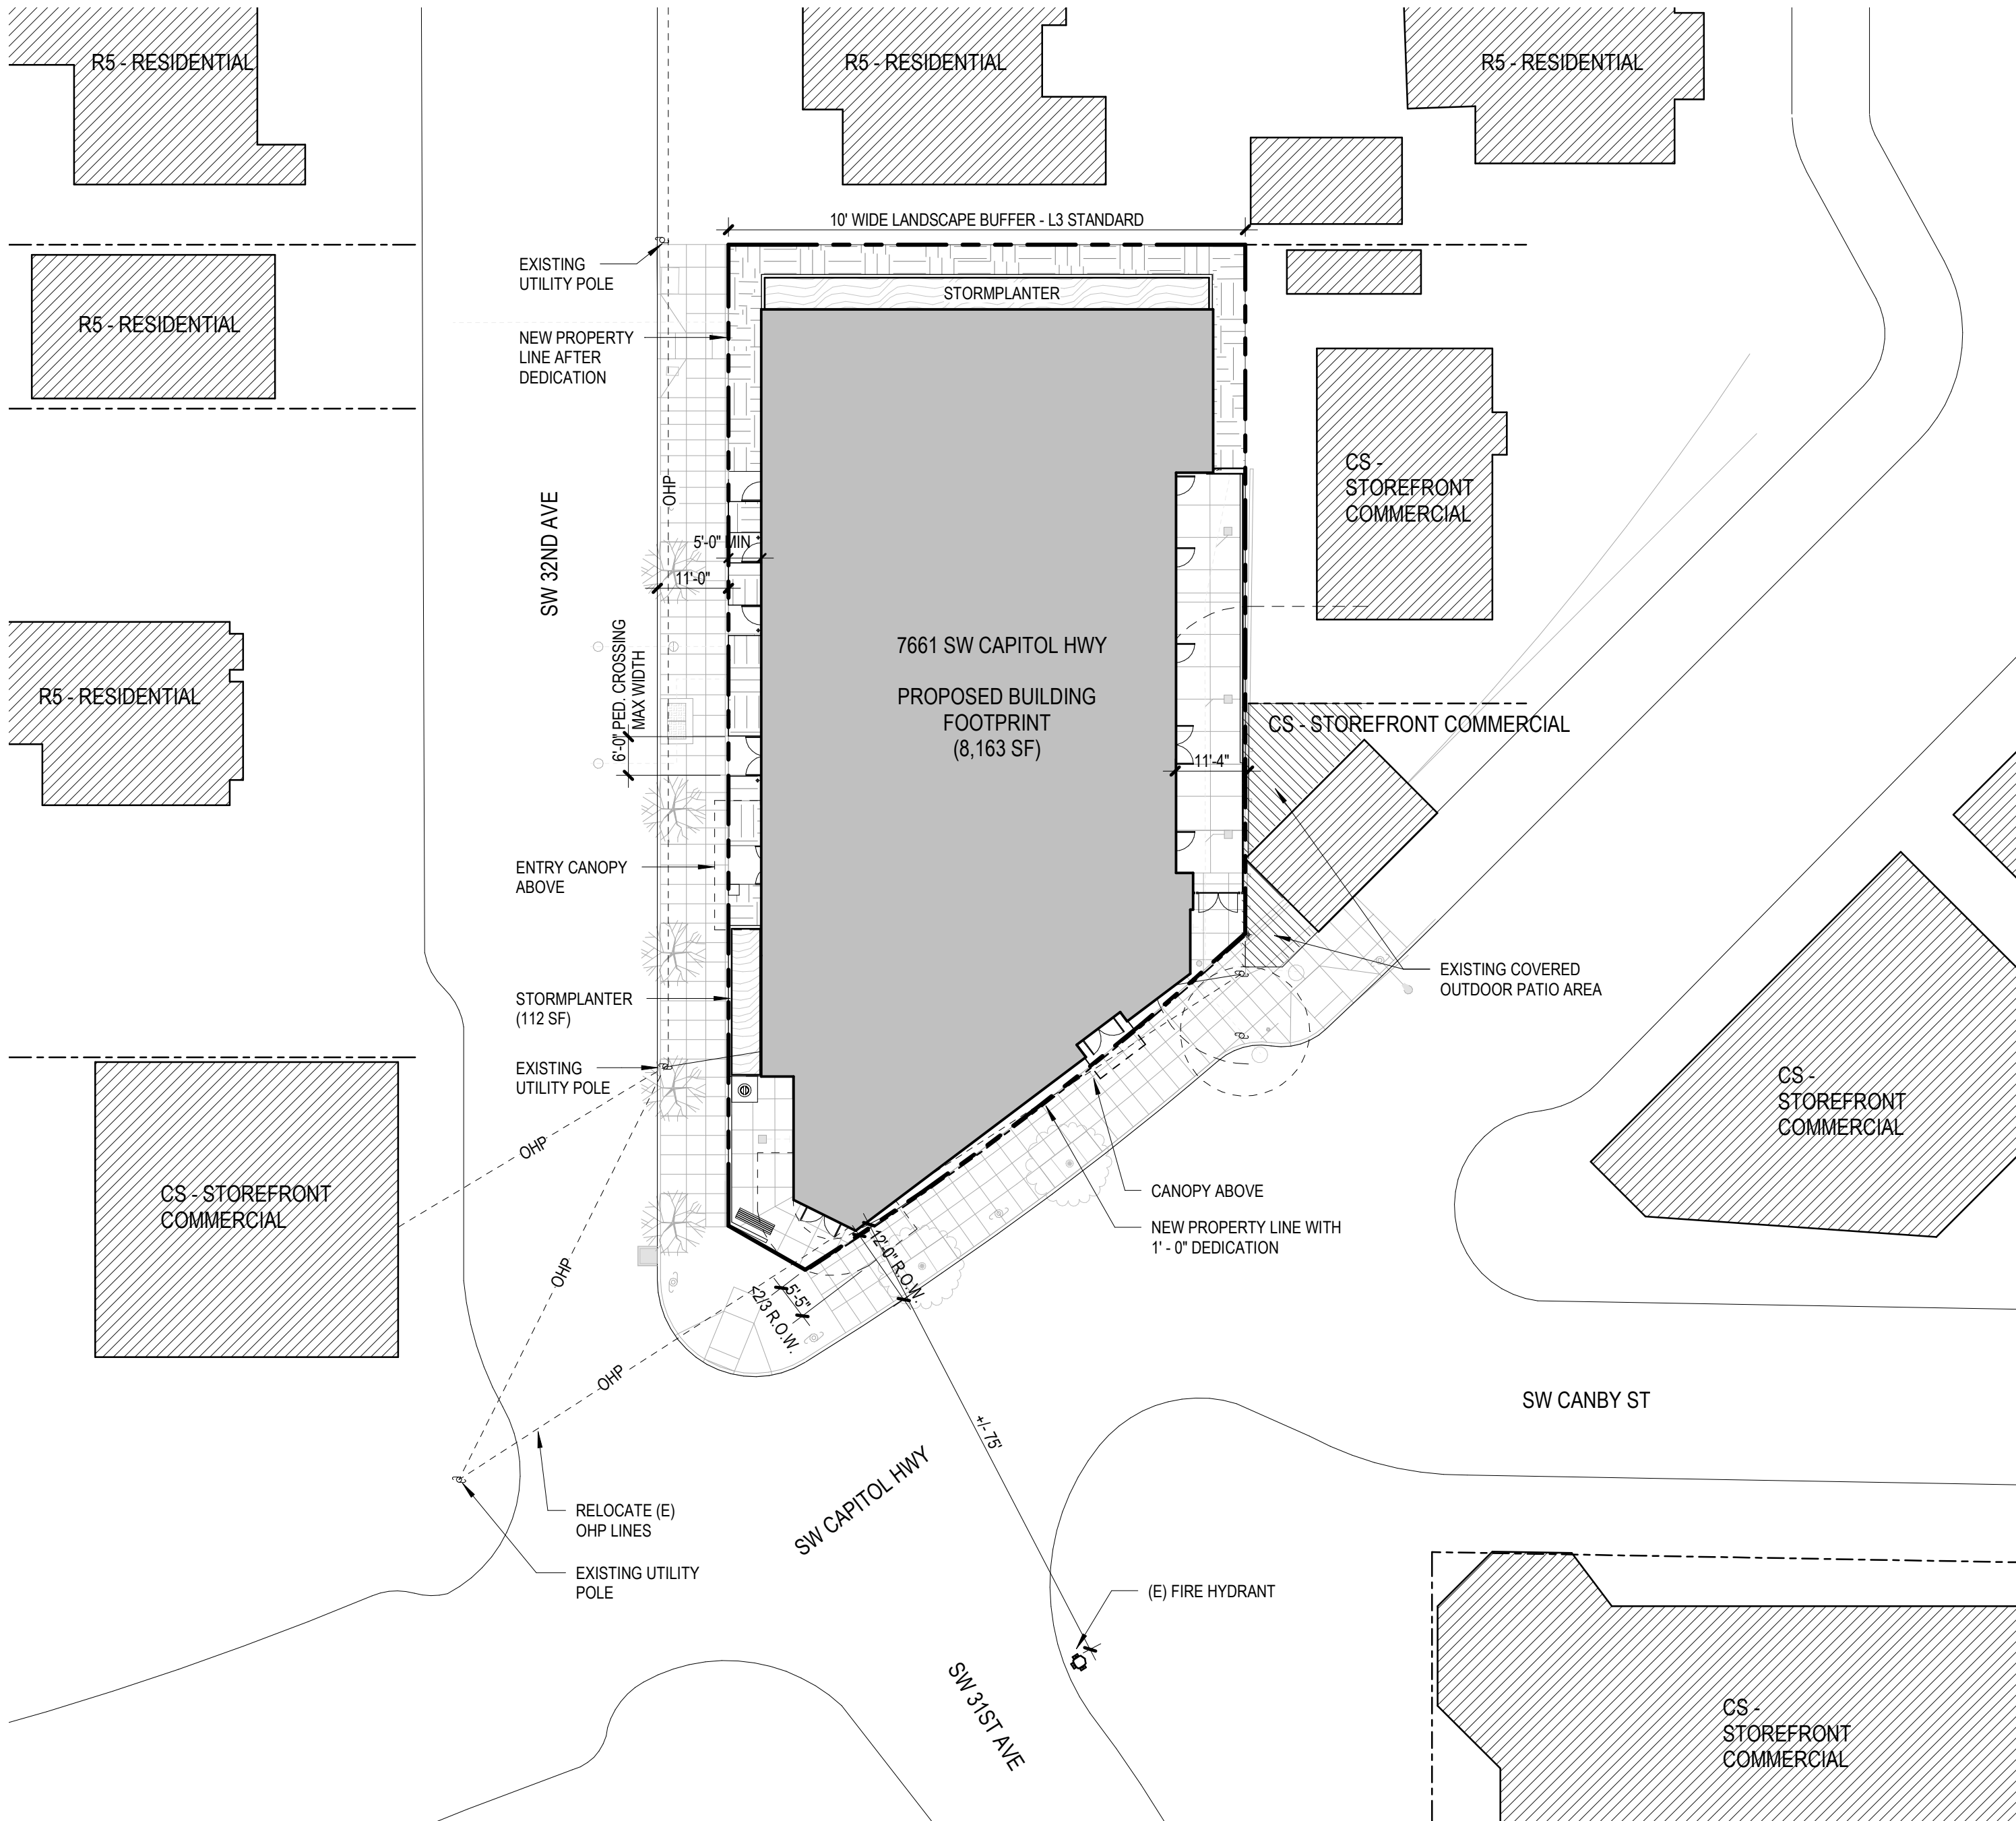

SYMBOLS LEGEND

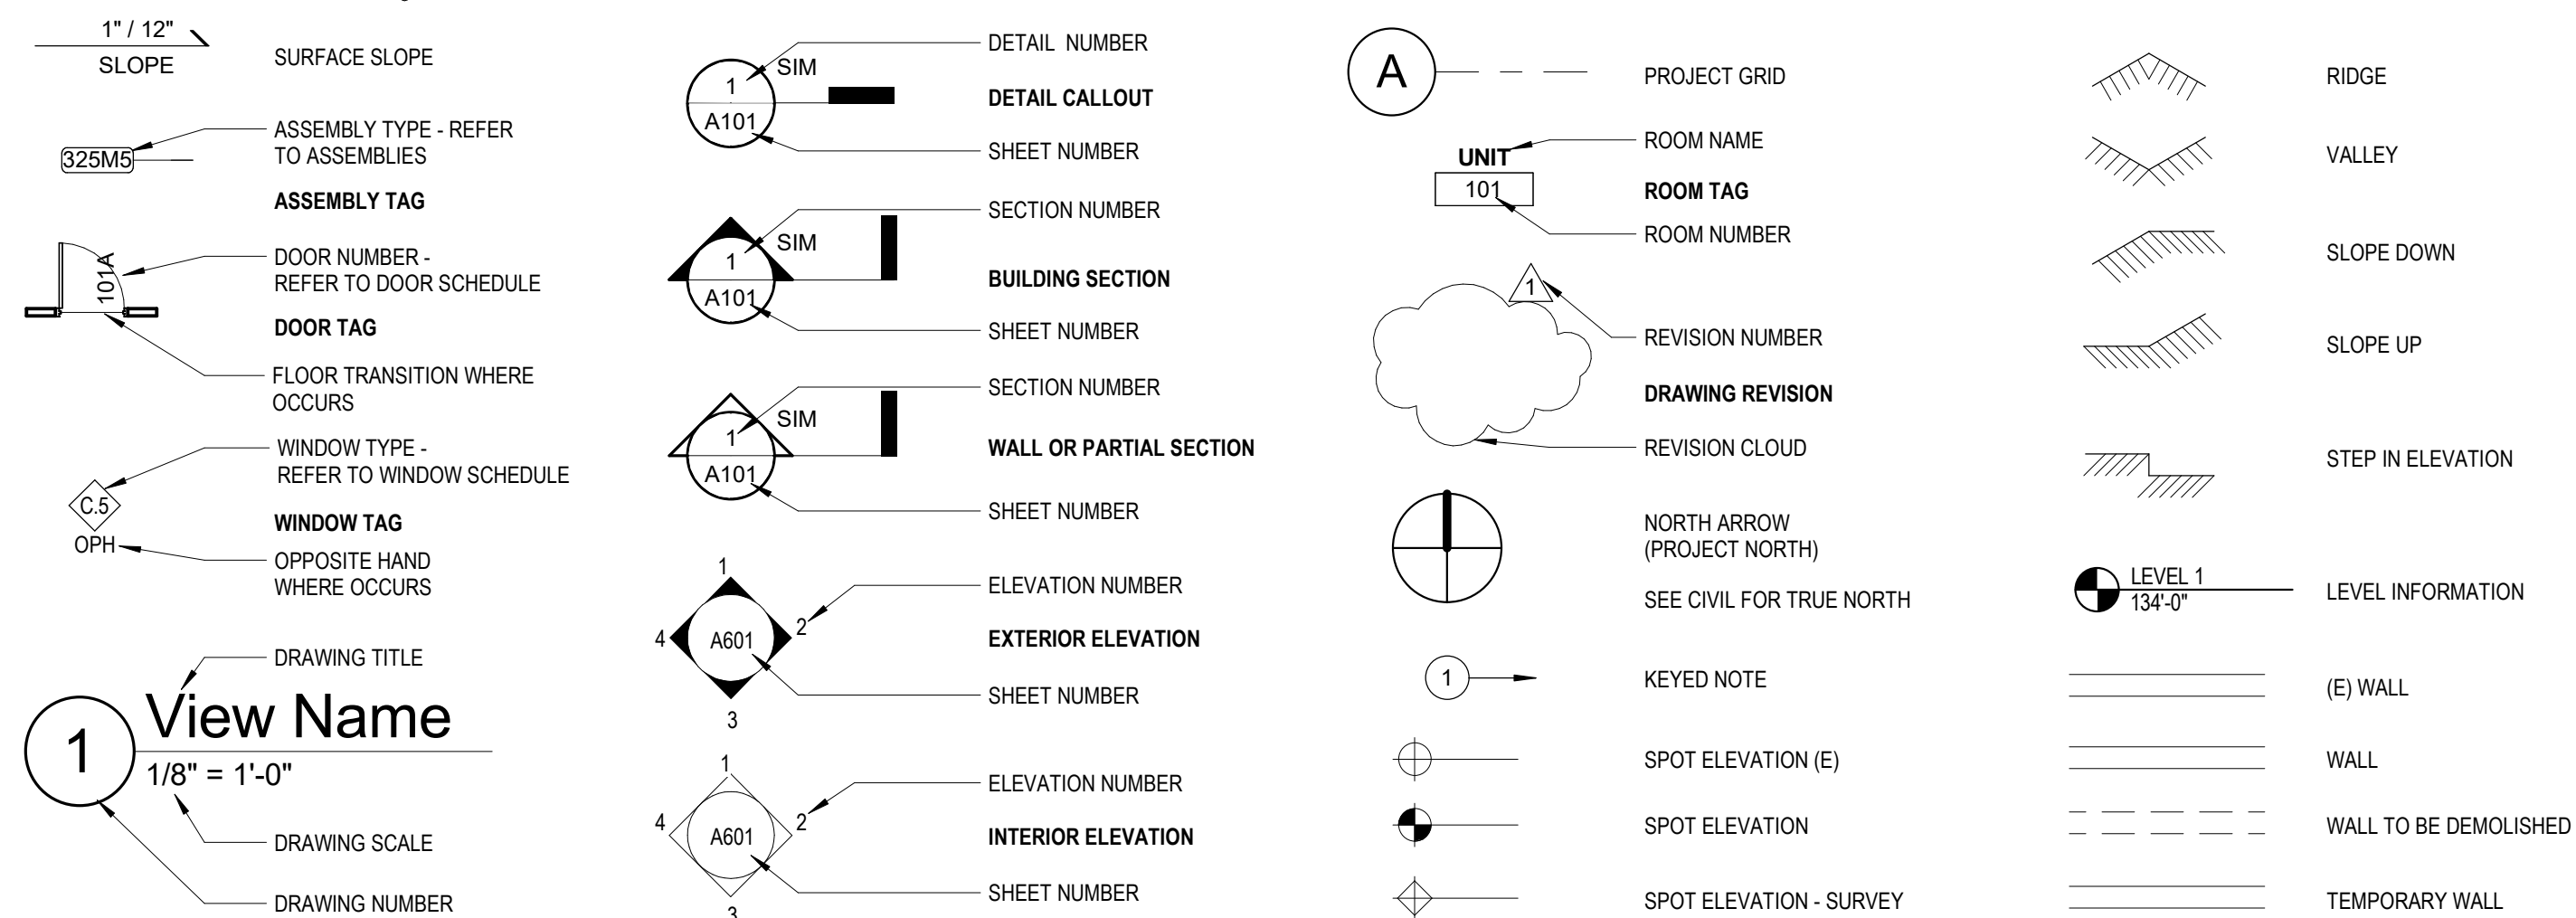

MATERIAL CODES

ACT-# ACUSTICAL CEILING
AWCS-# ACUSTICAL WALL OR CEILING SYSTEM
BR-# BRICK
CHW-# CABINET HARDWARE
CONC-# CONCRETE
CORK-# CORK
CTP-# CARPET
CTP-# COUNTERTOP
EP-# EPOXY PAINT
F-# FABRIC
FAF-# FLUID-APPLIED FLOORING
FRP-# FIBERGLASS REINFORCED PLASTIC PANELING
GL-# GLAZING
GLF-# GLAZING FILM
HPC-# HIGH-PERFORMANCE COATING
MIR-# MIRROR
MIL-# METAL
MTL-# METAL BASE
MTC-# METAL CEILING
MTP-# METAL PANELING
P-# PAINT
PL-# PLASTIC LAMINATE
RAF-# RESILIENT ATHLETIC FLOORING
RB-# RESILIENT BASE
RF-# RESILIENT FLOORING
SS-# STAINLESS STEEL
SSF-# SIMULATED STONE FABRICATIONS
ST-# STONE CLADDING
STN-# STAIN
T-# TILE
T-# TERRAZZO
T-# VISUAL DISPLAY BOARD
V-# VENEER PLASTERING
W-# WALL COVERING
WD-# WOOD
WDB-# WOOD BASE
WDC-# WOOD CEILING
WDF-# WOOD FLOORING
WDP-# WOOD PANELING
WDM-# WALK OFF MAT
WP-# WALL PROTECTION
WT-# WINDOW TREATMENT

ABBREVIATIONS

--- NONE
& AND
@ AT
± APPROXIMATELY
CL CENTERLINE
Ø DIAMETER
NUMBER
" INCHES
' FEET
ACSF ACCESS FLOORING
ADJ ADJACENT
AFF ABOVE FINISH FLOOR
AHJ AUTHORITY HAVING JURISDICTION
BO BOTTOM OF
BOB BOTTOM OF BEAM
BOT BOTTOM
BOS BOTTOM OF STEEL
CJ APPLICABLE REGULATIONS GOVERNING CONTRACT SCOPE OF WORK, SEE CODE COMPLIANCE SUMMARY SHEETS
CLG CEILING
CMU CONCRETE MASONRY UNIT
CO CEAN OUT
CS DOWN SPOUT
DW DISHWASHER
DWG DRAWING
EJ EXISTING
EQ EXPANSION JOINT
EQ EQUAL
EXP EXPOSED STRUCTURE
FD FLOOR DRAIN
FE FIRE EXTINGUISHER
FEC FIRE EXTINGUISHER CABINET
FF FL FINISH FLOOR ELEV
FO FACE OF
FOB FACE OF BEAM
FOC FACE OF CONCRETE
FOF FACE OF FINISH
FOM FACE OF MASONRY
FOS FACE OF STUD
FW FACE OF WALL
GA GAUGE
GB GYPSUM BOARD
GALV GALVANIZED
HB HOSE BIB
HS HEAT STRENGTHENED
ID INSIDE DIAMETER
MAX MAXIMUM
MH MANHOLE
MIN MINIMUM
MO MASONRY OPENING
MTR MATERIAL
MW MICROWAVE
NIC NOT IN CONTRACT
NTS NOT TO SCALE
OAE OR APPROVED EQUAL
OC ON CENTER
OD OUTSIDE DIAMETER
OFD OVERFLOW DRAIN
OFICI OWNER FURNISHED, CONTRACTOR INSTALLED
OFIO OWNER FURNISHED, OWNER INSTALLED
OPH OPPOSITE HAND
PREFINISHED (ALTERNATE PREFIN)
PLAS PLASTER
RCP REFLECTED CEILING PLAN
RD ROOF DRAIN
REF REFRIGERATOR
RO ROUGH OPENING
ROW RIGHT OF WAY
SF SQUARE FOOT (FEET)
SHTHG SHEATHING
SIMILAR
SST STAINLESS STEEL (BASE, WALL PANEL, OR COVERING)
STN STAIN
T TEMPERED
TOB TOP OF
TOC TOP OF BEAM
TOC TOP OF CONCRETE
TOD TOP OF STEEL DECK
TOP TOP OF PARAPET
TOS TOP OF STEEL
TOW TOP OF WALL
TM TO MATCH
TYP TYPICAL
UNO UNLESS NOTED OTHERWISE
VIF VERIFY IN FIELD

VICINITY MAP



GENERAL NOTES

- FIELD VERIFY ALL EXISTING CONDITIONS AND DIMENSIONS PRIOR TO PROCEEDING WITH THE WORK.
- DIMENSIONS TAKE PRECEDENCE OVER DRAWINGS. DO NOT SCALE. DRAWINGS NOTIFY ARCHITECT OF DISCREPANCIES PRIOR TO PROCEEDING WITH THE WORK.
- CONTRACTOR IS SOLELY RESPONSIBLE FOR CONSTRUCTION MEANS AND METHODS AND SHALL MAINTAIN THE STRUCTURAL INTEGRITY OF CONSTRUCTION UNTIL FINAL LATERAL AND VERTICAL CARRYING SYSTEMS ARE COMPLETED.
- DIMENSIONS SHOWN ARE TO FACE OF STUD, FACE OF CONCRETE, FACE OF MASONRY, GRID/COLUMN LINE, CENTER OF ELEMENT, COUNTERTOP EDGE, OR AS NOTED.
- CONTRACTOR IS RESPONSIBLE FOR VERIFICATION AND COORDINATION OF SUBCONTRACTORS WORK, COMPLIANCE WITH DRAWINGS AND SPECIFICATIONS, ACCURATE LOCATION OF STRUCTURAL MEMBERS, OPENINGS FOR MECHANICAL, ELECTRICAL, AND MISCELLANEOUS EQUIPMENT. CONTRACTOR SHALL VERIFY DIMENSIONS AND OPENING SIZES (CLEARANCES REQUIRED) FROM THE MANUFACTURERS PRIOR TO CONSTRUCTION OF OR INSTALLATION OF EQUIPMENT, FURNISHINGS, AND ACCESSORIES.
- DETAILS NOTED AS "TYPICAL" OR "TYP" APPLY IN ALL CASES UNLESS SPECIFICALLY REFERENCED. DETAILS THAT ARE SPECIFICALLY REFERENCED SHALL TAKE PRECEDENCE OVER DETAILS NOTED AS "TYPICAL" OR "TYP". SPECIFIC NOTES AND DETAILS SHALL TAKE PRECEDENCE OVER GENERAL NOTES AND DETAILS.
- CONTRACTOR IS RESPONSIBLE FOR THE COMPLETE SECURITY OF THE SITE WHILE THE PROJECT IS IN PROGRESS UNTIL PROJECT COMPLETION.
- LOCATE EXISTING UTILITIES WHETHER INDICATED OR NOT AND PROTECT FROM DAMAGE. CONTRACTOR SHALL BEAR REPAIR OR REPLACEMENT EXPENSES OF UTILITIES OR OTHER PROPERTY DAMAGED BY OPERATIONS IN CONJUNCTION WITH THE PROSECUTION OF THE WORK.
- PROVIDE ACCESS PANELS AS REQUIRED. LOCATION, FINISH, AND TYPE SHALL BE APPROVED BY ARCHITECT PRIOR TO OBTAINING AND INSTALLING ACCESS PANEL. LOCATIONS NOT APPROVED BY ARCHITECT WILL BE SUBJECT TO MODIFICATION AT NO ADDITIONAL COST. PROVIDE RATED ACCESS PANELS WITH THE SAME RATING AS THE ASSEMBLY IN WHICH THEY ARE INSTALLED. ACCESS PANELS IN SHIRT WALLS, RATED FLOOR/CEILING OR RATED ROOF/CEILING SHALL BE SMOKE SEALED.
- TEMPORARY PEDESTRIAN PROTECTION SHALL BE PROVIDED AS REQUIRED BY THE AUTHORITY HAVING JURISDICTION STANDARDS.
- ALL PENETRATIONS THROUGH RATED ASSEMBLIES SHALL BE FIRE STOPPED PER SPECIFICATION SECTION 07 84 00 - FIRESTOPPING AND THE AUTHORITY HAVING JURISDICTION'S REQUIREMENTS. RATED ASSEMBLIES SHALL BE CONSTRUCTED TO PREVENT THE MOVEMENT OF HOT FLAME OR GASES PER OSSC SECTION 709.6.
- ALL SAFETY GLAZING SHALL BE PERMANENTLY LABELED WITH THE MANUFACTURERS NAME AND TEST APPROVAL INFORMATION.
- CONTRACTOR IS RESPONSIBLE FOR TRADE PERMITS, INCLUDING, BUT NOT LIMITED TO MECHANICAL, ELECTRICAL, AND EXTERIOR SIGNAGE. REFERENCE DEFERRED PERMITS SUMMARY ON THIS SHEET.
- PROVIDE BACKING, BLOCKING, OR STRAPPING AS REQUIRED FOR MOUNTING GRAB BARS, SHELVING, EQUIPMENT, HANDRAILS, ACCESSORIES, AND CASEWORK.
- PROPOSED BUILDING FUEL OF 497.12 AS SHOWN ON THE CIVIL DRAWINGS IS EQUAL TO 100'-0" ON ALL OTHER DOCUMENTS.
- THE CONSTRUCTION SHALL NOT RESTRICT A FIVE-FOOT CLEAR AND UNOBSTRUCTED ACCESS TO ANY WATER OR POWER FACILITIES POWER POLES, PULL-BOXES, TRANSFORMERS, VAULTS, PUMPS, VALVES, METERS, APPURTENANCES, ETC.) OR TO THE LOCATION OF HOOD-UP. THE CONSTRUCTION SHALL NOT BE WITHIN TEN FEET OF ANY POWER LINES - WHETHER OR NOT THE LINES ARE LOCATED ON THE PROPERTY. FAILURE TO COMPLY MAY CAUSE CONSTRUCTION DELAYS AND/OR ADDITIONAL EXPENSES.
- CONTRACTOR SHALL SCHEDULE A FIRESTOPPING PRE-INSTALLATION MEETING WITH THE SUB-CONTRACTORS AND BUILDING INSPECTOR.
- CONTRACTOR SHALL PROVIDE LIST OF THE FIRESTOP MATERIALS/ASSEMBLIES TO BE USED, THEIR RESPECTIVE PENETRATION TYPES/LOCATIONS, AND UL AND/OR ICC REPORT/SUSTAINING NUMBERS TO THE BUILDING INSPECTOR FOR REVIEW AND APPROVAL.
- SMOKE AND FIRE DAMPERS SHALL BE INSTALLED PER 2014 OSSC SECTION 717.
- MECHANICAL EXHAUST OF BATHROOMS AND LAUNDRY FACILITIES IS REQUIRED. AIR CHANGES AND DISTANCE OF DISCHARGE FROM OPERABLE OPENINGS SHALL BE COMPLIANT WITH OSSC 2014 SECTION 1203.
- AN APPROVED GAS SHUT-OFF VALVE SHALL BE INSTALLED ON THE FUEL GAS LINE ON THE DOWNSTREAM SIDE OF THE UTILITY METER AND BE RIGIDLY CONNECTED TO THE EXTERIOR OF THE BUILDING OR STRUCTURE CONTAINING THE FUEL GAS PIPING.
- THIS BUILDING MUST BE EQUIPPED WITH AN AUTOMATIC FIRE EXTINGUISHING SYSTEM COMPLYING WITH NFPA-13.
- SPRINKLER SYSTEMS ARE TO BE APPROVED BY THE FIRE MARSHAL'S OFFICE PRIOR TO INSTALLATION.
- REFERENCE SPECIFICATION SECTION 01 31 16 FOR ADDITIONAL INFORMATION. FIRE SPRINKLER AND FIRE ALARM SYSTEMS PERMITTED SEPARATELY.
- SEE SHEET S002 FOR ALL REQUIRED SPECIAL INSPECTIONS.
- ANTI-GRAFFITI COATINGS ARE REQUIRED AT THE GROUND LEVEL WHERE CONCRETE OR MASONRY FINISHES ARE USED. REFERENCE THE SPECIFICATION SECTION 07 19 00.

SHEET INDEX

Sheet Number	Sheet Name	SD	DD	PERMIT	GMP	Issue 5	Issue 6
GENERAL							
G001	COVER SHEET						
G002	GENERAL INFORMATION						
G003	CODE COMPLIANCE SUMMARY						
G004	CODE COMPLIANCE						
G005	CODE COMPLIANCE						
G006	APPEALS AND CODE DIAGRAMS						
G301	CODE - ELEVATIONS						
G801	ACCESSIBILITY DIAGRAMS						
G802	ACCESSIBILITY DIAGRAMS						
CIVIL							
C200	CIVIL NOTES						
C250	DEMOLITION & EROSION CONTROL PLAN						
C100	GRADING AND PAVING PLAN						
C200	UTILITY PLAN						
C300	CIVIL DETAILS						
C400	PWP - COVER SHEET						
C401	PWP - TYP STREET SECTIONS						
C402	PWP - SW CAPITOL HWY PLAN AND PROFILE						
C403	PWP - SW 32ND AVE PLAN AND PROFILE						
C404	PWP - ENLARGED PLAN AND PROFILE						
C405	PWP - ENLARGED PLAN AND PROFILE						
C406	PWP - STANDARD DETAILS						
C407	PWP - STANDARD DETAILS						
C408	PWP - EROSION CONTROL PLAN						
LANDSCAPE							
L101	LANDSCAPE PLAN						
L104	LEVEL 4 LANDSCAPE PLAN						
L201	CONSTRUCTION DETAILS						
L202	PLANTING DETAILS						
L301	IRRIGATION PLAN						
L304	LEVEL 4 IRRIGATION PLAN						
L401	IRRIGATION DETAILS						
ARCHITECTURE							
A001	HORIZONTAL ASSEMBLIES						
A002	VERTICAL INTERIOR ASSEMBLIES, METAL-CONC						
A003	VERTICAL INTERIOR ASSEMBLIES - WOOD						
A004	VERTICAL ASSEMBLIES - EXTERIOR						
A021	TYPICAL RATED CONDITIONS						

SHEET INDEX

Sheet Number	Sheet Name	SD	DD	PERMIT	GMP	Issue 5	Issue 6
A000	EXISTING CONDITIONS						
A001	SITE PLAN						
A101	FLOOR PLAN - LEVEL 1						
A101S	SLAB PLAN - LEVEL 1						
A102	FLOOR PLAN - LEVEL 2						
A102S	SLAB PLAN - LEVEL 2						
A103	FLOOR PLAN - LEVEL 3						
A104	FLOOR PLAN - LEVEL 4						
A105	ROOF PLAN						
A151A	ENLARGED PLAN						
A151B	ENLARGED PLAN						
A152A	ENLARGED PLAN						
A152B	ENLARGED PLAN						
A153A	ENLARGED PLAN						
A153B	ENLARGED PLAN						
A154A	ENLARGED PLAN						
A154B	ENLARGED PLAN						
A201	REFLECTED CEILING PLAN - LEVEL 1						
A202	REFLECTED CEILING PLAN - LEVEL 2						
A203	REFLECTED CEILING PLAN - LEVEL 3						
A204	REFLECTED CEILING PLAN - LEVEL 4						
A301	BUILDING ELEVATIONS						
A401	BUILDING SECTIONS						
A451	WALL SECTIONS						
A452	WALL SECTIONS						
A453	WALL SECTIONS						
A501	VERTICAL CIRCULATION - ELEVATOR						
A502	VERTICAL CIRCULATION - NORTH STAIR						
A503	VERTICAL CIRCULATION - DETAILS						
A601	INTERIOR ELEVATIONS						
A602	INTERIOR ELEVATIONS - KITCHENS						
A601	INTERIOR ELEVATIONS - BATHROOMS						
A701	EXTERIOR DETAILS - GRADE						
A702	EXTERIOR DETAILS - GRADE						
A705	EXTERIOR DETAILS - BRICK & MISC						
A710	EXTERIOR DETAILS - STOREFRONT						
A711	EXTERIOR DETAILS - STOREFRONT						
A712	EXTERIOR DETAILS - ROUNDED CORNER						
A713	EXTERIOR DETAILS - CANOPES						
A714	EXTERIOR DETAILS - SOFFIT						
A716	EXTERIOR DETAILS - STUCCO						
A720	EXTERIOR DETAILS - VINYL WINDOWS						
A722	EXTERIOR DETAILS - PTHP						
A740	EXTERIOR DETAILS - ROOF						
A741	EXTERIOR DETAILS - ROOF						
A742	EXTERIOR DETAILS - ROOF TERRACE						
A743	EXTERIOR DETAILS - ROOF TERRACE						
A750	WINDOW WRAP SEQUENCE						
A751	PROJECT MOCKUP						
A801	INTERIOR DETAILS - FLOOR TRANSITIONS						
A802	INTERIOR DETAILS - UNIT CASEWORK						
A803	INTERIOR DETAILS - LOBBY & UNIT						
A804	INTERIOR DETAILS - WALLS & CEILINGS						
A805	INTERIOR DETAILS - DOORS						
A901	WINDOW SCHEDULE						
A902	DOOR AND OPENING SCHEDULES						
A921	ROOM FINISH SCHEDULE						

S000	COVER SHEET						
S001	GENERAL STRUCTURAL NOTES						
S001B	GENERAL STRUCTURAL NOTES						
S002	SPECIAL INSPECTION						
S003	SCHEDULES						
S101	FOUNDATION PLAN						
S102A	2ND FLOOR TENDON PLAN						
S102B	2ND FLOOR REBAR PLAN						
S102C	2ND FLOOR SHEAR WALLS						
S103	3RD FLOOR FRAMING PLAN						
S104	4TH FLOOR FRAMING PLAN						
S105	ROOF FRAMING PLAN						
S301	VERTICAL CIRCULATION						
S302	STAIR DETAILS						
S303	ELEVATOR SECTION, PLANS & DETAILS						
S304	EXTERIOR BUILDING ELEVATIONS						
S400	CANOPY PLAN						
S401	CANOPY DETAILS						
S501	FOUNDATION DETAILS						
S502	FOUNDATION DETAILS						
S601	PT PODIUM DETAILS						
S602	PT PODIUM DETAILS						
S603	PT PODIUM DETAILS						
S611	FLOOR FRAMING DETAILS						
S612	FLOOR FRAMING DETAILS						
S701	ROOF FRAMING DETAILS						
S801	STANDARD SHEAR WALL DETAILS						

M101	HVAC PLAN - LEVEL 1						
M102	HVAC PLAN - LEVEL 2						
M103	HVAC PLAN - LEVEL 3						
M104	HVAC PLAN - LEVEL 4						
M105	HVAC PLAN - LEVEL 5						
M800	HVAC SCHEDULES						
M801	HVAC DETAILS						
M802	HVAC DETAILS						

P001	PLUMBING LEGEND AND SCHEDULES						
P002	PLUMBING WATER DIAGRAMS						
P003	PLUMBING WASTEVENT DIAGRAMS						
P100	PLUMBING FLOOR PLAN - BELOW SLAB						
P101	PLUMBING FLOOR PLAN - LEVEL 1						
P102	PLUMBING FLOOR PLAN - LEVEL 2						
P103	PLUMBING FLOOR PLAN - LEVEL 3						
P104	PLUMBING FLOOR PLAN - LEVEL 4						
P105	PLUMBING FLOOR PLAN - LEVEL 5						
G100	GAS SCHEDULES						
G101	GAS - LEVEL 1						
G102	GAS - LEVEL 2						
G103	GAS - LEVEL 3						
G104	GAS - LEVEL 4						
G105	GAS - LEVEL 5						

E001	COVER SHEET - ELECTRICAL						
E001	SITE PLAN - ELECTRICAL						
E101	LEVEL 1 FLOOR PLAN - POWER						
E102	LEVEL 2 FLOOR PLAN - POWER						
E103	LEVEL 3 FLOOR PLAN - POWER						
E104	LEVEL 4 FLOOR PLAN - POWER						
E105	LEVEL 5 FLOOR PLAN - POWER						
E301	DETAILS - ELECTRICAL						
E401	ENLARGED UNIT PLANS - ELECTRICAL						
E402	ENLARGED UNIT PLANS - ELECTRICAL						
E403	ENLARGED UNIT PLANS - ELECTRICAL						
E501	ONE-LINE DIAGRAM - ELECTRICAL						
E502	SCHEDULES - ELECTRICAL						
E503	CALCULATIONS - ELECTRICAL						

T001	COVER SHEET - TECHNOLOGY						
T101	LEVEL 1 - TECHNOLOGY						
T102	LEVEL 2 - TECHNOLOGY						
T103	LEVEL 3 - TECHNOLOGY						
T104	LEVEL 4 - TECHNOLOGY						
T601	DIAGRAM - TECHNOLOGY						

FIRE PROTECTION							
FP001	SITE PLAN			■	■		
FP002	FIRST AND SECOND FLOOR PLANS			■	■		
FP003	THIRD AND FOURTH FLOOR PLANS			■	■		
FP004	ATTIC AND SECTION			■	■		