


Drawings and Specifications as Instruments of service are and shall remain the property of the Architect. They are not to be used on extensions of the project or other projects, except by agreement in writing and appropriate compensation to the Architect. The General Contractor is responsible for confirming and correlating dimensions at the job site. The Architect will not be responsible for construction means, methods, techniques, sequences, or procedures, or for safety precautions and programs in connection with the project.

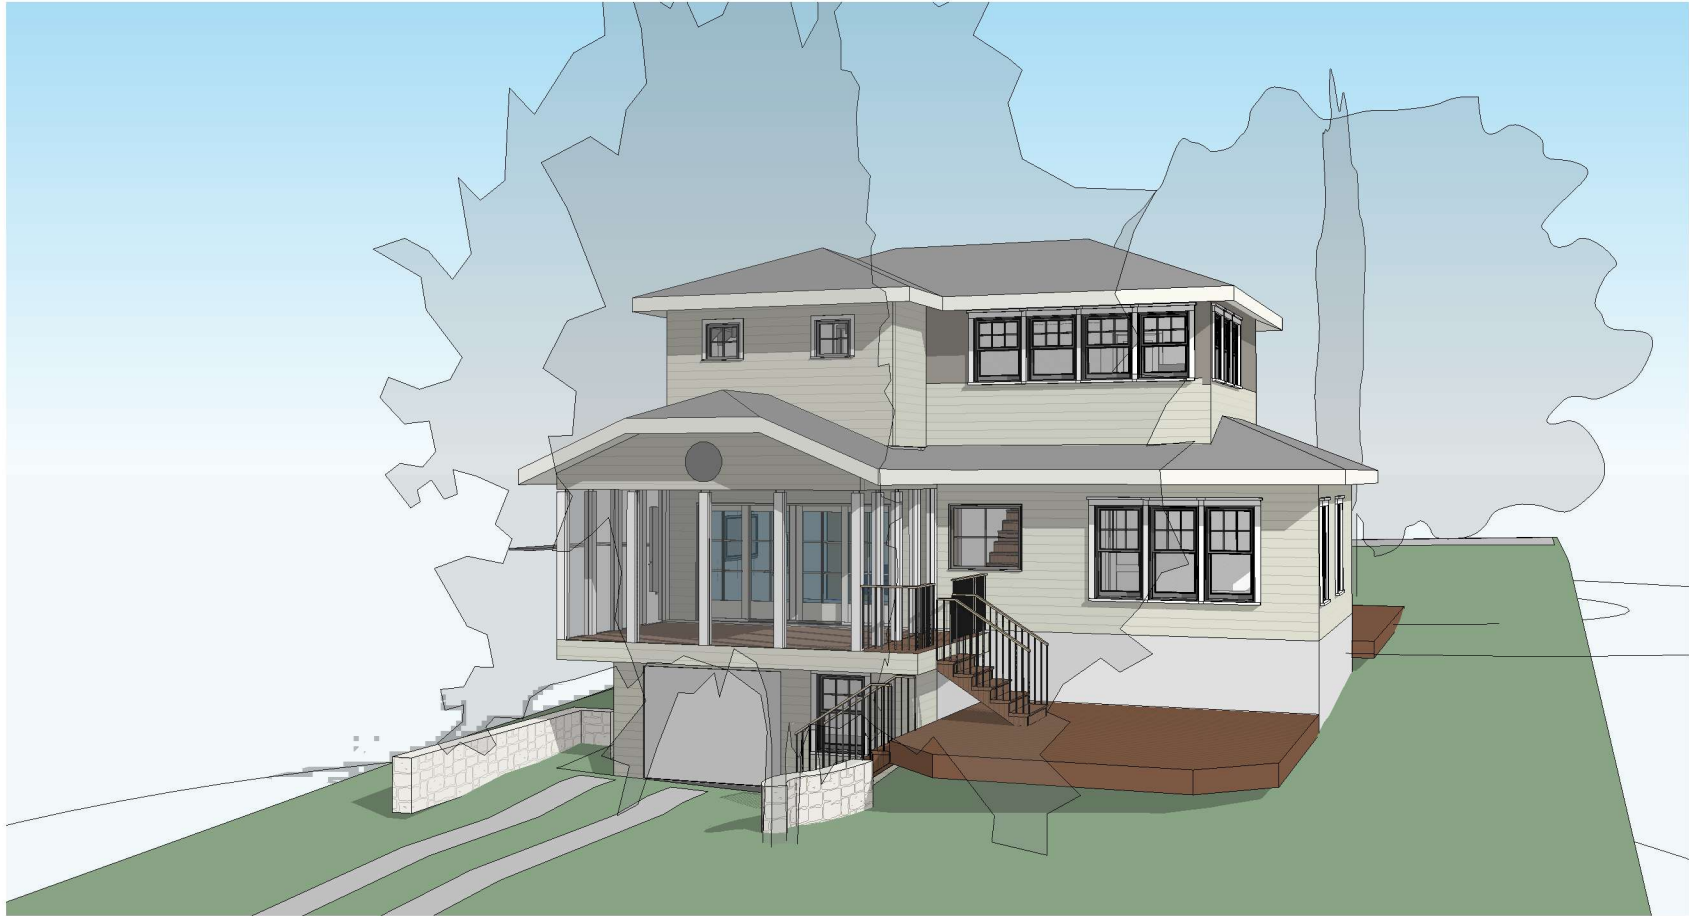


PROJECT INFORMATION

PROJECT DESCRIPTION
REMODEL AND ADDITION TO A SPLIT-LEVEL RESIDENCE IN THE CITY OF AUSTIN

LEGAL DESCRIPTION
LOT 5, BLOCK 4 OF TRAVIS HEIGHTS, A SUBDIVISION IN AUSTIN, TEXAS, ACCORDING TO THE MAP OR PLAT THEREOF RECORDED IN VOLUME 3 PAGE 15 OF THE PLAT RECORD OF TRAVIS COUNTY, TEXAS. (TCAD PARCEL #282923)

ZONING
SF-3-NP - SINGLE-FAMILY RESIDENTIAL
RESIDENTIAL DESIGN STANDARDS (MCMANSION)
SOUTH RIVER CITY NEIGHBORHOOD PLANNING AREA

VICINITY MAP

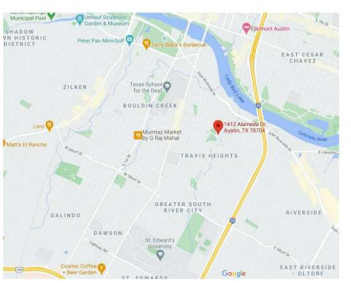

GENERAL PROJECT NOTES

PERFORM ALL WORK IN ACCORDANCE WITH THE CITY OF AUSTIN CODES, REGULATIONS & ORDINANCES

DO NOT SCALE DRAWING, CONTACT ARCHITECT UPON DISCOVERY OF MISSING INFORMATION OR CONFLICTS IN DRAWINGS

STRUCTURAL ENGINEERING FOR ALL PARTS OF THIS PROJECT TO BE DESIGNED BY OTHERS

MECH, ELEC, PLUMB & FIRE ENGINEERING TO BE PROVIDED BY OTHERS, MAY REQUIRE COORDINATION WITH ARCHITECT

VERIFY EXISTING CONDITIONS AND DIMENSIONS PRIOR TO CONSTRUCTION START

FIRE PROTECTION

THIS PROJECT DOES NOT EXCEED 3,600 SF AND THEREFORE IS NOT REQUIRED TO BE REVIEWED BY THE FIRE DEPARTMENT

CONTACTS

CLIENT
BEN & ANNA HALLMARK

ARCHITECT
CVMA
CONTACT: CAROLYN VAN METER
E-MAIL: CAROLYN@CVMARCHITECTURE.COM
PHONE: 512.740.8595

CONTRACTOR:
-NAME:
CONTACT:
E-MAIL:
PHONE:

STRUCTURAL ENGINEER:
STEINMAN LUEVANO STRUCTURES
CONTACT: DREW CAVE
E-MAIL: DREW@SLSTRUCTURES.COM
PHONE: 512.891.6766

INTERIOR DESIGNER:
-NAME:
CONTACT:
E-MAIL:
PHONE:

SYMBOLS LEGEND

- 1 View Name**
1/8" = 1'-0"
- DRAWING TITLE
DRAWING NUMBER
- Room name**
??? CLG.
??? FLOOR
- ROOM NAME
- CEILING HEIGHT
- FLOOR MATERIAL
- ELEVATION MARKER**
- BUILDING SECTION MARKER**
- WALL SECT./DETAIL MARKER**
- LEVEL MARKER**
- KEY NOTE**
- DOOR NUMBER**
- WINDOW KEY**
- CENTERLINE**
- REVISION NUMBER**
- FLOOR DROP**
- NORTH ARROW**

DRAWING INDEX

- ARCHITECTURAL**
- A0.0 COVER SHEET
 - A1.1 SITE PLAN AND AREA CALCULATIONS
 - A1.2 DEMOLITION PLAN
 - A1.3 DEMOLITION ELEVATIONS
 - A2.1 LEVEL 1 PLAN
 - A2.2 LEVEL 2 PLAN
 - A2.3 ROOF PLAN
 - A4.1 EXTERIOR ELEVATIONS
 - A4.2 EXTERIOR ELEVATIONS
- STRUCTURAL**
- S1 FOUNDATION PLAN
 - S2 FIRST FLOOR CEILING FRAMING AND SECOND FLOOR FRAMING PLAN
 - S3 ROOF FRAMING PLAN AND SECOND FLOOR CEILING PLAN
 - S4 DETAILS
 - S5 BRACE WALL PLANS
 - S6 NOTES

CVMA
Carolyn Van Meter Architecture
carolyn@cvmarchitecture.com
c. 512.740.8595

REGISTERED ARCHITECT
CAROLYN VAN METER
24997
STATE OF TEXAS

HALLMARK RESIDENCE

1412 ALAMEDA DR.
AUSTIN, TEXAS 78704

ISSUE DATES:

PERMIT SET 7.20.21
REV. PERMIT SET 10.13.21

A0.0
COVER SHEET