



6/28/2023
3:51:13 PM

WEST 10TH - PERMIT SET

1505 WEST 10TH STREET, AUSTIN, TX 78703

INDEX OF DRAWINGS

ARCHITECTURAL	
A0.1	TREE PROTECTION PLAN
A0.2	SITE PLAN
A1.1	FLOOR PLANS
A1.2	FLOOR PLANS
A1.3	FLOOR PLANS
A1.4	FLOOR PLANS
A2.1	EXTERIOR ELEVATIONS
A2.2	EXTERIOR ELEVATIONS
A2.3	EXTERIOR ELEVATIONS
A3.1	BUILDING SECTIONS
A3.2	BUILDING SECTIONS
A3.3	BUILDING SECTIONS
A6.0	SCHEDULES

STRUCTURAL	
S0	PROJECT COVER SHEET
S0.0	GENERAL NOTES
S0.1	WOOD FRAMING NOTES
S0.2	FASTENERS SCHEDULE
S1.0	FOUNDATION PLAN 1
S1.1	FOUNDATION PLAN 2
S2.0	1ST LEVEL CEILING FRAMING PLAN
S2.1	2ND LEVEL FLOOR FRAMING PLAN
S2.2	2ND LEVEL CEILING FRAMING PLAN
S2.3	ATTIC LEVEL FLOOR FRAMING PLAN
S2.4	ATTIC LEVEL CEILING FRAMING PLAN
S2.5	MAIN HOUSE LOWER ROOF FRAMING PLAN
S2.6	MAIN HOUSE HIGHER ROOF FRAMING PLAN
S2.7	LOFT FRONT HOUSE FRAMING PLAN
S2.8	LOFT & CARPORT LOWER ROOF FRAMING PLAN
S2.9	LOFT HIGHER ROOF FRAMING PLAN
S3.0	1ST LEVEL BRACING PLAN
S3.1	2ND LEVEL BRACING PLAN
S3.2	ATTIC LEVEL BRACING PLAN
S3.3	FRONT HOUSE BRACING PLAN
S4.0	FOUNDATION DETAILS
S4.1	FOUNDATION DETAILS
S4.2	FOUNDATION DETAILS
S4.10	FOUNDATION DETAILS
S4.11	FOUNDATION DETAILS
S5.0	FRAMING DETAILS
S5.1	FRAMING DETAILS
S5.2	FRAMING DETAILS
S5.3	FRAMING DETAILS
S5.4	FRAMING DETAILS
S5.5	FRAMING DETAILS
S5.6	FRAMING DETAILS
S5.7	FRAMING DETAILS
S5.8	FRAMING DETAILS
S6.0	STANDARD FRAMING DETAILS
S6.1	STANDARD FRAMING DETAILS
S6.2	STANDARD FRAMING DETAILS



OWNER INFORMATION

CODY MITCHELL & DANIELLA BUSTILLOS
1505 WEST 10TH ST, AUSTIN, TX 78703

CONTACTS

ARCHITECT: SIDE ANGLE SIDE
470 RED BLUFF ROAD
AUSTIN, TEXAS 78702
CONTACT: ANNIE LAURIE GRABIEL
PHONE: (305) 904-9318 or (305) 450-0806

CODE ANALYSIS

BUILDING CODE:	INTERNATIONAL RESIDENTIAL BUILDING CODE 2021, WITH AUSTIN AMENDMENTS WUI (WILDLAND URBAN INTERFACE CODE)
BUILDING DESCRIPTION:	3 STORY SLAB ON GRADE (W/ STUCCO)
LEGAL JURISDICTION:	CITY OF AUSTIN, TEXAS; TRAVIS COUNTY

LEGAL DESCRIPTION

BEING A 0.336 ACRE PORTION OF A TRACT OF LAND CALLED 189.5' 225' OUT OF OUTLOT 4, DIVISION Z, ORIGINAL CITY OF AUSTIN, SAME BEING THAT CERTAIN TRACT OF LAND CONVEYED BY DEED TO SAM LINCOLN ARCHER, AS RECORDED IN VOL. 410428 PG. 233, DEED RECORDS, TRAVIS COUNTY, TEXAS.


SITE INFORMATION

SITE INFORMATION GATHERED FROM SURVEY PERFORMED BY ALL POINTS SURVEYING ON 11/10/2022.

ZONING INFORMATION

ZONING:	SF-3 NP
FUTURE LAND USE:	SF-3 NP
PROPERTY ID:	X
LEGAL DESCRIPTION:	BEING A 0.336 ACRE PORTION OF A TRACT OF LAND CALLED 189.5' 225' OUT OF OUTLOT 4, DIVISION Z, ORIGINAL CITY OF AUSTIN, SAME BEING THAT CERTAIN TRACT OF LAND CONVEYED BY DEED TO SAM LINCOLN ARCHER, AS RECORDED IN VOL. 410428 PG. 233, DEED RECORDS, TRAVIS COUNTY, TEXAS.
DATE BUILT:	1987
NEIGHBORHOOD:	CLARKSVILLE
NEIGHBORHOOD PLAN:	OLD WEST AUSTIN NEIGHBORHOOD (OWANA)
TOD:	N/A
OVERLAY DISTRICT:	N/A
FLOODPLAIN:	N/A
WATERSHED:	N/A
EASEMENTS:	7'-6" P.U.E. AT REAR OF PROPERTY
DEED RESTRICTIONS:	YES
OPEN/EXP'D PERMITS:	NONE
PROTECTED TREES:	YES (6)
MCMASSON:	YES
COMPATIBILITY STANDARDS:	COM. AMENDMENTS
MINIMUM SETBACKS:	FRONT: 20' INTERIOR SIDE: 5' REAR: 10' (5' ALLEY)
MAX. BLDG. HEIGHT:	35'
LOT SIZE:	14,636 SF (0.336 ACRE) PER SURVEY
MAX BLDG. COVERAGE:	5,854.4 SF (40%)
MAX IMPROVISED COVER:	6,586.2 SF (45%)
MAX F.A.R.:	5,854.4 SF (40%)
PARKING:	PER BUILDING USE PROPOSED (CODE: 25-6 ZONING/TRANSPORTATION/APPENDIX A)

VICINITY MAP

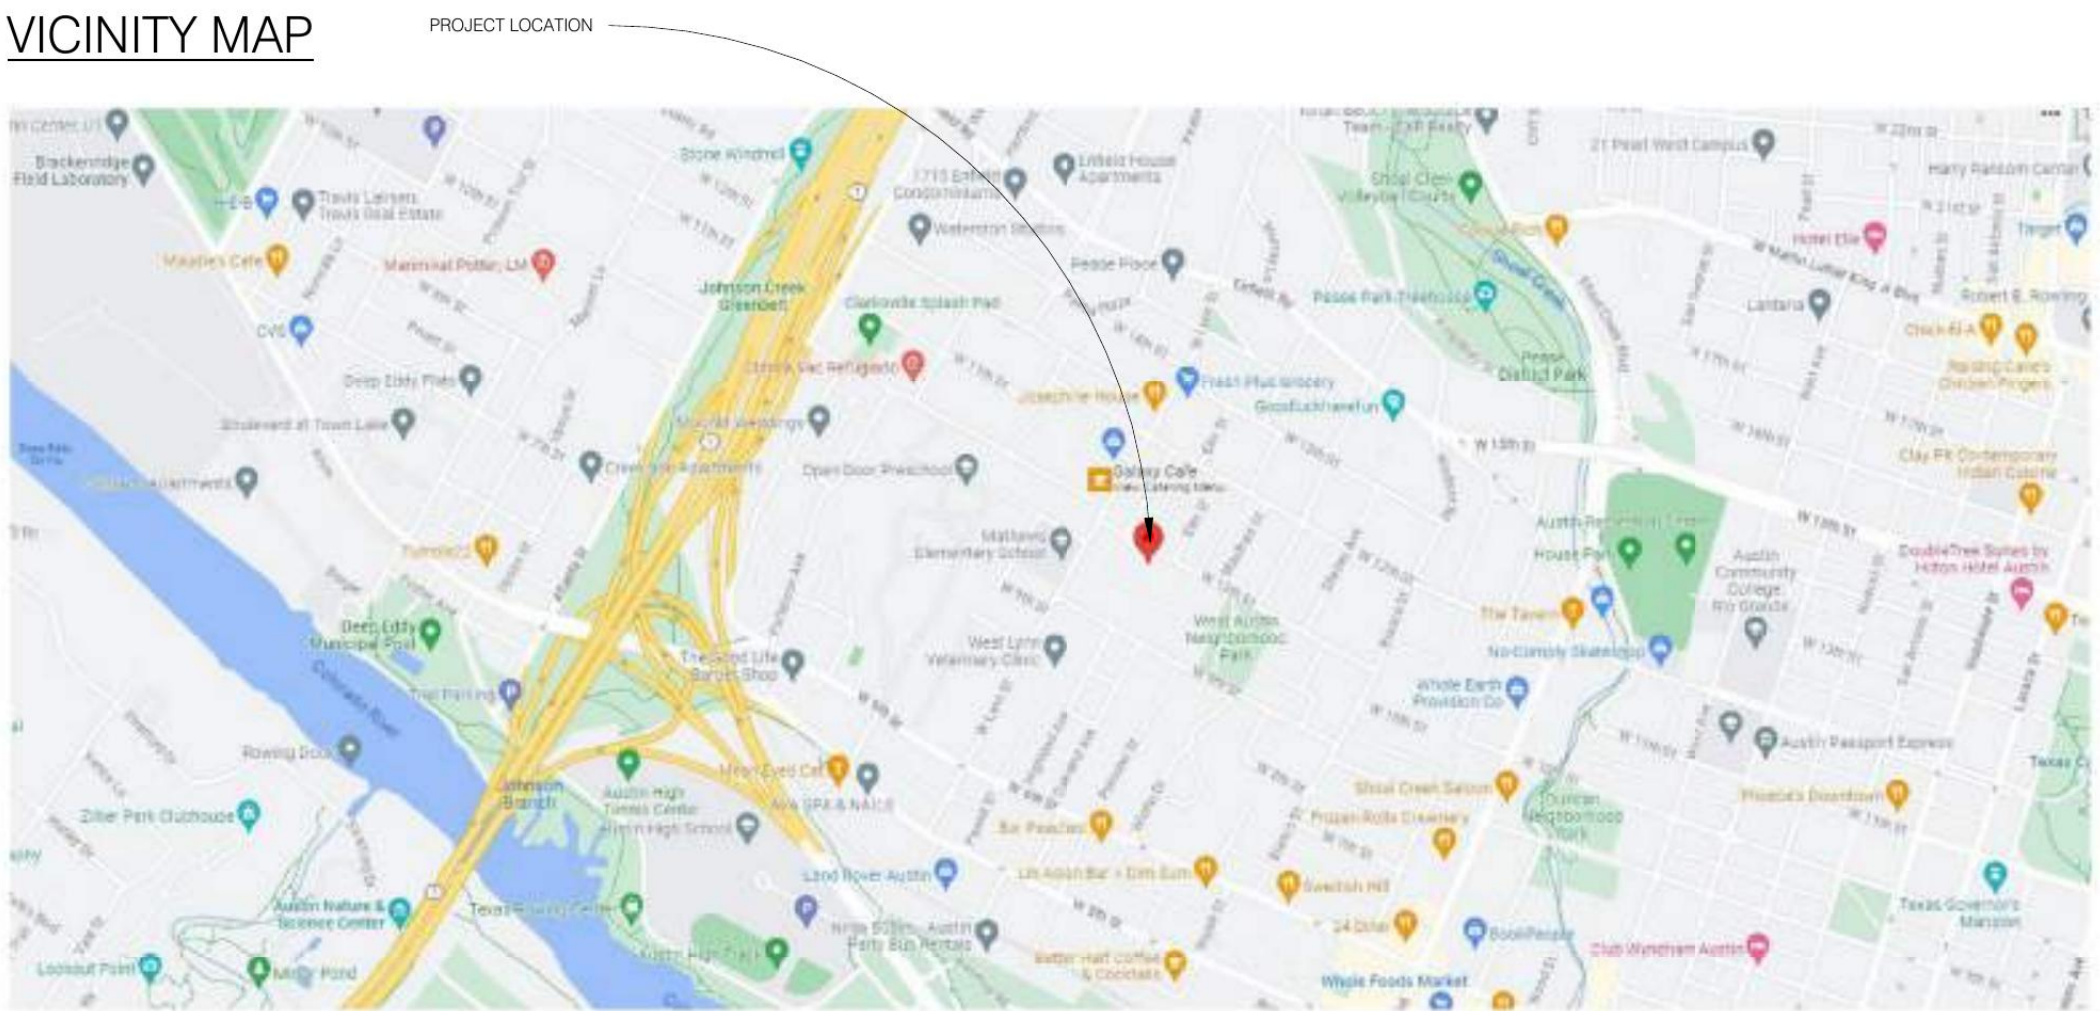

TAKEN FROM GOOGLE MAPS

SYMBOL LEGEND

	EXTERIOR ELEVATION SYMBOL
	INTERIOR ELEVATION SYMBOL
	SECTION DETAIL SYMBOL
	SECTION SYMBOL
	PARTITION TYPE SYMBOL
	ROOM ID TAG
	DETAIL SYMBOL
	DOOR ID TAG
	WINDOW ID TAG

WEST 10TH

1505 WEST 10TH ST, AUSTIN, TX 78703