



Harthan Street
2005

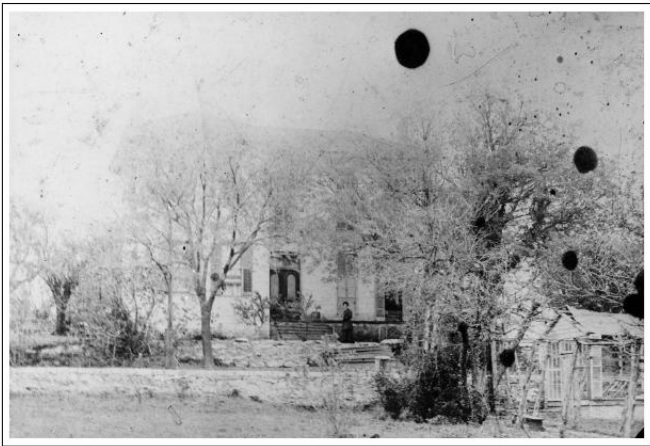

19th Century view, undated, A. J. Jernigan House. The house was built in 1875. The view is looking north, towards the south elevation of the house. PICH 01952, Austin History Center, Austin Public Library.



20th Century view, about 1975, A. J. Jernigan House/Las Ventanas. The view is looking west, towards the east elevation of the house. A portion of a late 1880's masonry addition is shown on the right. The covered porch was added in 1912 along with a wood frame addition to the northwest corner, by Charles Capron, the second owner of the house. PICH 08793, Austin History Center, Austin Public Library.

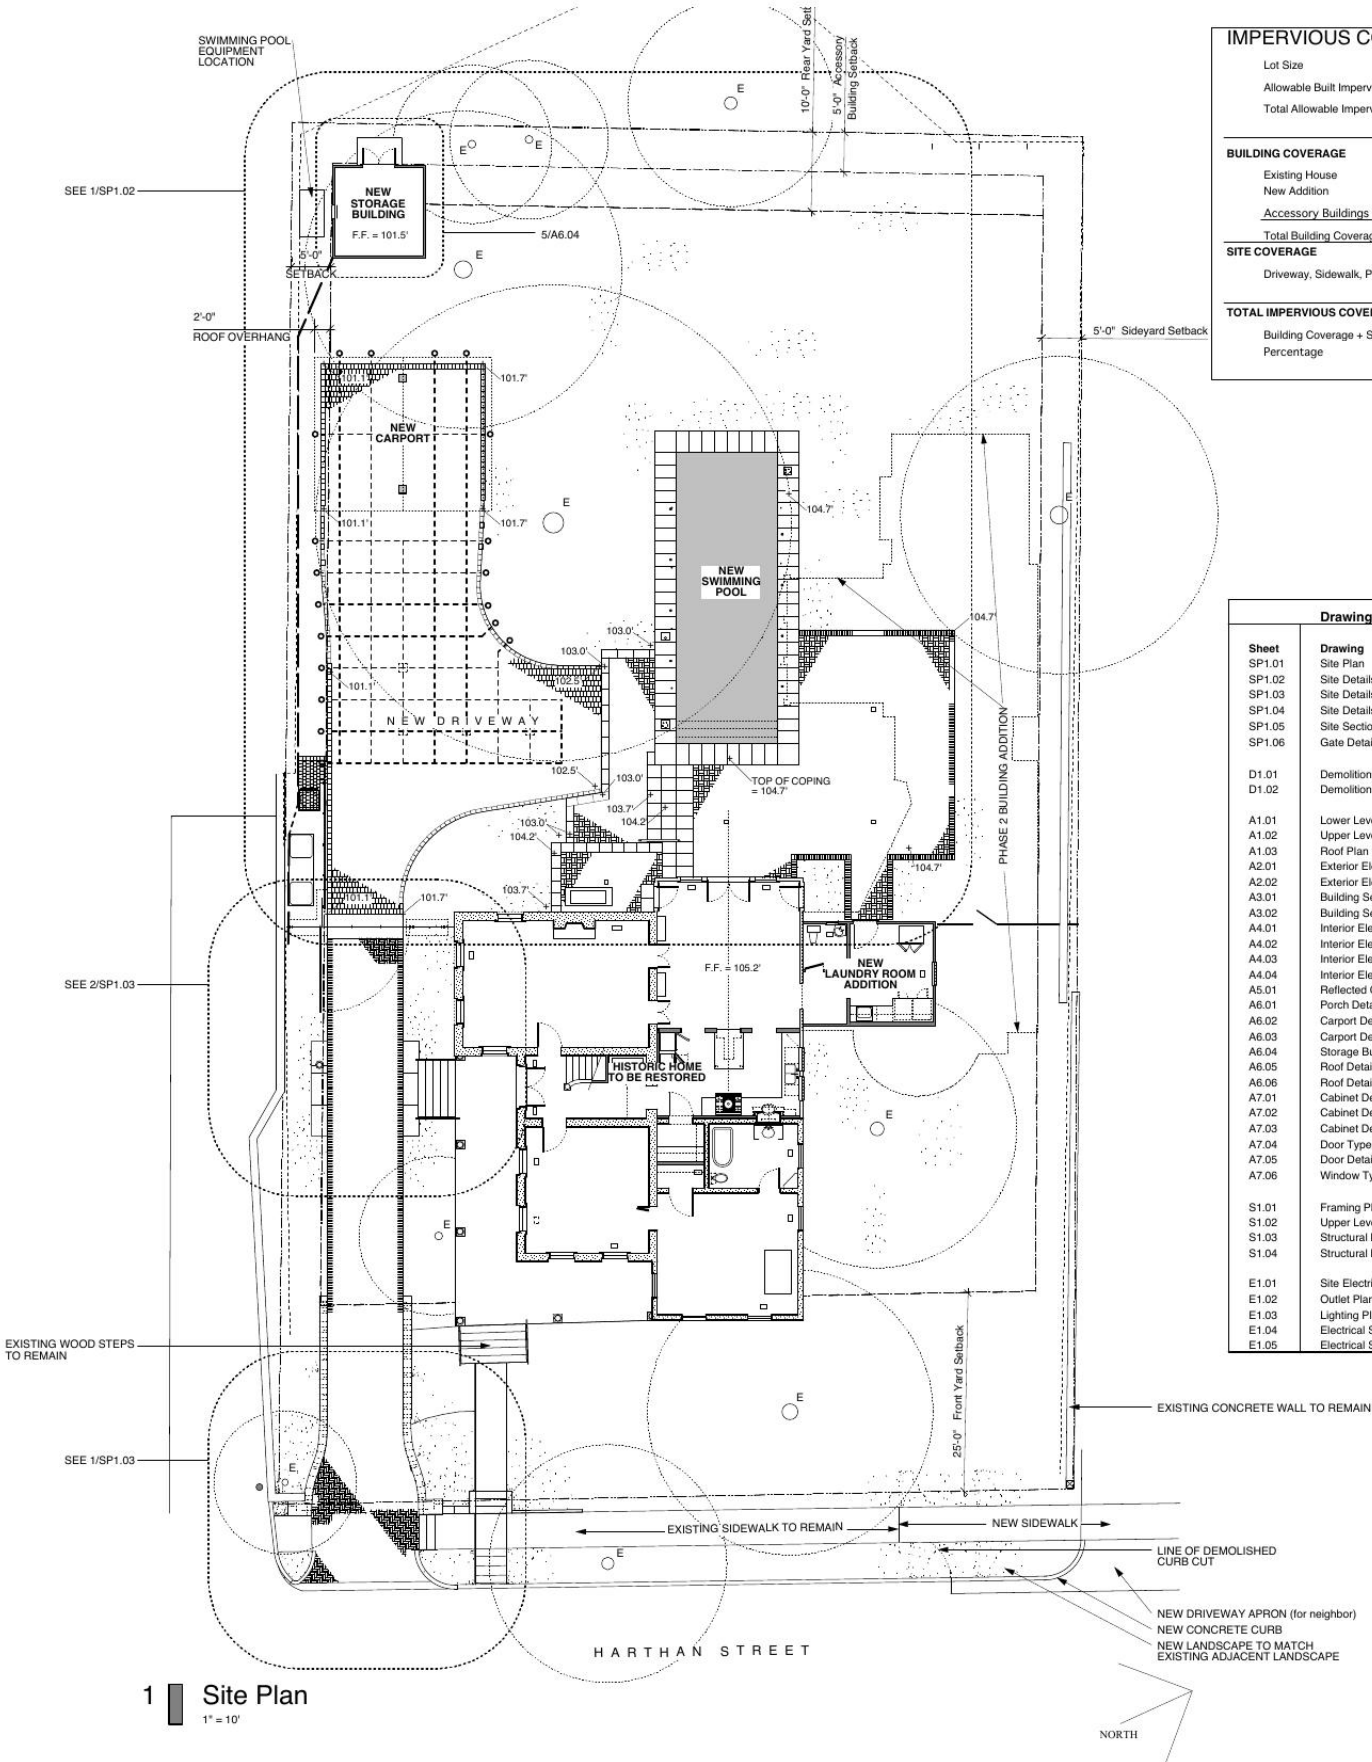

1 Site Plan
1" = 10'

IMPERVIOUS COVER	
Lot Size	17,224 sq. ft.
Allowable Built Impervious Cover (50%)	8,612
Total Allowable Impervious Cover (55%)	9,473

BUILDING COVERAGE	
Existing House	2338 sq. ft.
New Addition	206
Accessory Buildings	200
Total Building Coverage on Lot	2744 sq. ft.

SITE COVERAGE	
Driveway, Sidewalk, Patios, Pool, Other	4600

TOTAL IMPERVIOUS COVERAGE	
Building Coverage + Site Coverage	7344 sq. ft.
Percentage	42.6 %

Drawing Index	
Sheet	Drawing
SP1.01	Site Plan
SP1.02	Site Details
SP1.03	Site Details
SP1.04	Site Details
SP1.05	Site Sections
SP1.06	Gate Details
D1.01	Demolition Site Plan
D1.02	Demolition Floor Plans
A1.01	Lower Level Plan
A1.02	Upper Level Plan
A1.03	Roof Plan
A2.01	Exterior Elevations
A2.02	Exterior Elevations
A3.01	Building Section
A3.02	Building Section
A4.01	Interior Elevations
A4.02	Interior Elevations
A4.03	Interior Elevations
A4.04	Interior Elevations
A5.01	Reflected Ceiling Plans
A6.01	Porch Details
A6.02	Carport Details
A6.03	Carport Details
A6.04	Storage Building Details
A6.05	Roof Details
A6.06	Roof Details
A7.01	Cabinet Details
A7.02	Cabinet Details
A7.03	Cabinet Details
A7.04	Door Types & Schedule
A7.05	Door Details
A7.06	Window Types & Schedule
S1.01	Framing Plans
S1.02	Upper Level Floor Framing Plan
S1.03	Structural Details
S1.04	Structural Details
E1.01	Site Electrical Plan
E1.02	Outlet Plans
E1.03	Lighting Plans
E1.04	Electrical Schedule
E1.05	Electrical Schedule

Limbacher & Godfrey
Architects, Inc.
3406 Glenview Ave.
Suite 200
Austin, Texas
78703

LIMBACHER & GODFREY
ARCHITECTS

EXP. 7/31/06

Seal of the State of Texas



10/20/05

PRESERVATION AND ADDITIONS TO THE
A. J. JERNIGAN HOUSE
LAS VENTANAS
PHASE ONE
602 HARTHAN STREET AUSTIN, TEXAS 78703