


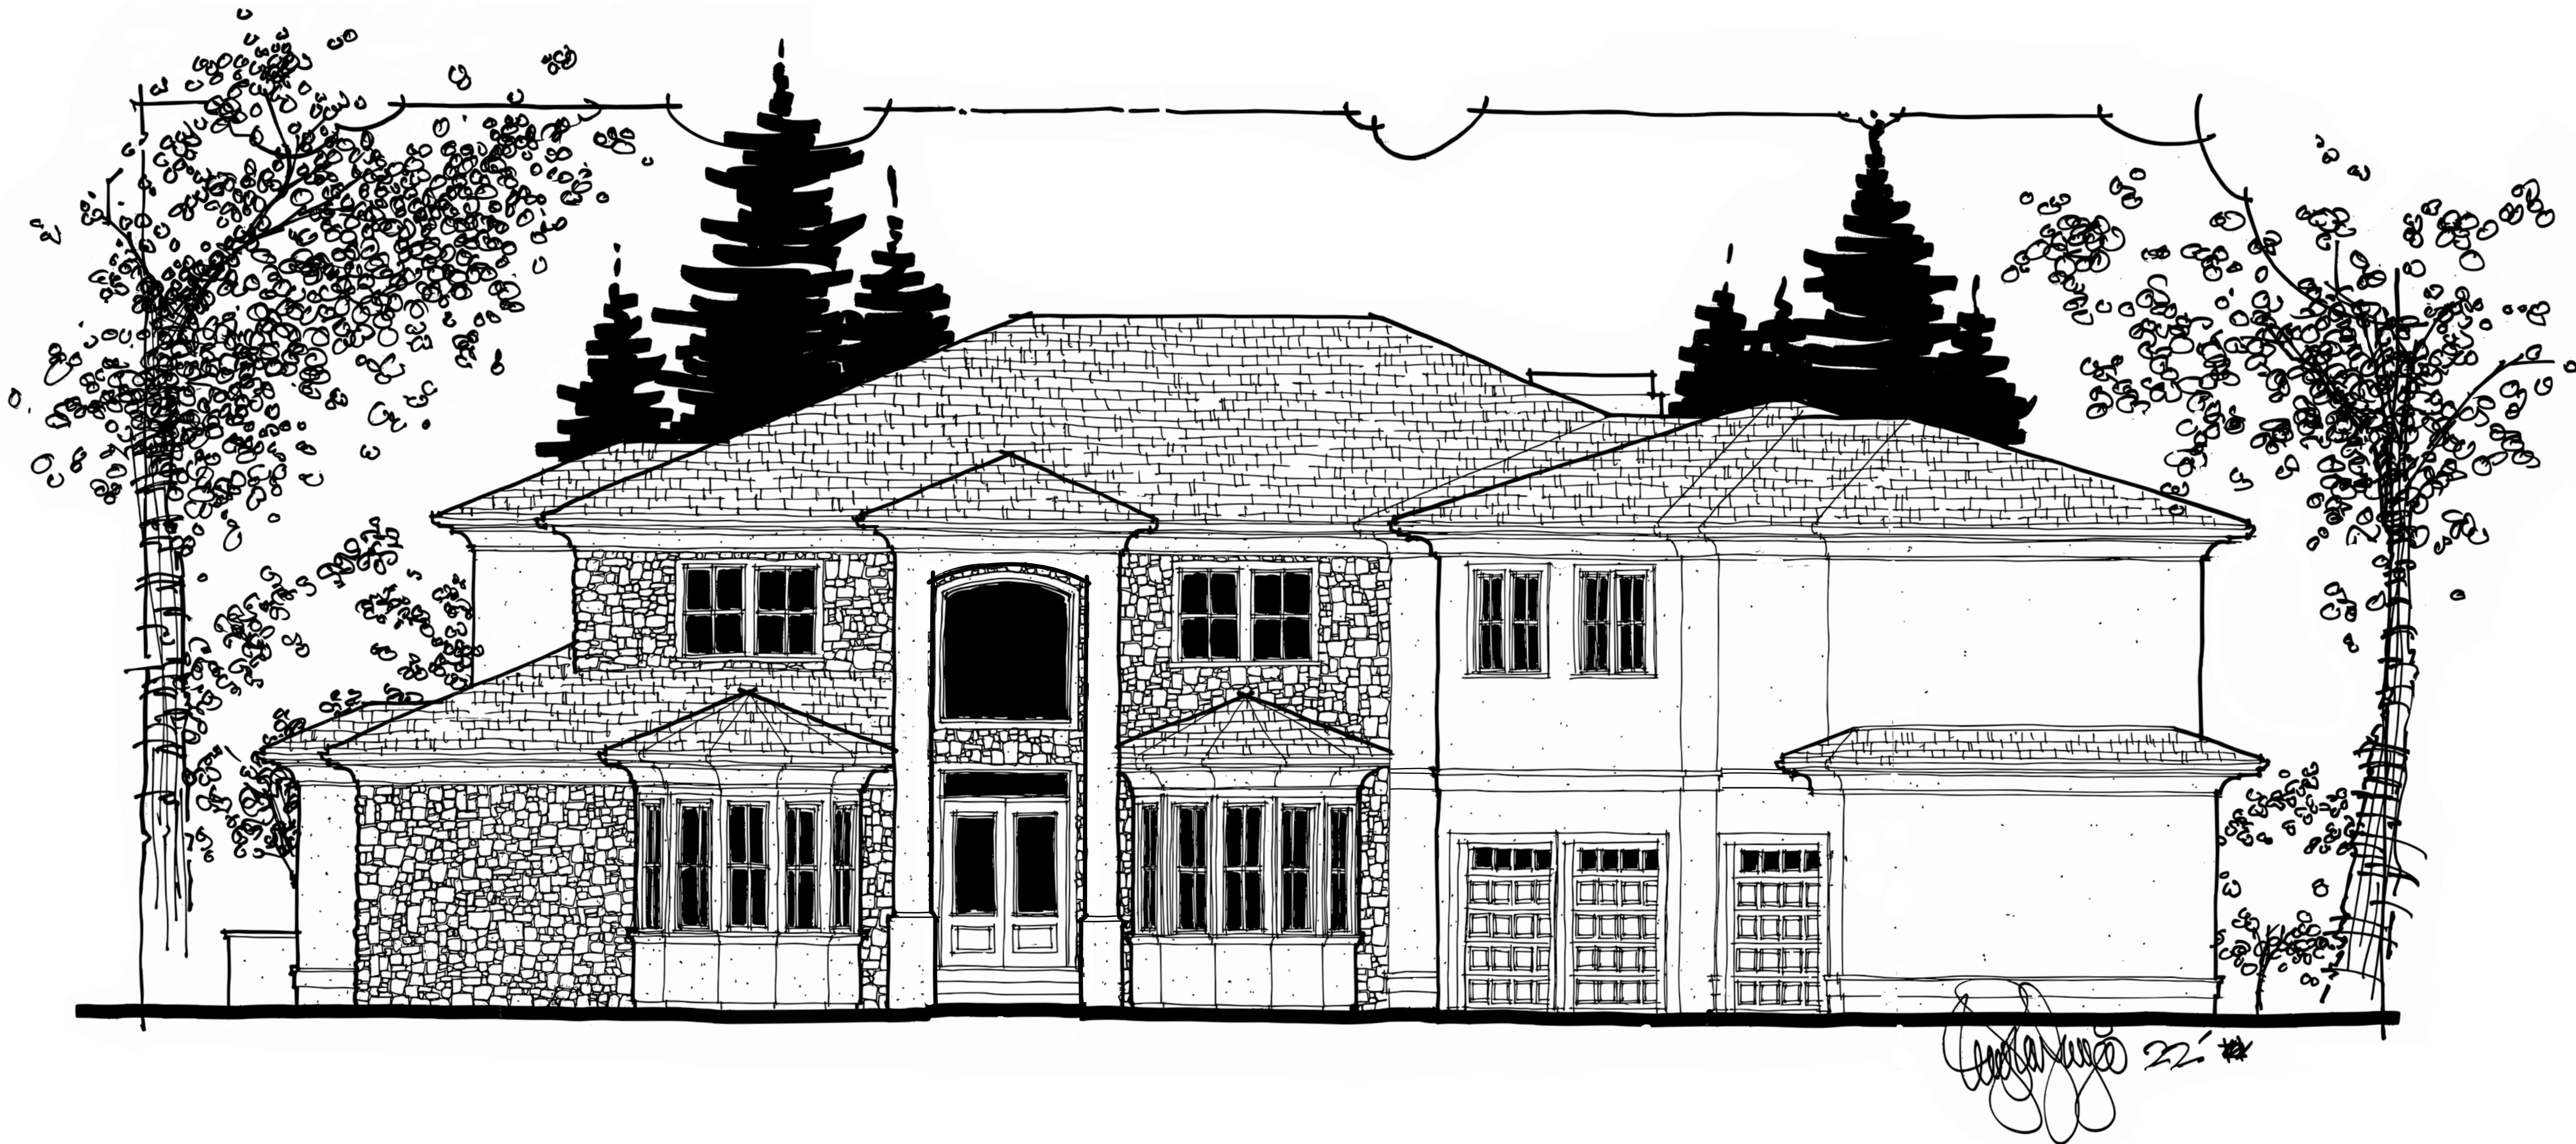

A NEW CUSTOM HOME DESIGN FOR:
MESECHER - GLOUDREAU
RESIDENCE

LOT 221, BLOCK 104, RIVERBEND, BLUFFTON TOWNSHIP, SC

PROJECT DESIGNED BY: **Myles Nelson McKenzie DESIGN**
Mailing Address: 110 Traders Cross, Suite 100
Bluffton, SC 29909
Telephone: 843-505-1031
Email: mmckenzie@mylesmckenzie.com
Website: www.mylesmckenzie.com

PROJECT OWNER: Don Mesecher / Kathrine Goudreau
Lot 221, Block 104, Riverbend
Bluffton Township, SC

PROJECT SCOPE: A new custom residence as per plan.

STRUCTURAL CONSULTANT: **Dan'l Moulton, P.E.**
10 Clayton Court
Bluffton, SC 29910
843-949-0658
dmoulton72@gmail.com

ENERGY CONSULTANT: **Elm Energy Group, LLC**
Jamie Kaye
843-296-3715
Jamie@ElmEnergyGroup.com

GENERAL CONTRACTOR: **JD Construction**
James Duncan
843-422-1027
jdduncanconstruction@aol.com

PROJECT CODE NOTES: 2018 S.C. Residential Code
2018 S.C. Fire Code
2018 S.C. Plumbing Code
2018 S.C. Mechanical Code
2018 S.C. Fuel Gas Code
2018 S.C. Building Code Modifications
2009 S.C. Energy Code
2017 National Electrical Code

Occupancy: R1
Type: V-B
Number of stories: 2
Residence sprinklers: No
Building Department: County of Beaufort

AREA CALCULATIONS: (S.F.)	
Residence	
Conditioned Space	
First Floor Livable	3702
Second Floor Livable	3177
Total:	6879
Non-conditioned Space	
Unfinished Storage	323
Total:	323
Mechanical Rooms	39
Garage	1072
Porches	
Front Porch	120
Lower Screen-in Porch	399
Screened Spa Lanai	179

SHEET INDEX:	
No.	Description
CS	Cover Sheet
A1	Site Plan
LGP	Lot Grading Plan
A1.0	General Notes SC
A1.1	Survey
A1.2	Door & Window Schedules
A1.3	Stair Details
A2.1	First Floor Plan - Dimensional
A2.2	First Floor Plan - Notational
A3.1	Second Floor Plan - Dimensional
A3.2	Second Floor Plan - Notational
A4	Roof Plan
A5	Exterior Material Colors
A6	Exterior Elevations
A7	Exterior Elevations
A8	Building Sections
A9	Gazebo Plans
Structural	
SN1	General Structural Notes
SN2	General Structural Notes
S1	Foundation Plan
S2	Framing Plan - 2nd Floor & Lower Roof
S3	Framing Plan - Second Floor Ceiling
S4	Framing Plan - Upper Roof
D1	Foundation Details - Slab
D2	Framing Details
D3	Framing Details
Electrical	
E1	First Floor Electrical Plan
E2	Second Floor Electrical Plan
E3	Generator Documentation
Landscape	
L1	Landscape Plan
L2	Landscape Notes & Details
L3	Landscape Lighting Notes & Details



MYLES
NELSON
McKENZIE
DESIGN

Telephone: 843-683-6895
843-505-1031
Email: info@mylesmckenzie.com
Web: www.mylesmckenzie.com

These drawings, documents and specifications are an instrument of service, copyright and the property of MYLES NELSON McKENZIE DESIGN and shall not be used or reproduced in any part or whole, except by written agreement with the Architect or Designer of MYLES NELSON McKENZIE DESIGN. Their use for publication shall be restricted to the original project in which they are designed for.

Written dimensions shall be verified on the job site. Any discrepancy shall be brought to notice of the Architect or Designer of MYLES NELSON McKENZIE DESIGN prior to the commencement of any construction.

These plans have been reviewed and approved by:

A NEW CUSTOM HOME DESIGN FOR:
MESECHER - GLOUDREAU
RESIDENCE
LOT 221, BLOCK 104, RIVERBEND
BLUFFTON TOWNSHIP, SC

Project

Number Date Description

Revisions

Issue Date 5/17/20

Plot Date 5/9/22

COVER SHEET

Sheet

CS