


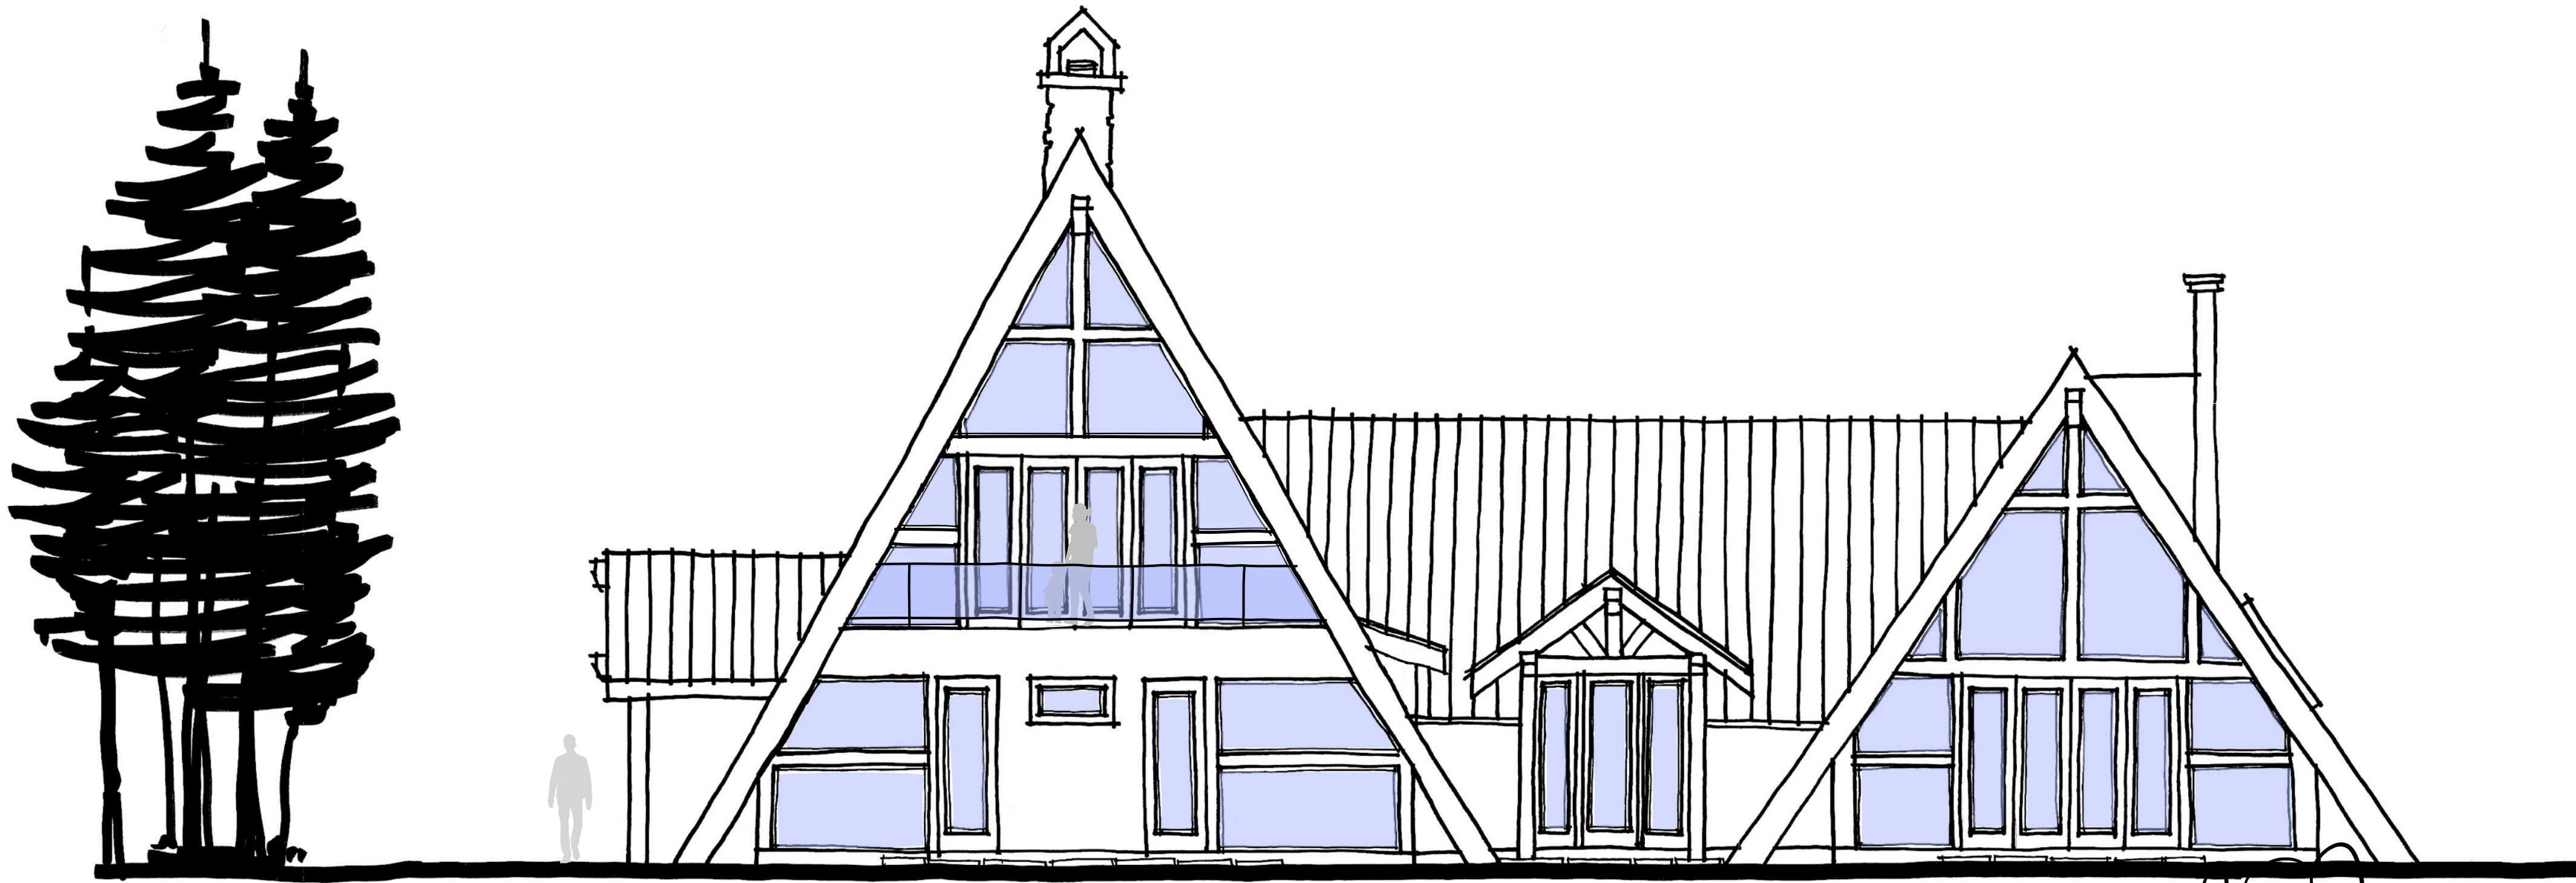

A NEW CUSTOM RESIDENCE FOR
MR. & MRS. AIVAD
183 SNOWS POINT ROAD, SAINT GEORGE, ME 04860

SHEET INDEX:

No.	Description	No.	Description
CS	Cover Sheet	Structural - General Notes	
A0.1	Project Images	GSN1	General Structural Notes
A0.2	Project Images	GSN2	General Structural Notes
A1.0	General Notes	Structural - Residence	
A1.1	Maine General Notes	S1	Foundation Plan - Residence
A1.3	Stair Details	S2	Floor Framing Plan - Residence 1st Floor
A2	Site Plan	S3	Floor Framing Plan - Residence 2nd Floor
Residence		S4	Roof Framing Plan - Residence
A3	Residence Schedules	Structural - Workshop & Studio	
A4	First Floor Plan	S5	Foundation Plan - Workshop & Studio
A5	Second Floor Plan	S6	Floor & Ceiling Framing Plan - Workshop & Studio
A6	Roof Plan	S7	Roof Framing Plan - Workshop & Studio
A7	Exterior Elevation - East	Details	
A8	Exterior Elevation - South	D1	Details
A9	Exterior Elevation - West	D2	Details
A10	Exterior Elevation - North	D3	Details
A11	Building Section	D4	Details
A12	Building Sections	Electrical - Residence	
Workshop & Studio		E1	First Floor Electrical Plan
A13	Workshop & Studio Schedules	E2	Second Floor Electrical Plan
A14	Workshop Floor Plan	Electrical - Workshop & Studio	
A15	Studio Floor Plan	E3	Workshop Electrical Plan
A16	Workshop - Studio Roof Plan	E4	Studio Electrical Plan
A17	Workshop - Studio Exterior Elevations		
A18	Workshop - Studio Exterior Elevations		
A19	Workshop - Studio Building Sections		

PROJECT DESIGNED BY:

Myles Nelson McKenzie DESIGN

Mailing Address: 110 Traders Cross, Suite 100
Bluffton, SC 29909

Telephone: 843-505-1031

Email: mmckenzie@mylesmckenzie.com

Website: www.mylesmckenzie.com

PROJECT OWNER:

Mr. & Mrs. Awad
183 Snows Point Road
Saint George, ME 04860

PROJECT SCOPE:

A new residence and a workshop / studio.

STRUCTURAL CONSULTANT:

Dan'l Moulton, P.E.
10 Clayton Court
Bluffton, SC 29910
843-949-0658
dmoulton72@gmail.com

ENERGY CONSULTANT:

Elm Energy Group, LLC
Jamie Kaye
843-296-3715
Jamie@ElmEnergyGroup.com

PROJECT CODE NOTES:

MUBEC, MUBC & MUEC
2015 International Residential Code (IRC)
2009 International Energy Conservation Code (IECC)

Occupancy: R1
Type: V-B
Number of stories: 2
Residence sprinklers: No
Building Department: City of Saint George

AREA CALCULATIONS: (S.F.)

Residence	1st Floor Livable:	2840
	2nd Floor Livable:	783
	Covered Porches:	50
	Covered Deck:	215
	Total Covered Residence	3888
Workshop / Studio	1st Floor (unheated):	1600
	2nd Floor Livable:	696
	Covered Decks:	104
	Total Covered W/S:	2400
	Total Livable:	4319
	Total Covered Area:	6288



MYLES
NELSON
McKENZIE
DESIGN

Telephone: 949-683-6895
843-505-1031
Email: info@mylesmckenzie.com
Web: www.mylesmckenzie.com

These drawings documents and specifications are an instrument of service, copyright and the property of MYLES NELSON MCKENZIE DESIGN and shall not be used or reproduced in any part or whole, except by written agreement with the Architect or Designer of MYLES NELSON MCKENZIE DESIGN. Their use for publication shall be restricted to the original project in which they are designed for.


Written dimensions shall be verified on the job site. Any discrepancy shall be brought to notice of the Architect or Designer of MYLES NELSON MCKENZIE DESIGN prior to the commencement of any construction.

These plans have been reviewed and approved by:

[Signature]

A NEW CUSTOM RESIDENCE FOR
MR. & MRS. AIVAD
183 SNOWS POINT ROAD
SAINT GEORGE, ME 04860

Project

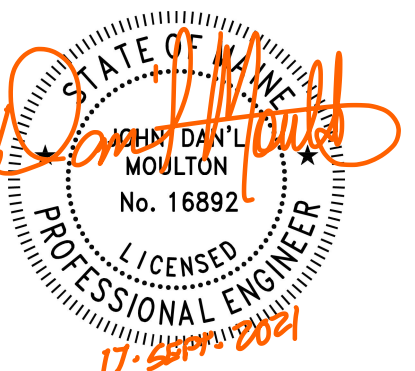

Number Date Description

Revisions

Issue Date 00/00/00

Plot Date 9/14/21

COVER SHEET

CS

Sheet