


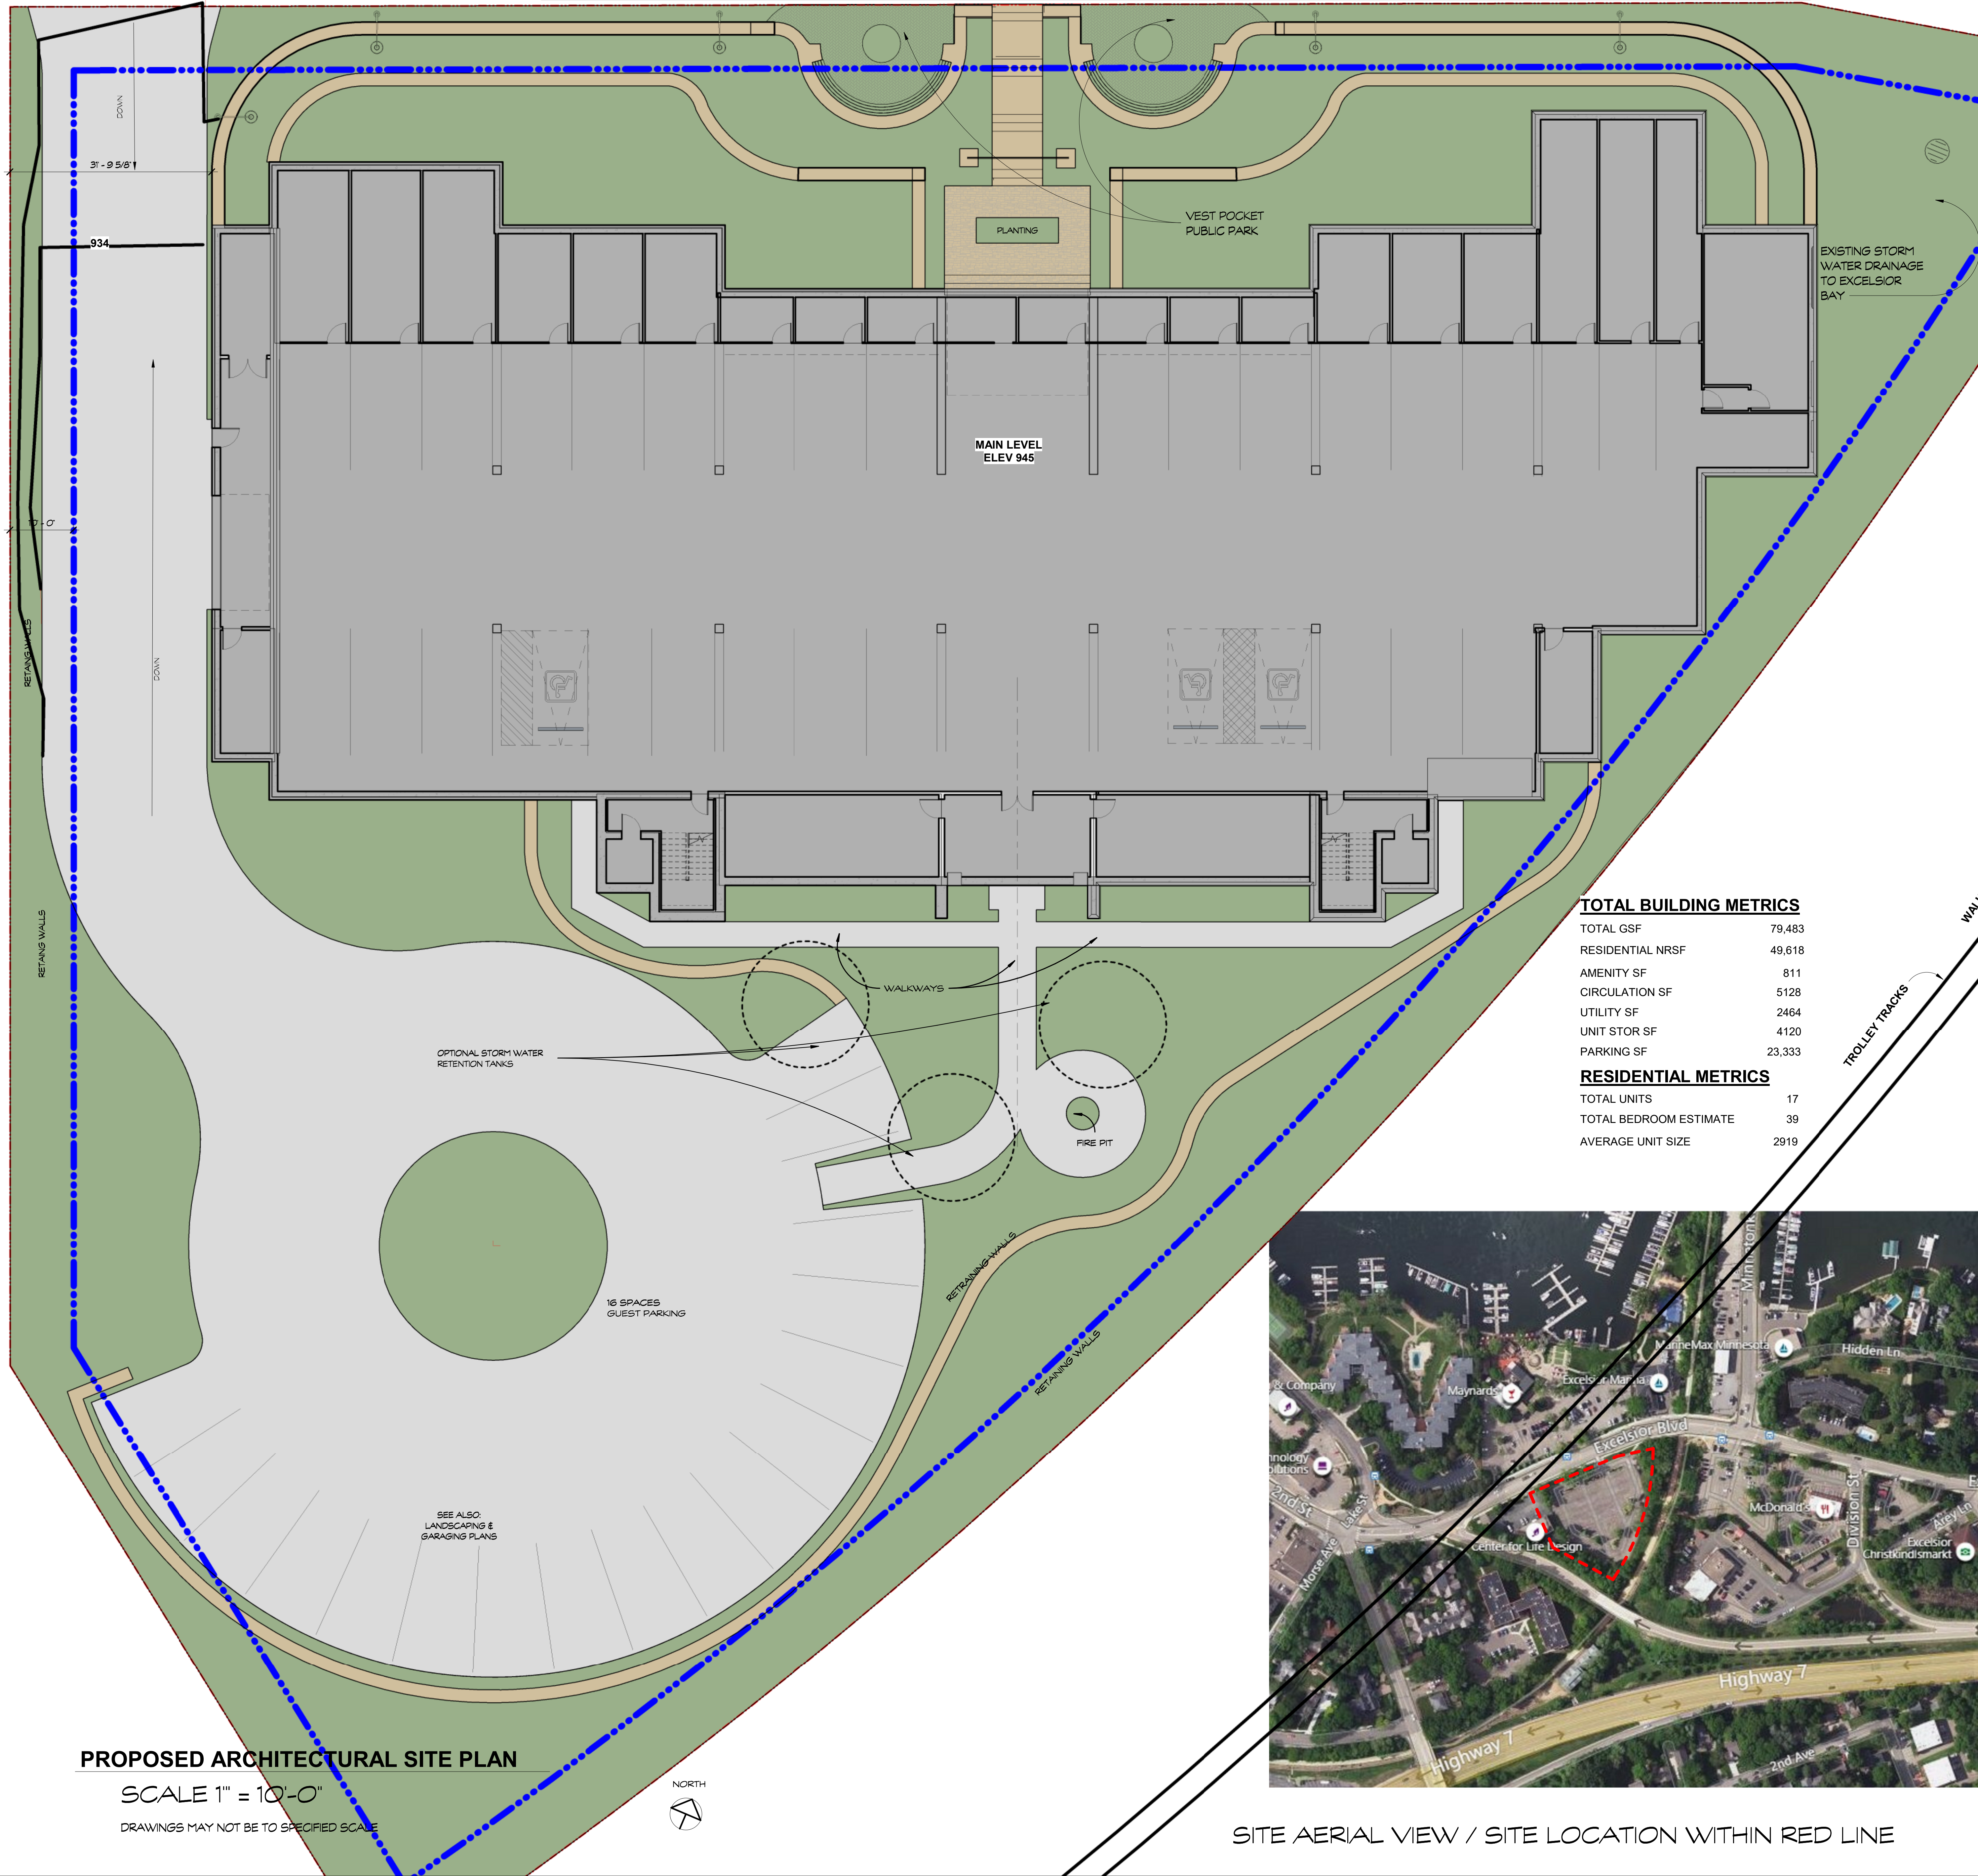


PROPOSED ARCHITECTURAL SITE PLAN

SCALE 1" = 10'-0"

DRAWINGS MAY NOT BE TO SPECIFIED SCALE

NORTH

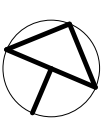

TOTAL BUILDING METRICS

TOTAL GSF	79,483
RESIDENTIAL NRSF	49,618
AMENITY SF	811
CIRCULATION SF	5128
UTILITY SF	2464
UNIT STOR SF	4120
PARKING SF	23,333

RESIDENTIAL METRICS

TOTAL UNITS	17
TOTAL BEDROOM ESTIMATE	39
AVERAGE UNIT SIZE	2919

WALL BETWEEN UNITS SHALL HAVE A 1 HOUR RATING (BC 708)

RESIDENTIAL CORRIDORS SHALL HAVE A RATING OF 0.5 HOURS (BC 1020.1)

CORRIDOR DOORS SHALL HAVE A 0.33 HOUR RATING (BC 716.2.2.1)

OCCUPANCY LOADS

OCCUPANCY = R-2 -SECTION (BC 310.3)
TYPE II B - FULL SPRINKLED- S13R
79,483 SQ FT TOTAL BUILDING GROSS AREA SEC- 506.2

OCCUPANCY LOAD - 200 GROSS. (IBC 1004.5)

CALCULATIONS.
PARKING LEVEL. 23,333 SQ.FT. = 117 (3 EXITS TOTAL PROVIDED)
MAIN LEVEL- 20,062 SQ.FT. = 97 (4 EXITS TOTAL PROVIDED)
SECOND LEVEL - 18,298 SQ.FT. = 90 (2 EXITS TOTAL PROVIDED)
THIRD LEVEL - 17,790 SQ. FT. = 90 (2 EXITS TOTAL PROVIDED)

TOTAL LOAD = 394

EXITING REQUIREMENTS

PARKING.
OCCUPANCY = S-2 - (IBC 310.3)
2 EXITS REQUIRED - 3 TOTAL PROVIDED (BC 1019.1)

MIN NUMBER 1-500 IS, 2 REQUIRED PER STORY. (BC 1006.3.2)
EGRESS MAXIMUM NUMBER OF 4 DWELLING UNITS ABOVE GRADE PER SINGLE EXIT (BC 1006.3.3)
WE HAVE NO MORE THAN 5 UNITS WITH ACCESS TO SINGLE STAIR TOWER SAFE SPACE / EXIT

PARKING REQUIREMENTS
2 STALLS PER UNIT
17 UNITS X 2 = 34 PARKING STALLS REQUIRED (36 STALL PROVIDED ENCLOSED. + 16 STALLS EXTERIOR)

APPLICABLE CODES
2018 - INTERNATIONAL BUILDING CODE
2020 - MINNESOTA BUILDING CODE
CURRENT EXCELSIOR CITY CODE

SITE INFORMATION
AREA 66,583 SF. - 1.53 ACRES
STAND ALONE RESIDENTIAL
SEPARATION IN EXCESS OF 30'-0" ON ALL SIDES (BC 603)

BUILDING INFORMATION:
23,333 GROSS SF. BUILDING FOOTPRINT

LOWER LEVEL PARKING & STORAGE UNITS
OCCUPANCY GROUP S2

RESIDENTIAL AREAS
OCCUPANCY GROUP R-2 (IBC 310.3)
-MAIN LEVEL AREA 20,062 SF
-SECOND LEVEL AREA 18,298 SF
-THIRD LEVEL AREA 17,790 SF

ONE STORY BELOW AVERAGE GRADE
WITH NON-RESIDENTIAL OCCUPANCY

MAX HEIGHT (TO CORNICE) FROM AVERAGE GRADE PLANE 37'-4"

THE ENTIRE BUILDING TO BE SPRINKLED IN COMPLIANCE WITH NFPA 13R REQUIREMENTS

ALLOWABLE BUILDING AREA CALCULATIONS

CONSTRUCTION TYPE TYPE II B (IBC 602.2)

BASE ALLOWABLE AREA
GROUP S-2 4 STORIES 21,000 SF
GROUP R-2 4 STORIES 16,000 SF

MODIFIED ALLOWABLE AREA
GROUP S-2 4 STORIES 26,250 SF
GROUP R-2 4 STORIES 20,000 SF

TOTAL FACADE LENGTH 252'-10"
AREA FACTOR 25% (IBC 506.3.1)

BUILDING IS FULLY SPRINKLED S13R
MAXIMUM HEIGHT INCREASED NOT REQUIRED.

FIRE RATINGS

OCCUPANT SEPARATION (508.3.3)

BETWEEN S-2 AND R-2 1 HOUR

FIRE RATINGS OF BUILDING ELEMENTS

STRUCTURAL FRAME	1 HOUR
BEARING WALLS	
EXTERIOR	1 HOUR
NON-BEARING WALLS	
EXTERIOR	1 HOUR
INTERIOR	1 HOUR

FIRE RETARDANT LUMBER TO BE USED (IBC 603.1)

INCIDENTAL USE AREA FIRE RATING
STORAGE ROOM OVER 100 SF 0 HOURS

RATINGS REDUCED DUE TO AUTOMATIC SPRINKLERS

MECHANICAL SHAFTS, ELEVATORS AND TRASH CHUTES TO HAVE A 1 HOUR RATING



SITE AERIAL VIEW / SITE LOCATION WITHIN RED LINE



464 SECOND STREET SUITE 100 EXCELSIOR, MN. 55331
PHONE: 952-470-9750 FAX: 952-767-5859
info@sharrattdesign.com

SHEET INDEX

A1	SITE PLAN
A2	PARKING LEVEL PLAN
A3	MAIN LEVEL PLAN
A4	SECOND LEVEL PLAN
A5	UPPER LEVEL PLAN
A6	ROOF PLAN
A7	EXTERIOR ELEVATIONS
A8	EXTERIOR ELEVATIONS
A9	BUILDING SECTION
A10	BUILDING SECTION
A11	BUILDING SECTION
A12	BUILDING SECTION
A13	BUILDING SECTION
A14	BUILDING SECTION
A15	SIGN ELEVATION
E1	SITE & FIRST LEVEL LIGHTING PLAN
E2	SECOND LEVEL LIGHTING PLAN
E3	THIRD LEVEL LIGHTING PLAN
S1	FOUNDATION PLAN
S2	MAIN LEVEL FRAMING PLAN
S3	SECOND LEVEL FRAMING PLAN
S4	THIRD LEVEL FRAMING PLAN
S5	ROOF FRAMING PLAN
S6	STRUCTURAL NOTES
C1	EXISTING CONDITIONS SURVEY
C2	REMOVALS PLAN
C3	SITE PLAN
C4	EROSION & SEDIMENT CONTROL PLAN
C5	GRADING PLAN
C6	UTILITY PLAN
C7	UTILITY PROFILES
C8	GARAGE LEVEL STORM SEWER
C9	SWPPP
C10	DETAILS
L1	LANDSCAPE PLAN

PROJECT TEAM

ARCHITECT

NORA KIRKWOLD/ MIKE SHARRATT
SHARRATT DESIGN & CO
464 SECOND STREET #100
EXCELSIOR, MN 55331
952-470-9750

CIVIL ENGINEER

ADAM PAWELK
HANSEN THORP PELLINEN OLSON, INC.
7510 Market Pl Dr # 101
Eden Prairie, MN 55344
952-829-0700

STRUCTURAL ENGINEER

DAVE WAGNER
A.M. STRUCTURAL ENGINEERING
112 E. MAPLE STREET
RIVER FALLS, WI. 54222
715-426-4930

DEVELOPER

GARY KRAEMER
JOHN KRAEMER & SONS, INC
4906 LINCOLN DRIVE
EDINA, MN 55436
952-935-9100

GENERAL CONTRACTOR

GARY KRAEMER
JOHN KRAEMER & SONS, INC
4906 LINCOLN DRIVE
EDINA, MN 55436
952-935-9100

ISSUED FOR

ISSUE DATE	CHECK	CLIENT	MEETING	ESTIMATES	REVISION	PERMIT	BID SET	ADDENDUM	CONSTRUCTION SET	SET TO STRUCTURE
02-18-2021				X						
03-01-2021				X						
03-05-2021				X						
04-02-2021				X						
06-07-2021	X									CONCEPT REVIEW BY PLANNING
11-17-2021	X									REVIEW W/ INSPECTIONS
11-30-2021				X						
12-09-2021	X									
12-22-2021	X									CHECK SET OF CITY PUD
04-15-2021	X									CITY PLANNING AND PUD APP.
08-09-2022	X									CITY PLANNING HEARING
07-18-2022				X						
07-20-2022	X									CITY PLANNING AND PUD APP.
08-27-2022										TO TRAFFIC ENG.
08-29-2022										TO STRUCTURAL ENG.
10-21-2022										TO HTPD
10-22-2022										TO STRUCTURAL ENG.
10-25-2022										MDS REVIEW
10-27-2022										FINAL PLAN OF DEVELOPMENT

PROPOSED NEW PUD CONSTRUCTION FOR:

THE EXCELSIOR FLATS

690 EXCELSIOR BLVD.
EXCELSIOR, MN 55331

SHEET A1 NUMBER

LEGAL NOTICE:
THESE DOCUMENTS SHALL NOT BE REPRODUCED OR REDISTRIBUTED WITHOUT EXPRESSED WRITTEN CONSENT OF SHARRATT DESIGN & COMPANY, LLC.
© COPYRIGHT 2022 SHARRATT DESIGN & COMPANY, LLC.