

COLLETON COUNTY RECREATION CENTER ADDITION AND RENOVATION

OWNER:

COLLETON COUNTY
113 MAPLE T. WILLIS BLVD.
WALTERBORO, SC, 29488
TEL: (843) 539-1968

ARCHITECT:

CLARK PATTERSON LEE
6302 FAIRVIEW RD., SUITE 102
CHARLOTTE, NC, 28210
Tel: (800) 274-9000
Fax: (704) 331-0402
www.clarkpatterson.com

MEP ENGINEERS:

CLARK PATTERSON LEE
912 SOUTH MAIN ST., SUITE ONE
GREENVILLE, SC, 29601
Tel: (800) 274-9000
Fax: (864) 220-9933
www.clarkpatterson.com

STRUCTURAL ENGINEERS:

MICHAEL M. SIMPSON &
ASSOCIATES, WC.
30 PATEWOOD DR., SUITE 100
GREENVILLE, SC 29615
TEL: (864) 331-1201
FAX: (864) 331-1070


CIVIL ENGINEERS:

INFRASTRUCTURE CONSULTING AND ENGINEERING
1691 TURNBULL AVENUE
NORTH CHARLESTON, SC 29405
TEL: (843) 266-3581
FAX: (843) 266-3583
WWW.ICE-ENG.COM

LIST OF DRAWINGS

GENERAL	COVER	HVAC
G001	UL ASSEMBLIES	H000
G002	UL ASSEMBLIES	H100
G003	UL ASSEMBLIES	H200
G004	UL ASSEMBLIES	H201
G005	UL ASSEMBLIES	H500
G006	UL ASSEMBLIES	H800
G007	PARTITION DETAILS	H801
		H900
CIVIL	COVER SHEET	FIRE PROTECTION
C0.0	EXISTING CONDITIONS & DEMOLITION PLAN	FP200
C2.0	SITE PLAN	
C3.0	GRADING & DRAINAGE PLAN	PLUMBING
C4.0	EROSION CONTROL PLAN	P000
C5.1	EROSION CONTROL DETAILS	P100
C6.0	UTILITY PLAN	P200
C6.1	UTILITY DETAILS	P201
		P300
		P800
STRUCTURAL	GENERAL NOTES	ELECTRICAL
S001	BASIS OF DESIGN	E000
S002	FOUNDATION/SLAB PLAN	E001
S101	ROOF FRAMING PLAN	E100
S201	SECTIONS AND DETAILS	E200
S301	SECTIONS AND DETAILS	E201
S401	SECTIONS AND DETAILS	E300
S402	SECTIONS AND DETAILS	E700
S501	MASONRY SECTIONS AND DETAILS	E800
		E900
ARCHITECTURAL	LIFE SAFETY PLAN	SPLASH PAD
A001	ARCHITECTURAL SITE PLAN	SP-1
A002	DEMOLITION FLOOR PLAN	SP-2
A100	GROUND FLOOR FURNITURE PLAN	SP-3
A200A	ROOF PLAN	SP-4
A200B	BUILDING ELEVATIONS	SP-5
A300	WALL TYPES	SP-6
A401	BUILDING SECTIONS	SP-7
A402	WALL SECTIONS	SP-8
A403	WALL SECTIONS	SP-9
A404	REFLECTED CEILING PLAN	SP-10
A700	TYP. FIXTURE AND ACCESS, HEIGHTS AND LEGENDS	SP-11
A701	ENLARGED FLOOR PLAN AND INTERIOR ELEVATIONS	SP-12
A702	INTERIOR ELEVATIONS	SP-13
A800	TYPICAL DETAILS	SP-14
A801	ROOF DETAILS	SP-15
A802	ROOF DETAILS	
A810	PLAN DETAILS	
A811	PLAN DETAILS	
A820	TYPICAL CEILING AND MILLWORK DETAILS	
A900	DOOR SCHEDULE, DOOR FRAMES, AND WINDOW TYPES	
INTERIORS	FIRST FLOOR FINISH PLAN	
I200	FINISH SPECIFICATIONS	
I900		

LOCATION MAP

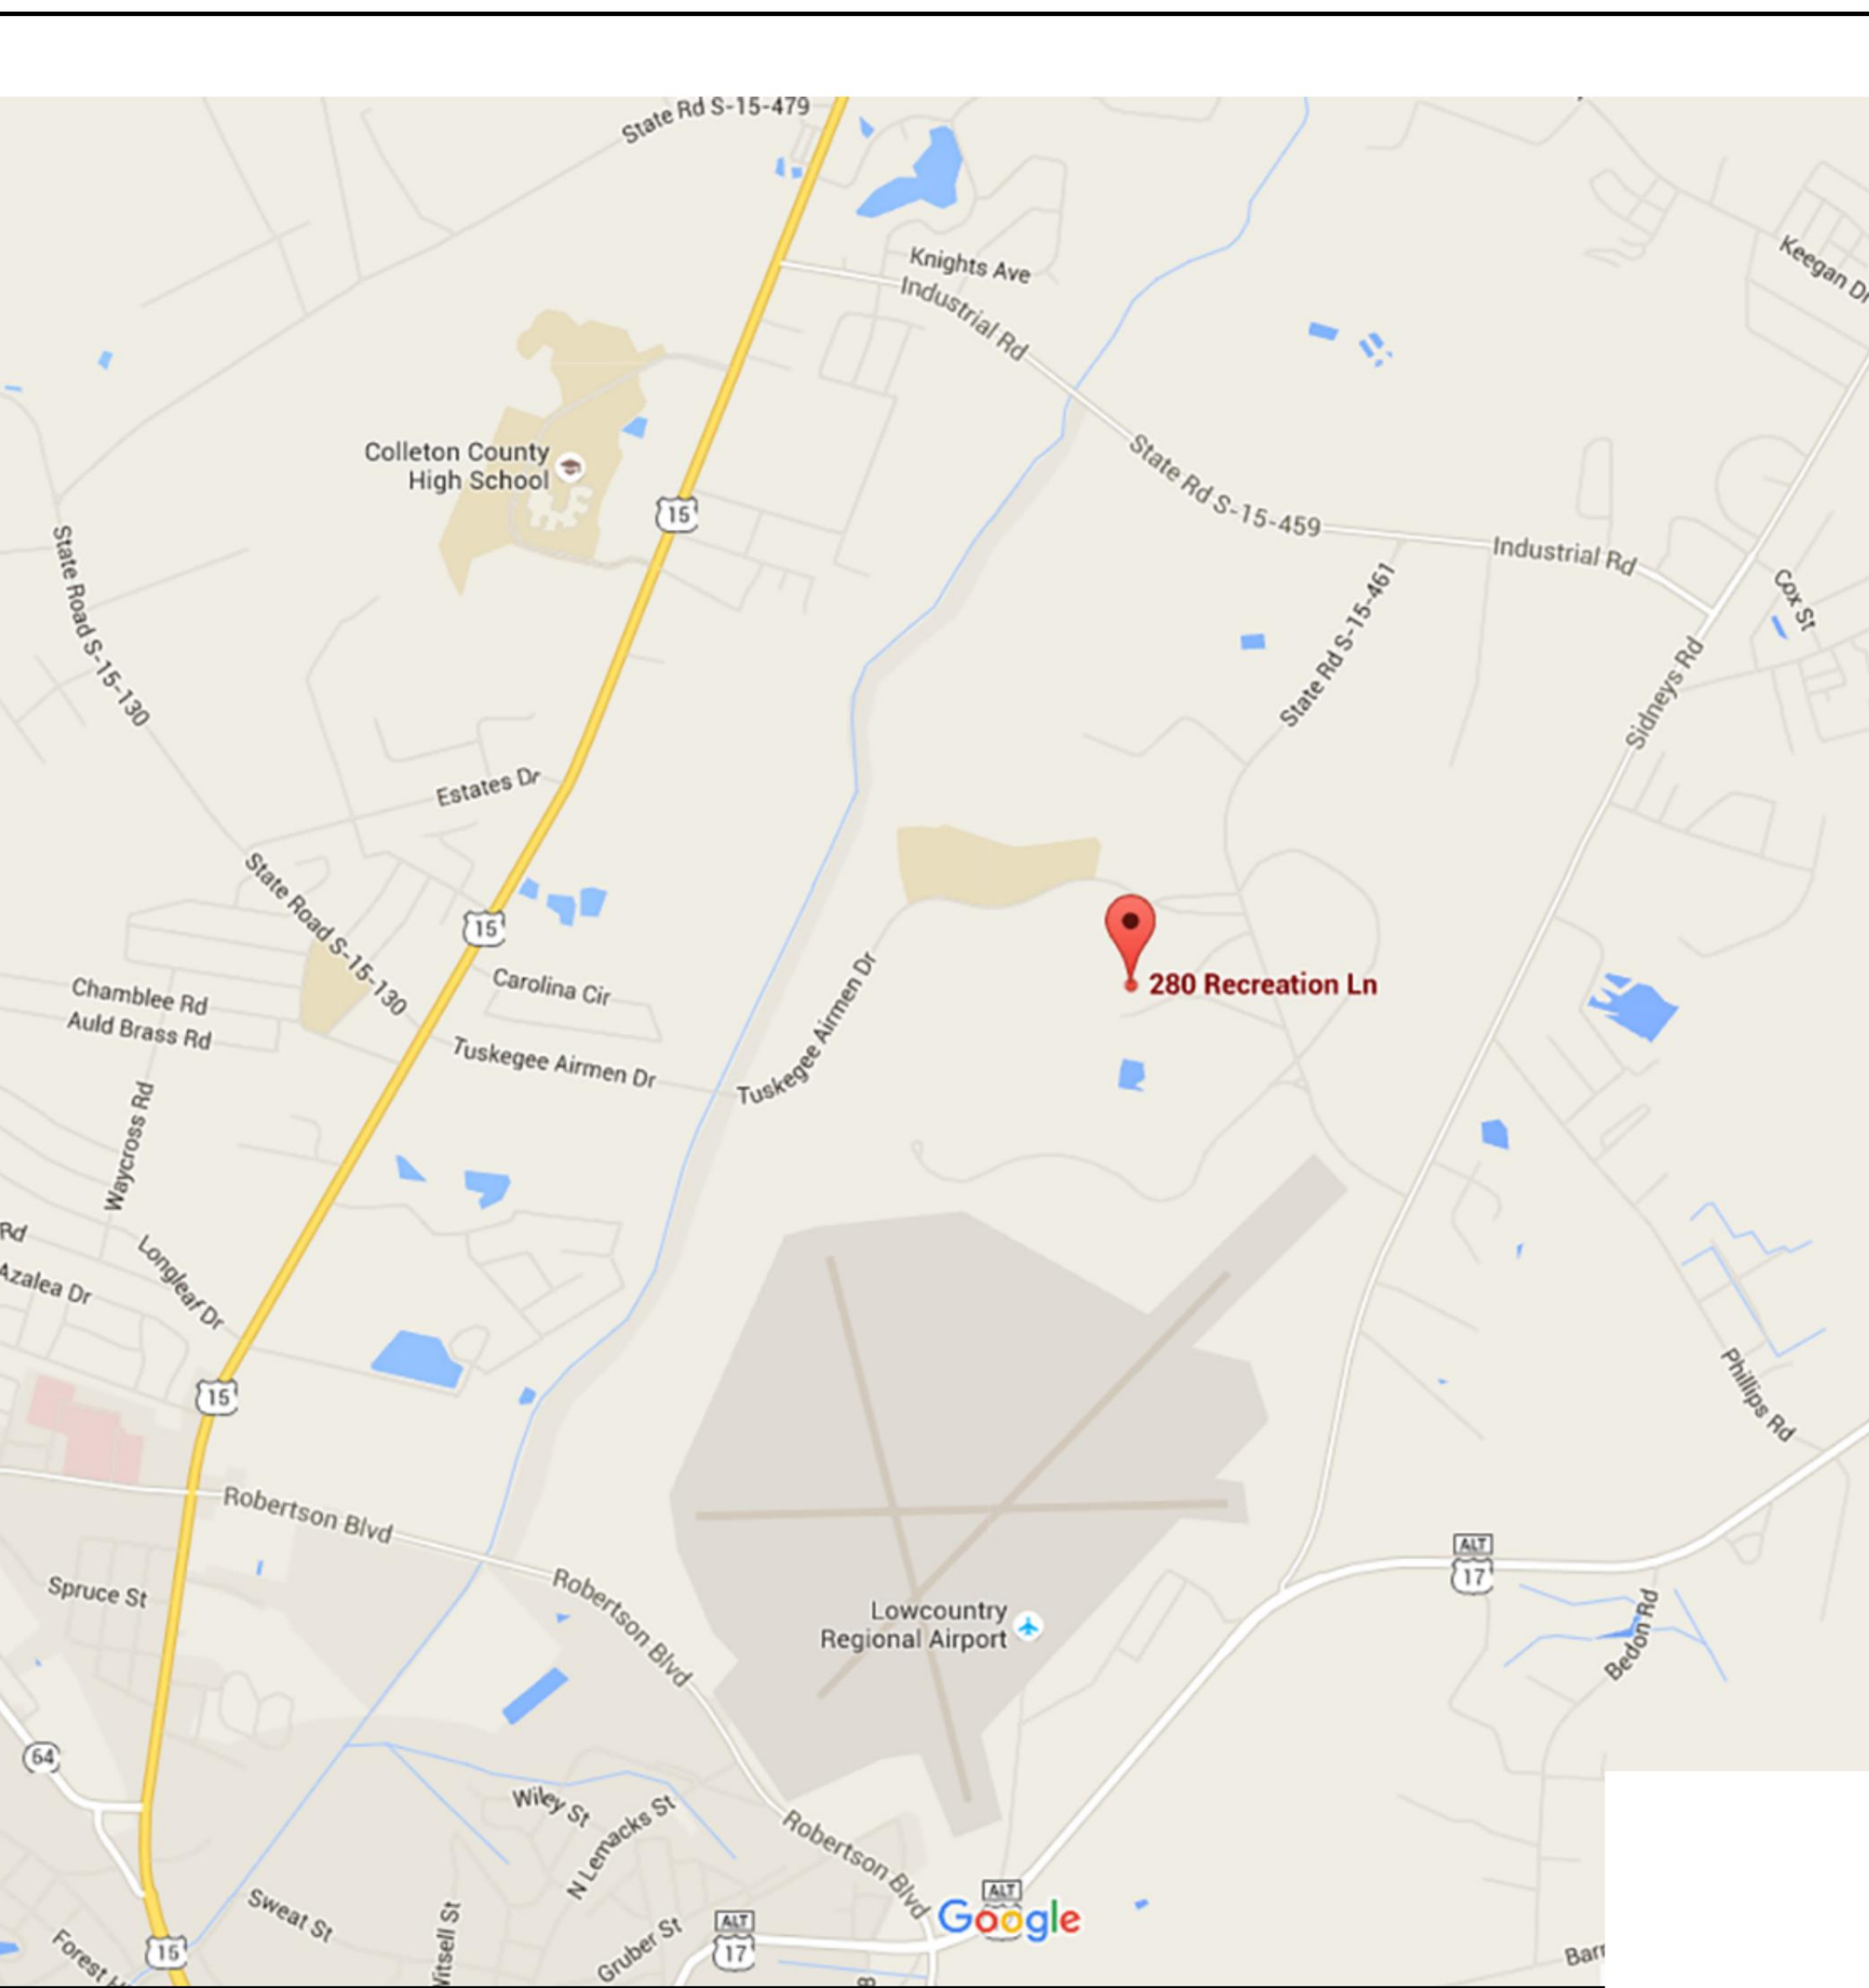

LIST OF ABBREVIATIONS

5/25/2017 1:37:50 PM
H:\Collabor\Co-Editing\Bldg Plans_13474_ARCH\294\clarkpatterson.com.rvt

MATERIAL SYMBOLS

EARTH	BRICK	RIGID INSULATION	1 HR RATING
GYPSUM BOARD	STEEL	BATT OR LOOSE INSULATION	2 HR RATING
GRAVEL TYPE 1 (ENGINEERED FILL)	GROUT	CAVITY DRAINAGE MAT	SMOKE RATING
PRECAST CONCRETE	ROUGH WOOD BLOCKING	ALUMINUM	EXISTING BUILDING MATERIALS
CRUSHED STONE	ROUGH WOOD BLOCKING, NON-CONTINUOUS	STANDING SEAM ROOF	
CONCRETE MASONRY UNIT (CMU)	WOOD, FINISHED WOODWORK	CONCRETE	
METAL STUD PARTITION	PLYWOOD (LARGE SCALE)	TERRAZZO	

GRAPHIC SYMBOLS

A COLUMN CENTERLINE A	II PARTITION TYPE 11 (1hr RATED) SEE PARTITION LEGEND	PROPERTY LINE	CASEWORK TAG
3 SIM DETAIL #3 on SHEET A201	REVISION NO. 1	FENCE	ACCESSORY TAG
1 SIM BUILDING SECTION (NO.) or WALL SECTION (LETTER) on SHEET A101	+100.75 EXISTING SPOT ELEVATION	EXISTING TREE TO REMAIN	WINDOW TAG (TYPE LETTER)