




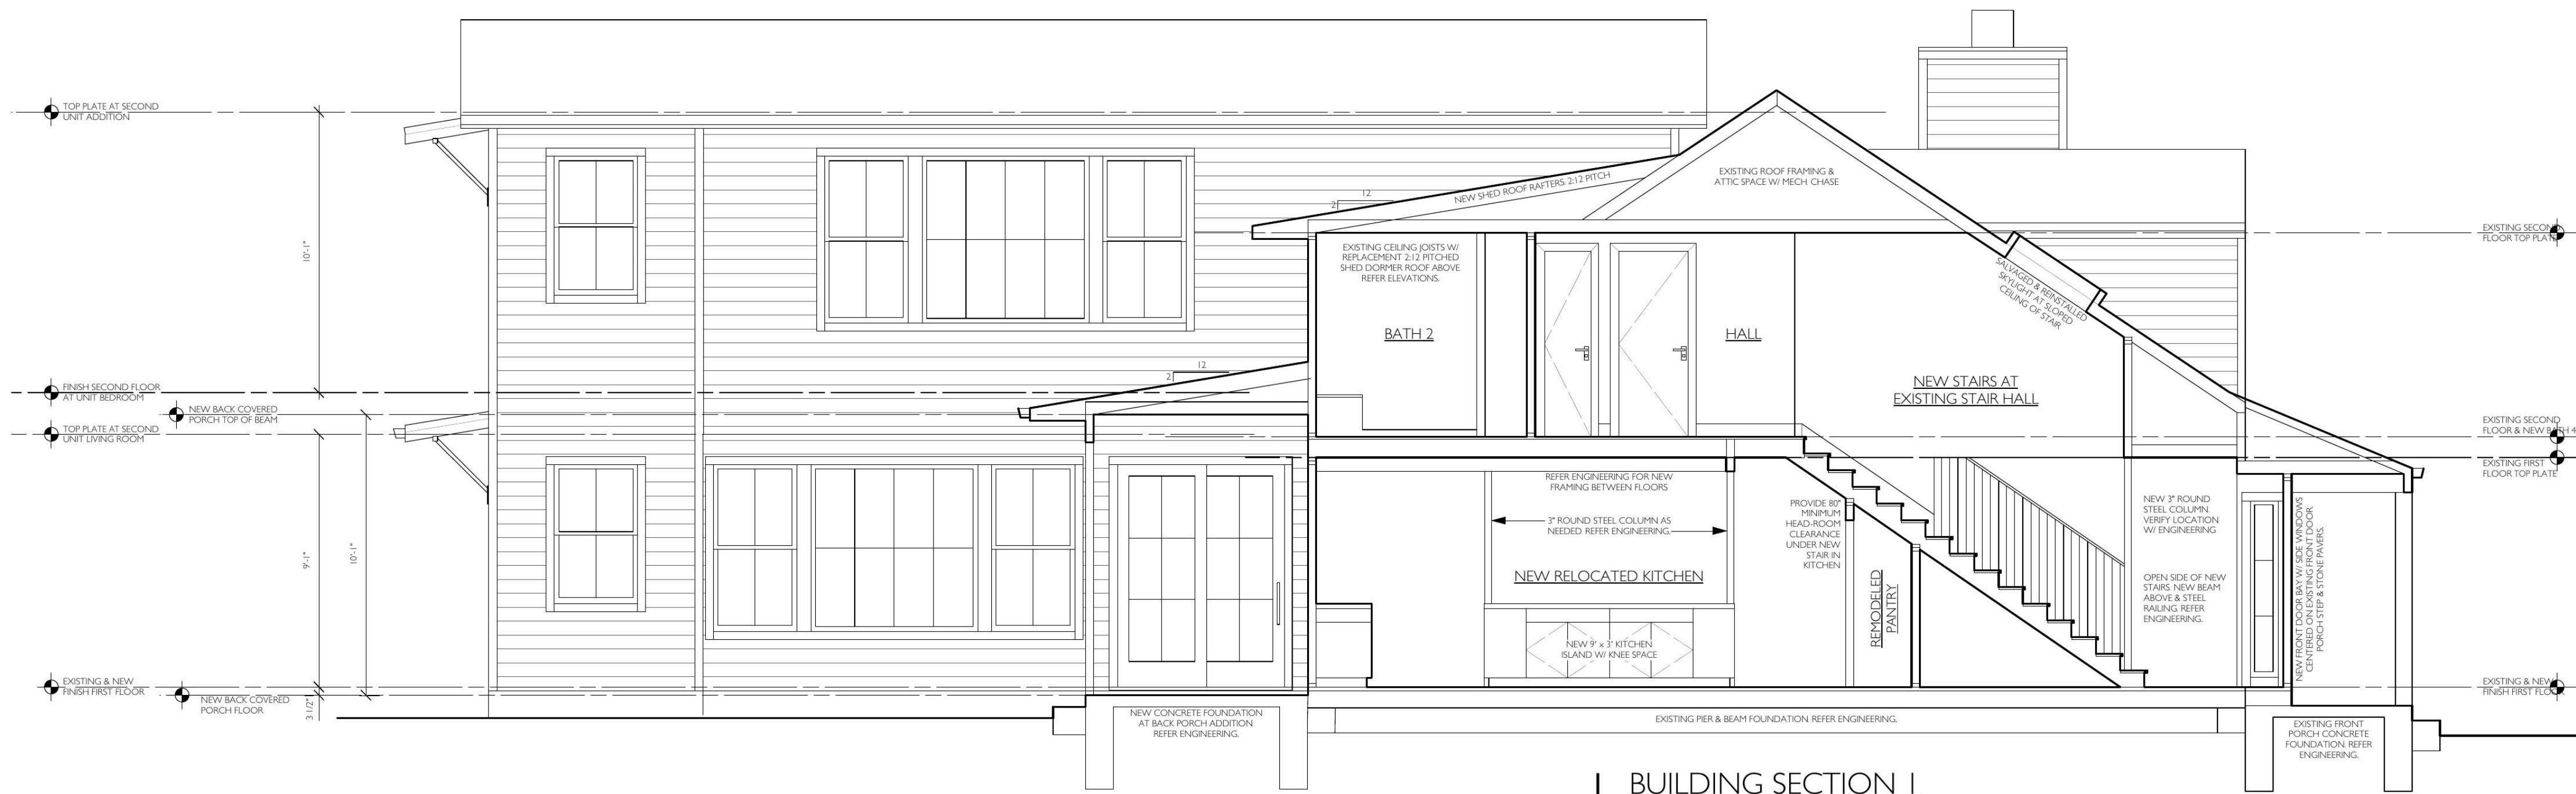

BUILDING SECTION 1
SCALE: 1/4" = 1'-0"

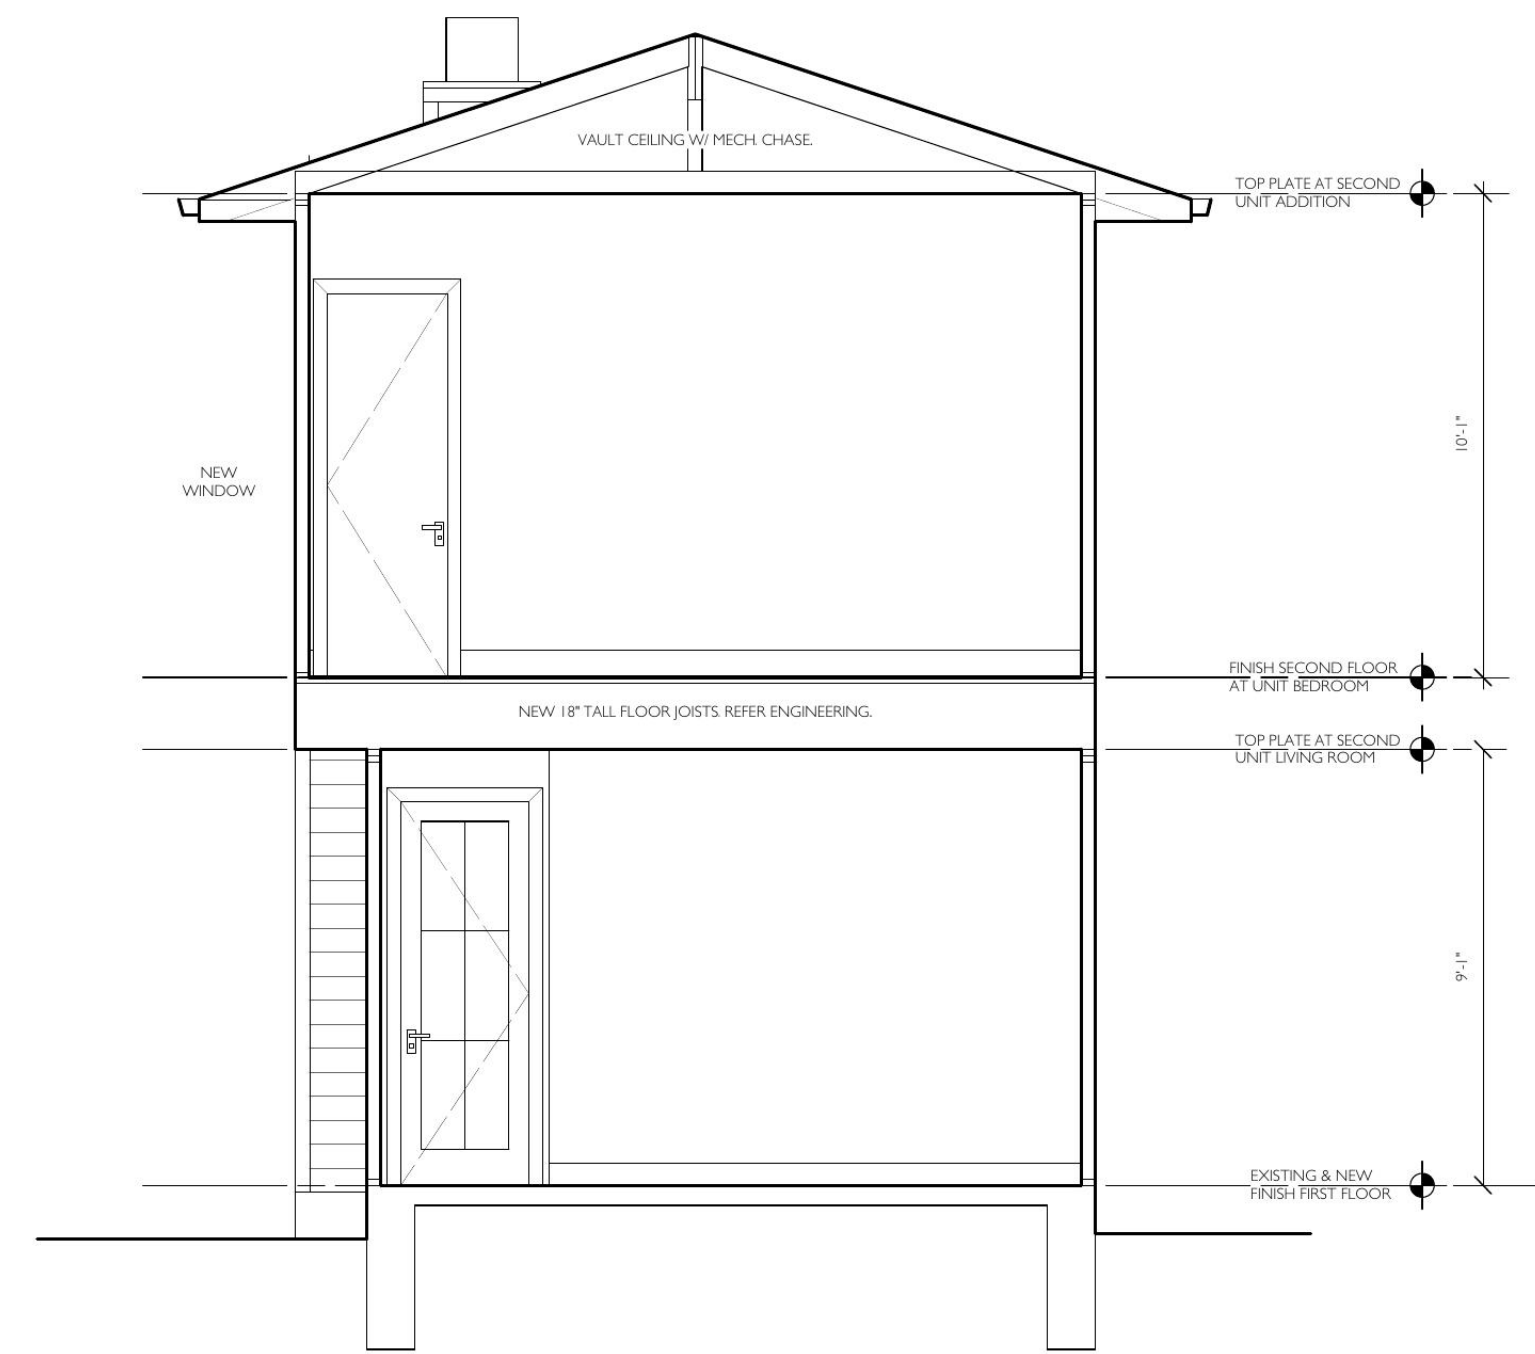

BUILDING SECTION 2
SCALE: 1/4" = 1'-0"

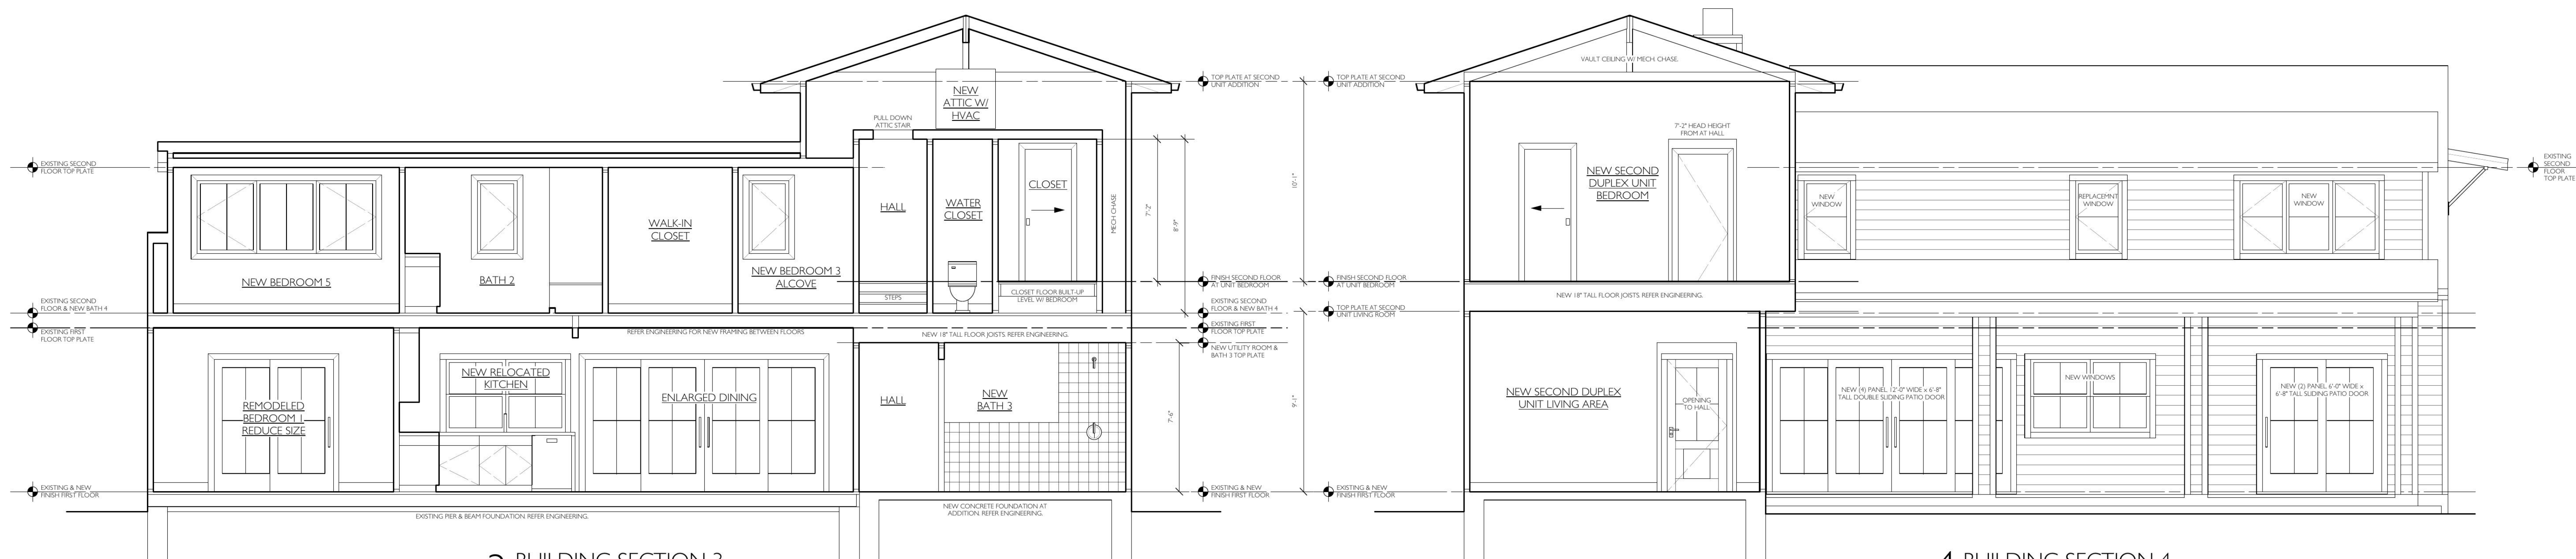

BUILDING SECTION 3
SCALE: 1/4" = 1'-0"



BUILDING SECTION 4
SCALE: 1/4" = 1'-0"



R.H.
1926

Richard HUGHES Principal, Architect

1606 West 11th Street, Austin, TX 78703
T: 512.789.6959
info@richardhughesarchitect.com



W DUPLEX ADDITION & REMODEL
102 GLENVIEW AVENUE, AUSTIN, TX 78703