




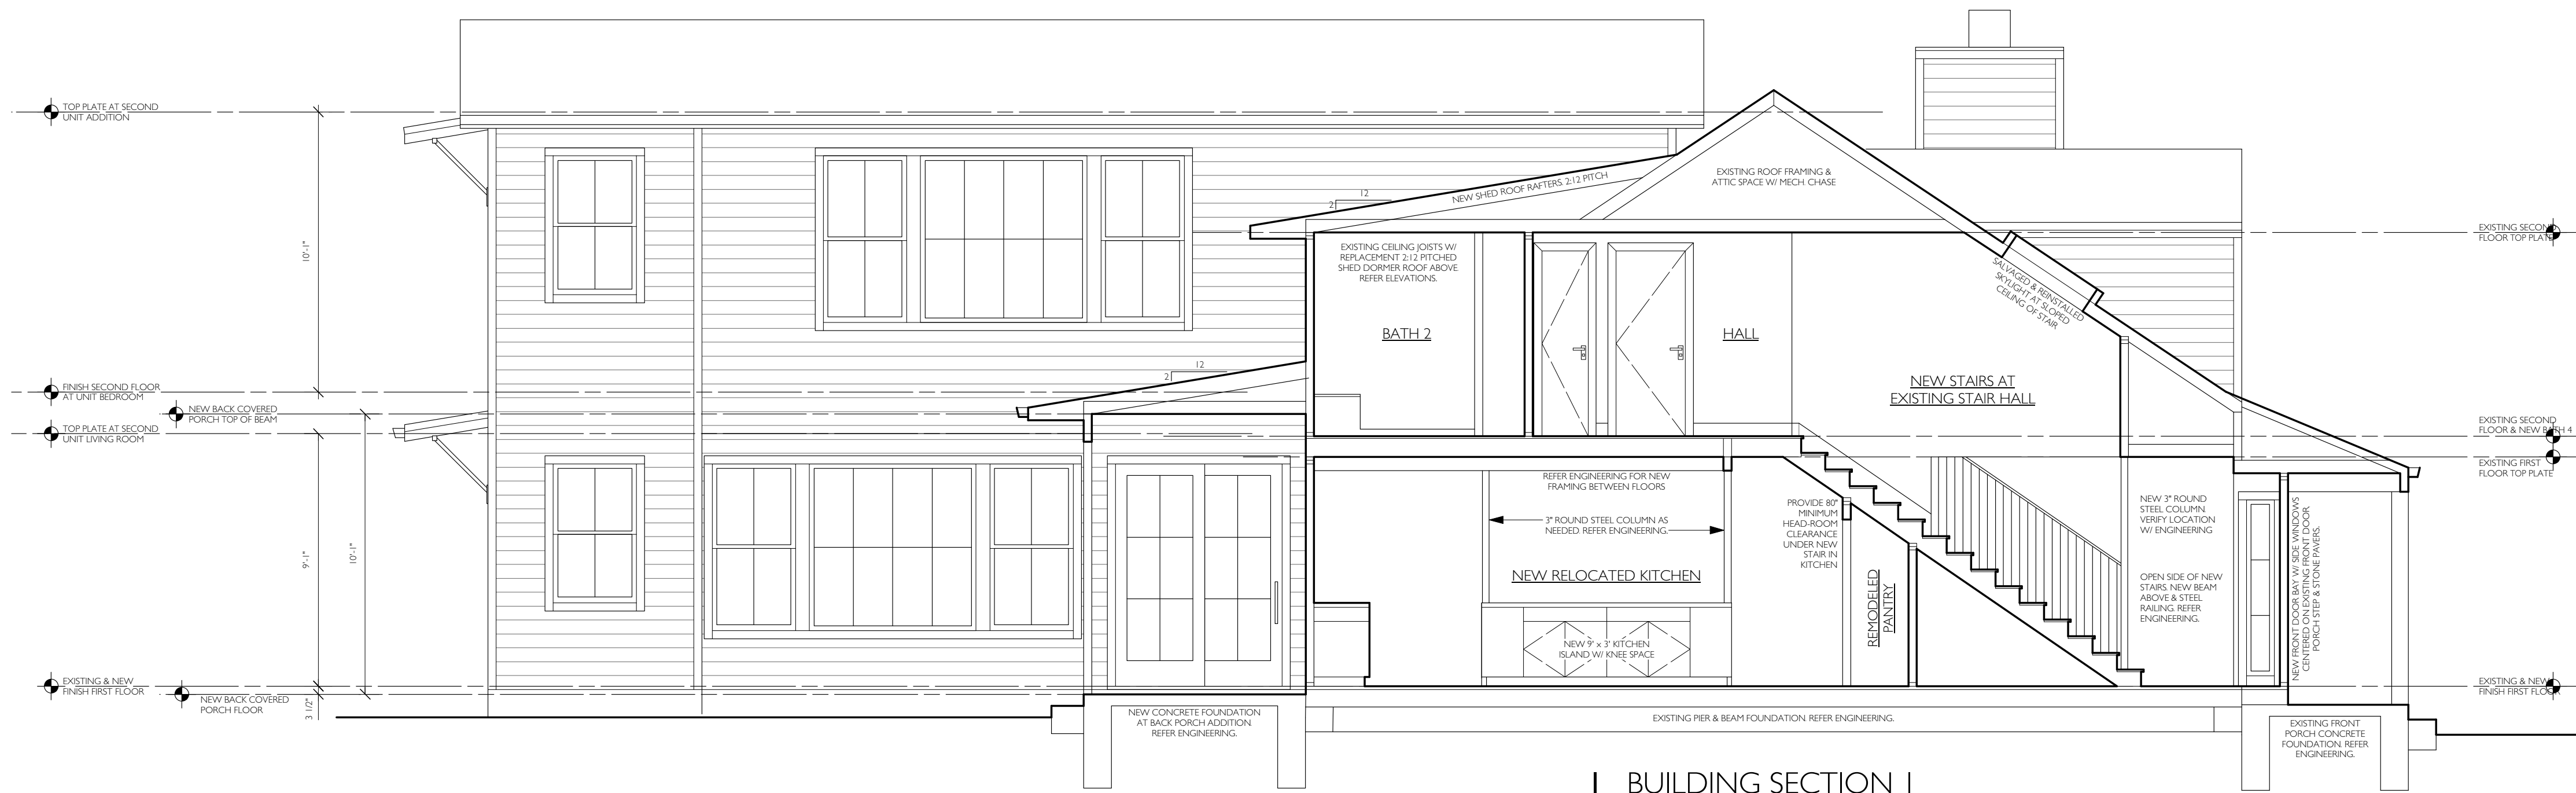

BUILDING SECTION 1
SCALE: 1/4" = 1'-0"

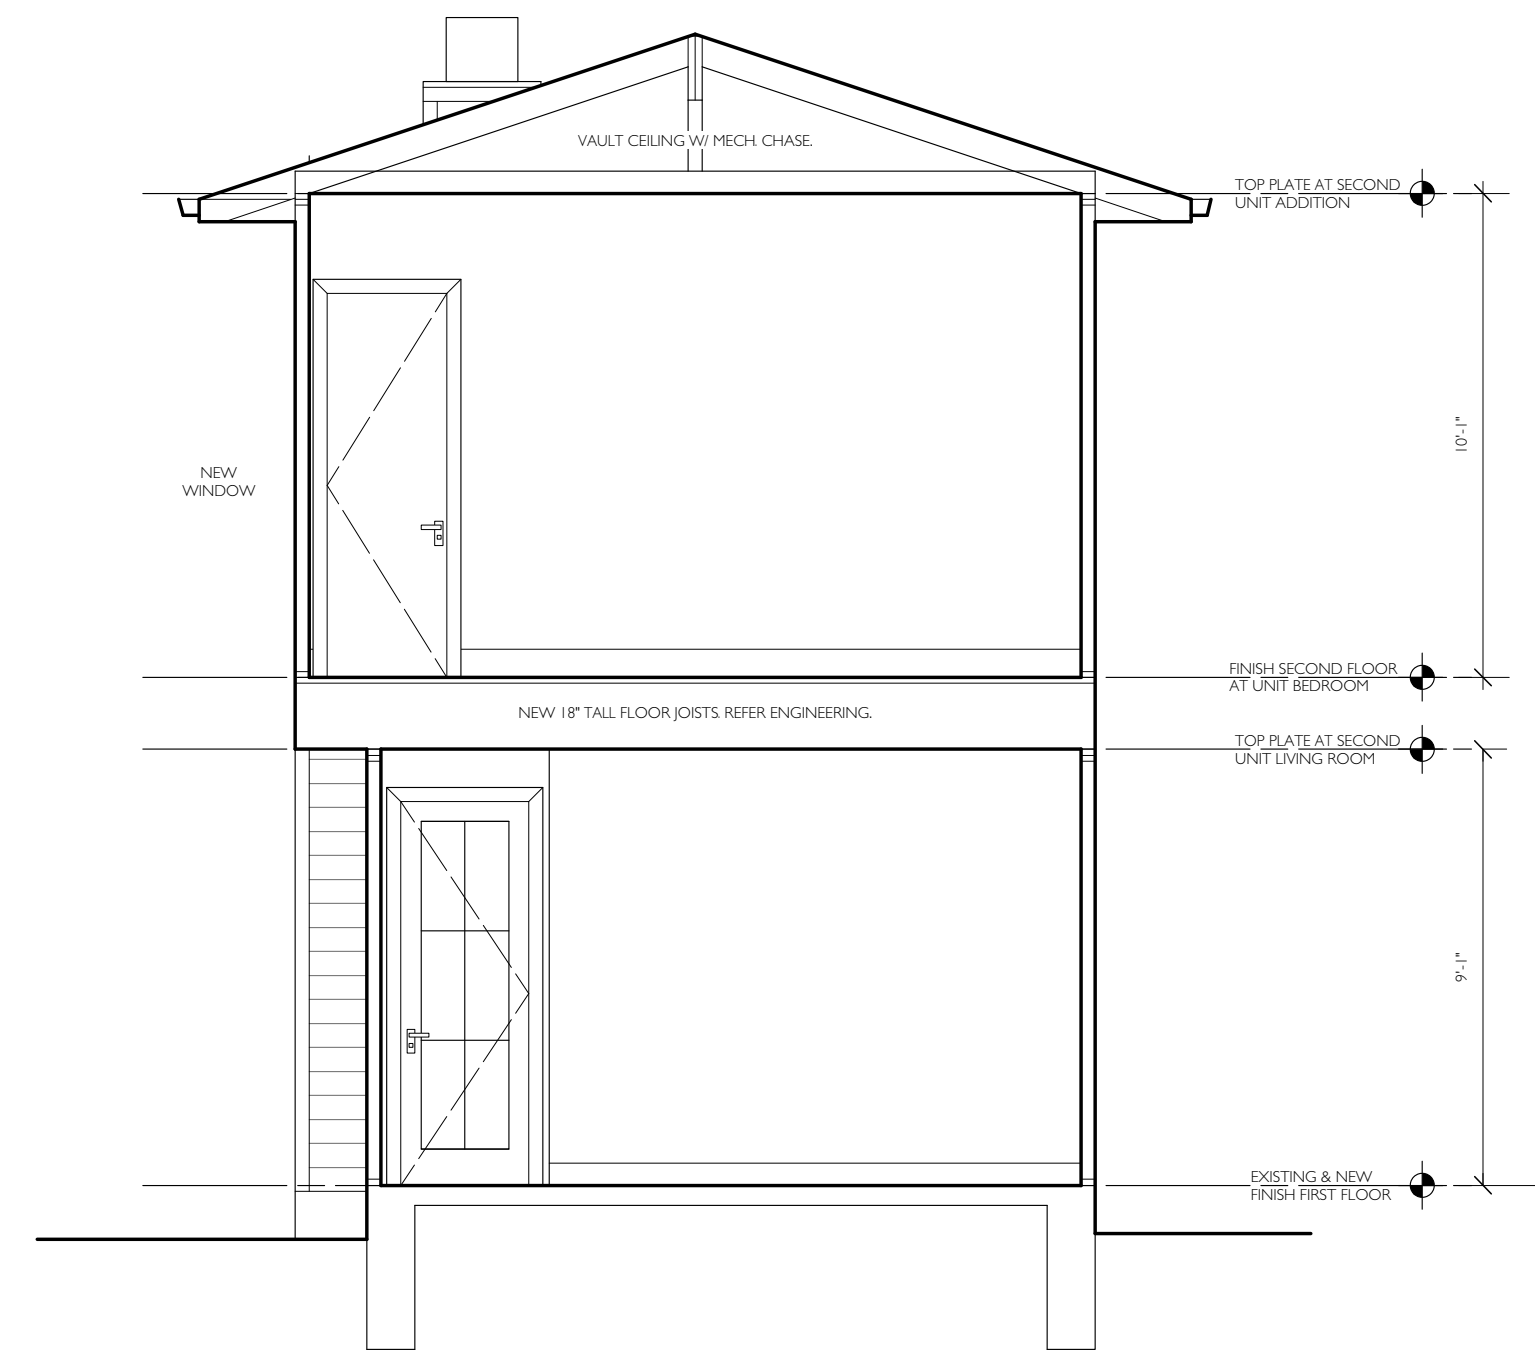

2 BUILDING SECTION 2
SCALE: 1/4" = 1'-0"

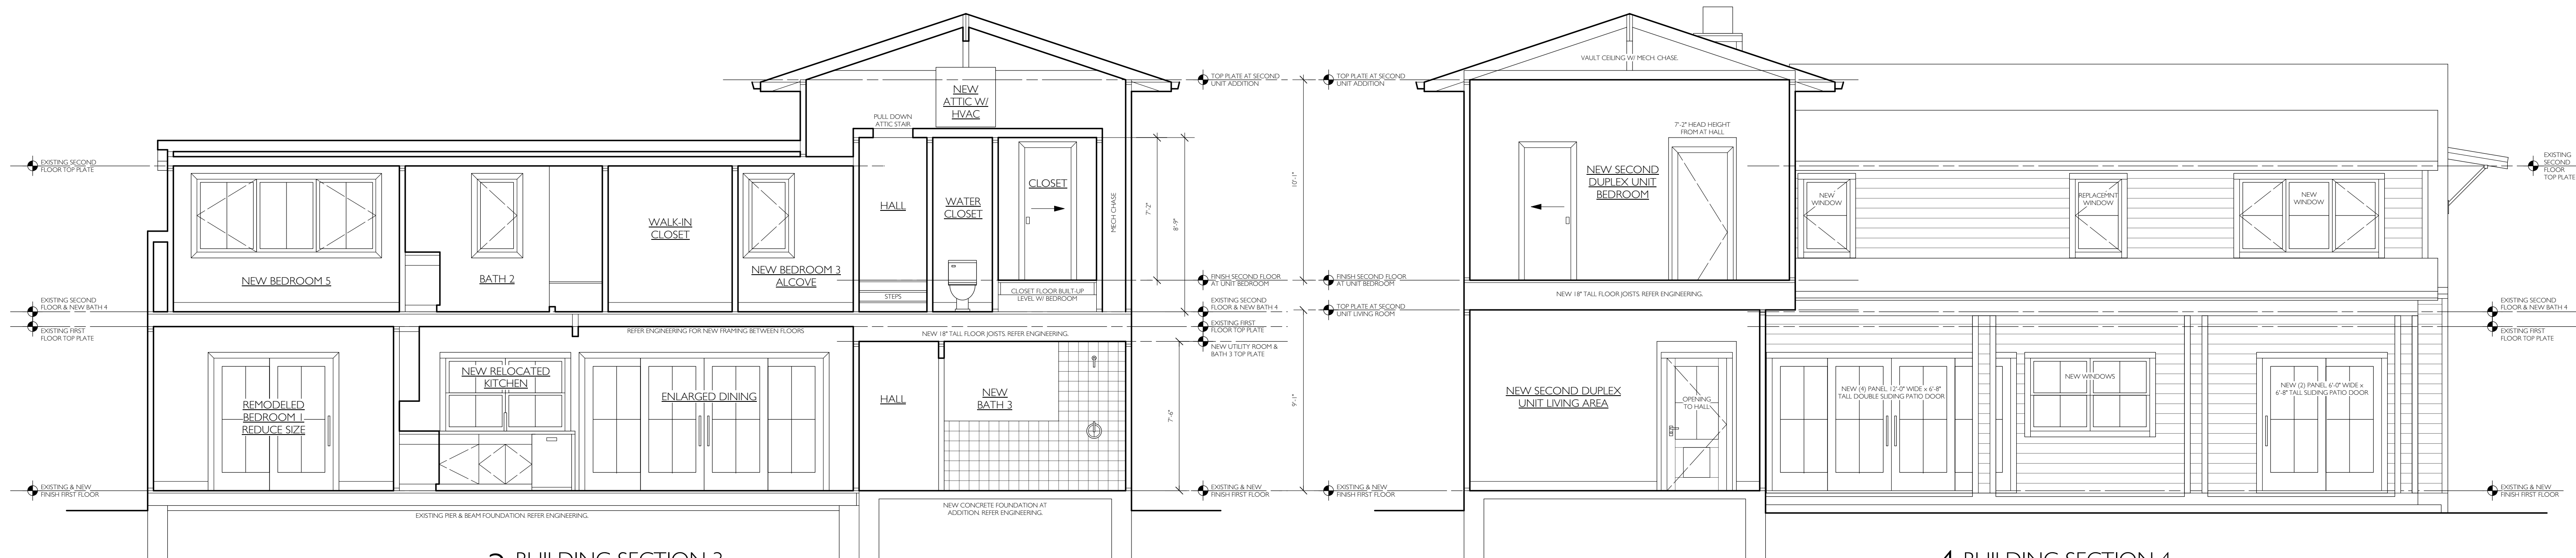

3 BUILDING SECTION 3
SCALE: 1/4" = 1'-0"



4 BUILDING SECTION 4
SCALE: 1/4" = 1'-0"



R.H.
1926

Richard HUGHES Principal, Architect
1605 West 11th Street, Austin, TX 78703
T: 512.789.6959
info@richardhughesarchitect.com



NEIL NEW DUPLEX ADDITION & REMODEL
3102 GLENVIEW AVENUE, AUSTIN, TX 78703

DATE:

10-16-24
10-31-24
11-18-24
11-20-24
11-21-24
12-13-24
8-15-25
9-3-25
10-14-25
10-17-25
10-20-25
10-28-25
12-5-25
12-18-25
12-19-25
12-19-25
1-7-26
1-9-26

A6