



JOHAN, EVA AND WILLY WALL

692 4TH CONCESSION ROAD
WALSINGHAM, ONTARIO
NOE 1X0

P: 519-501-9725
E: GOODJOHAN19@GMAIL.COM

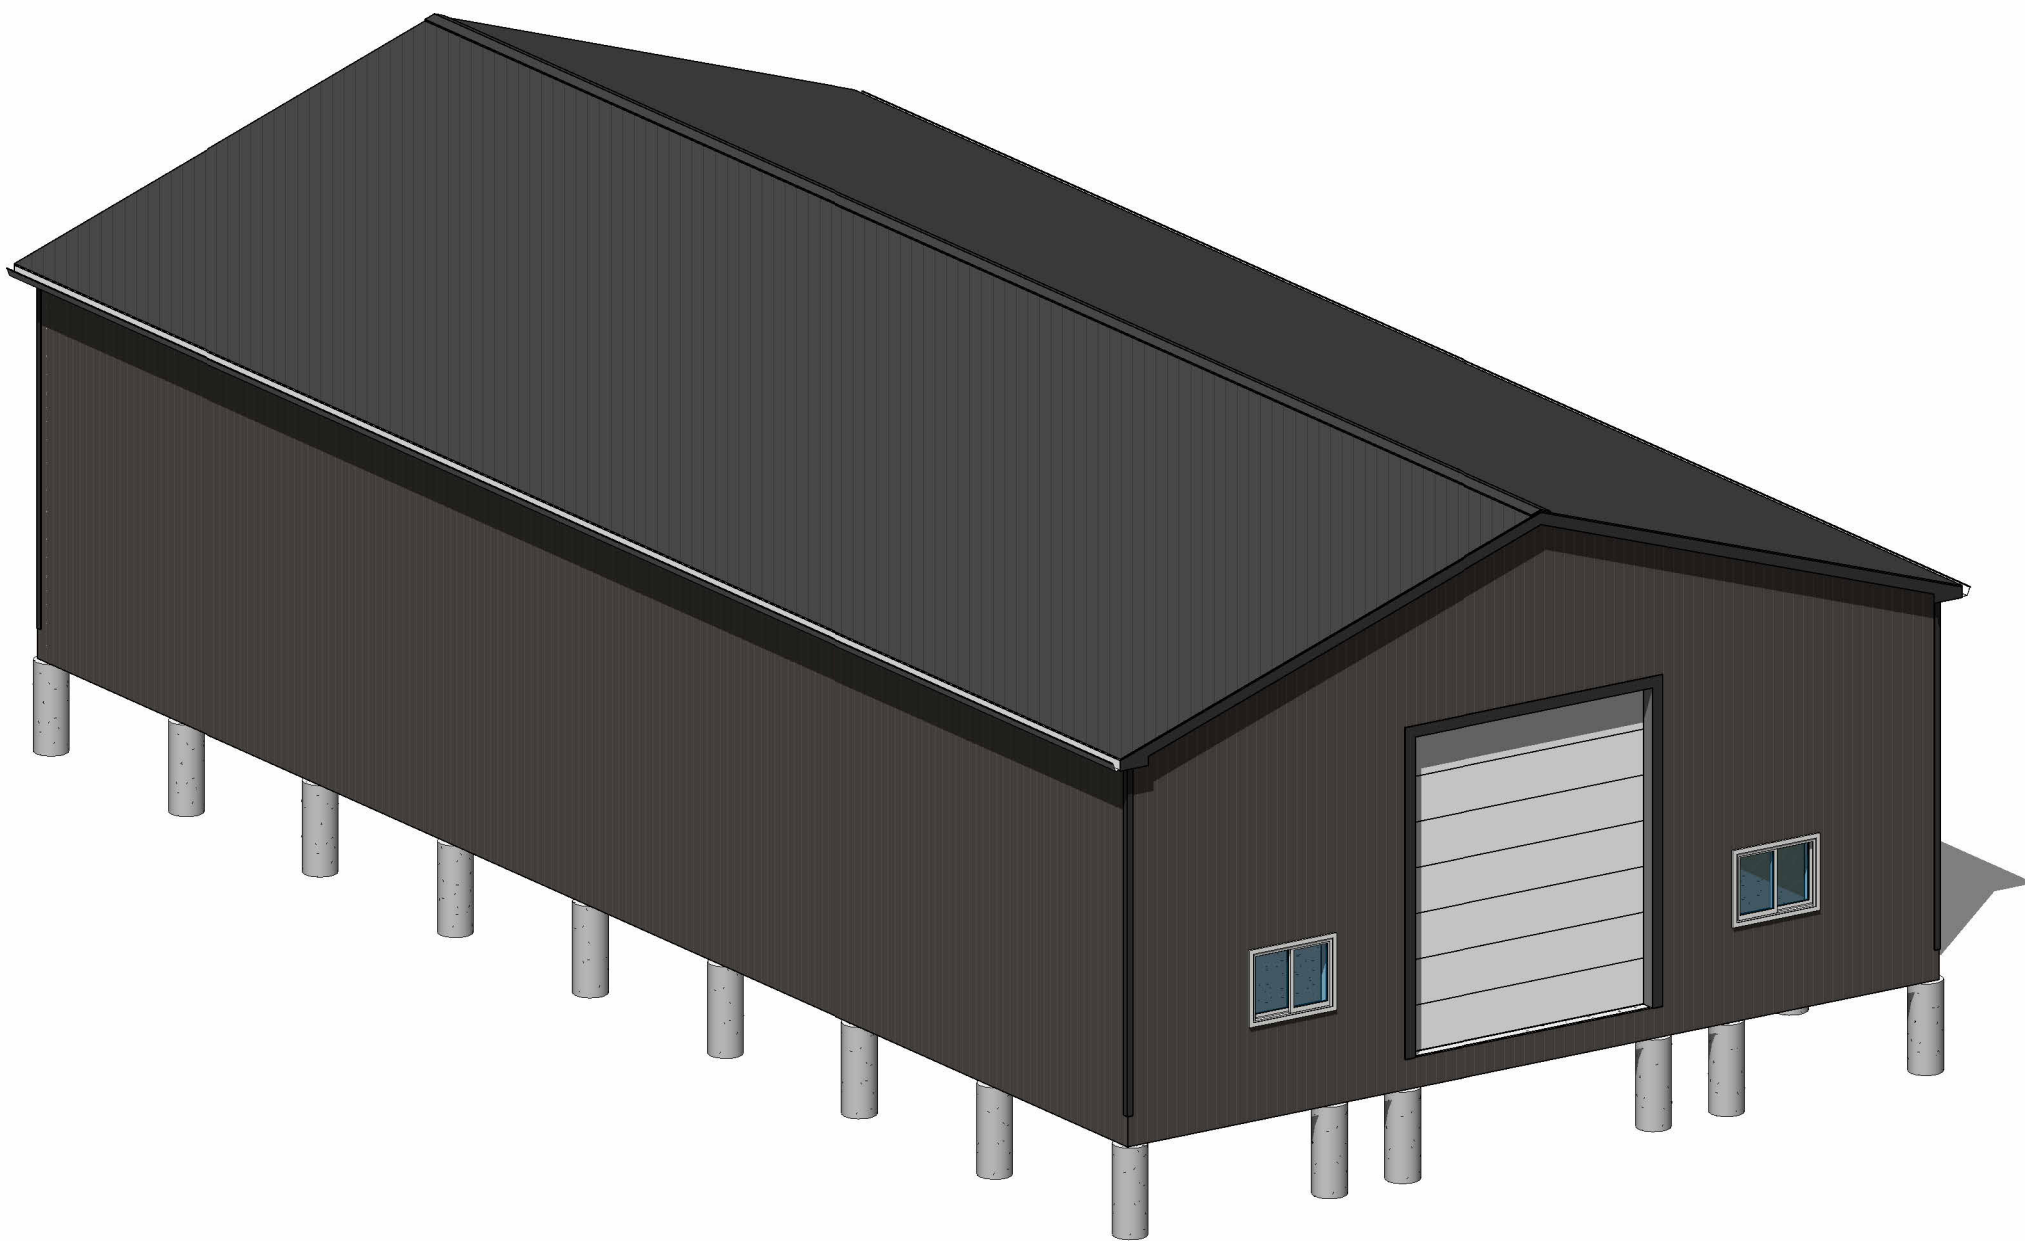

2 FRONT VIEW
A0.00

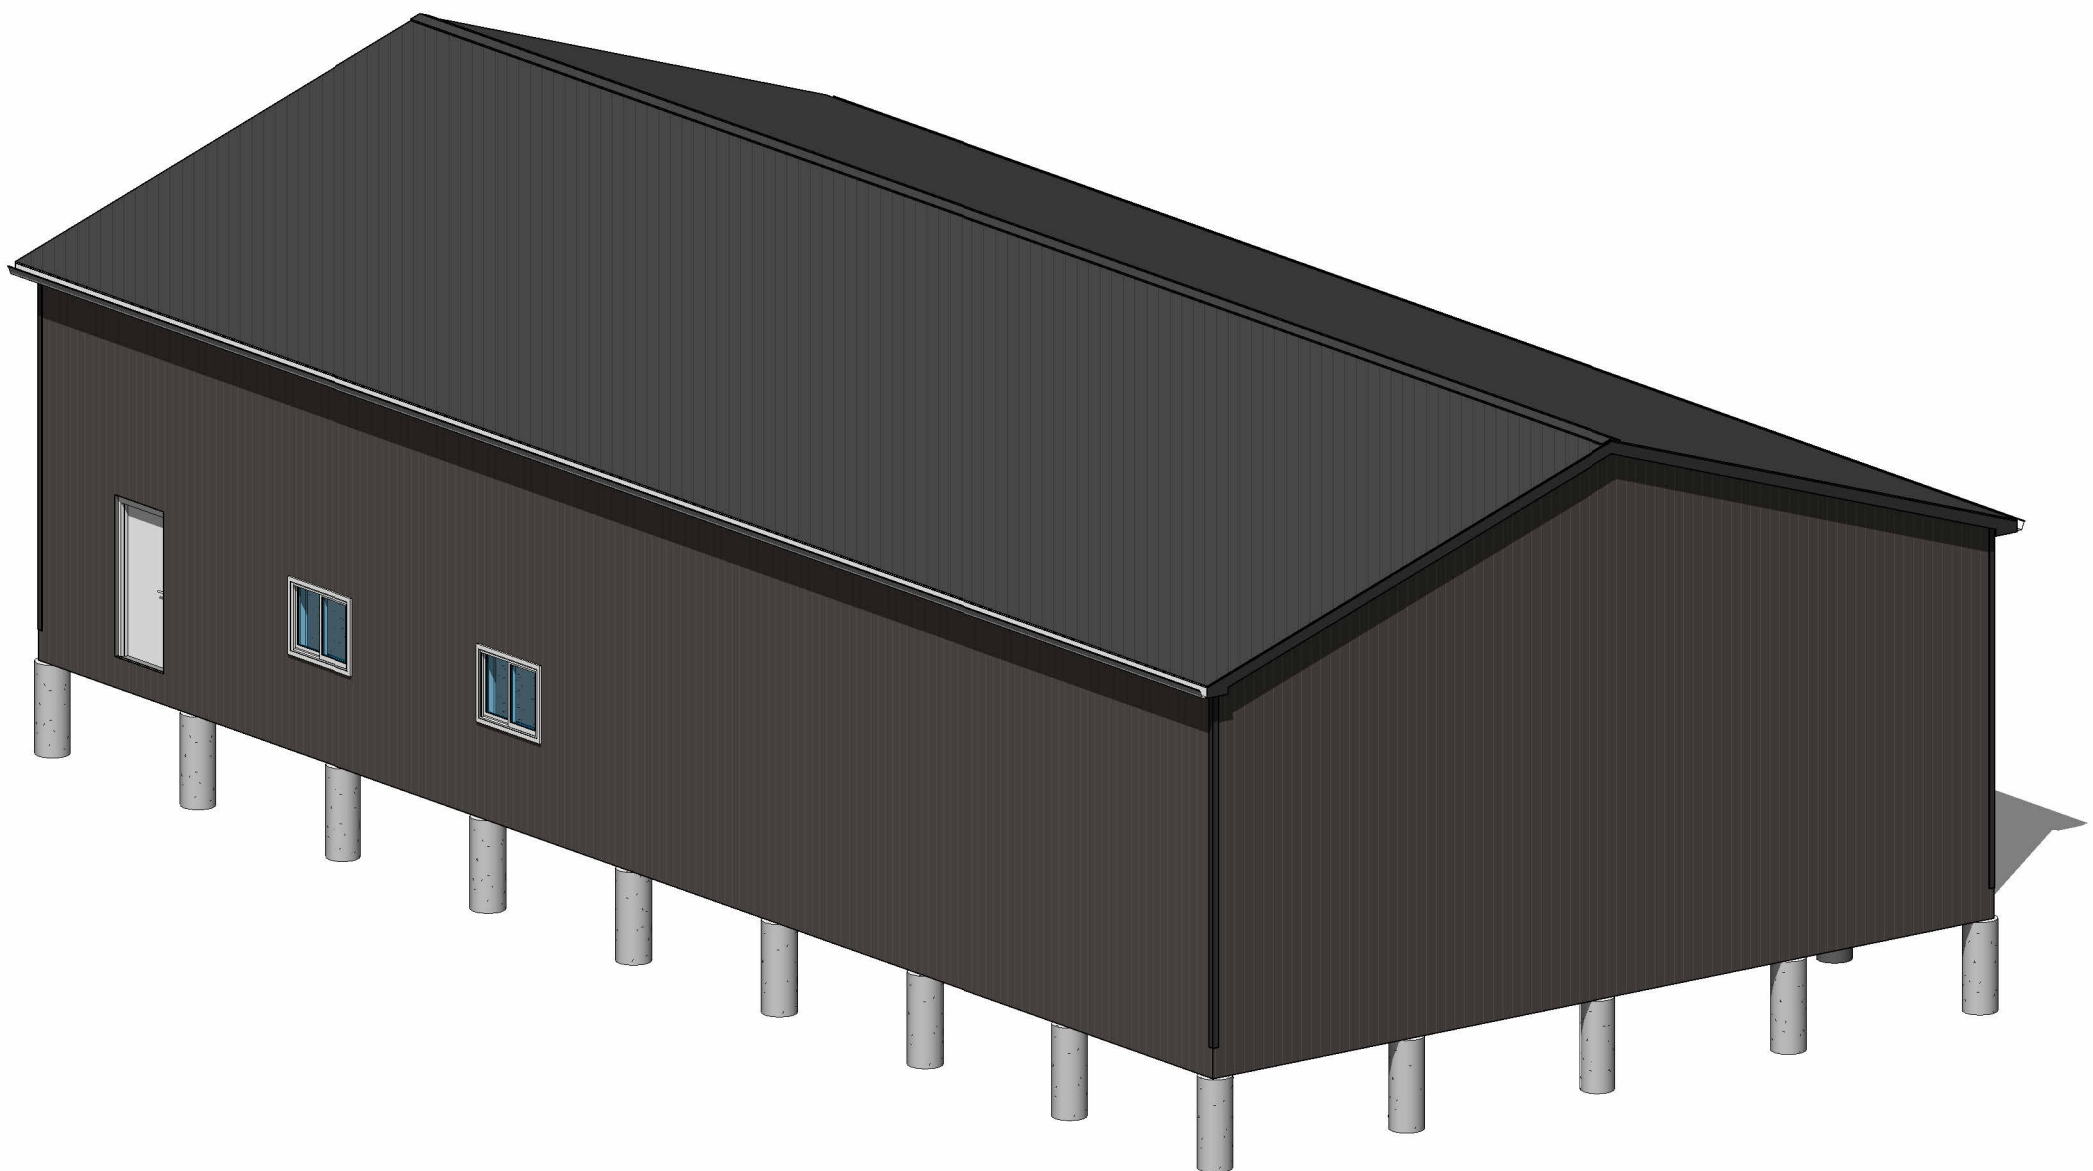

3 REAR VIEW
A0.00

ARCHITECTURAL	
NO.	SHEET NAME
A0.01	SITE PLAN
A0.02	GENERAL NOTES (STRUCT)
A1.02	FLOOR PLAN
A2.01	ELEVATION
A2.02	ELEVATION
A3.01	ARCHITECTURAL DETAILS
A3.02	ARCHITECTURAL ROOF DETAILS
A3.03	WASHROOM DETAILS
A4.01	SECTION 'A'

STRUCTURAL	
NO.	SHEET NAME
F1.01	SLAB EDGE PLAN
F2.01	ELEVATIONS
F3.01	FOUNDATION DETAILS
F5.01	SECTIONS
S1.01	POST PLAN
S1.02	TRUSS & BRACING LAYOUT
S2.01	STRUCTURAL ELEVATIONS
S2.02	STRUCTURAL ELEVATIONS
S2.03	STRUCTURAL ELEVATIONS
S2.04	STRUCTURAL ELEVATIONS
S3.01	DETAILS
S3.02	DETAILS

PROJECT DESCRIPTION:
DETACHED 1 STOREY ACCESSORY BUILDING

JURISDICTION: NORFOLK COUNTY
LOT ZONING: AGRICULTURAL
ZONING BYLAW: ZONING BYLAW 1-Z-2014
SECTION 3 - ACCESSORY FOR RESIDENTIAL USE

LOT AREA: 2 ACRES
MAXIMUM LOT COVERAGE: 200 m²
FRONT YARD SETBACK: NOT IN FRONT YARD
SIDE YARD SETBACK: 1.2 m
REAR YARD SETBACK: 1.2 m
MAXIMUM BUILDING HEIGHT: 8 m

	DOOR TAG
	WINDOW TAG
	WALL TAG
	REVISION TAG
	ROOM NAME & NUMBER
	ELEVATION NUMBER & SHEET NUMBER
	View Name 1/8" = 1'-0"
	DETAIL NUMBER SHEET NUMBER
	SECTION NUMBER SHEET NUMBER
	PROJECT LEGEND 1/4" = 1'-0"

20 ST ELIZABETH CRES
COURTLAND, ON
N0J 1E0
P: 226 931 1865
E: MHDESIGN.TALK@GMAIL.COM
W: M-H.DESIGN



GENERAL NOTES
THE BUILDING IS DESIGNED IN ACCORDANCE WITH THE 2012 ONTARIO BUILDING CODE AND ALL UP TO DATE AMENDMENTS.

LOADS:
a) SNOW S_s = 1.2 kPa (DEAD LOAD = 0.4 kPa)
S_r = 0.4 kPa
C_d = 0.8
C_s = 0.92
I_s = 0.9
S = 1.16 kPa / 24.2 psf
b) WIND q₅₀ = 0.47 kPa
P = AS PER 2020 NBCC FIGURE 4.1.7.6-A

NO.	DESCRIPTION	DATE
REVISION TABLE		

JOHAN, EVA
AND WILLY WALL
692 4TH CONCESSION ROAD
WALSINGHAM, ONTARIO
NOE 1X0

COVER SHEET

PROJECT NUMBER	25-001
DATE	2025/01/20
DRAWN BY	MH
CHECKED BY	LDO
SCALE	1/4" = 1'-0"

A0.00