
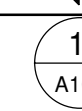
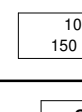
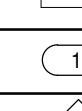
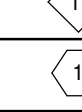
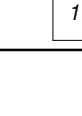



ABBREVIATIONS

AC.	ACOUSTIC	GA.	GAUGE
ADJ.	ADJUSTABLE	GB.	GRAB BAR
ALT.	ALTERNATE	GL.	GLASS
ALUM.	ALUMINUM	GLULAM	GLUE-LAMINATED
ANOD.	ANODIZED	GR.	GRADE
APPROX.	APPROXIMATE	GWB	GYPSUM WALL BOARD
AVM	AIR/VAPOUR/MOISTURE	GWB.WR.	GYPSUM WALL BOARD - WATER RESISTANT
BD.	BOARD	HCW	HOLLOW CORE WOOD
BLDG.	BUILDING	HDR.	HEADER
BLK.	BLOCK	HD.WD.	HARD WOOD
BLKG.	BLOCKING	HHS	HAND HYGIENE SINK
BM.	BEAM	HM	HOLLOW METAL
BOT.	BOTTOM	HORIZ.	HORIZONTAL
CB	CATCH BASIN	HSS	HOLLOW STRUCTURAL SECTION
CG	CORNER GUARD	HTR.	HEATER
OG	CAST IN PLACE	HWT	HOT WATER TANK
CJ	CONTROL JOINT		
CL	CENTER LINE	ID	INSIDE DIAMETER
CLG.	CEILING	IF	INSIDE FACE
CMU	CONCRETE MASONRY UNIT	INSUL.	INSULATION
COL.	COLUMN	INT.	INTERIOR
COMP.	COMPACTED		
CONC.	CONCRETE	JT.	JOINT
CONT.	CONTINUOUS	LAV.	LAVATORY
CORR.	CORRIDOR	LG.	LONG
COV.	COVER		
C/W	COMPLETE WITH	M.STD.	METAL STUD
CS/CI	CONTRACTOR SUPPLY-CONTRACTOR INSTALL	m	METER
DEG.	DEGREE	MATL.	MATERIAL
DF	DRINKING FOUNTAIN	MAX.	MAXIMUM
DIA.	DIAMETER	MDF	MEDIUM DENSITY FIBREBOARD
DIAG.	DIAGONAL	MECH.	MECHANICAL
DN.	DOWN	MEZZ.	MEZZANINE
DRY.	DRYER (CLOTHES)	MH	MANHOLE
DWG(S).	DRAWINGS	MIN.	MINIMUM
EA.	EACH	MISC.	MISCELLANEOUS
EA.F	EACH FACE	mm	MILLIMETERS
ELEC.	ELECTRICAL	MO	MASONRY OPENING
ELEV.	ELEVATION	MR	MOISTURE RESISTANT
EQ.	EQUAL	MS	MOP SINK
ES	EXPOSED STRUCTURE		
EXIST.	EXISTING	NIC	NOT IN CONTRACT
EXP.	EXPOSED	NO.	(#)NUMBER
EXP.JT.	EXPANSION JOINT	NTS	NOT TO SCALE
EXP.N	EXPANSION	O/C	ON CENTER
EXTR.	EXTERIOR	O.D.	OUTSIDE DIAMETER
EXT.GR.	EXTERIOR GRADE	O.S.F.	OUTSIDE FACE
FOC	FACE OF CURB	OPP.	OPPOSITE
F	FILM	OSB	ORIENTED STRAND BOARD
FD	FLOOR DRAIN	OS/OI	OWNER SUPPLY-OWNER INSTALL
FDN.	FOUNDATION	OS/CI	OWNER SUPPLY-CONTRACTOR INSTALL
FE	FIRE EXTINGUISHER	OS/VI	OWNER SUPPLY-VENDOR INSTALL
FEC	FIRE EXTINGUISHER CABINET	OWSJ	OPEN WEB STEEL JOIST
FHC	FIRE HOSE CABINET		
FIN.GD.	FINISHED GRADE	PAT.	PATIENT
FLR.	FLOOR	PERIM.	PERIMETER
FP	FIRE PLACE	PG	PLATE GLASS
FRP	FIBER REINFORCED PLASTIC	PJ	PARALAM JOIST
FRS	FIRE SHUTTER	PLY.	PLYWOOD
FTG.	FOOTING	PLAM	PLASTIC LAMINATE
FURR.	FURRING	POLY.	POLYETHYLENE
F/O	FACE OF	PP	POWER POLE
		PR.	PAIR
		PSC	PARALAM STEEL CONNECTION
		PSF	PRESSED STEEL FRAME
		PT	PRESSURE TREATED
		PTD	PAPER TOWEL DISPENSER
		PROJ.	PROJECTION
		PVC	POLYVINYL CHLORIDE
		PVCW	POLYVINYL CHLORIDE WALLCOVERING


SYMBOL LEDGEND	
	BUILDING SECTION
	DETAIL
	GRID HEAD
Room name 	ROOM TAG
	KEYNOTE TAG
	DOOR TAG
	WALL TAG
	WINDOW TAG
	FLOOR TAG

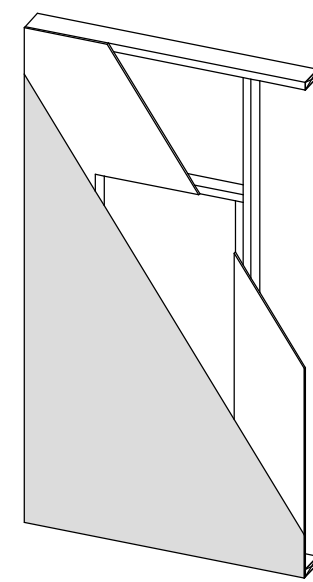

STEP 1
- WOOD FRAME WALL WITH
OSB AND HOUSEWRAP

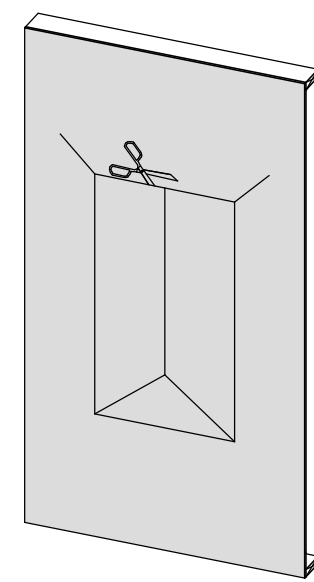


STEP 2
-MODIFY "I" CUT IN HOUSE WRAP

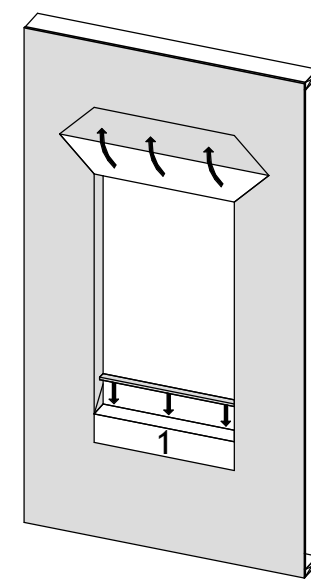


STEP 3


- INSTALL FIRST PIECE OF ADHESIVE-BACKED FLASHING
- HOUSEWRAP FOLDED IN; ALTERNATELY, TUCK HEAD FLAP UNDER
- INSTALL WOOD BACKDAM

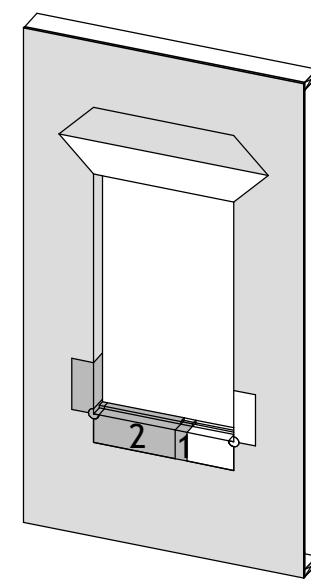


STEP 4
- INSTALL SECOND PIECE OF
ADHESIVE-
BACKED FLASHING
- INSTALL CORNER FLASHING
PATCHES
AT SILL

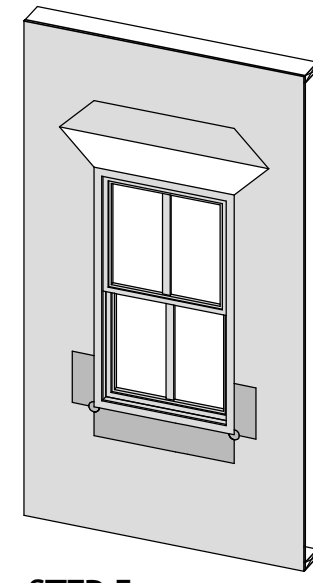


STEP 5
- INSTALL WINDOW PLUMB, LEVEL
AND SQUARE PER
MANUFACTURER'S
INSTRUCTIONS

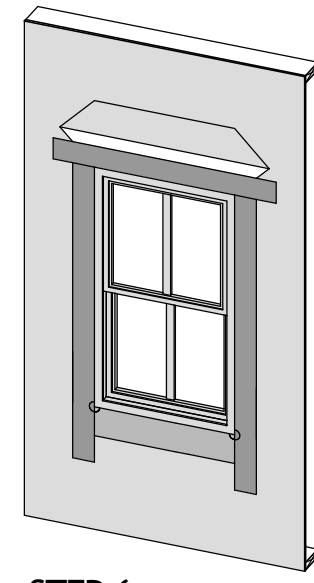


STEP 6
- INSTALL JAMB FLASHING FIRST
THEN
HEAD FLASHING

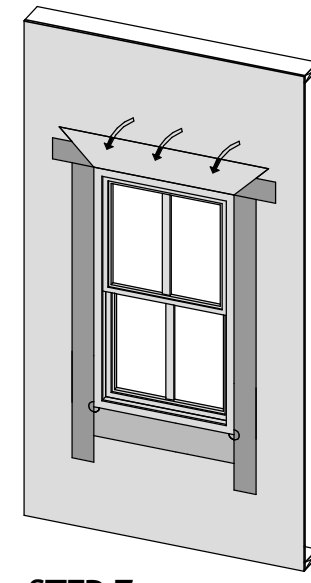


STEP 7
- FOLD DOWN HOUSEWRAP AT HEAD

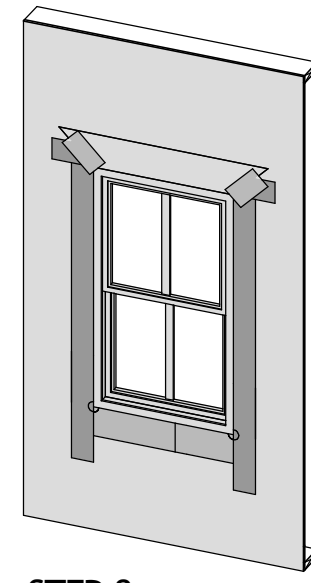


STEP 8
- APPLY CORNER PATCHES AT HEAD

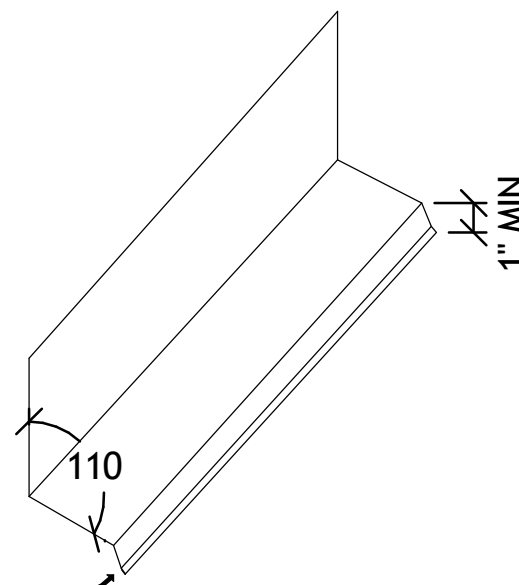


STEP 1
- FOLDED METAL FLASHING
(MIN. 6% SLOPE)
- FOLD FRONT FACE OF
FLASHING TO CREATE SAFETY
EDGE

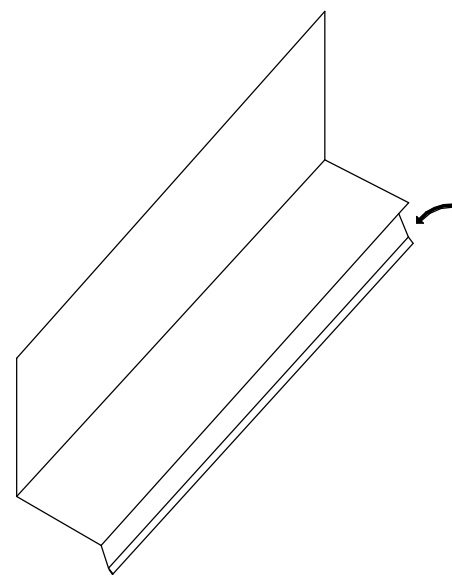

STEP 2
- NOTCH OUT FRONT FACE ONLY

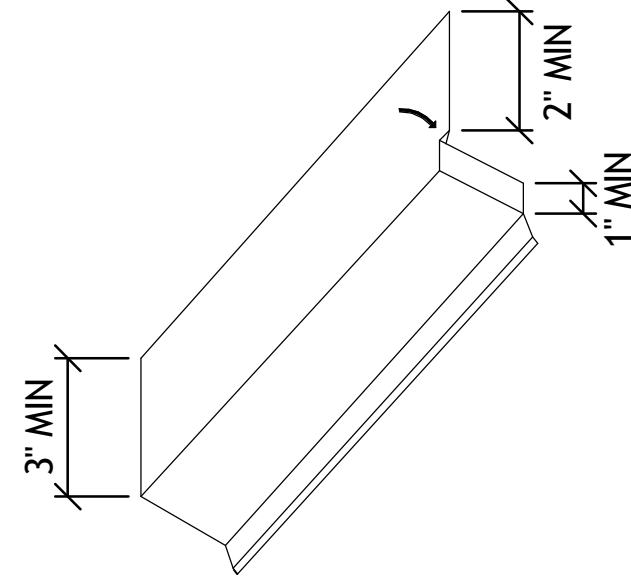

STEP 3
- FOLD UP EDGE
- DO NOT CRIMP BACK FOLD
TIGHT SO POSITIVE SLOPE IS
MAINTAINED

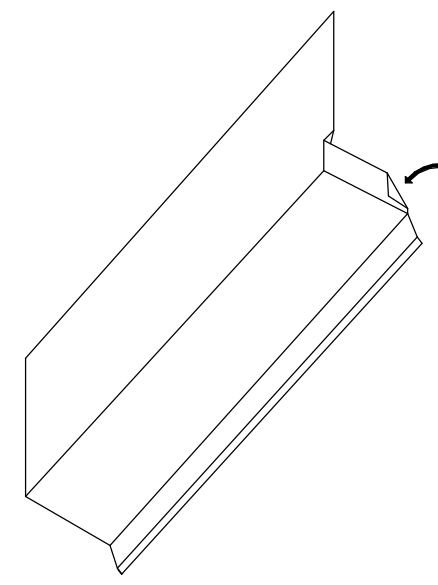

STEP 4
- FOLD OVER OUTER CORNER
TO CREATE SAFETY EDGE
- END DAM MUST EXTEND TO
FACE OF CLADDING



Dimensions to Face of Foundation or Framing Stud UNO.		
This plan and design is the property of WSA Engineering (2012) Ltd. and is solely for the use of the client with which WSA Engineering (2012) Ltd. has entered into agreement with, and cannot be used in whole or in part without the written consent of WSA Engineering (2012) Ltd.		
DO NOT SCALE DRAWINGS Written dimensions shall govern.		
All dimensions to be verified on site by the contractor/builder. Report all errors or additions to the owner or designer prior to proceeding with the work		
 Habitat for Humanity® Southeast BC		
C	FEB 22/22	FOR BUILDING PERMIT
1	FEB 09/22	DETAILS ADDED, FLOOR PLAN UPDATES, SCHEDULES UPDATED AS PER DESIGN REVIEW MEETING
B	FEB 02/22	FOR DEVELOPMENT PERMIT
1	JAN 24/22	DETAILS ADDED, UNIT C ADJUSTED
A	JAN 21/22	ISSUED FOR COORDINATION
No.	Date	Issue/Revision

Professional Engineer Stamp:	
------------------------------	--

 **ENGINEERING (2012) LTD.**
Civil • Structural
2248 Columbia Ave. Castlegar, B.C. V1N 2X1 Ph: (888) 617-4927

Project	
Habitat for Humanity	
560 8th Street Castlegar, BC	
Drawing	
ADDITIONAL NOTES	

Date	11/13/21	Project No.	
Designed	RS/ST	C21001 - 022	
Drawn	RS	Scale	C21001 - 022 A1
Checked	ST/DW	As indicated	
Approved	DS	Sheet No.	Issue/Rev.
		A1.02	A

A red rectangular stamp with rounded corners, tilted diagonally. The text inside is in red, uppercase letters. The top line reads "FOR BUILDING PERMIT" and the bottom line reads "NOT FOR CONSTRUCTION".