




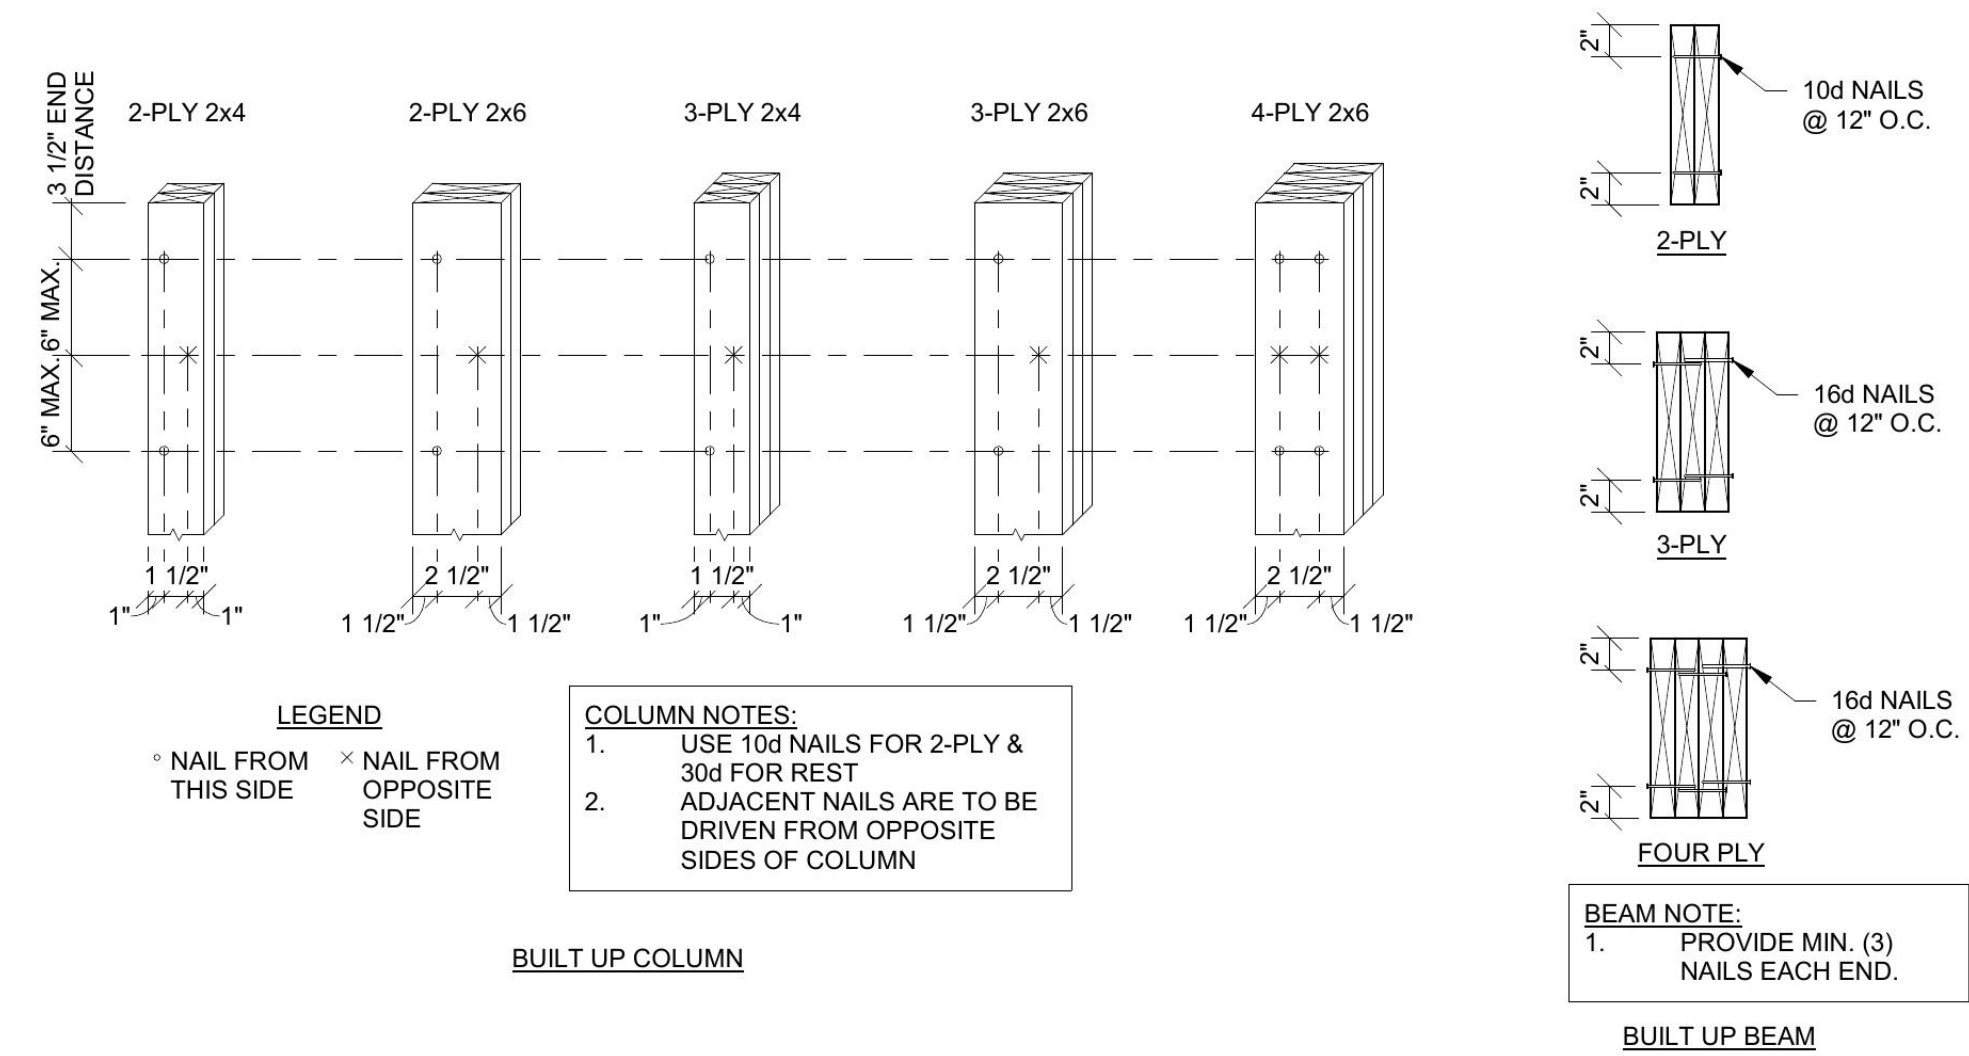


1 TYPICAL BUILT-UP MEMBERS
1" = 1'-0"

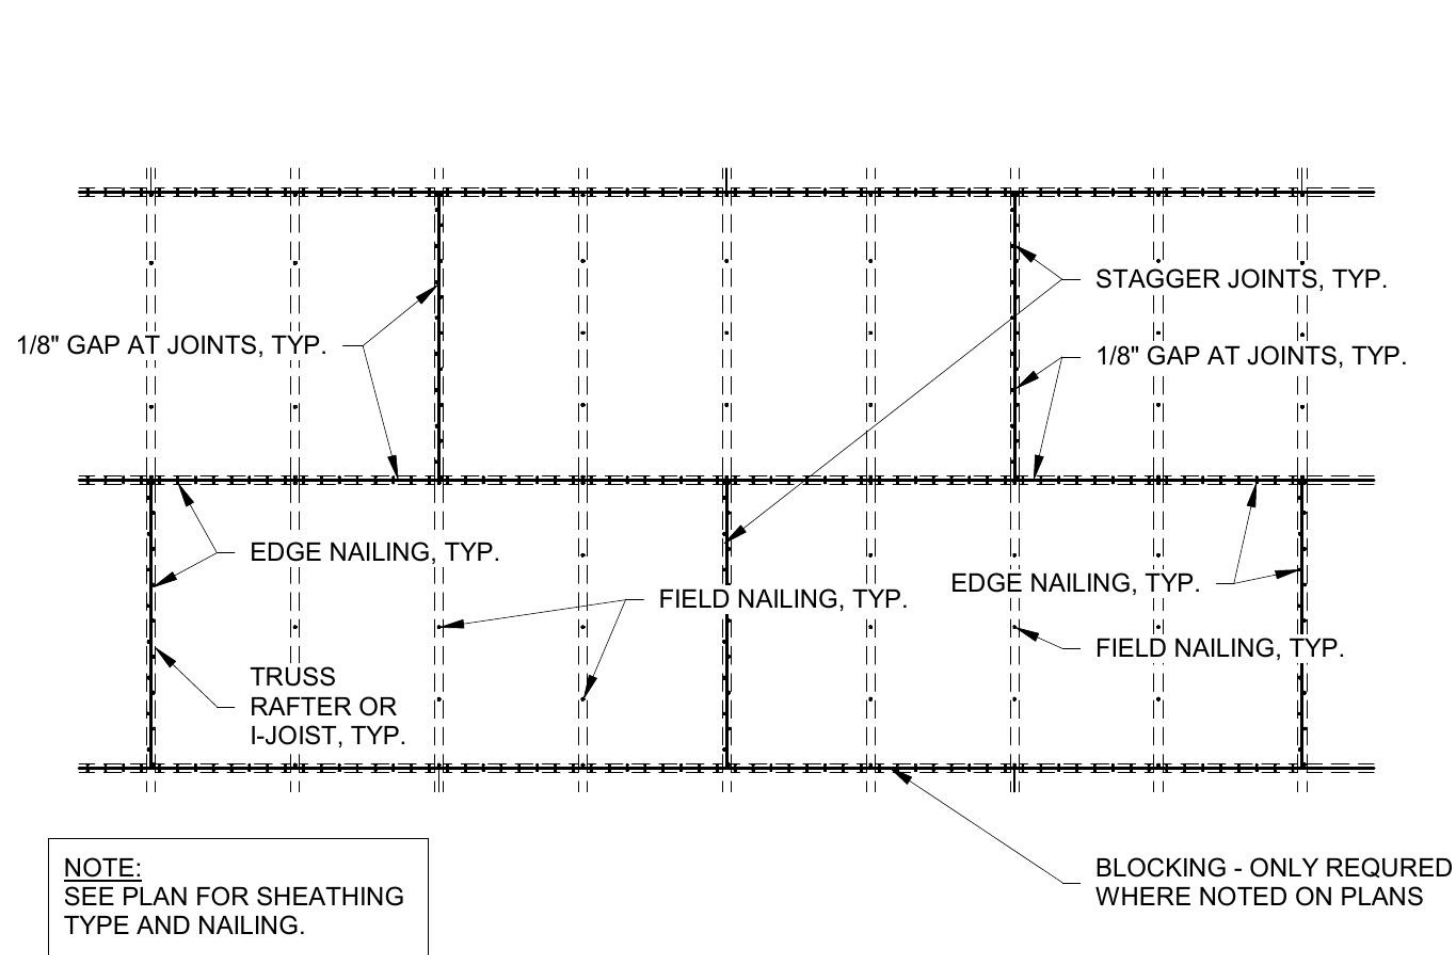


2 DIAPHRAGM NAILING
3/8" = 1'-0"

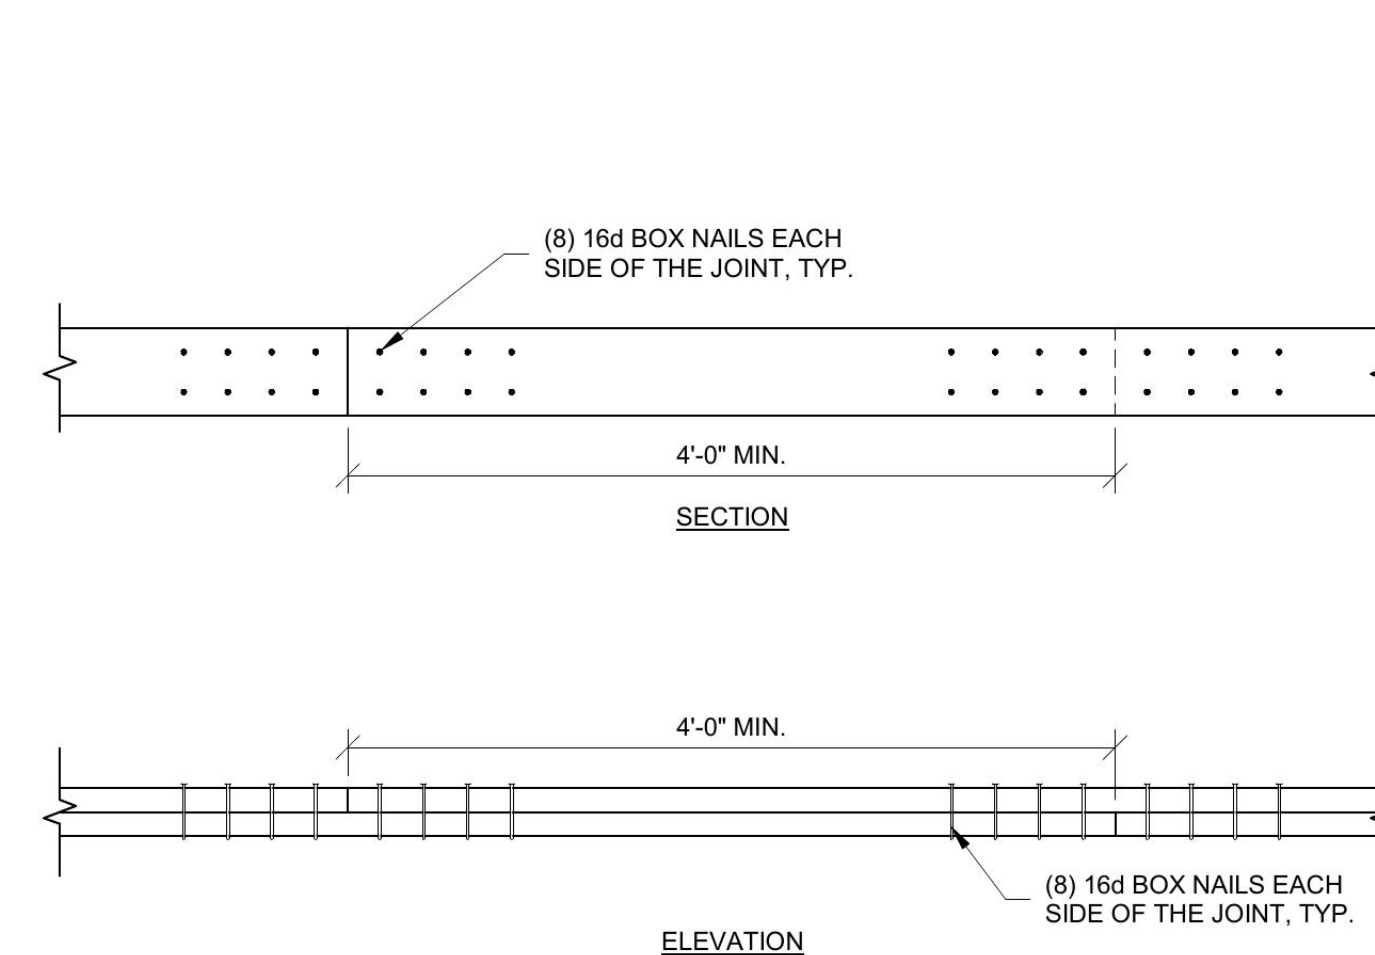


3 TOP PLATE SPLICE
1" = 1'-0"

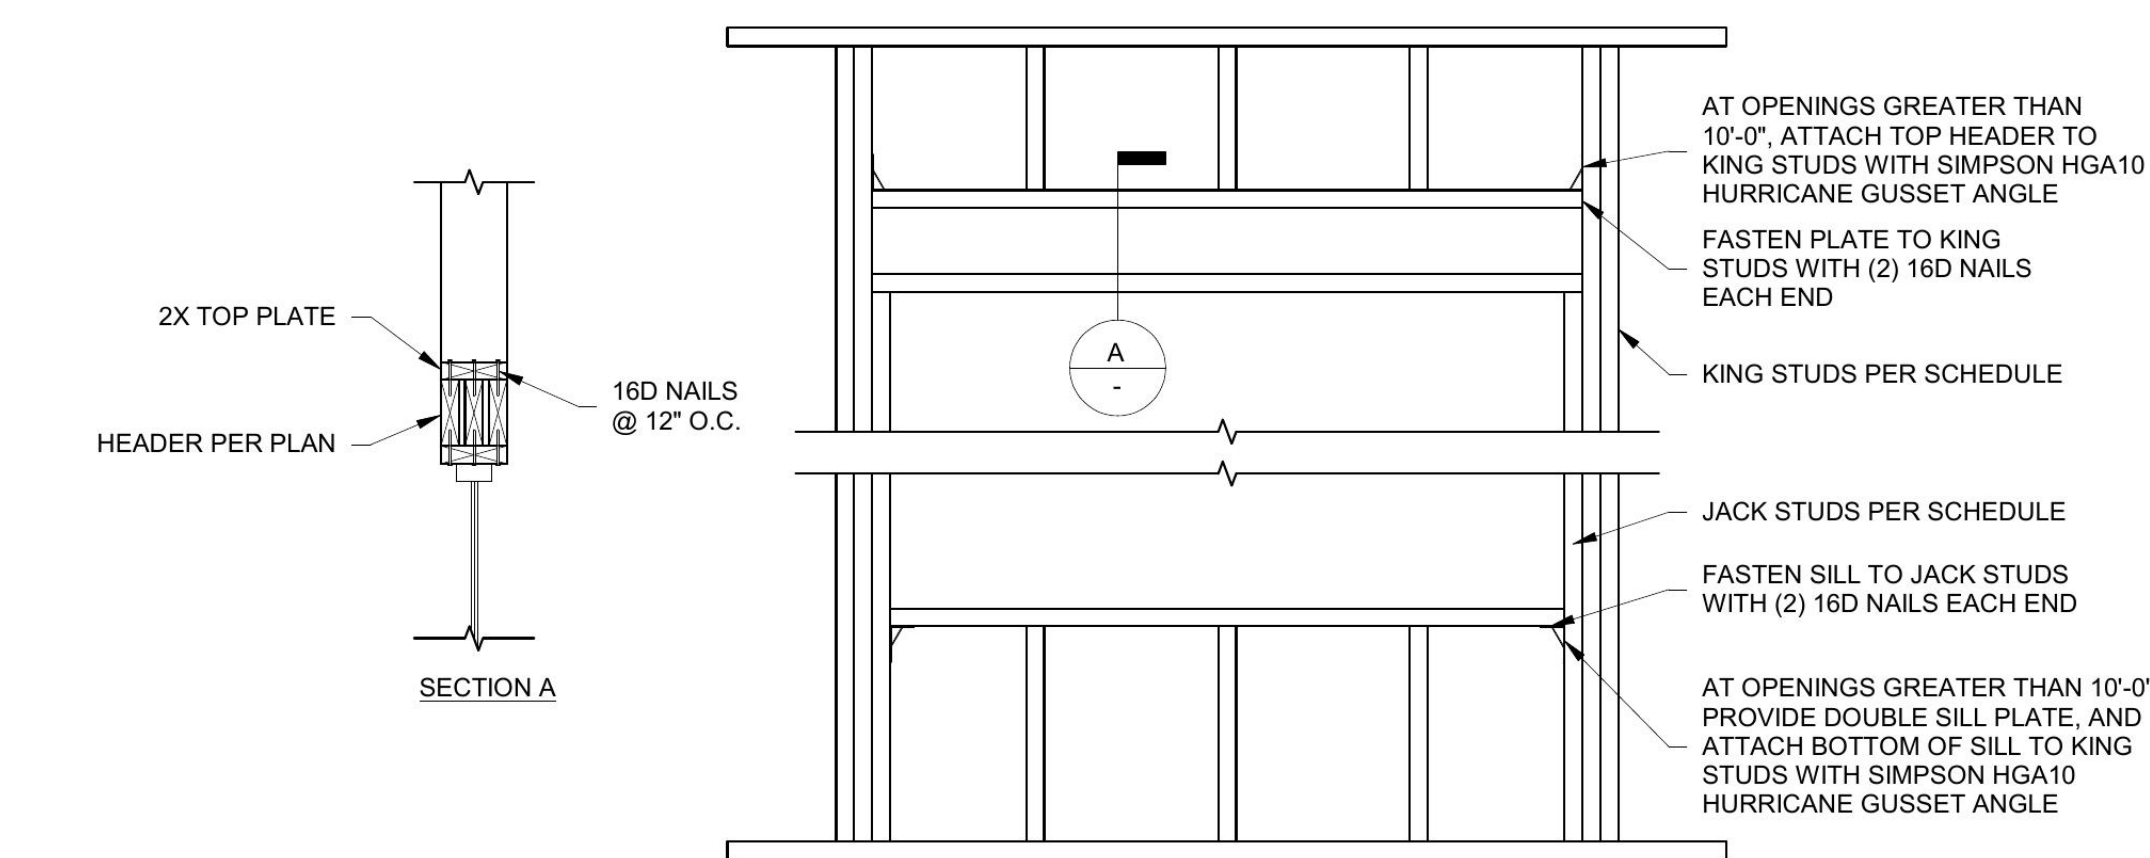


4 FRAMING AT OPENING
3/4" = 1'-0"

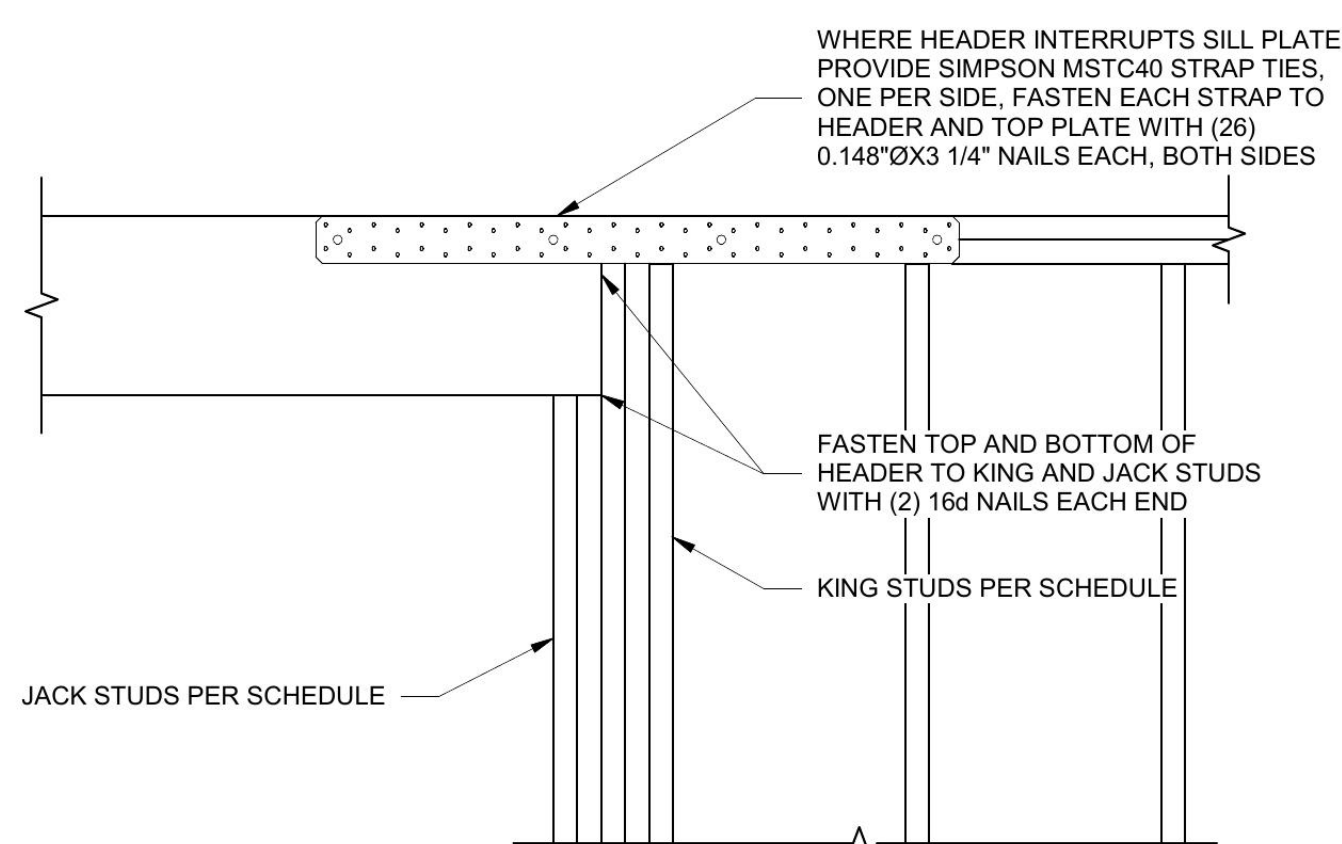


5 FRAMING AT OPENING - RAISED HEADER
1" = 1'-0"

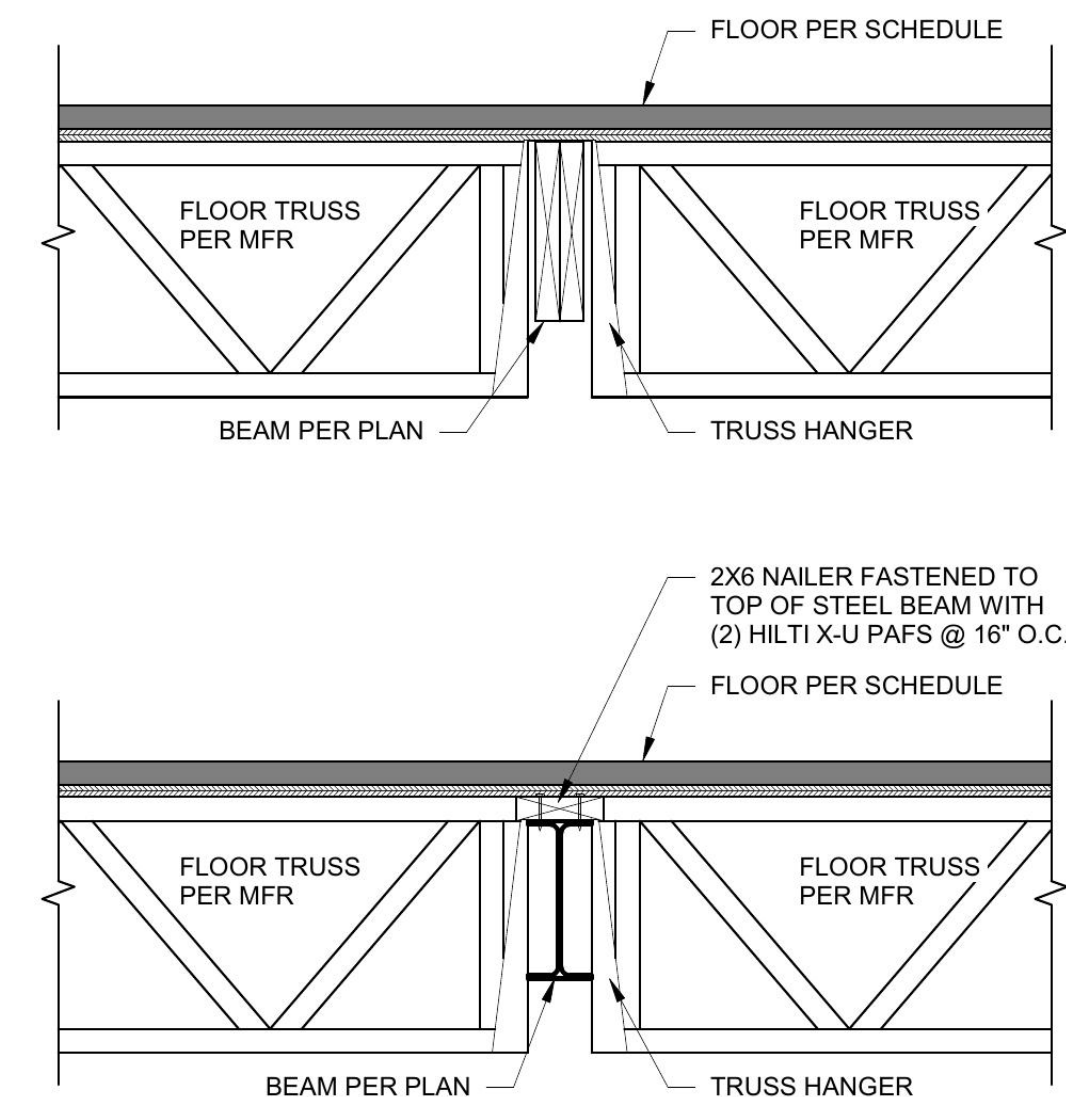


6 FLOOR TRUSS TO BEAM
1" = 1'-0"

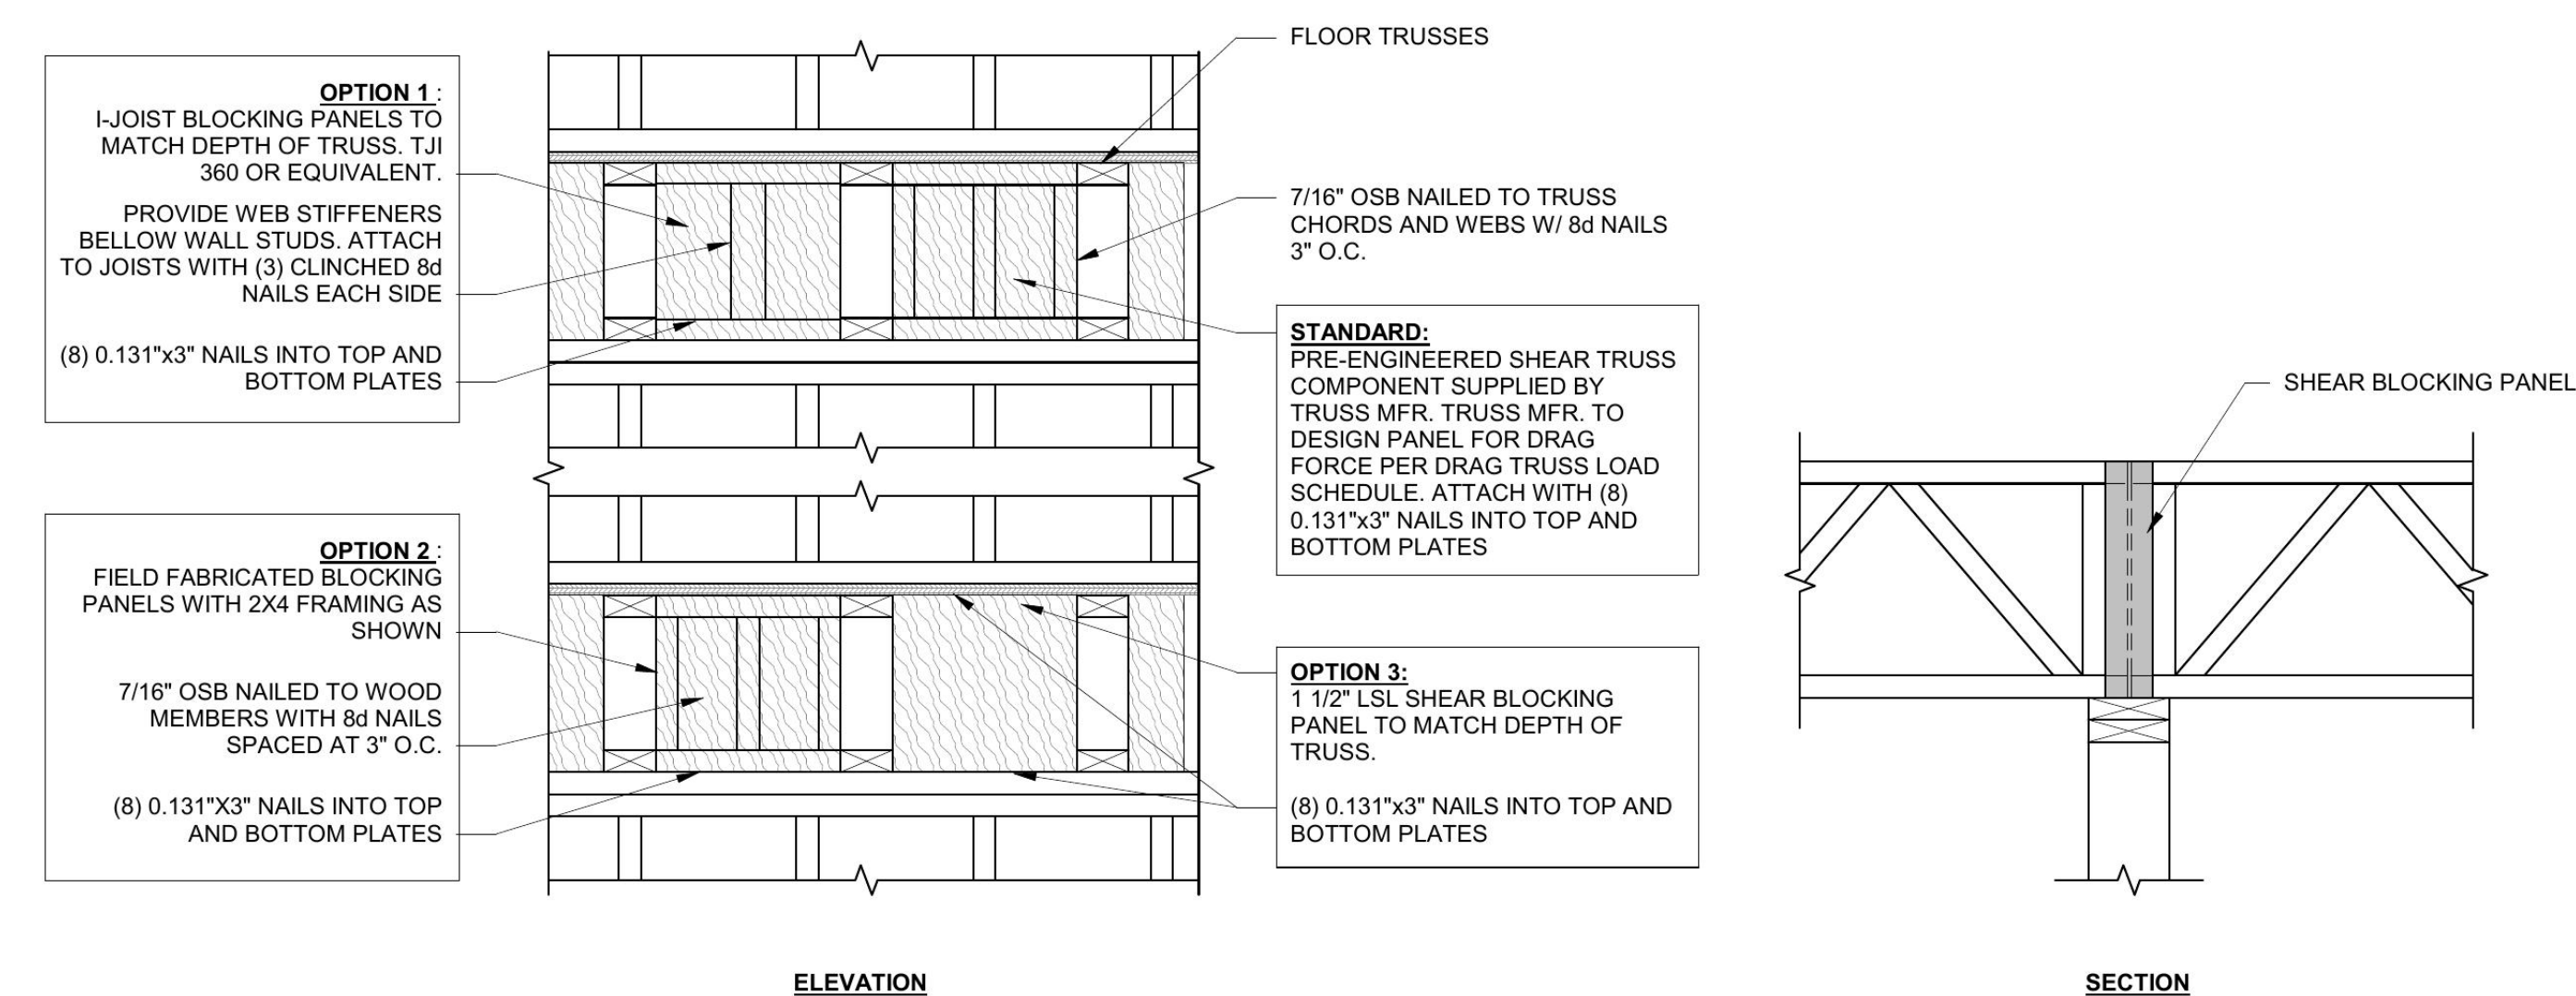

7 SHEAR BLOCKING OPTIONS AT SHEAR WALLS

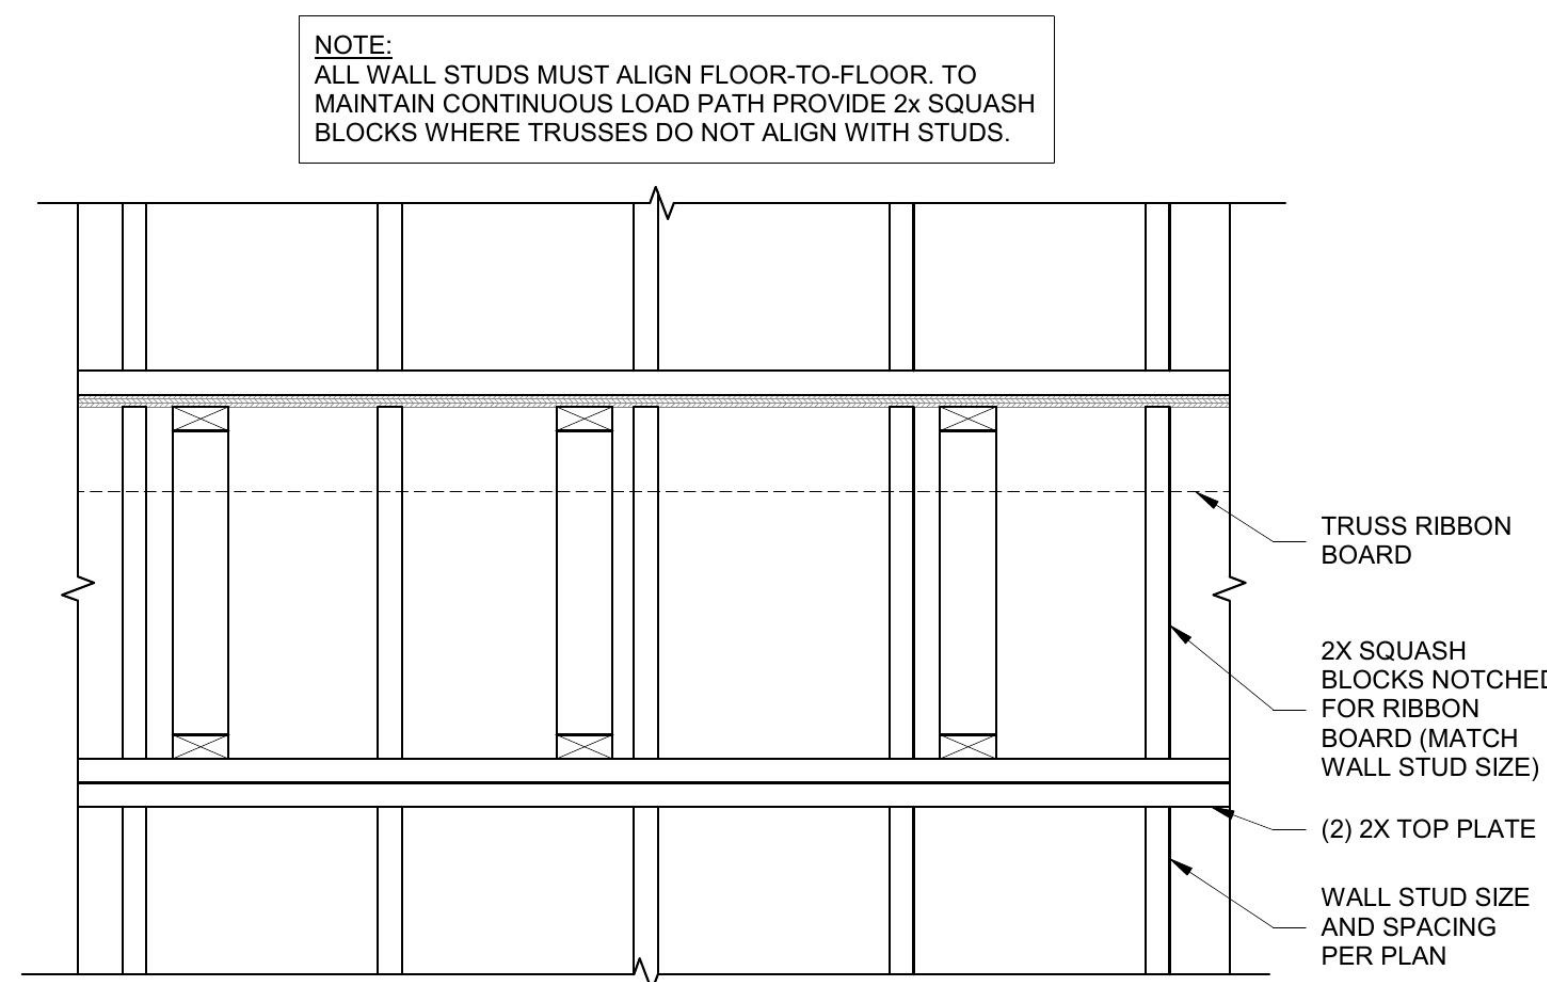

8 TYPICAL WALL FRAMING ELEVATION

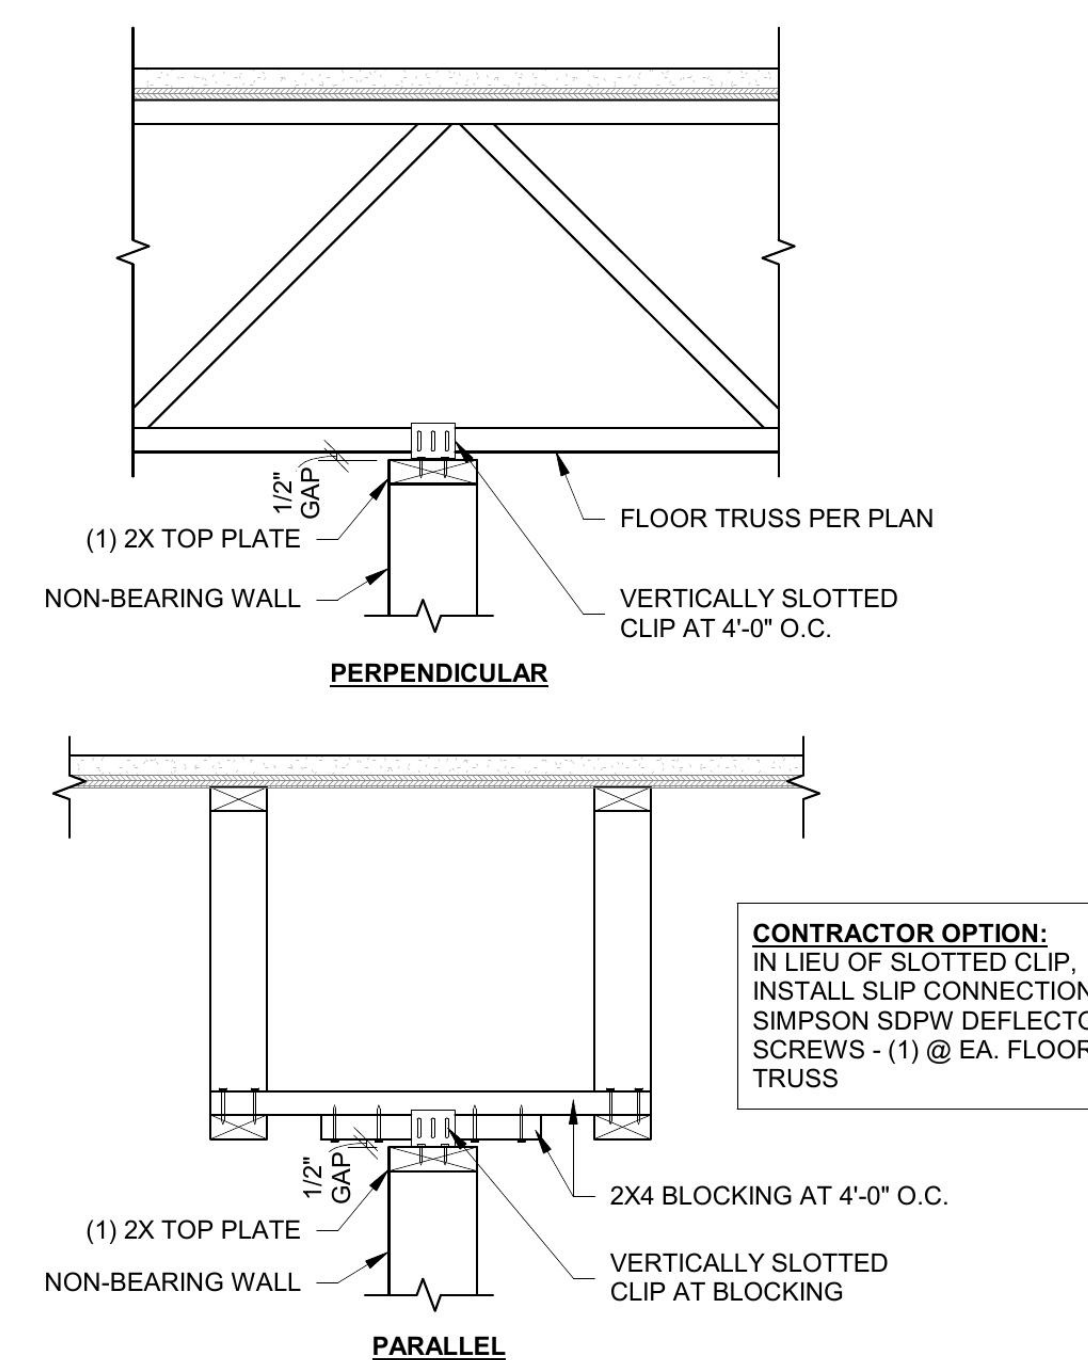

9 NON-BEARING WALL TO FLOOR TRUSS

No.	Description	Date

PROJECT NUMBER 2025001420	SET ISSUE DATE 08/01/2025
ENGINEER IWC	DRAWN BY CEL
CHECKED BY MDH	