
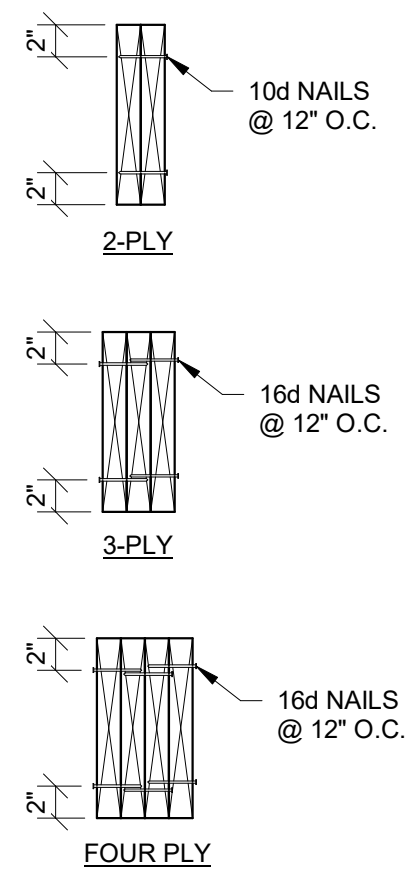


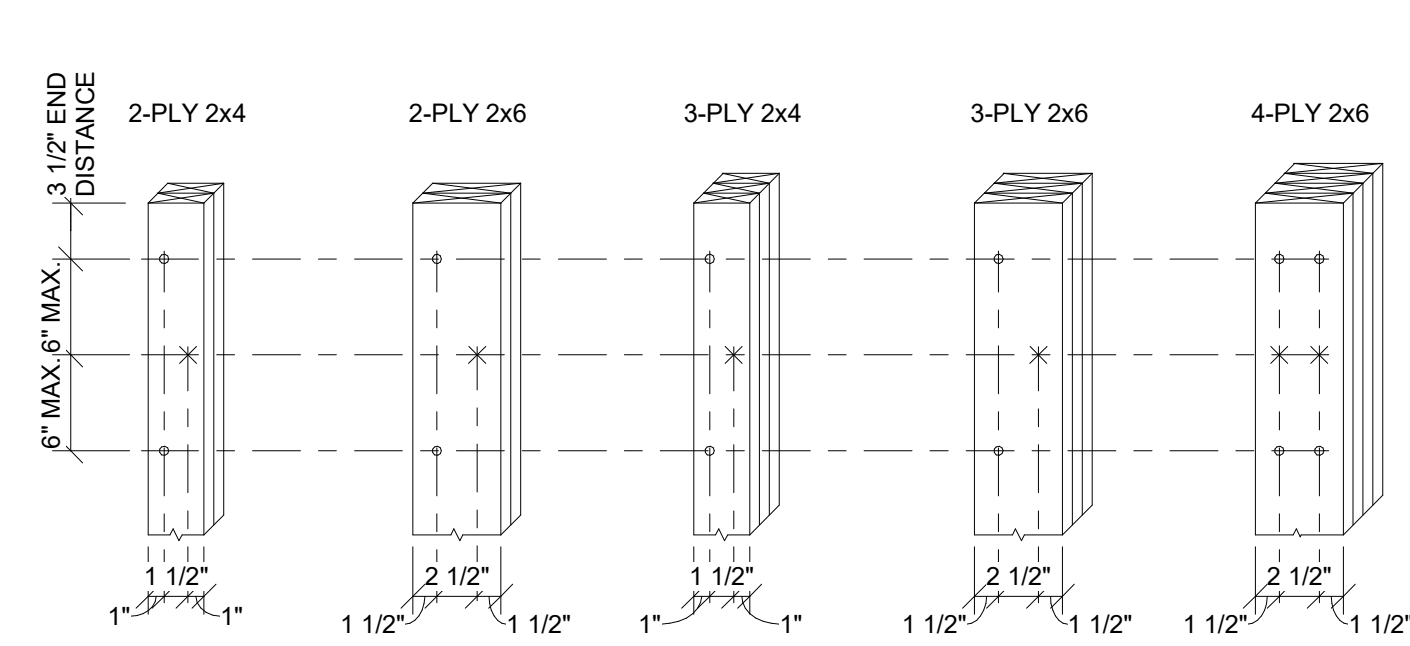

LEGEND
* NAIL FROM THIS SIDE
x NAIL FROM OPPOSITE SIDE


COLUMN NOTES:
1. USE 10d NAILS FOR 2-PLY & 3d FOR REST
2. ADJACENT NAILS ARE TO BE DRIVEN FROM OPPOSITE SIDES OF COLUMN

BUILT UP COLUMN

BEAM NOTE:
1. PROVIDE MIN. (3) NAILS EACH END.

BUILT UP BEAM



1 TYPICAL BUILT-UP MEMBERS
1" = 1'-0"

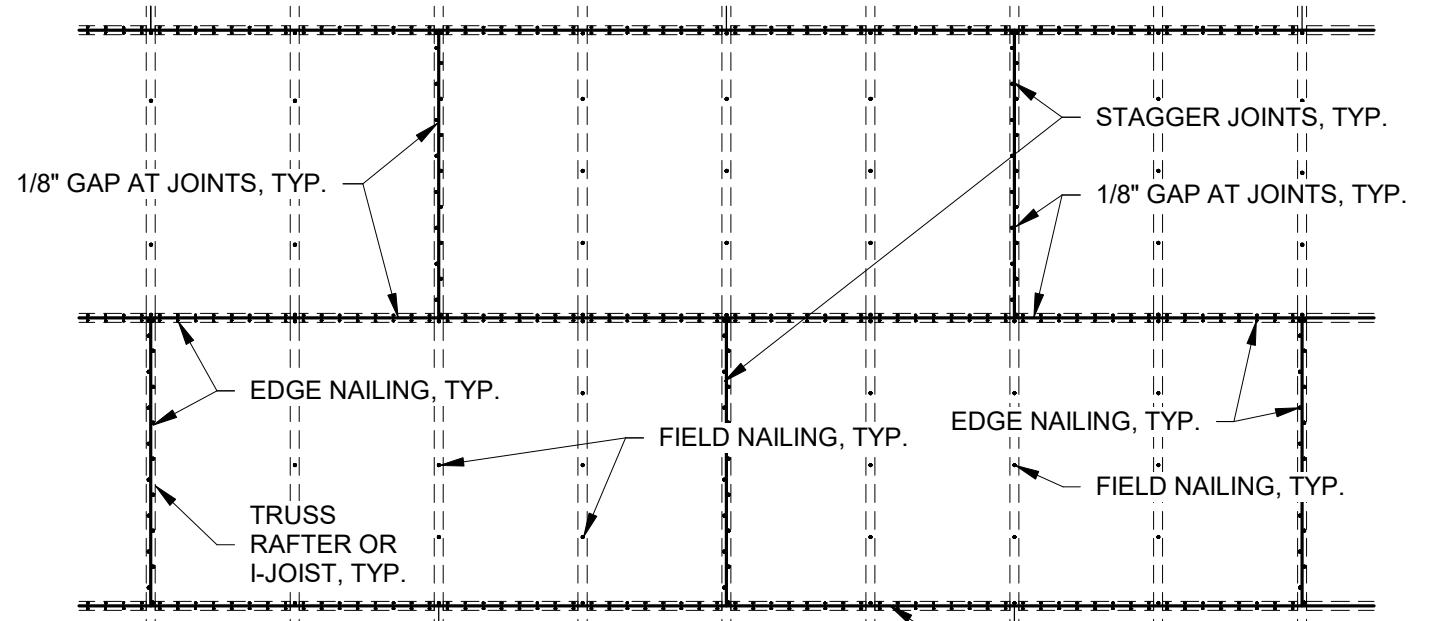


NOTE:
SEE PLAN FOR SHEATHING TYPE AND NAILING.

BLOCKING - ONLY REQUIRED WHERE NOTED ON PLANS


2 DIAPHRAGM NAILING
3/8" = 1'-0"

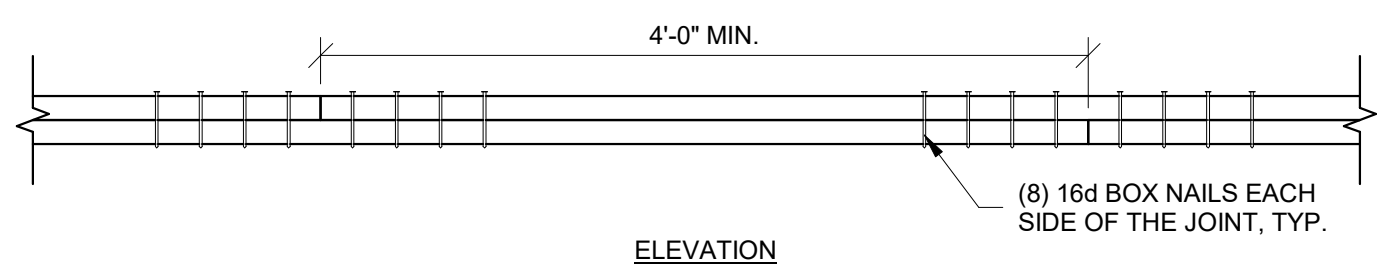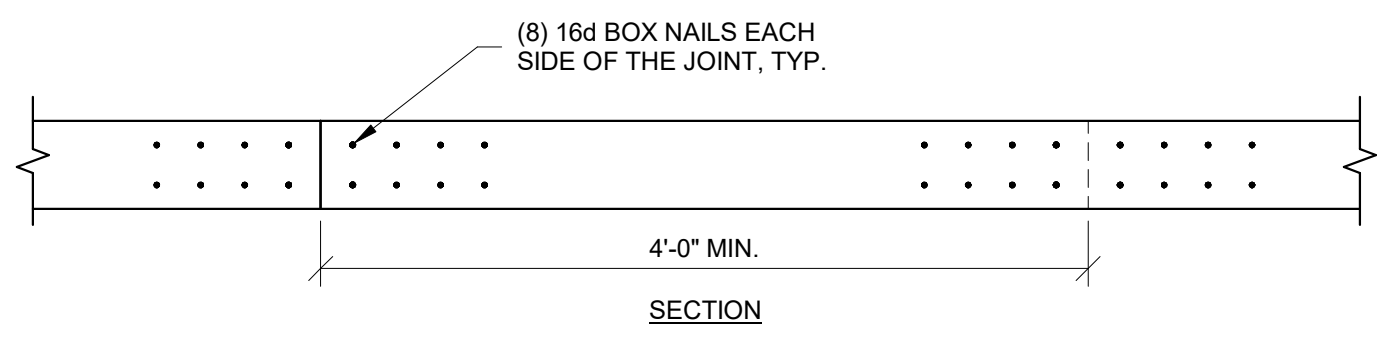



3 TOP PLATE SPLICE
1" = 1'-0"

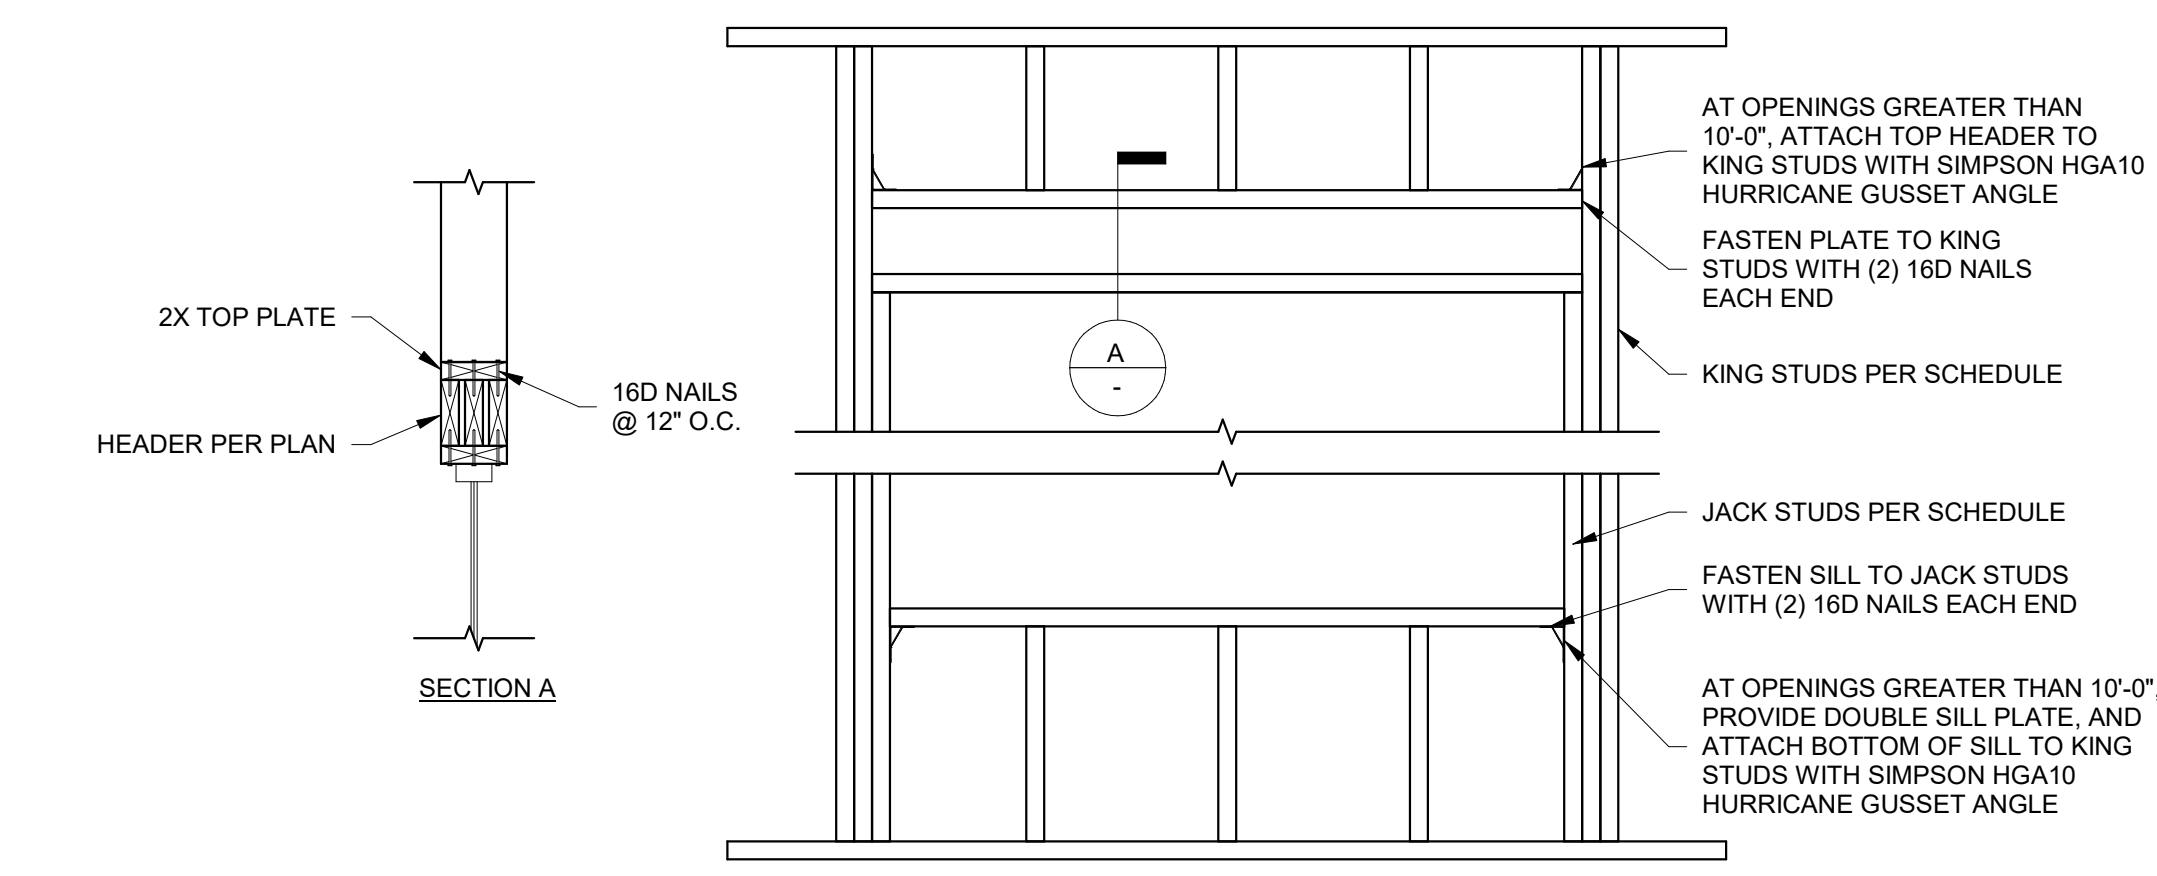


4 FRAMING AT OPENING
3/4" = 1'-0"

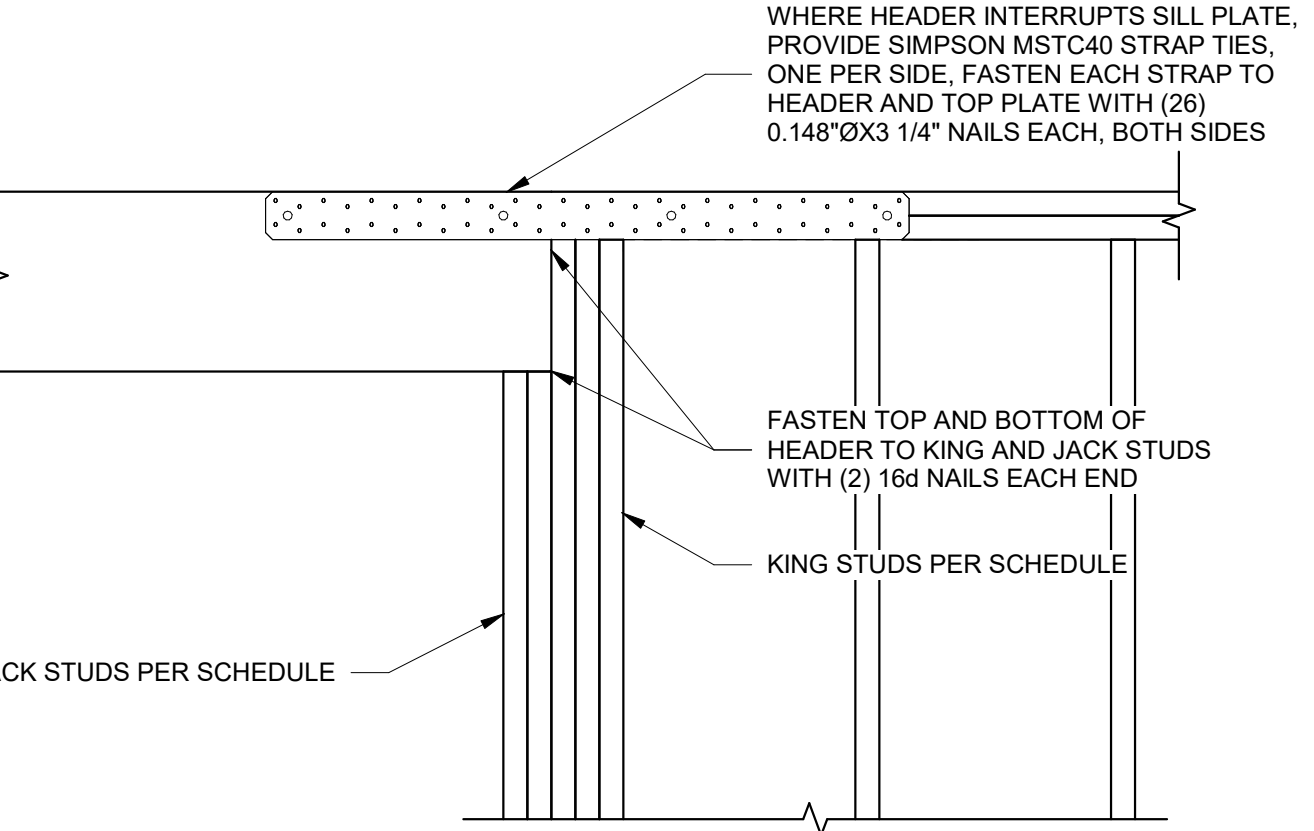


5 FRAMING AT OPENING - RAISED HEADER
1" = 1'-0"

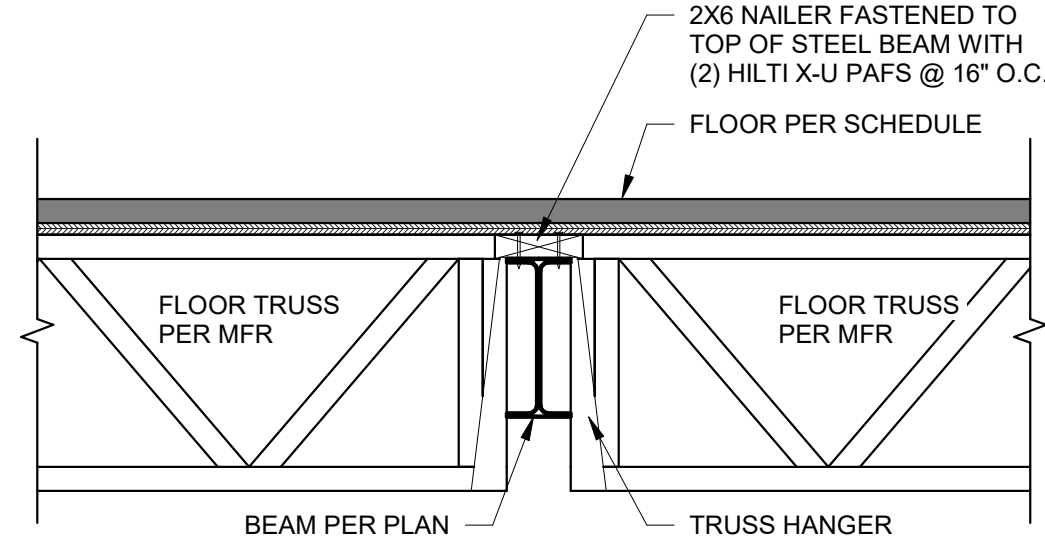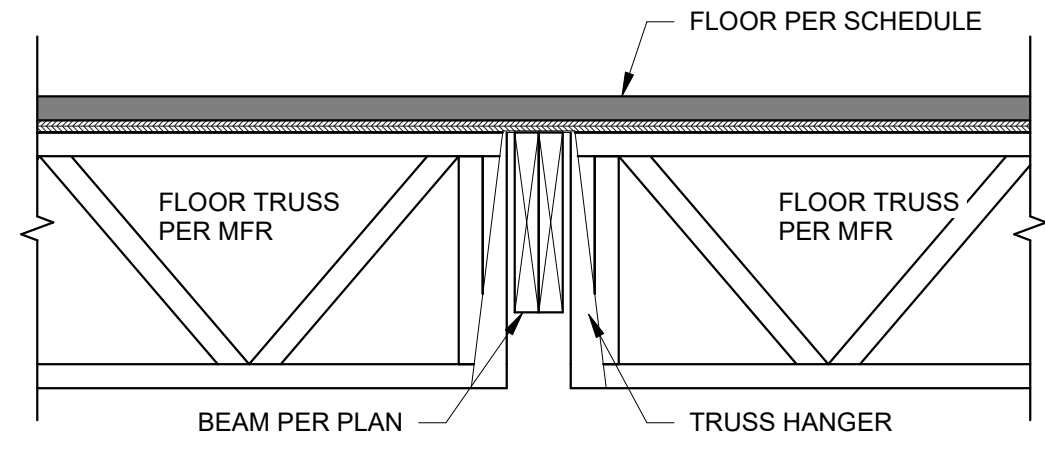


6 FLOOR TRUSS TO BEAM
1" = 1'-0"

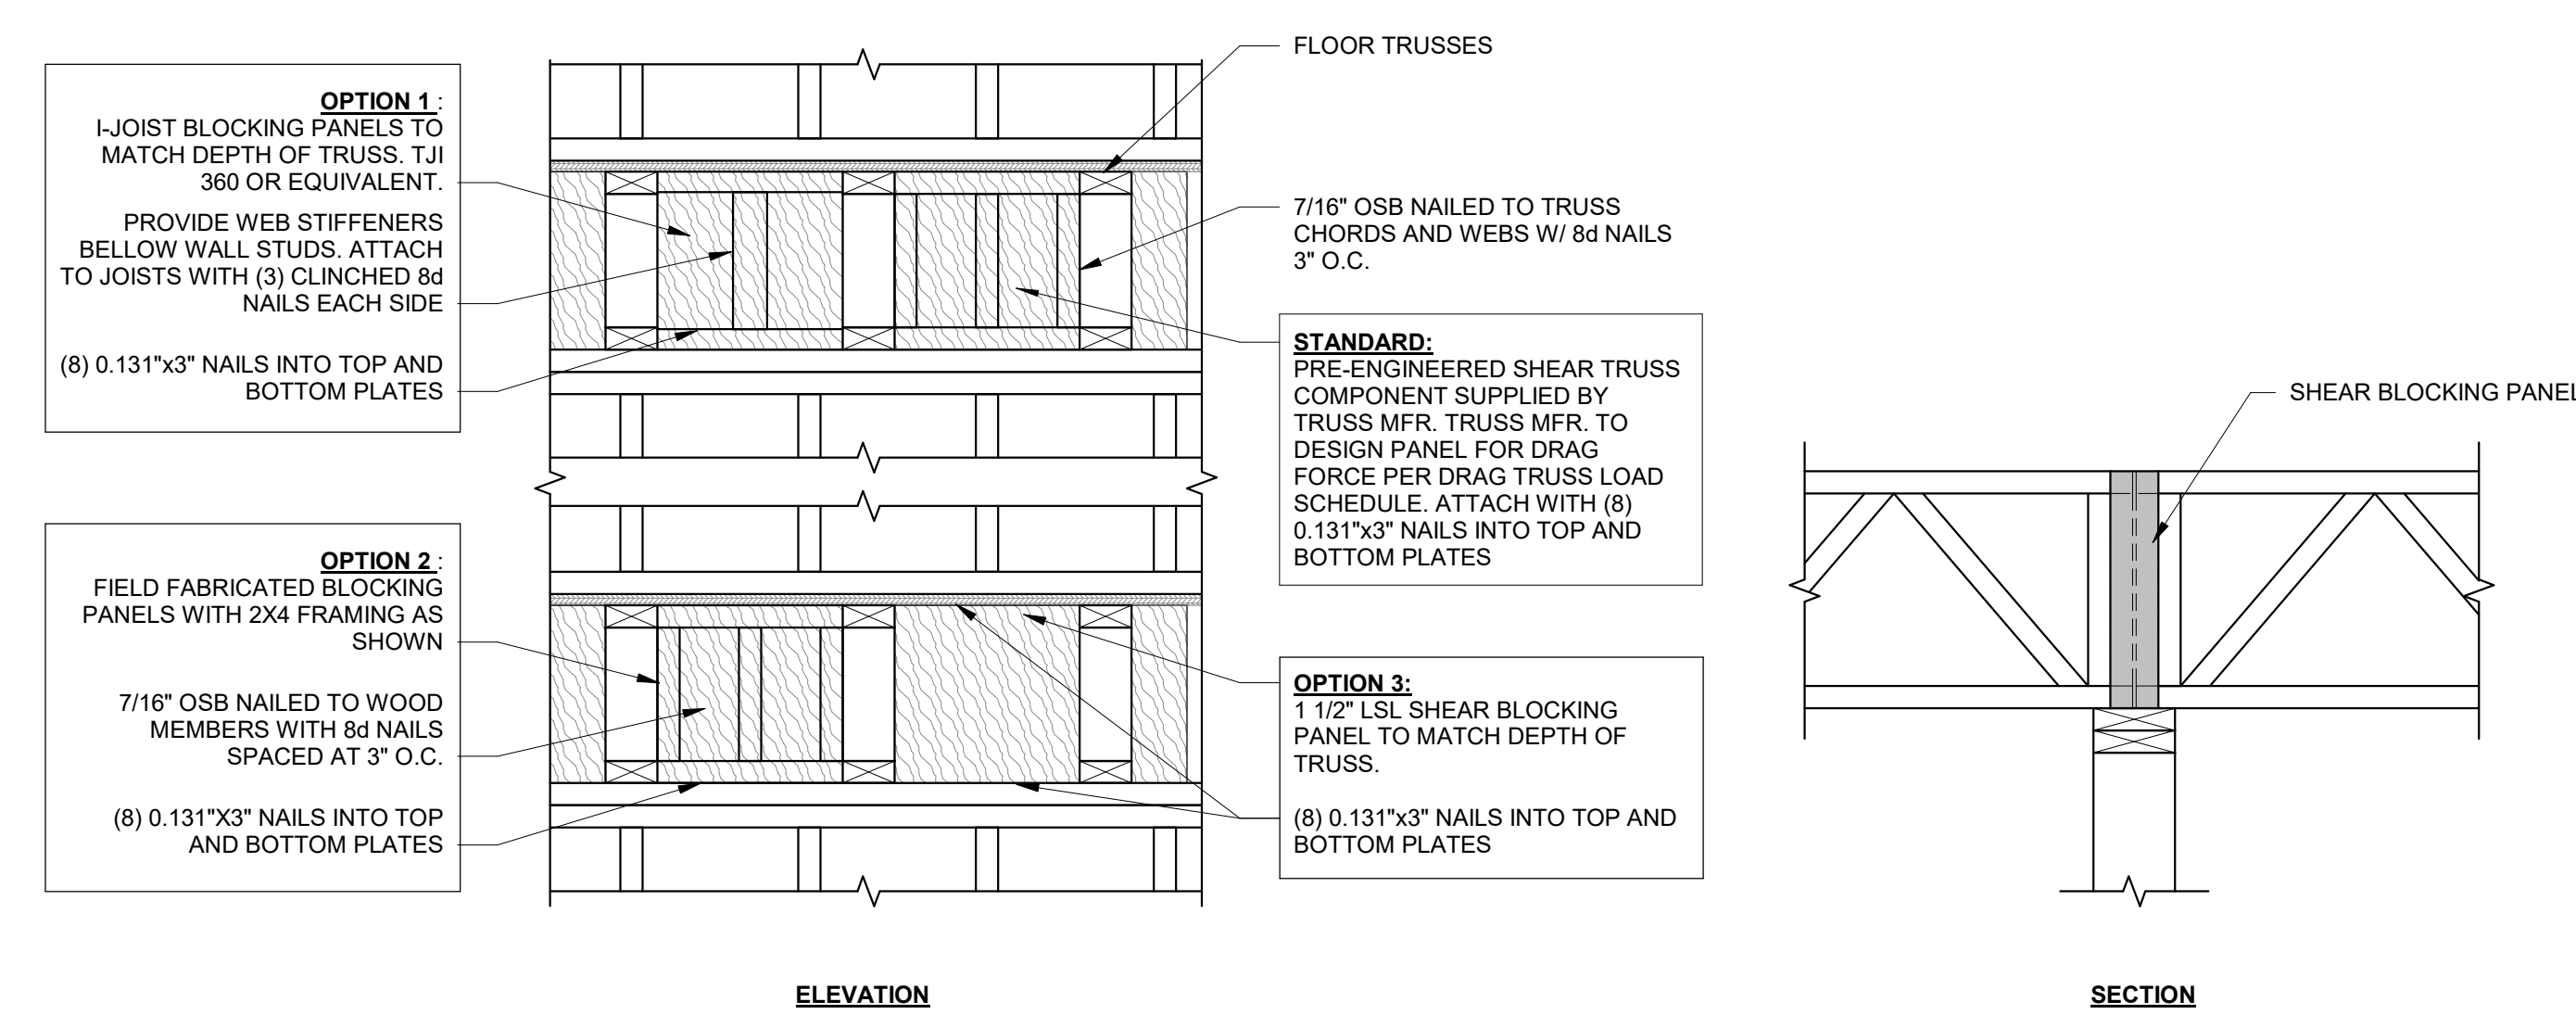

7 SHEAR BLOCKING OPTIONS AT SHEAR WALLS
1" = 1'-0"

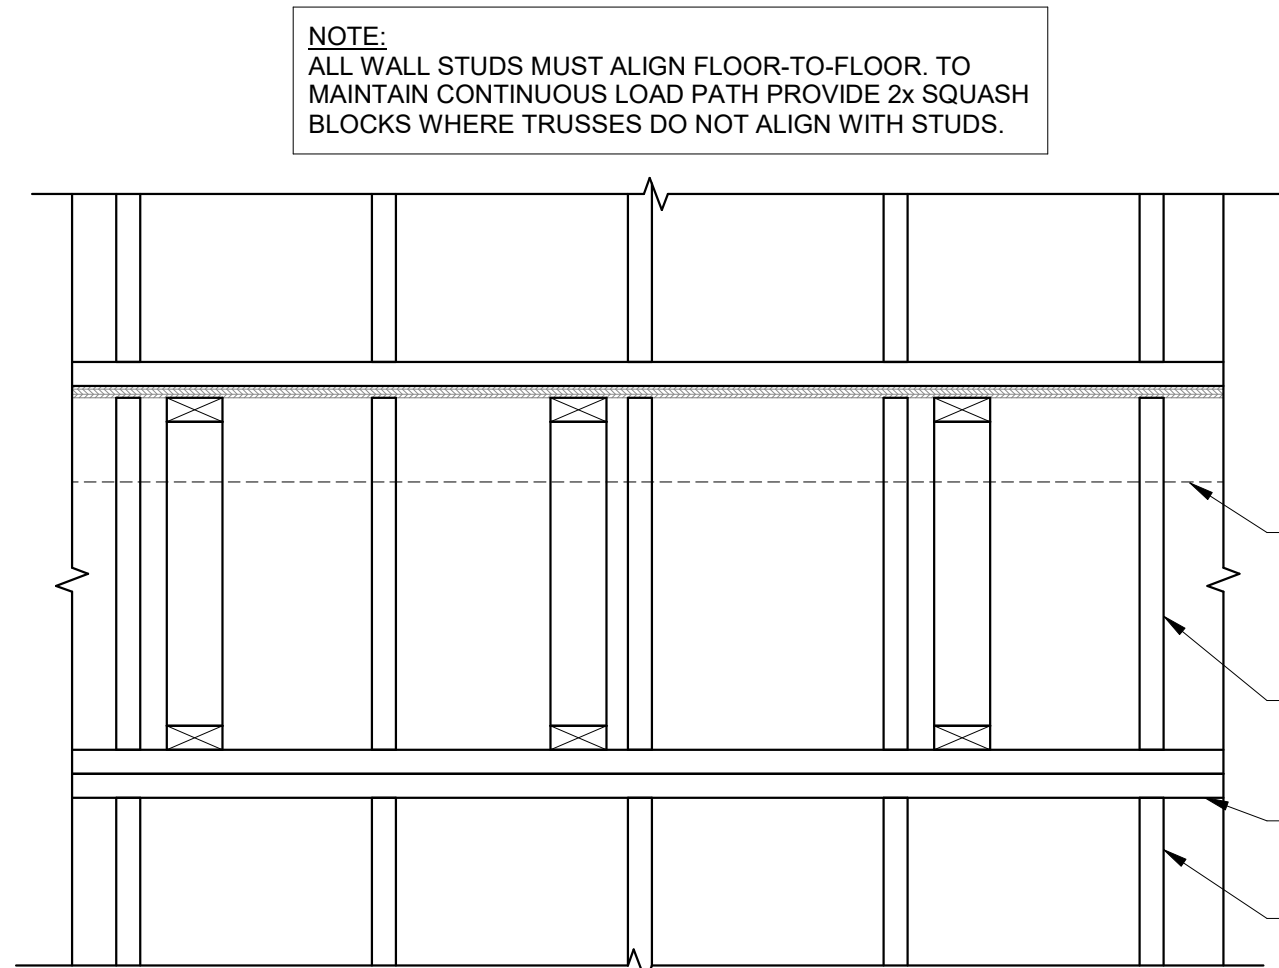


8 TYPICAL WALL FRAMING ELEVATION
1" = 1'-0"

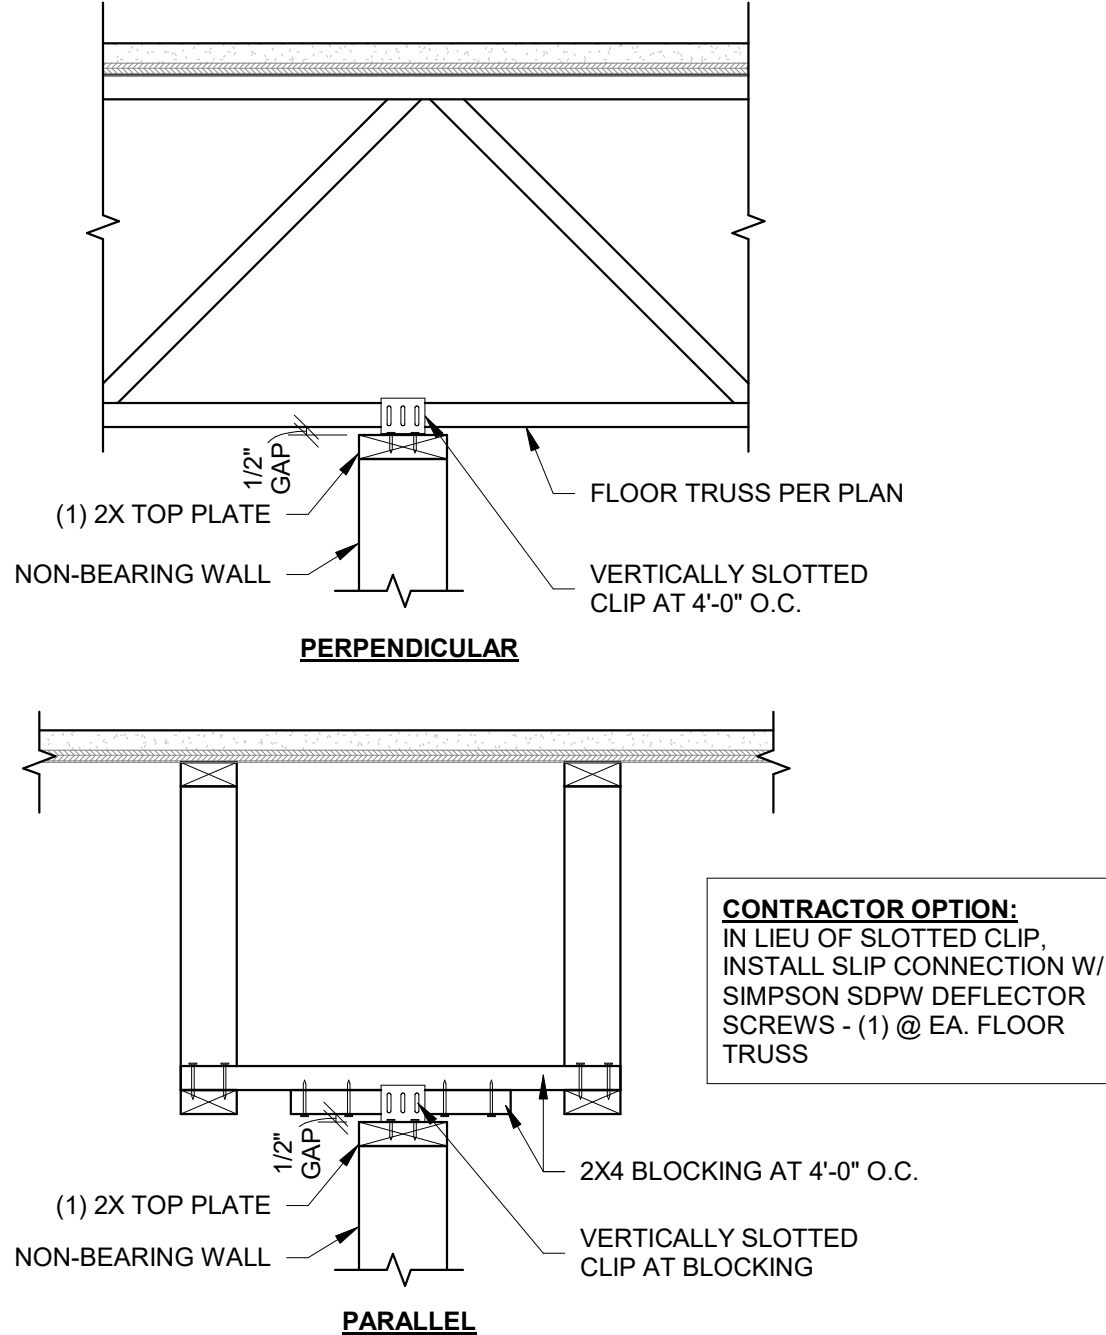

9 NON-BEARING WALL TO FLOOR TRUSS
1" = 1'-0"

NOTICE:
McClure Engineering Co. is not responsible or liable for any issues, claims, damages, or losses (collectively, "Losses") which arise from failure to follow these Plans, Specifications, and the engineering intent they convey, or for Losses which arise from failure to obtain and/or follow the engineers' or surveyors' guidance with respect to any alleged errors, omissions, inconsistencies, ambiguities, or conflicts contained within the Plans or Specifications.

IOWA CERTIFICATE OF AUTHORITY
NO. 26887

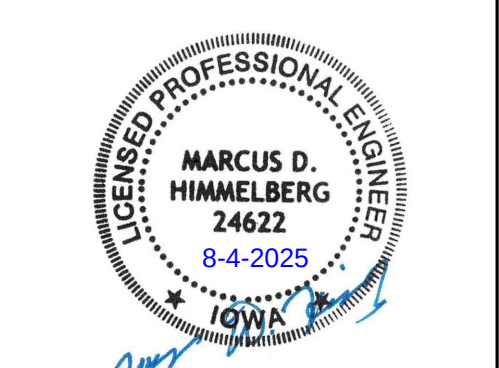

MARCUS HIMMELBERG
NO. P24622
EXP. 12/31/2025

I HEREBY CERTIFY THAT THIS ENGINEERING DOCUMENT WAS PREPARED BY ME OR UNDER MY DIRECT PERSONAL SUPERVISION AND THAT I AM A DULY LICENSED PROFESSIONAL ENGINEER UNDER THE LAWS OF THE STATE OF IOWA.

No.	Description	Date

PROJECT NUMBER 2025001420	SET ISSUE DATE 08/01/2025
ENGINEER IWC	DRAWN BY CEL
CHECKED BY MDH	

JONES GILLAM RENZ
THE RESIDENCE AT CARTER LAKE
CARTER LAKE, IOWA

TYPICAL WOOD DETAILS

Autodesk Docs://2025001420 - JGR - Carter Lake/2025001420 - JGR - Carter Lake R24.rvt