


DESIGN DEVELOPMENT

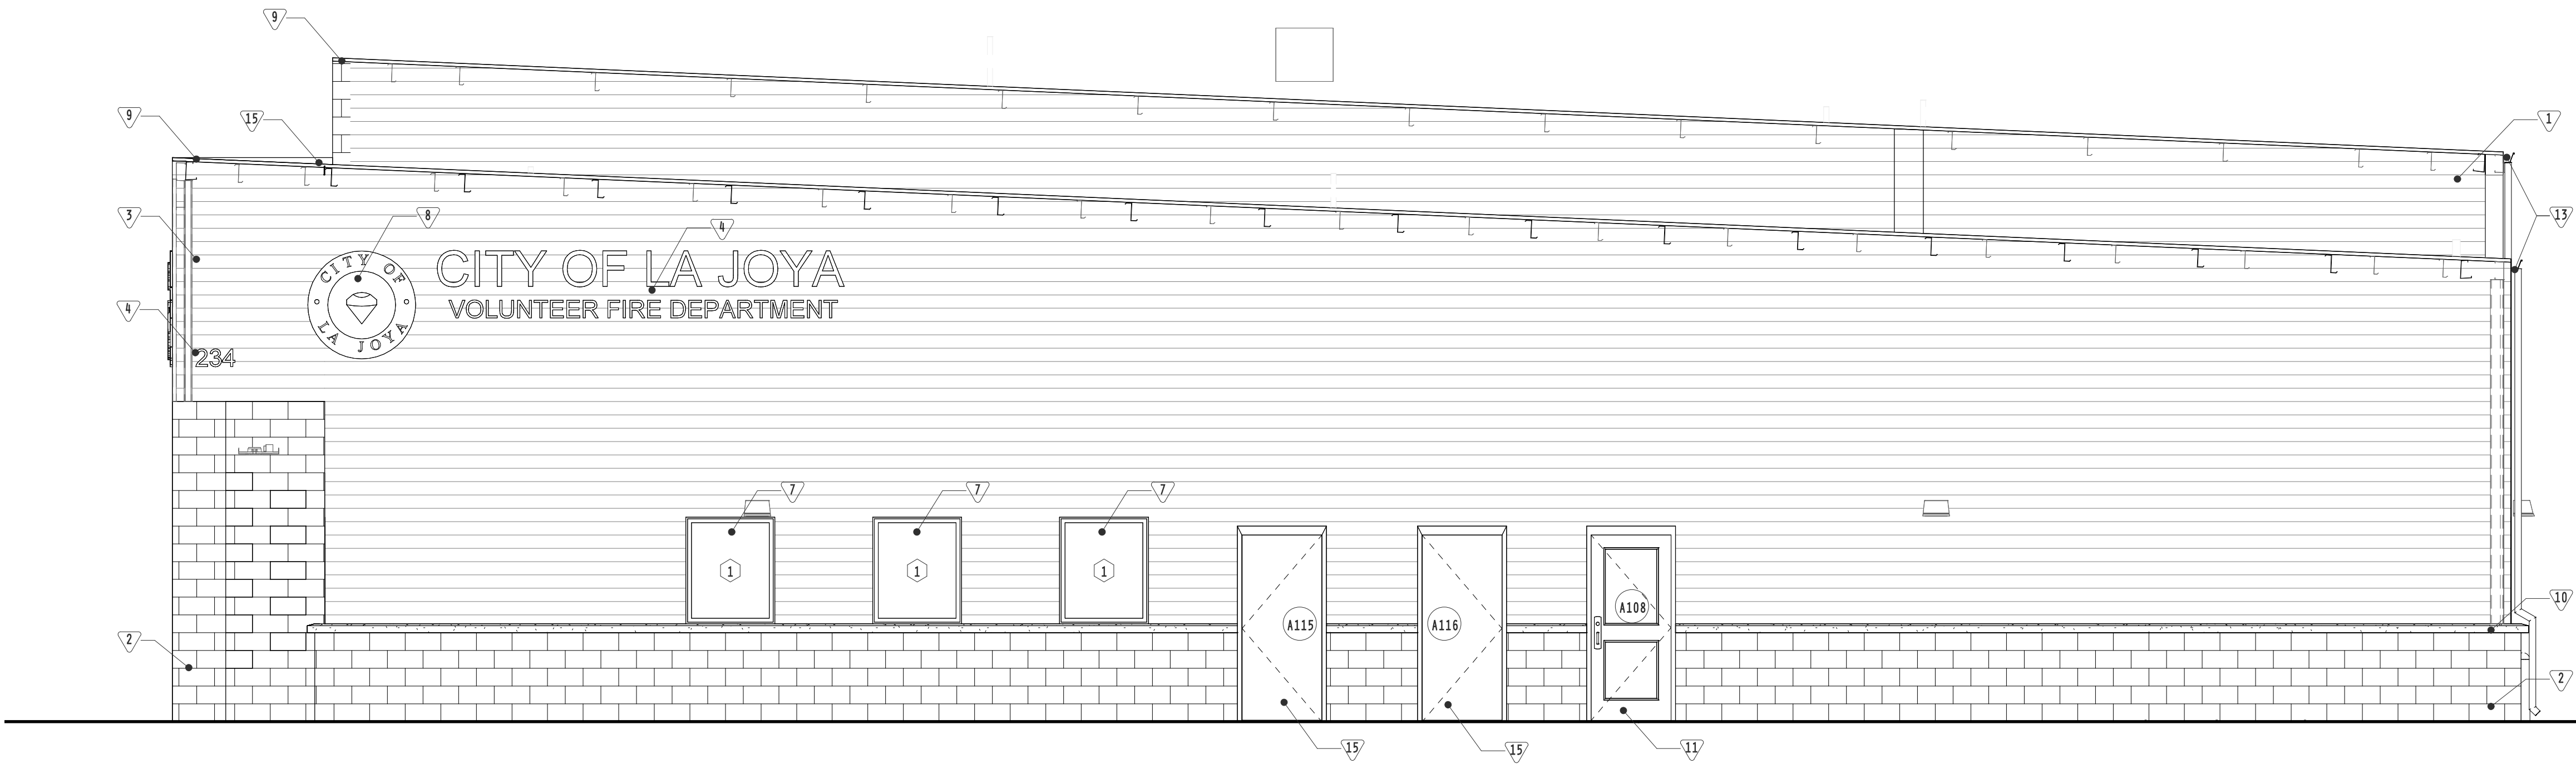

2 SOUTH ELEVATION
1/4" = 1'-0"



1 EAST ELEVATION
1/4" = 1'-0"

SHEET KEYNOTES

- 8" CMU, INTEGRAL COLOR
- 4" CMU VENEER, INTEGRAL COLOR
- 1 1/2" METAL PANEL
- 8" AND 16" TALL 3/8" THICK ALUMINUM LETTERS
- 6" CONCRETE FILLED BOLLARDS, PTD.
- OVERHEAD DOORS AS SPEC.
- ALUMINUM WINDOW SYSTEM, AS SCHED.
- 3/8" PERFORATED ALUMINUM LOGO
- PRE-FINISHED EAVE TRIM.
- CAST STONE CAP
- ALUMINUM DOOR SYSTEM, AS SCHED.
- HOLLOW METAL DOOR SYSTEM, PTD.
- PRE-FINISHED GUTTERS AND DOWNSPOUTS
- METAL PANEL ROOFING SYSTEM WITH LINER INSULATION SYSTEM
- HOLLOW METAL DOOR SYSTEM, PTD.

No. DESCRIPTION DATE

01.06.2023

SAM GARCIA ARCHITECT
1200 AUBURN AVE.
SUITE 280
McALLEN, TX 78504
(956) 631 - 8327
INFO@SANGARCIAARCHITECT.COM

CITY OF
LA JOYA
FIRE STATION

701 E EXPRESSWAY 83
LA JOYA, TX 78560

2022-016 01.06.2023

EXTERIOR
ELEVATIONS

A2.02