



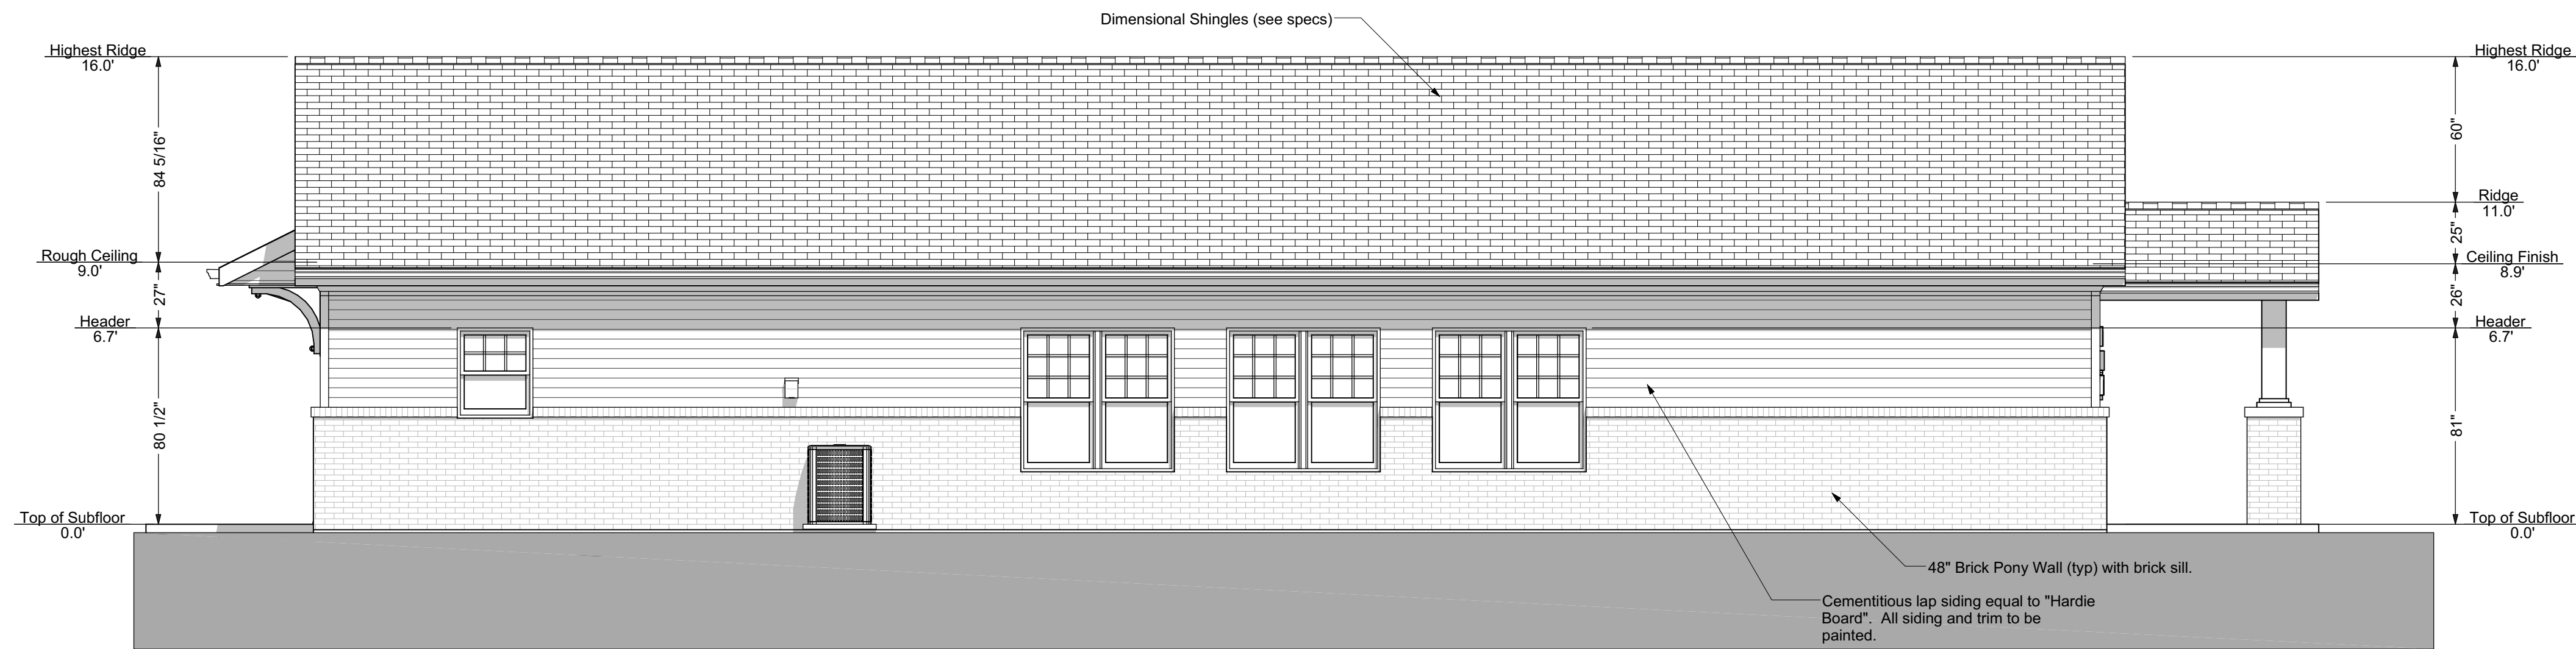

A South Elevation
A2 1/4 in = 1 ft

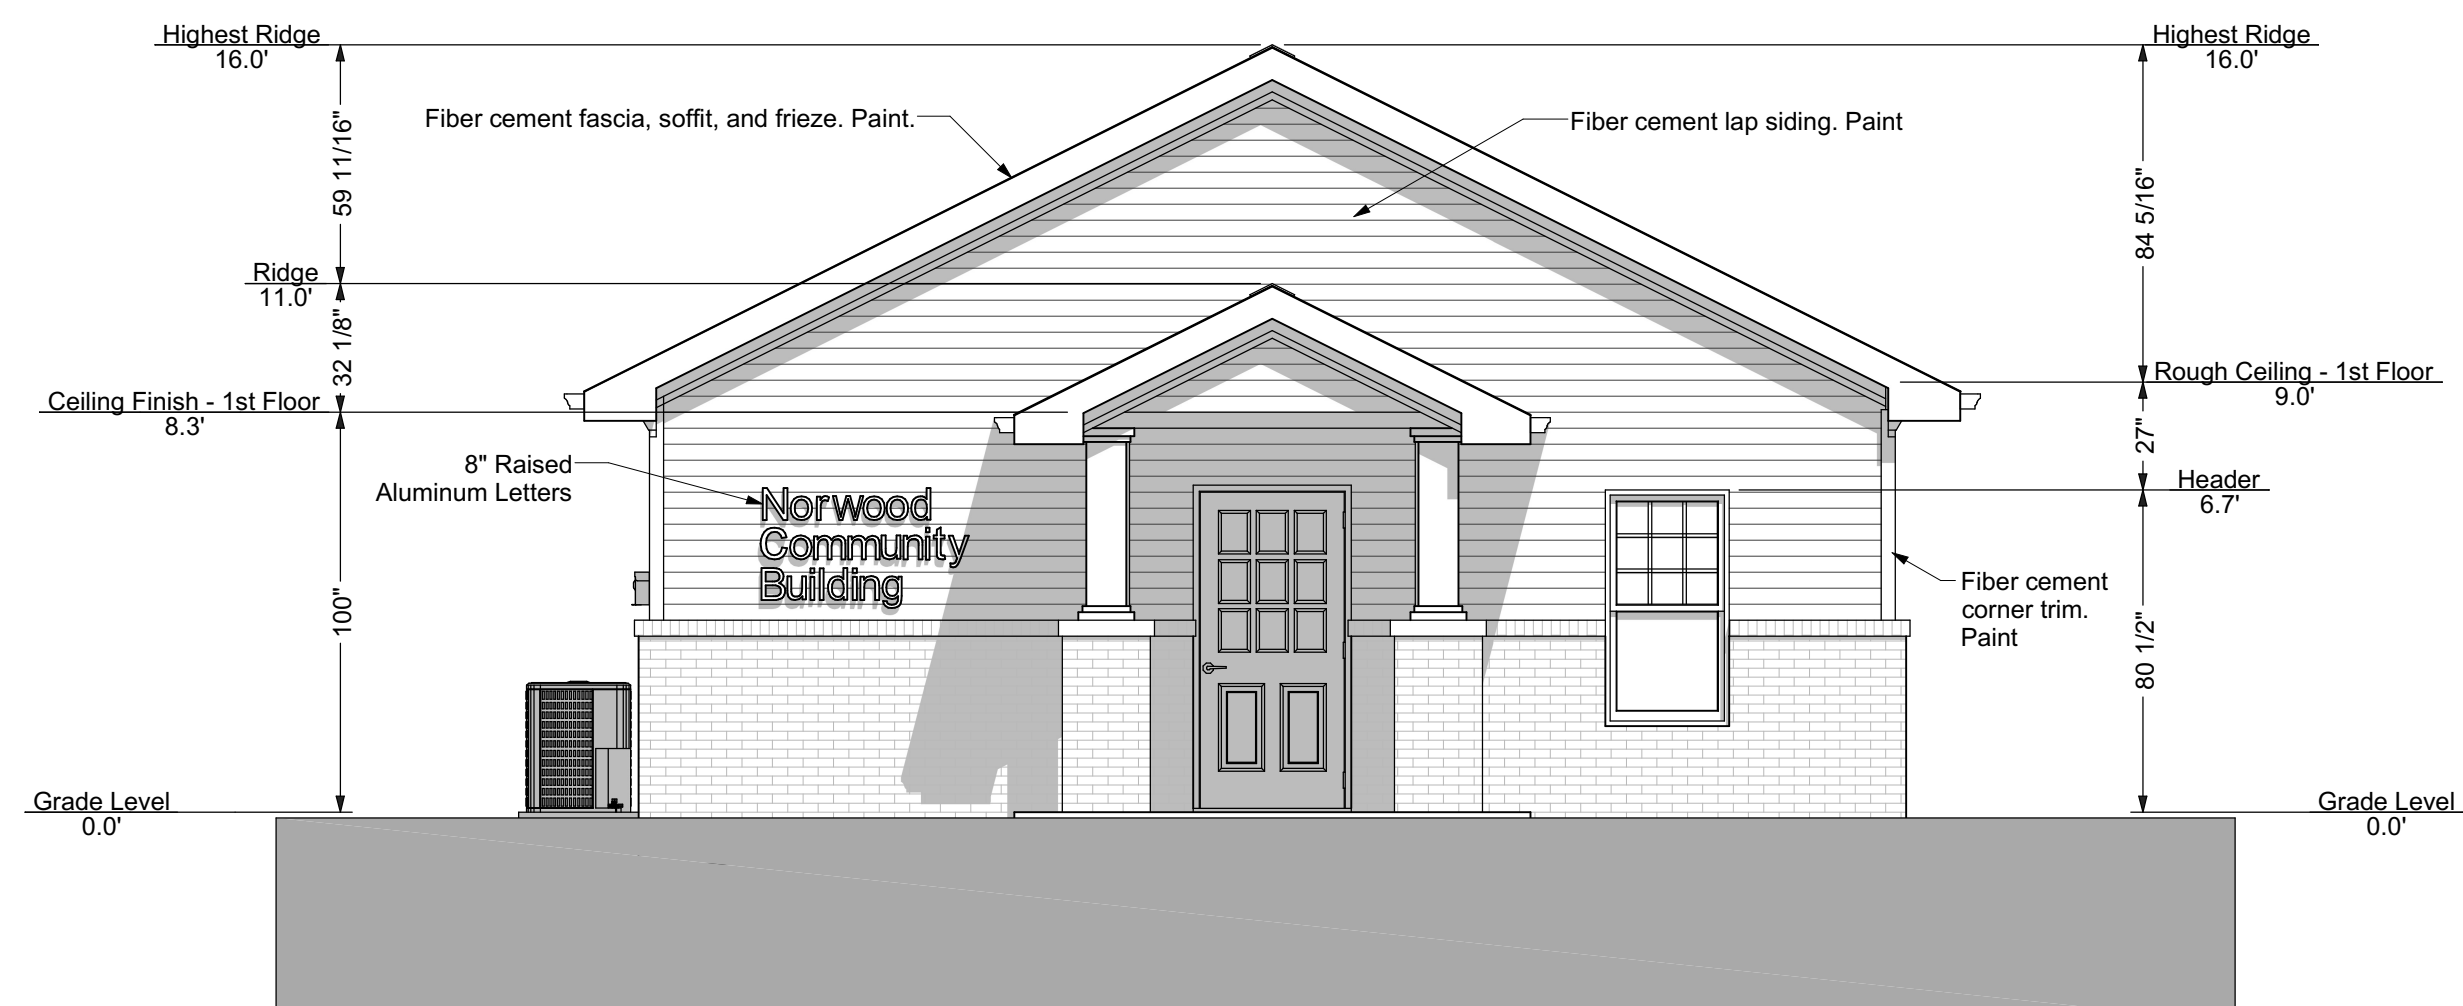


B East Elevation
A2 1/4 in = 1 ft



C West Elevation
A2 1/4 in = 1 ft




D North Elevation
A2 1/4 in = 1 ft

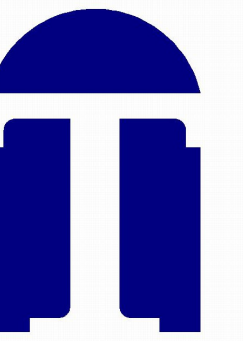

TDA
architects
LLC

125 West Columbus Street
Dadeville, Alabama 36853

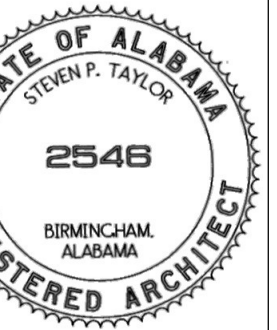

Norwood Community Center
Anniston Housing Authority
Anniston, Alabama

Revision Table		Revised By	Description
Number	Date		

Exterior
Elevations

TDA 445

DATE:
5/1/2023

SHEET:

A2