


THESE ARE NOT THE FINAL BID DOCUMENTS - REFERENCE ONLY

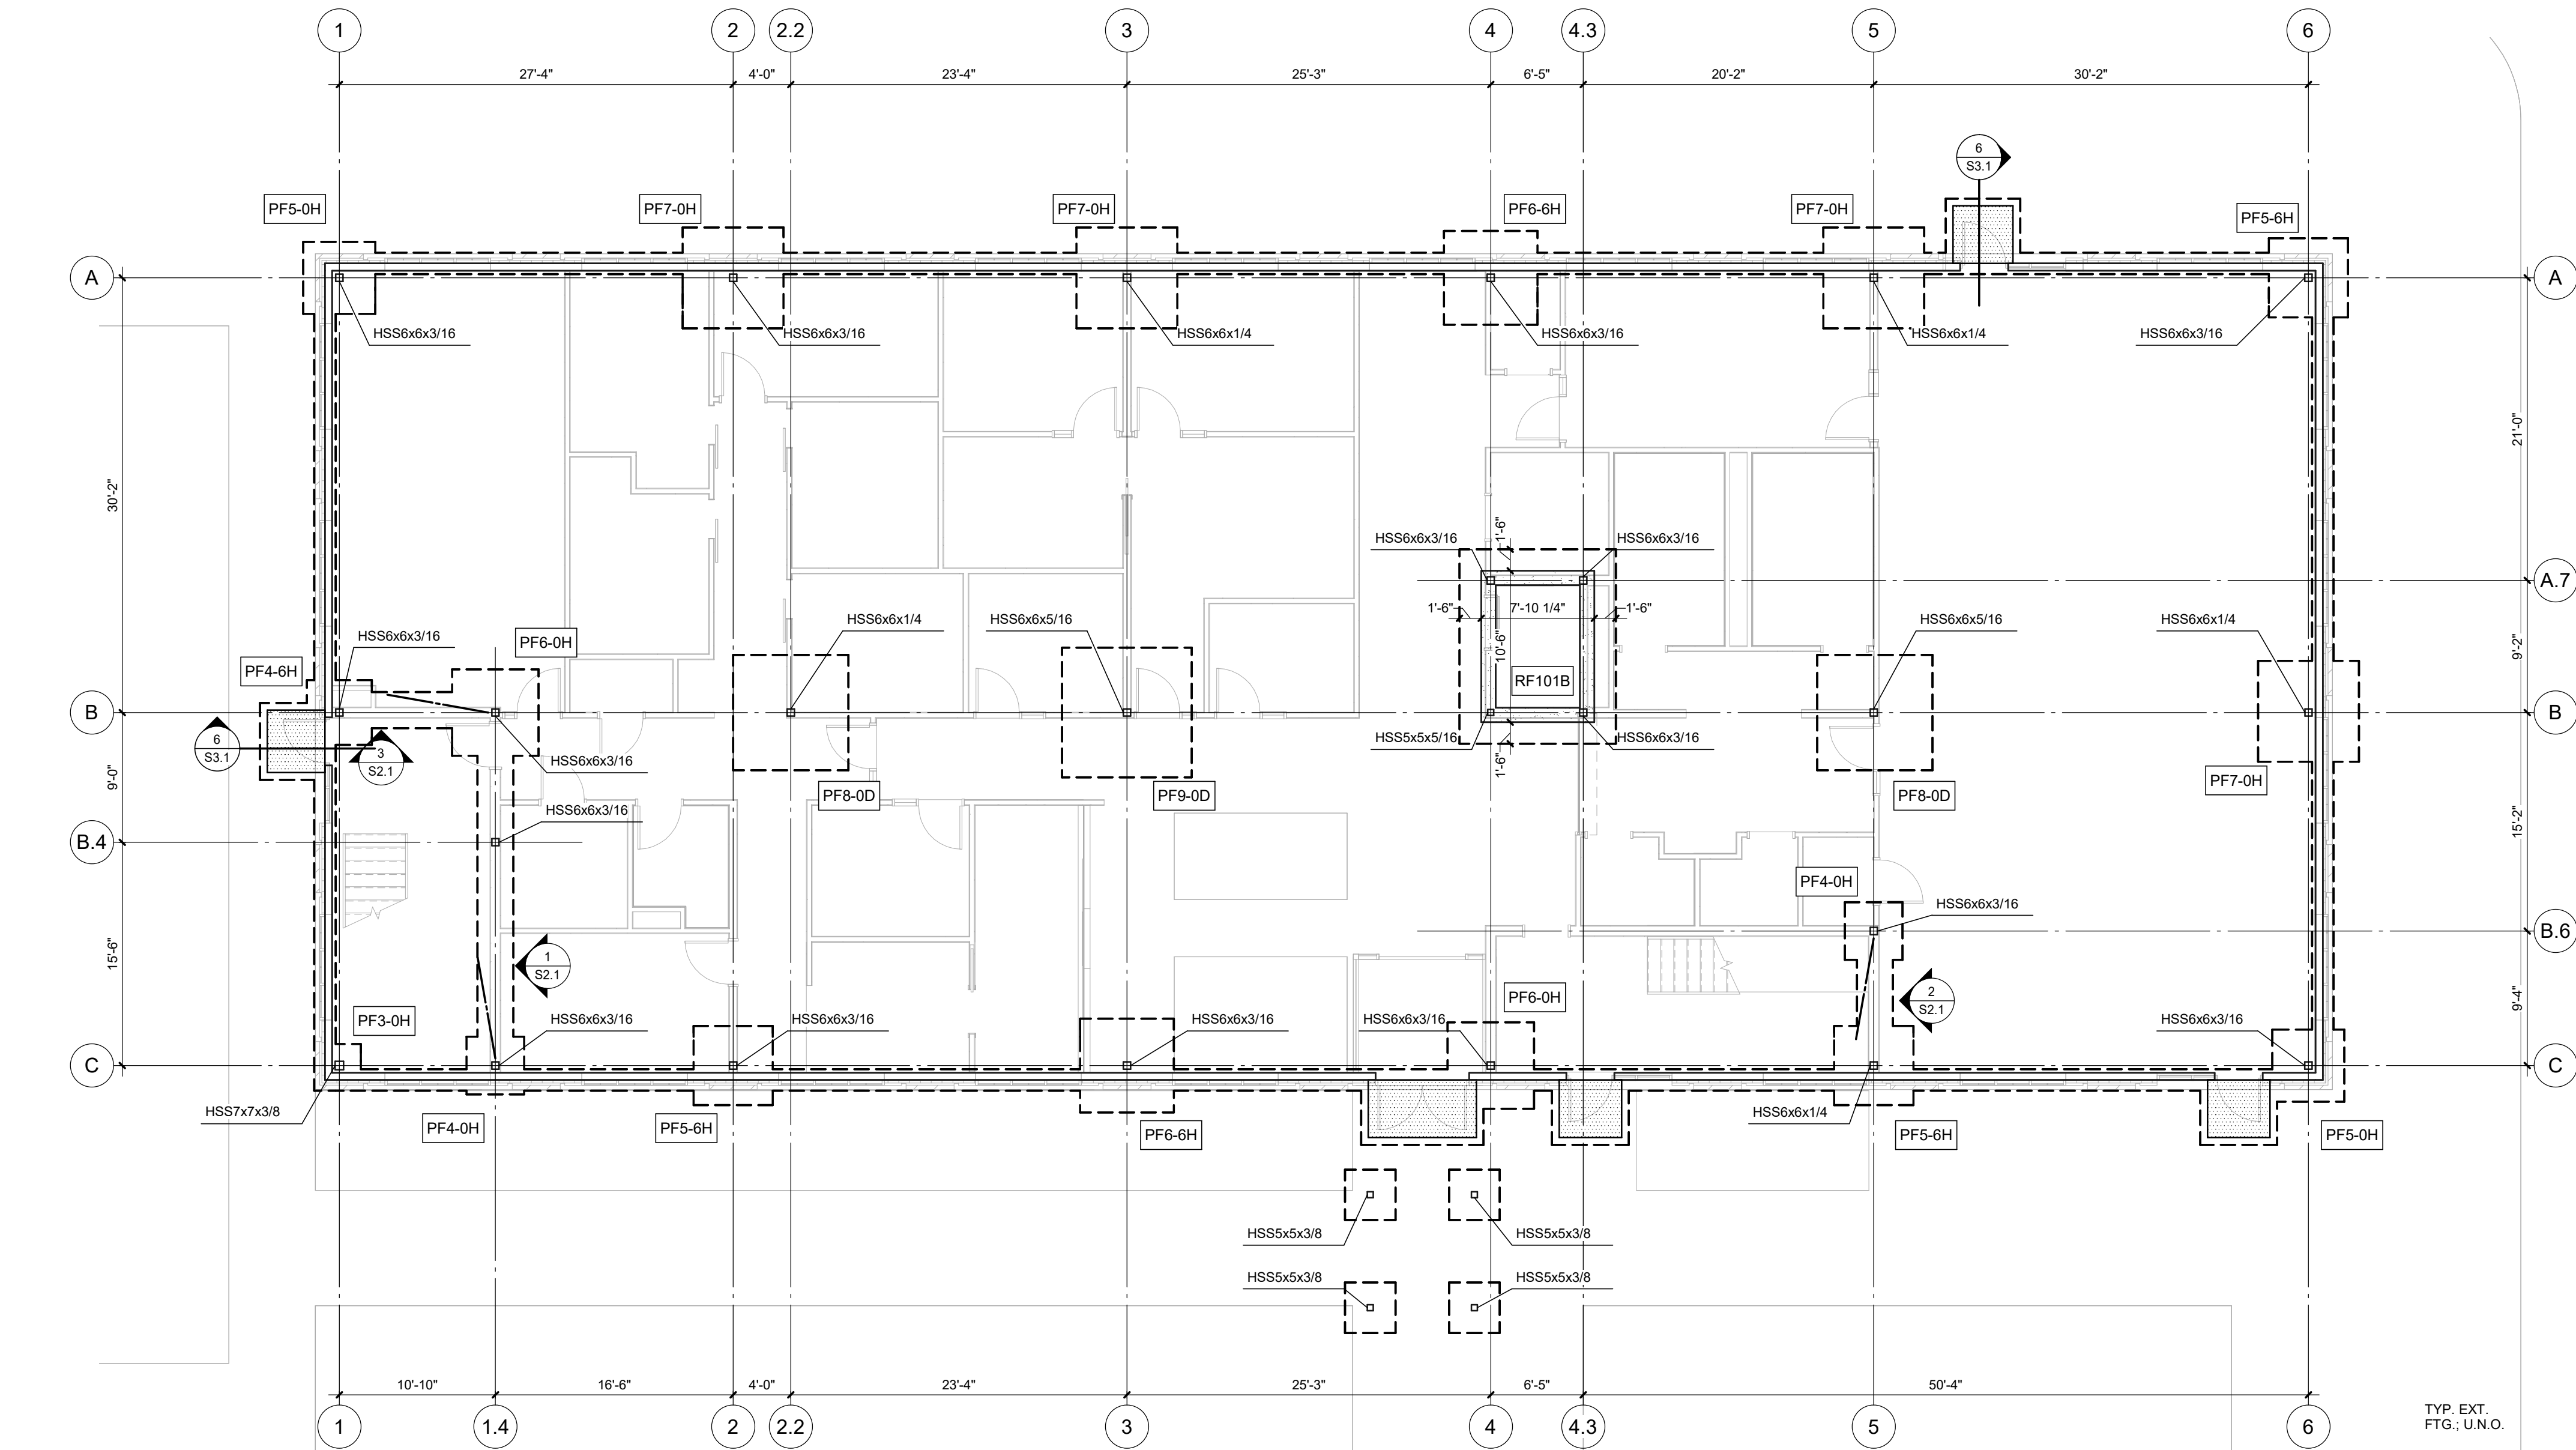

FOUNDATION PLAN
1/8" = 1'-0"

- FOUNDATION PLAN NOTES:
- SEE STRUCTURAL NOTES ON SHEET S0.0.
 - COORDINATE AND VERIFY ALL DIMENSIONS WITH ARCHITECTURAL DRAWINGS AND EXIST. CONDITIONS.
 - TOP OF FOOTING ELEVATION = 99'-4" UNLESS NOTED OTHERWISE THUS:
 - COL. SIZE: COL. MARK WITH CORRESPONDING BASEPLATE DETAIL.

FOOTING SCHEDULE						
MARK	SIZE			REINFORCING	REMARKS	
	W	L	D			
CF1-6H	1'-6"	CONT.	3'-2"	(1)-#8 TOP & BOTT.		
CF2-6H	2'-6"	CONT.	3'-2"	(2)-#6s TOP & BOTT. w/ #4 TIES AT 48"o.c.		
PF3-0H	3'-0"	3'-0"	3'-2"	(3)-#4s E.W. TOP & BOTT.		
PF3-6H	3'-6"	3'-6"	3'-2"	(4)-#4s E.W. TOP & BOTT.		
PF4-0H	4'-0"	4'-0"	3'-2"	(4)-#4s E.W. TOP & BOTT.		
PF4-6H	4'-6"	4'-6"	3'-2"	(5)-#4s E.W. TOP & BOTT.		
PF5-0H	5'-0"	5'-0"	3'-2"	(5)-#4s E.W. TOP & BOTT.		
PF5-6H	5'-6"	5'-6"	3'-2"	(6)-#4s E.W. TOP & BOTT.		
PF6-0H	6'-0"	6'-0"	3'-2"	(6)-#5s E.W. TOP & BOTT.		
PF6-6H	6'-6"	6'-6"	3'-2"	(7)-#5s E.W. BOTT. & BOTT.		
PF7-0H	7'-0"	7'-0"	3'-2"	(7)-#5s E.W. TOP & BOTT.		
PF8-0D	8'-0"	8'-0"	2'-0"	(8)-#6s E.W. TOP & BOTT.		
PF9-0D	9'-0"	9'-0"	2'-0"	(8)-#7s E.W. TOP & BOTT.		
RF101B	SEE PLAN	SEE PLAN	1'-4"	#5s AT 12"o.c. EACH WAY TOP AND BOTTOM	ELEVATOR PIT SLAB / FOOTING	

ALLEY POYNER
MACCHIETTO
ARCHITECTURE

DESIGN DEVELOPMENT

REVISION DATE
Project Number: 21064
Date: March 10, 2023

FOUNDATION PLAN



TD2 PROJECT # 748-749

S1.1

NOT FOR CONSTRUCTION