


A
B
C
D
E
F
G
H
J
K

1 2 3 4 5 6 7 8 9 10 11 12


INDEX OF DRAWINGS			
	SHEET NAME	ISSUE DATE	REVISION DATE
0.0 GENERAL			
T1	TITLE SHEET	09/09/2024	
G1.01	INDEX OF DRAWINGS	09/09/2024	
G1.02	GENERAL NOTES	09/09/2024	
G1.03	GENERAL INFORMATION # MOCK UP WALL	09/09/2024	
G1.11	ACCESSIBILITY INFORMATION	09/09/2024	
G1.21	PARTITION TYPES	09/09/2024	
G1.22	PARTITION DETAILS	09/09/2024	
G1.31	PENETRATION FIRESTOPPING SYSTEMS	09/09/2024	
G2.01	LIFE SAFETY - CODE STUDY	09/09/2024	
1.0 CIVIL			
C-001	PROJECT NOTES	09/09/2024	
C-002	EXISTING CONDITION	09/09/2024	
C-003	DEMOLITION PLAN	09/09/2024	
C-101	SITE LAYOUT # UTILITY PLAN	09/09/2024	
C-201	GRADING PLAN	09/09/2024	
C-304	DRAINAGE PLAN	09/09/2024	
C-601	EROSION # SEDIMENTATION CONTROL PLAN	09/09/2024	
C-901	EROSION # SEDIMENTATION CONTROL DETAILS	09/09/2024	
C-903	SITE DETAILS	09/09/2024	
C-904	STORM DRAINAGE DETAILS	09/09/2024	
C-905	UTILITY DETAILS	09/09/2024	
C-906	UTILITY DETAILS	09/09/2024	
2.0 LANDSCAPE			
L5.00	OVERALL LANDSCAPE PLAN	09/09/2024	
L5.01	LANDSCAPE PLAN	09/09/2024	
L5.02	LANDSCAPE PLAN	09/09/2024	
L5.03	LANDSCAPE PLAN	09/09/2024	
L5.04	LANDSCAPE PLAN	09/09/2024	
L5.05	LANDSCAPE PLAN	09/09/2024	
L5.06	LANDSCAPE PLAN	09/09/2024	
L5.07	LANDSCAPE PLAN	09/09/2024	
L6.00	LANDSCAPE DETAILS	09/09/2024	
L7.00	LIMITS OF IRRIGATION	09/09/2024	
3.0 ARCHITECTURE			
A1.01	FLOOR PLAN	09/09/2024	
A1.11	ENLARGED PLANS # DETAILS	09/09/2024	
A2.01	REFLECTED CEILING PLAN	09/09/2024	
A2.02	ENLARGED RCPS AND DETAILS	09/09/2024	
A3.01	ROOF PLAN	09/09/2024	
A4.01	EXTERIOR ELEVATIONS	09/09/2024	
A4.02	MECH # DUMPSTER ENCLOSURE	09/09/2024	
A5.11	WALL SECTIONS	09/09/2024	
A5.12	WALL SECTIONS	09/09/2024	
A5.20	TYP CONSTRUCTION DETAILS	09/09/2024	
A5.21	SECTION DETAILS	09/09/2024	
A6.01	DOOR SCHEDULE	09/09/2024	
A6.02	DOOR DETAILS	09/09/2024	
A6.11	WINDOW DETAILS	09/09/2024	
A7.01	INTERIOR ELEVATIONS	09/09/2024	
A7.02	INTERIOR ELEVATIONS	09/09/2024	
A7.03	INTERIOR ELEVATIONS	09/09/2024	
A7.04	INTERIOR ELEVATIONS	09/09/2024	
A7.05	INTERIOR ELEVATIONS	09/09/2024	
A7.06	INTERIOR ELEVATIONS	09/09/2024	
A7.11	MILLWORK DETAILS	09/09/2024	
A7.12	MILLWORK DETAILS	09/09/2024	
A8.01	FINISH LEGEND AND DETAILS	09/09/2024	
A8.02	FINISH SCHEDULE	09/09/2024	
A8.03	FINISH PLAN	09/09/2024	
A9.01	FURNITURE PLAN	09/09/2024	
4.0 STRUCTURAL			
S1.01	GENERAL NOTES	09/09/2024	
S1.02	2021 SCHEDULE OF SPECIAL INSPECTIONS	09/09/2024	
S1.03	TYPICAL DETAILS	09/09/2024	
S1.04	TYPICAL DETAILS	09/09/2024	
S1.05	TYPICAL DETAILS	09/09/2024	
S2.01	FLOOR AND FOUNDATION PLAN	09/09/2024	
S2.02	ROOF FRAMING PLAN	09/09/2024	
S3.01	SECTIONS	09/09/2024	
S3.02	SECTIONS	09/09/2024	
5.0 MECHANICAL			
M0.01	SCHEDULES AND LEGEND - HVAC	09/09/2024	
M0.02	SCHEDULES - HVAC	09/09/2024	
M0.03	OSA SCHEDULES - HVAC	09/09/2024	
M0.04	OSA SCHEDULES - HVAC	09/09/2024	
M0.05	OSA SCHEDULES - HVAC	09/09/2024	
M0.06	OSA SCHEDULES - HVAC	09/09/2024	
M1.00	OVERALL FLOOR PLAN LEVEL 1 - HVAC DUCTWORK	09/09/2024	
M1.01	PARTIAL FLOOR PLAN A LEVEL 1 - HVAC DUCTWORK	09/09/2024	
M1.02	PARTIAL FLOOR PLAN B LEVEL 1 - HVAC DUCTWORK	09/09/2024	
M2.00	OVERALL FLOOR PLAN LEVEL 1 - HVAC PIPING	09/09/2024	
M2.01	PARTIAL FLOOR PLAN A LEVEL 1 - HVAC PIPING	09/09/2024	
M2.02	PARTIAL FLOOR PLAN B LEVEL 1 - HVAC PIPING	09/09/2024	
M3.01	ROOF PLAN - HVAC	09/09/2024	
M4.01	ENLARGED FLOOR PLANS - HVAC	09/09/2024	
M6.01	DETAILS - HVAC	09/09/2024	
M6.02	DETAILS - HVAC	09/09/2024	
M7.01	CONTROLS - HVAC	09/09/2024	
M7.02	CONTROLS - HVAC	09/09/2024	

INDEX OF DRAWINGS			
	SHEET NAME	ISSUE DATE	REVISION DATE
6.0 PLUMBING			
P0.01	LEGENDS, NOTES, # SCHEDULES - PLUMBING	09/09/2024	
P1.00	FLOOR PLAN LEVEL 1 - PLUMBING SANITARY	09/09/2024	
P2.00	FLOOR PLAN LEVEL 1 - PLUMBING DOMESTIC	09/09/2024	
P4.01	PARTIAL FLOOR PLANS - PLUMBING	09/09/2024	
P5.01	RISERS - PLUMBING	09/09/2024	
P5.02	RISERS - PLUMBING	09/09/2024	
6.5 FIRE PROTECTION			
F0.01	GENERAL NOTES - FIRE PROTECTION	09/09/2024	
F1.00	FLOOR PLAN LEVEL 1 - FIRE PROTECTION	09/09/2024	
F2.01	DETAILS - FIRE PROTECTION	09/09/2024	
7.0 ELECTRICAL			
E0.01	SITE ELECTRICAL PLAN	09/09/2024	
E1.01	LIGHTING PLAN	09/09/2024	
E1.02	POWER PLAN	09/09/2024	
E1.03	MECHANICAL PLAN	09/09/2024	
E1.04	AUXILIARY PLAN	09/09/2024	
E1.05	SECURITY PLAN	09/09/2024	
E1.06	LARGE SCALE ELECTRICAL PLANS	09/09/2024	
E2.01	PANELBOARD SCHEDULES	09/09/2024	
E2.02	PANELBOARD SCHEDULES	09/09/2024	
E3.01	ELECTRICAL DETAILS	09/09/2024	
E3.02	ELECTRICAL DETAILS # RISER DIAGRAMS	09/09/2024	
E3.03	LEGEND, NOTES # SCHEDULES	09/09/2024	
105			

VICINITY MAP

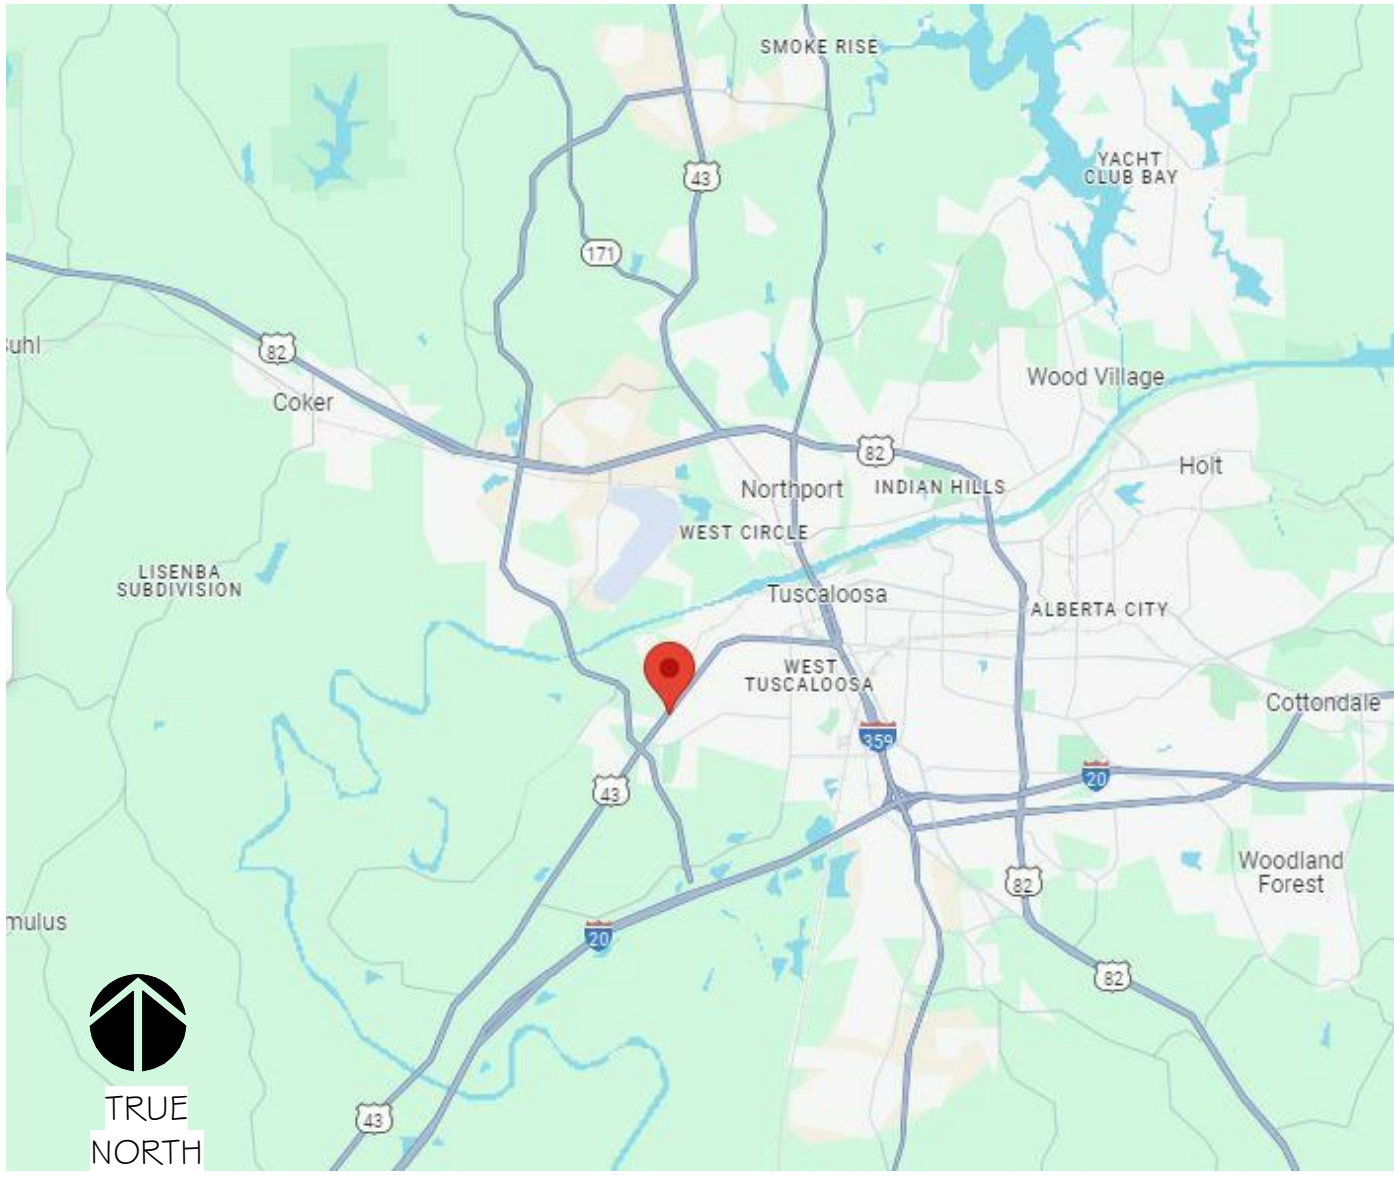

LOCATION MAP

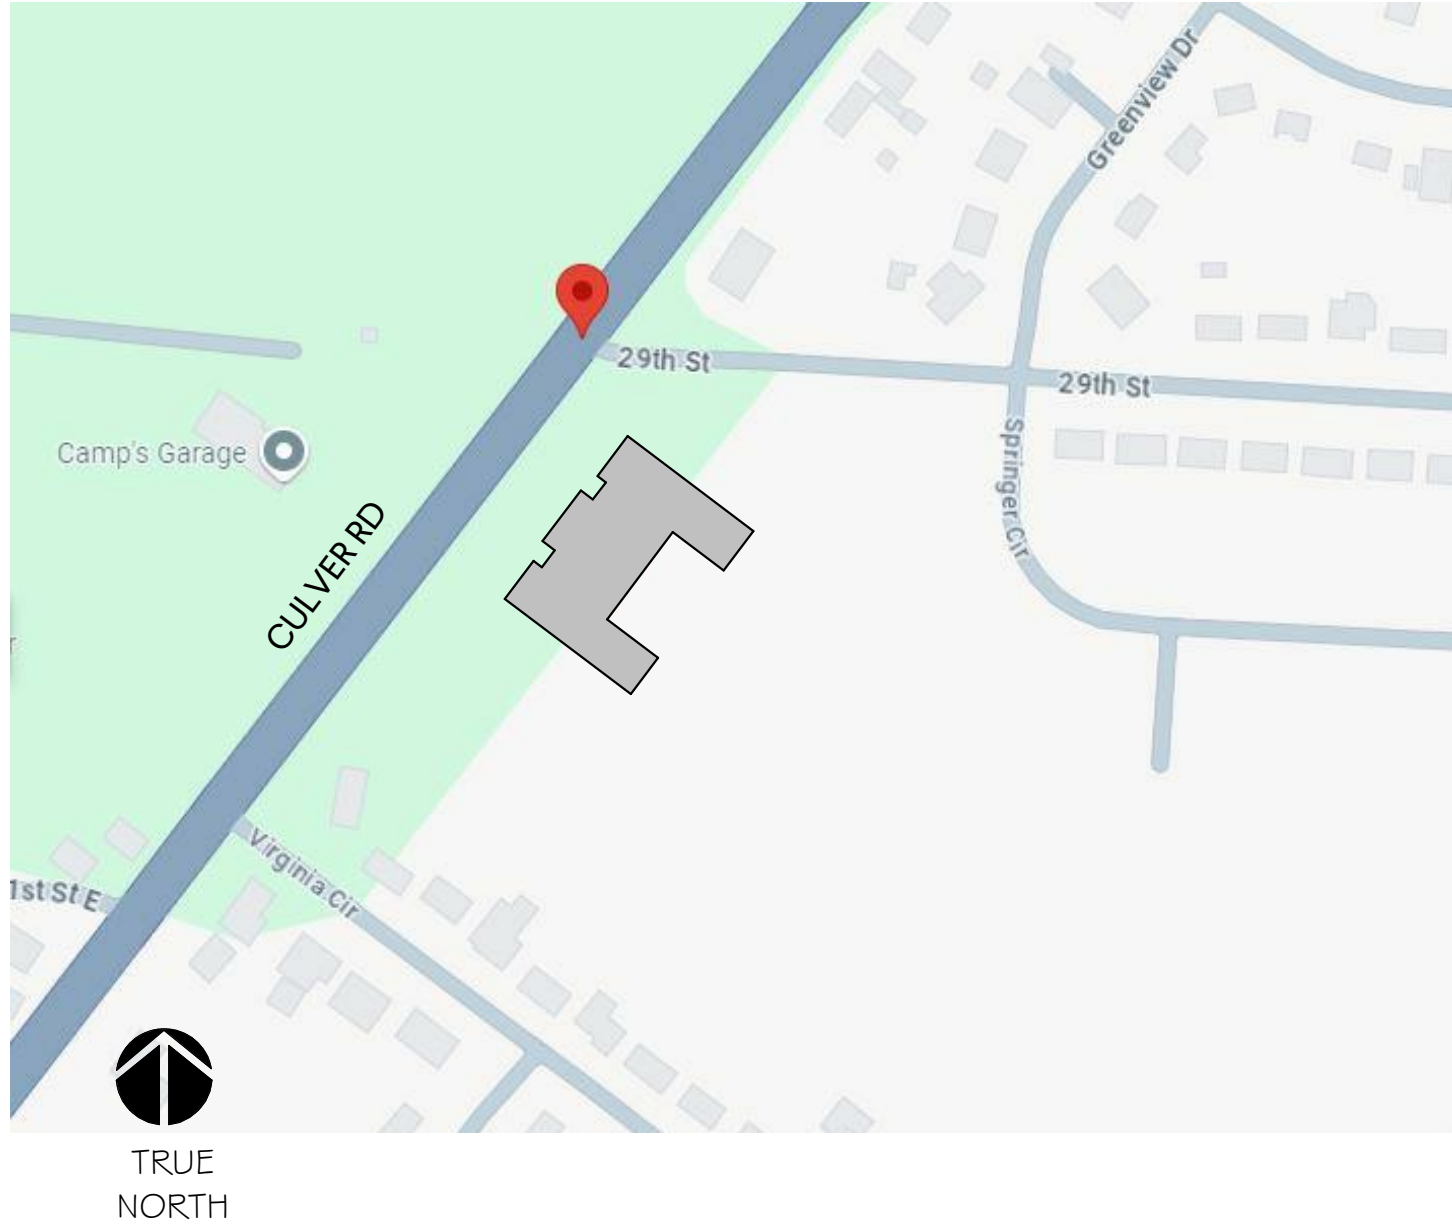

INDEX OF DRAWINGS

TUSCALOOSA COUNTY DHR
PROJECT ADDRESS PENDING

ISSUE DATE


BID SET 09/09/2024

GMC # ABHM220021
SBC # [ENTER VALUE]



G1.01
sheet of

2400 5th Avenue South, Suite 200
Birmingham, AL 35233
T 205.879.4462
GMCNETWORK.COM

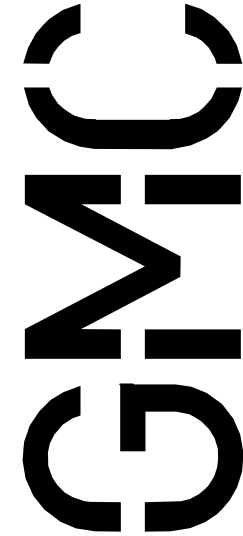

A
B
C
D
E
F
G
H
J
K

1 2 3 4 5 6 7 8 9 10 11 12