

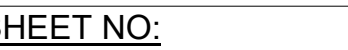


1. FLOOR FRAMING SHALL BE PRE-ENGINEERED WOOD TRUSSES AS FOLLOWS:
 RT = PREFABRICATED ROOF TRUSS
 GR = PREFABRICATED GIRDER TRUSS
2. SPAN ARROWS INDICATE TRUSS SPAN DIRECTION. ACTUAL LAYOUT OF TRUSSES SHALL BE PROVIDED BY TRUSS MANUFACTURER.
3. COORDINATE ALL PLUMBING AND MECHANICAL LOCATIONS WITH FRAMING AND TRUSS DRAWINGS. FRAMING MEMBERS SHALL NOT BE DAMAGED DUE TO INSTALLATION OF MECHANICAL OR PLUMBING SYSTEM AND ENGINEER SHALL BE NOTIFIED OF CONFLICTS FOR PROPER RESOLUTION. TRUSS MANUFACTURER SHALL PROVIDE OPEN CHASES AS REQUIRED FOR MEP SYSTEMS.
4. COORDINATE ALL STEPS, SLOPES AND DIMENSIONS NOT SHOWN HERE WITH ARCHITECTURAL DRAWINGS.
5. ALL DETAILS AND SECTIONS SHALL BE CONSIDERED TYPICAL FOR ALL SIMILAR CONDITIONS UNLESS NOTED OTHERWISE.
6. WELD CONCEALED FLANGES OF HUC HANGERS TO STEEL COLUMNS PER SAMPSON TECHNICAL BULLETIN T-C-HUHC-W

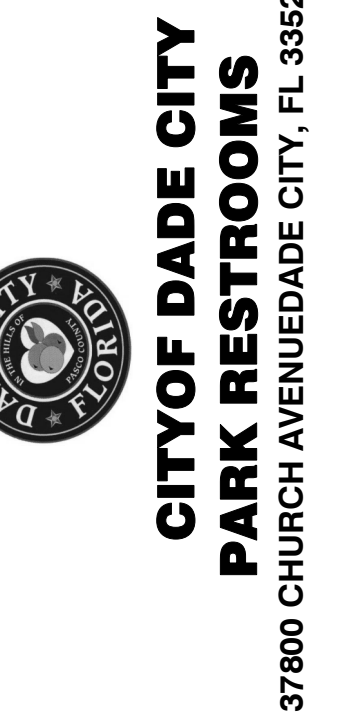

S1.10

PERMIT BID SET 10-19-2023

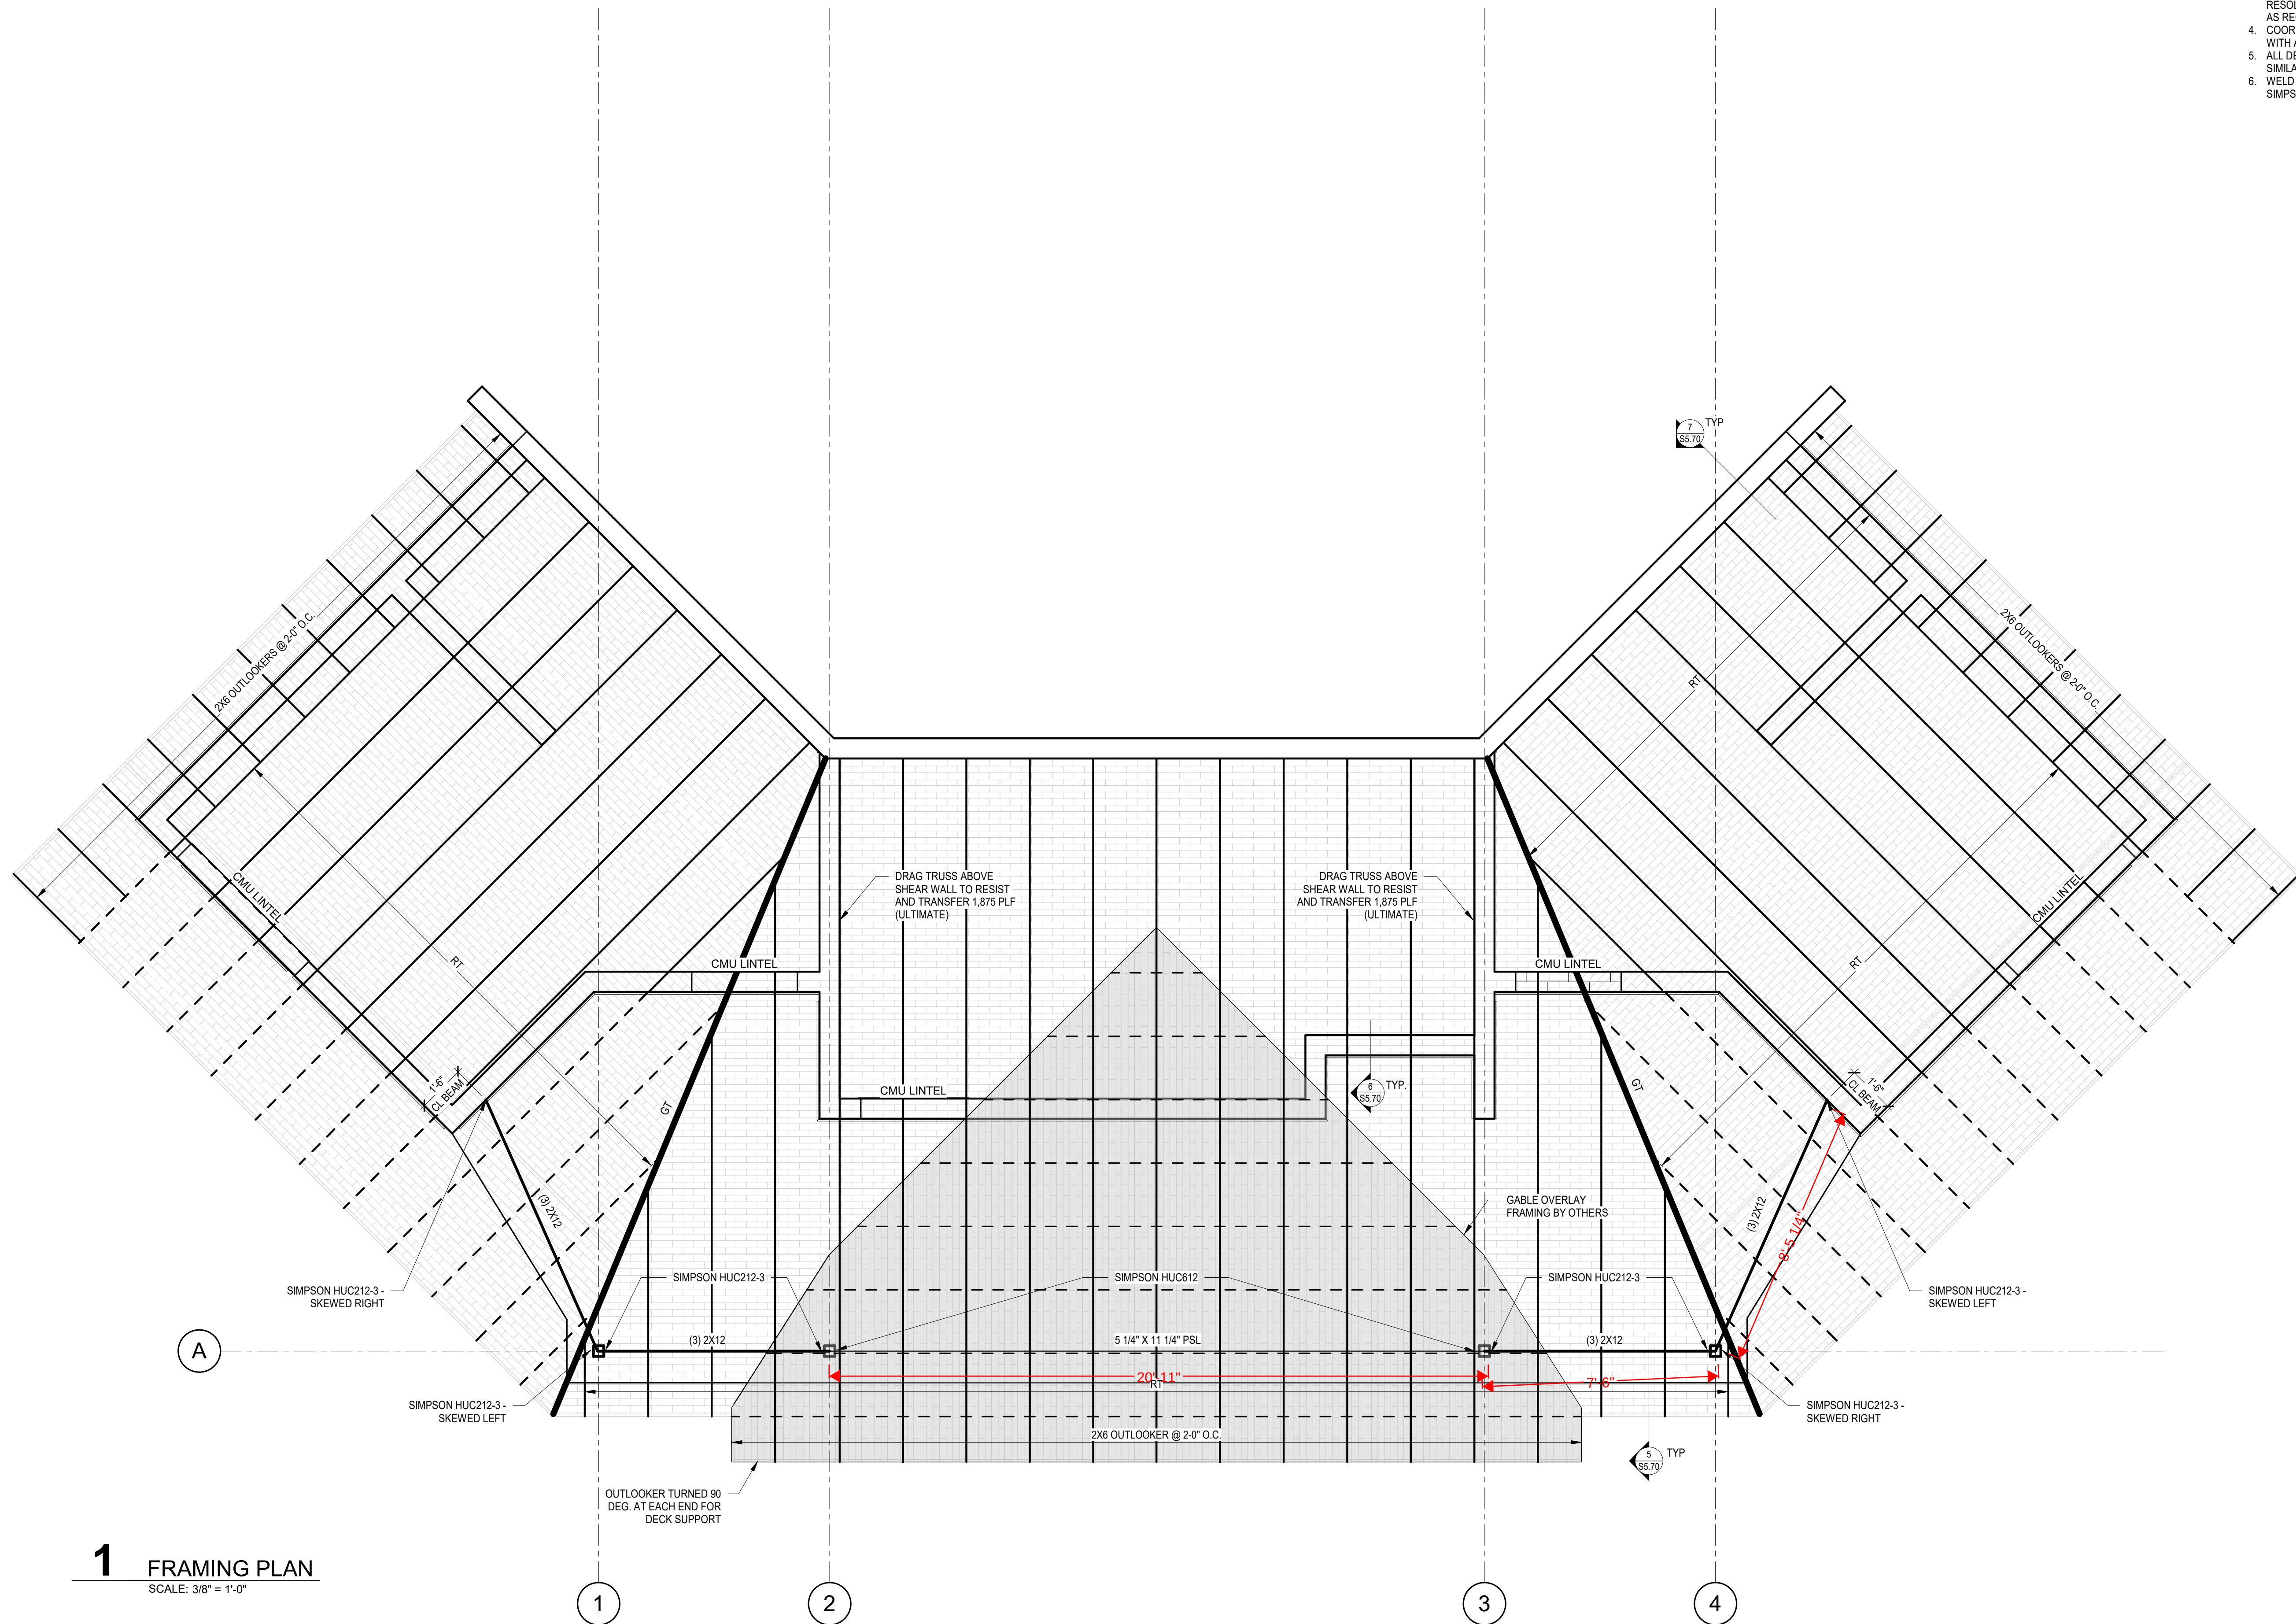

1 FRAMING PLAN

SCALE: 3/8" = 1'-0"

©2022 Boggs Design Partners, LLC. All rights reserved. No document, together with the contents and design presented herein, is intended to be a part of any specific project and client is not to be used, in whole or in part, for any other project without the prior written consent of Boggs Design Partners, LLC. Boggs Design Partners, LLC, shall be without liability to Boggs Design Partners, LLC, for any use of the contents and design presented herein, in whole or in part, for any other project without the prior written consent of Boggs Design Partners, LLC.