


ADDITION TO HOME
15083 MINOCK ST, DETROIT MI 48223

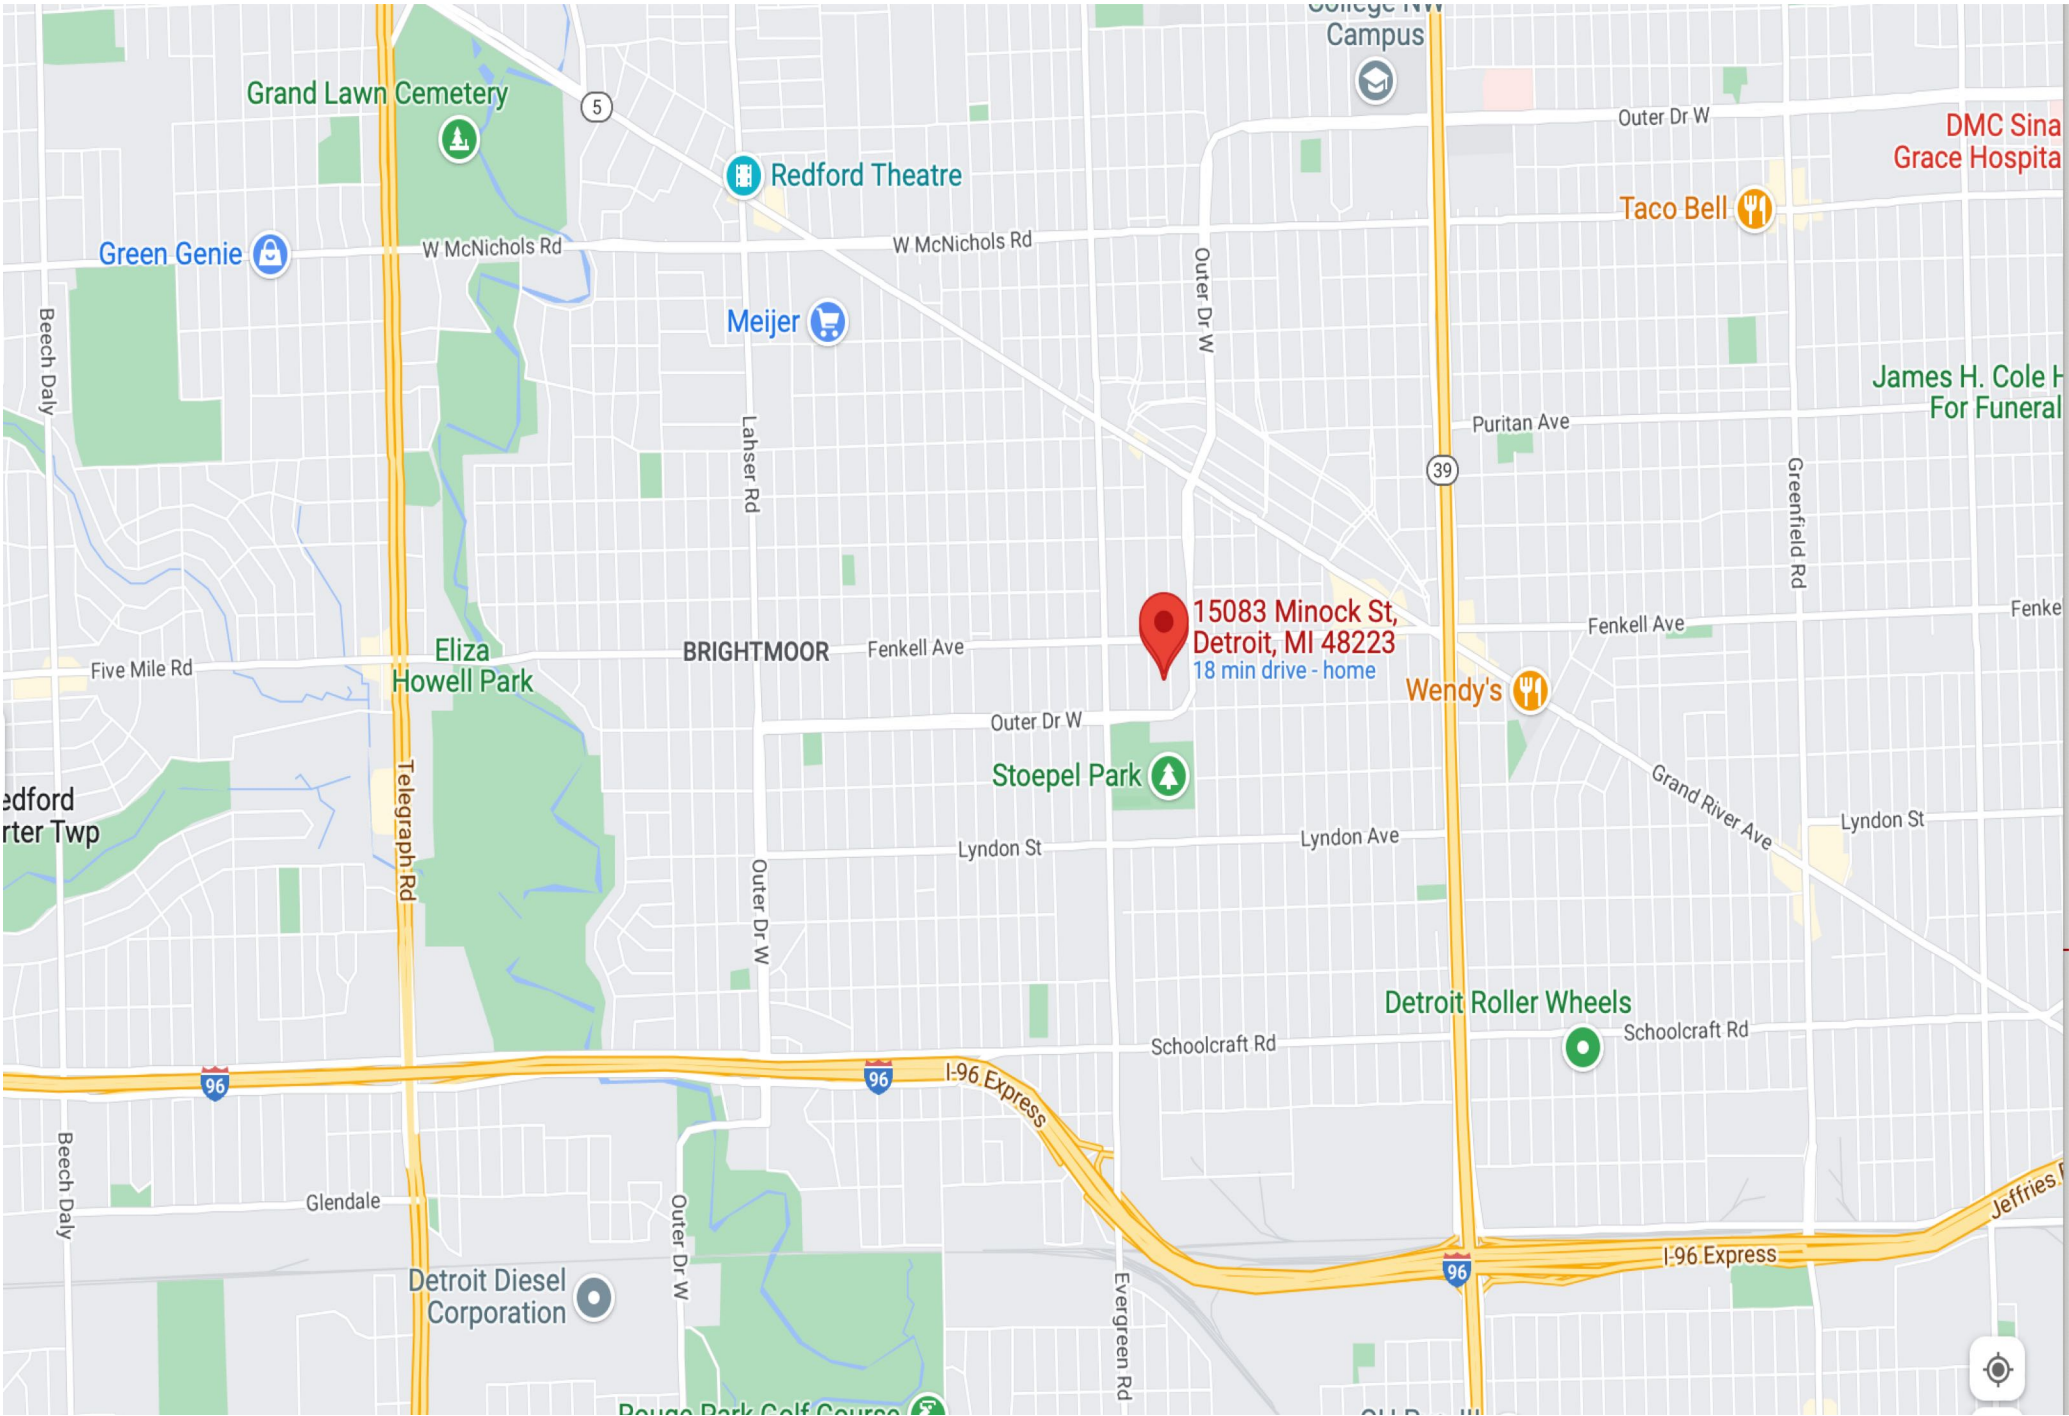


SCOPE OF WORK: 802SF ADDITION TO EXISTING RESIDENTIAL HOME. NEW DECK AND GARAGE.

ZONED: R-1 RESIDENTIAL

ALLOWABLE LOT COVERAGE: 35%

PROPOSED LOT COVERAGE: 30%

Sheet #	Sheet Name
G-00	GENERAL INFORMATION AND SITE PLAN
A-00	FOUNDATION PLANS AND DETAILS
A-10	PLANS
A-30	EXTERIOR ELEVATIONS
S-10	FRAMING PLANS
EM-10	ELECTRICAL AND MECHANICAL PLANS

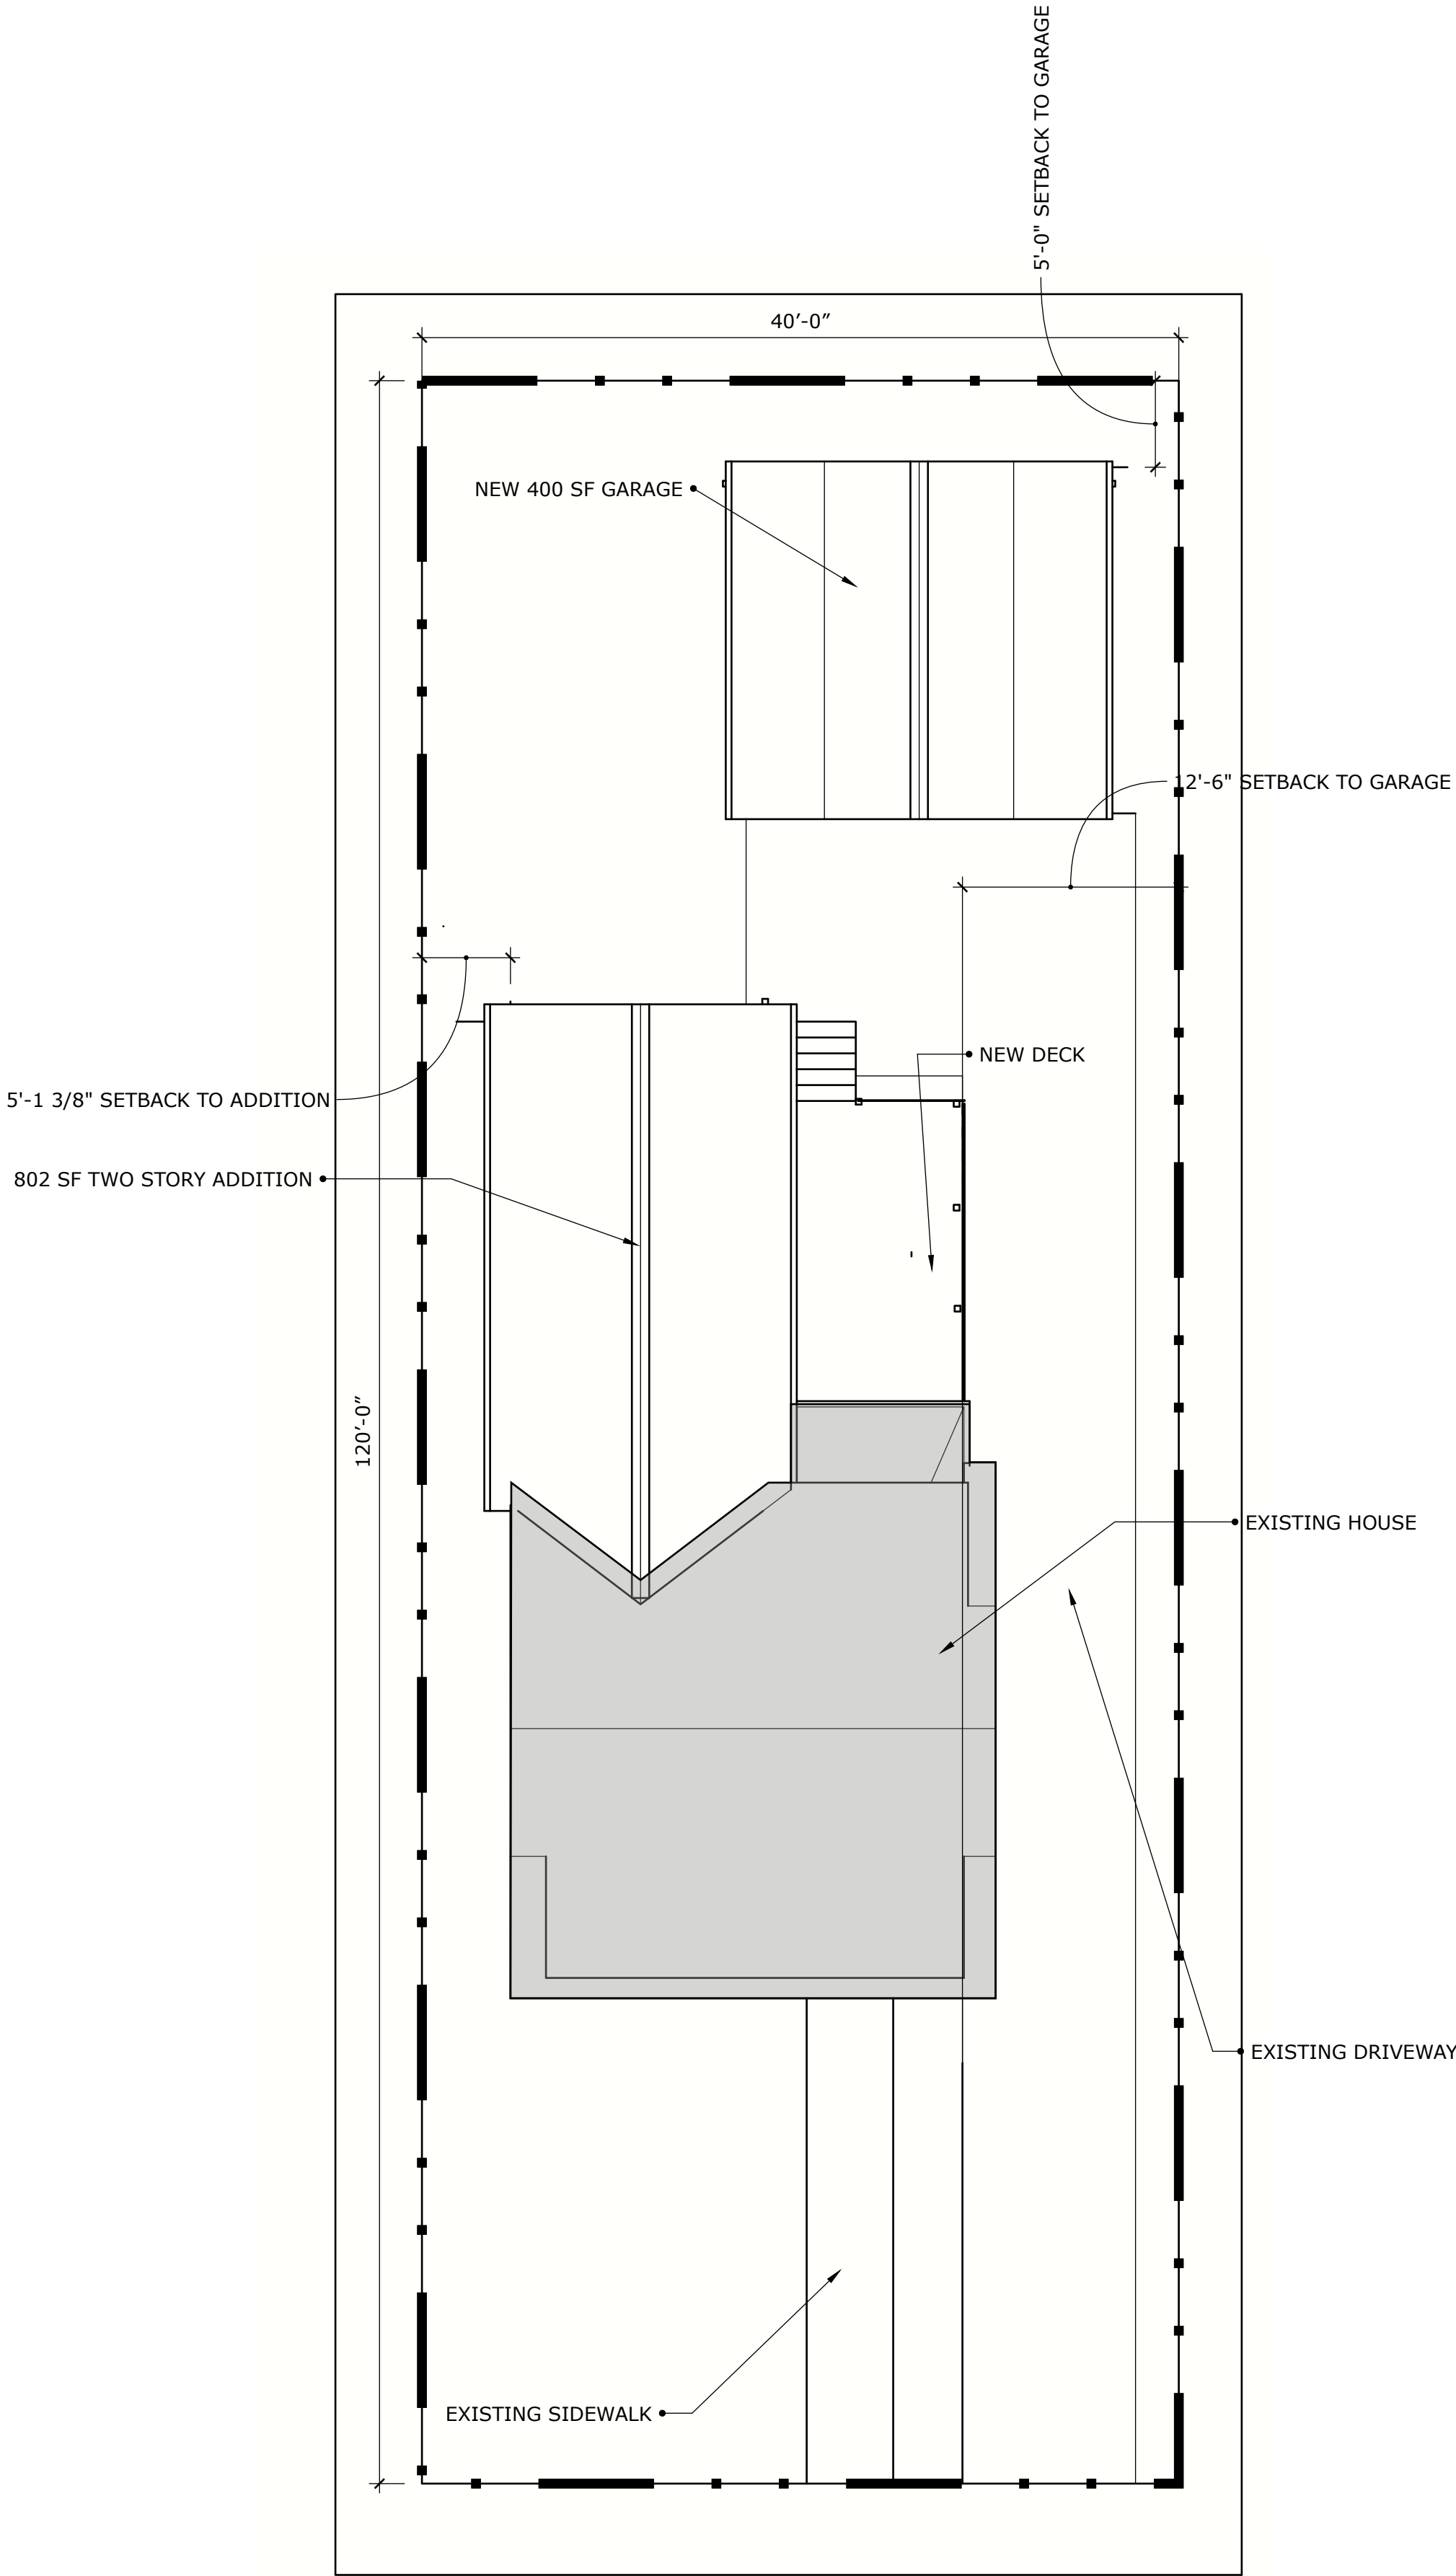

1
G-00 SITE PLAN
SCALE: 1/8" = 1'-0"


NINE
Design + Homes™

RESIDENTIAL ADDITION
15083 MINOCK ST DETROIT MI 48223


ISSUE

GENERAL
INFORMATION


G-00

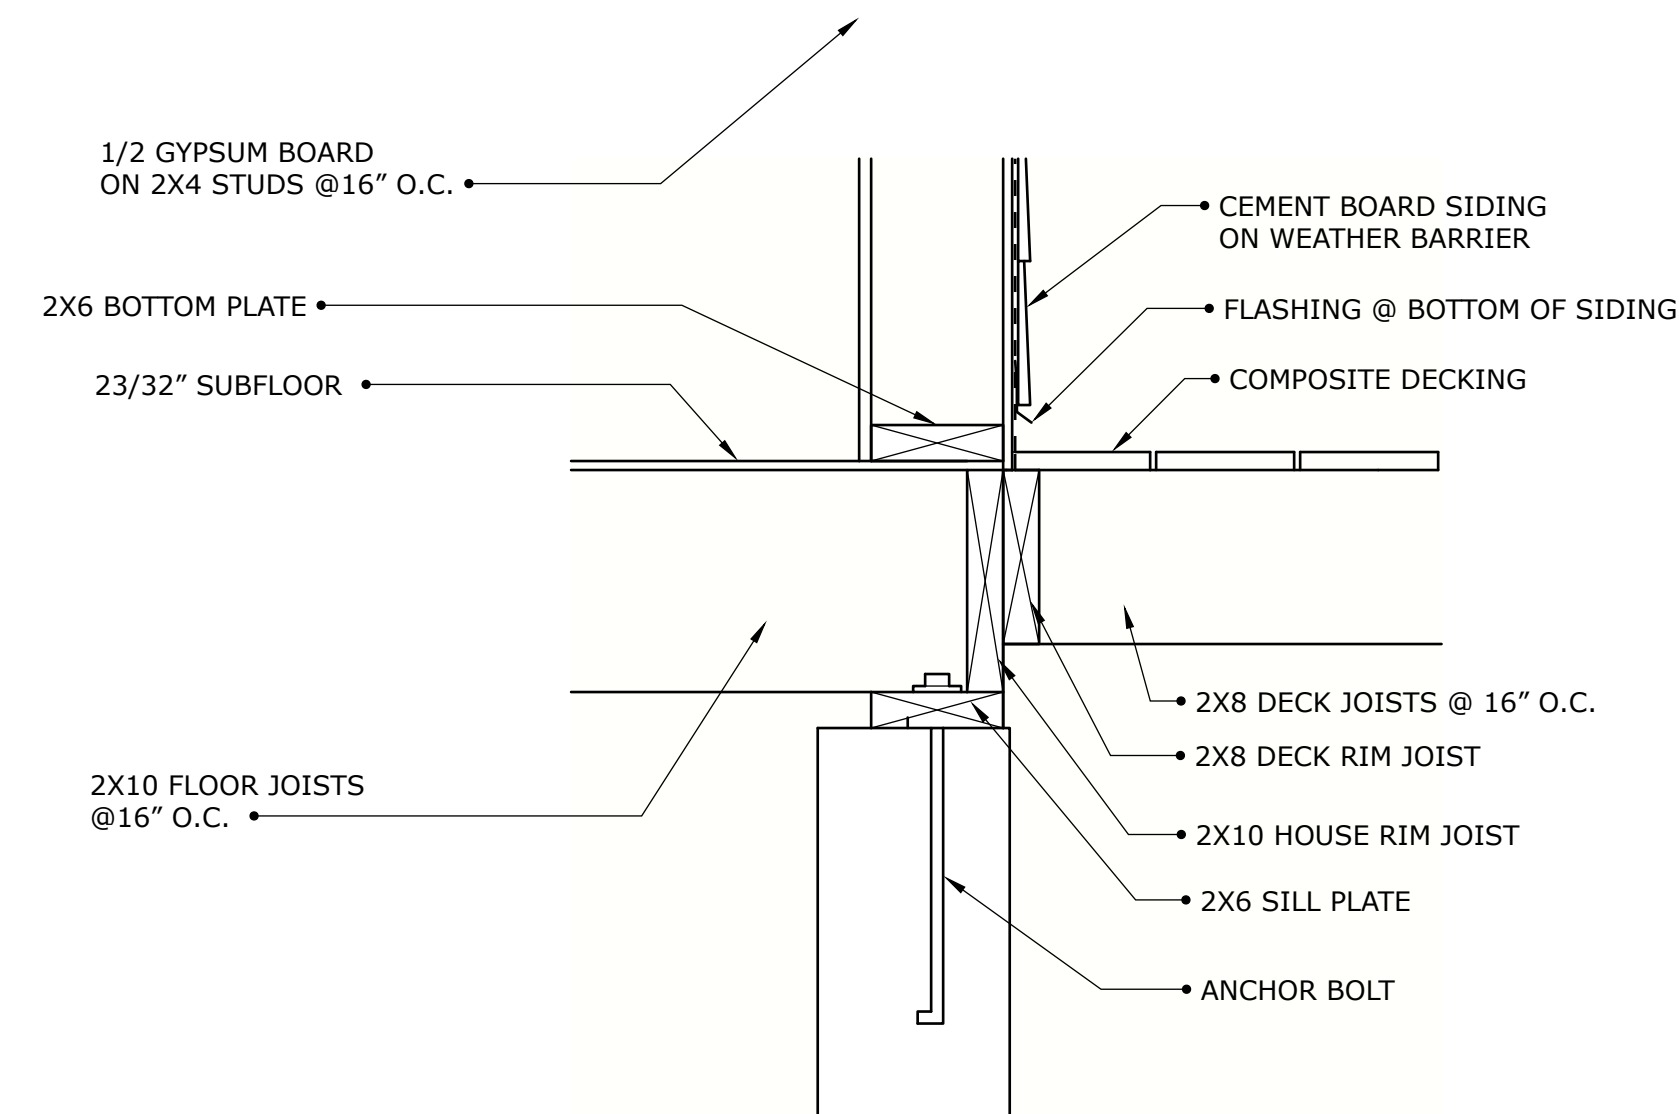


8 DECK EDGE DETAIL
A-00 SCALE: 1 1/2" = 1'-0"

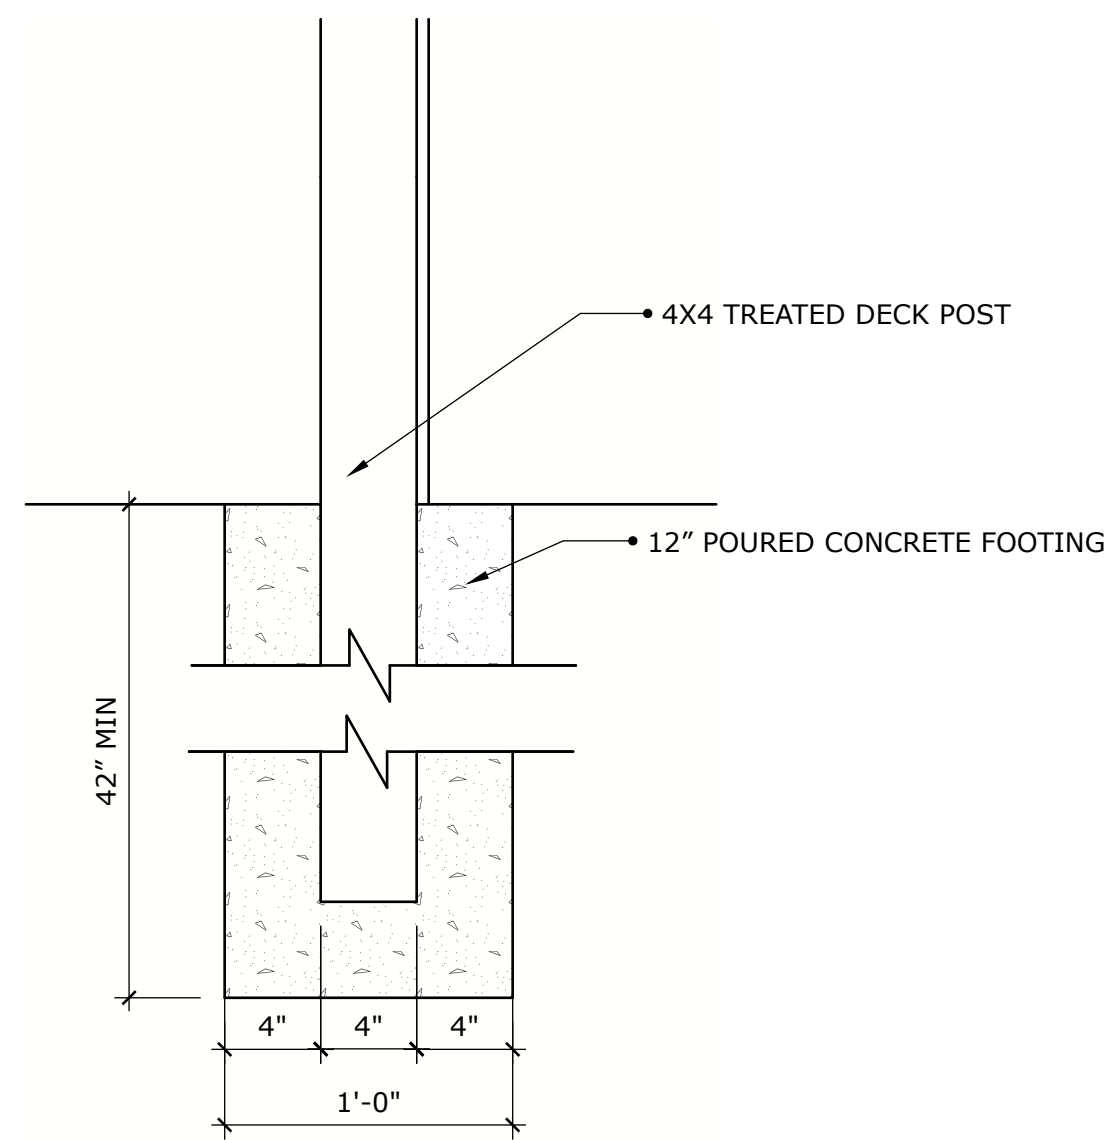


7 DECK POST FOOTING DETAIL
A-00 SCALE: 1 1/2" = 1'-0"

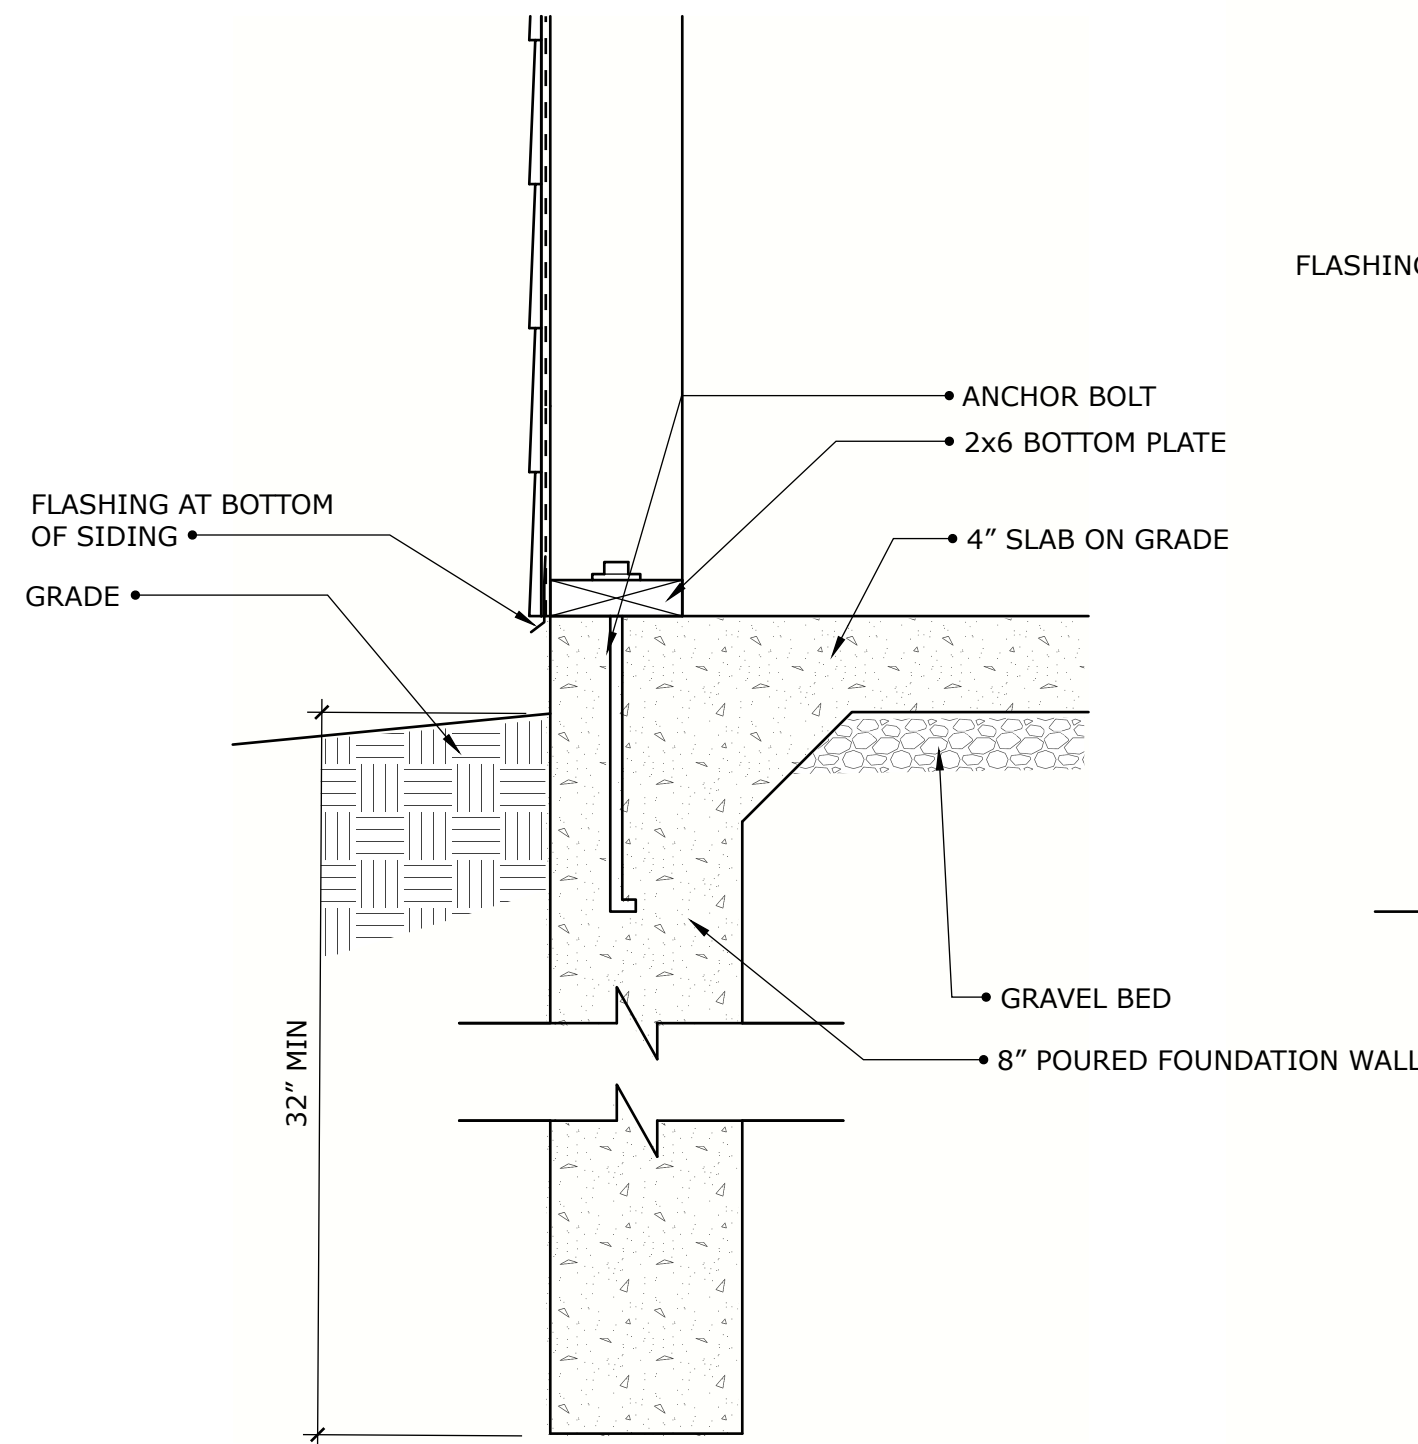


6 GARAGE FOUNDATION DETAIL
A-00 SCALE: 1 1/2" = 1'-0"

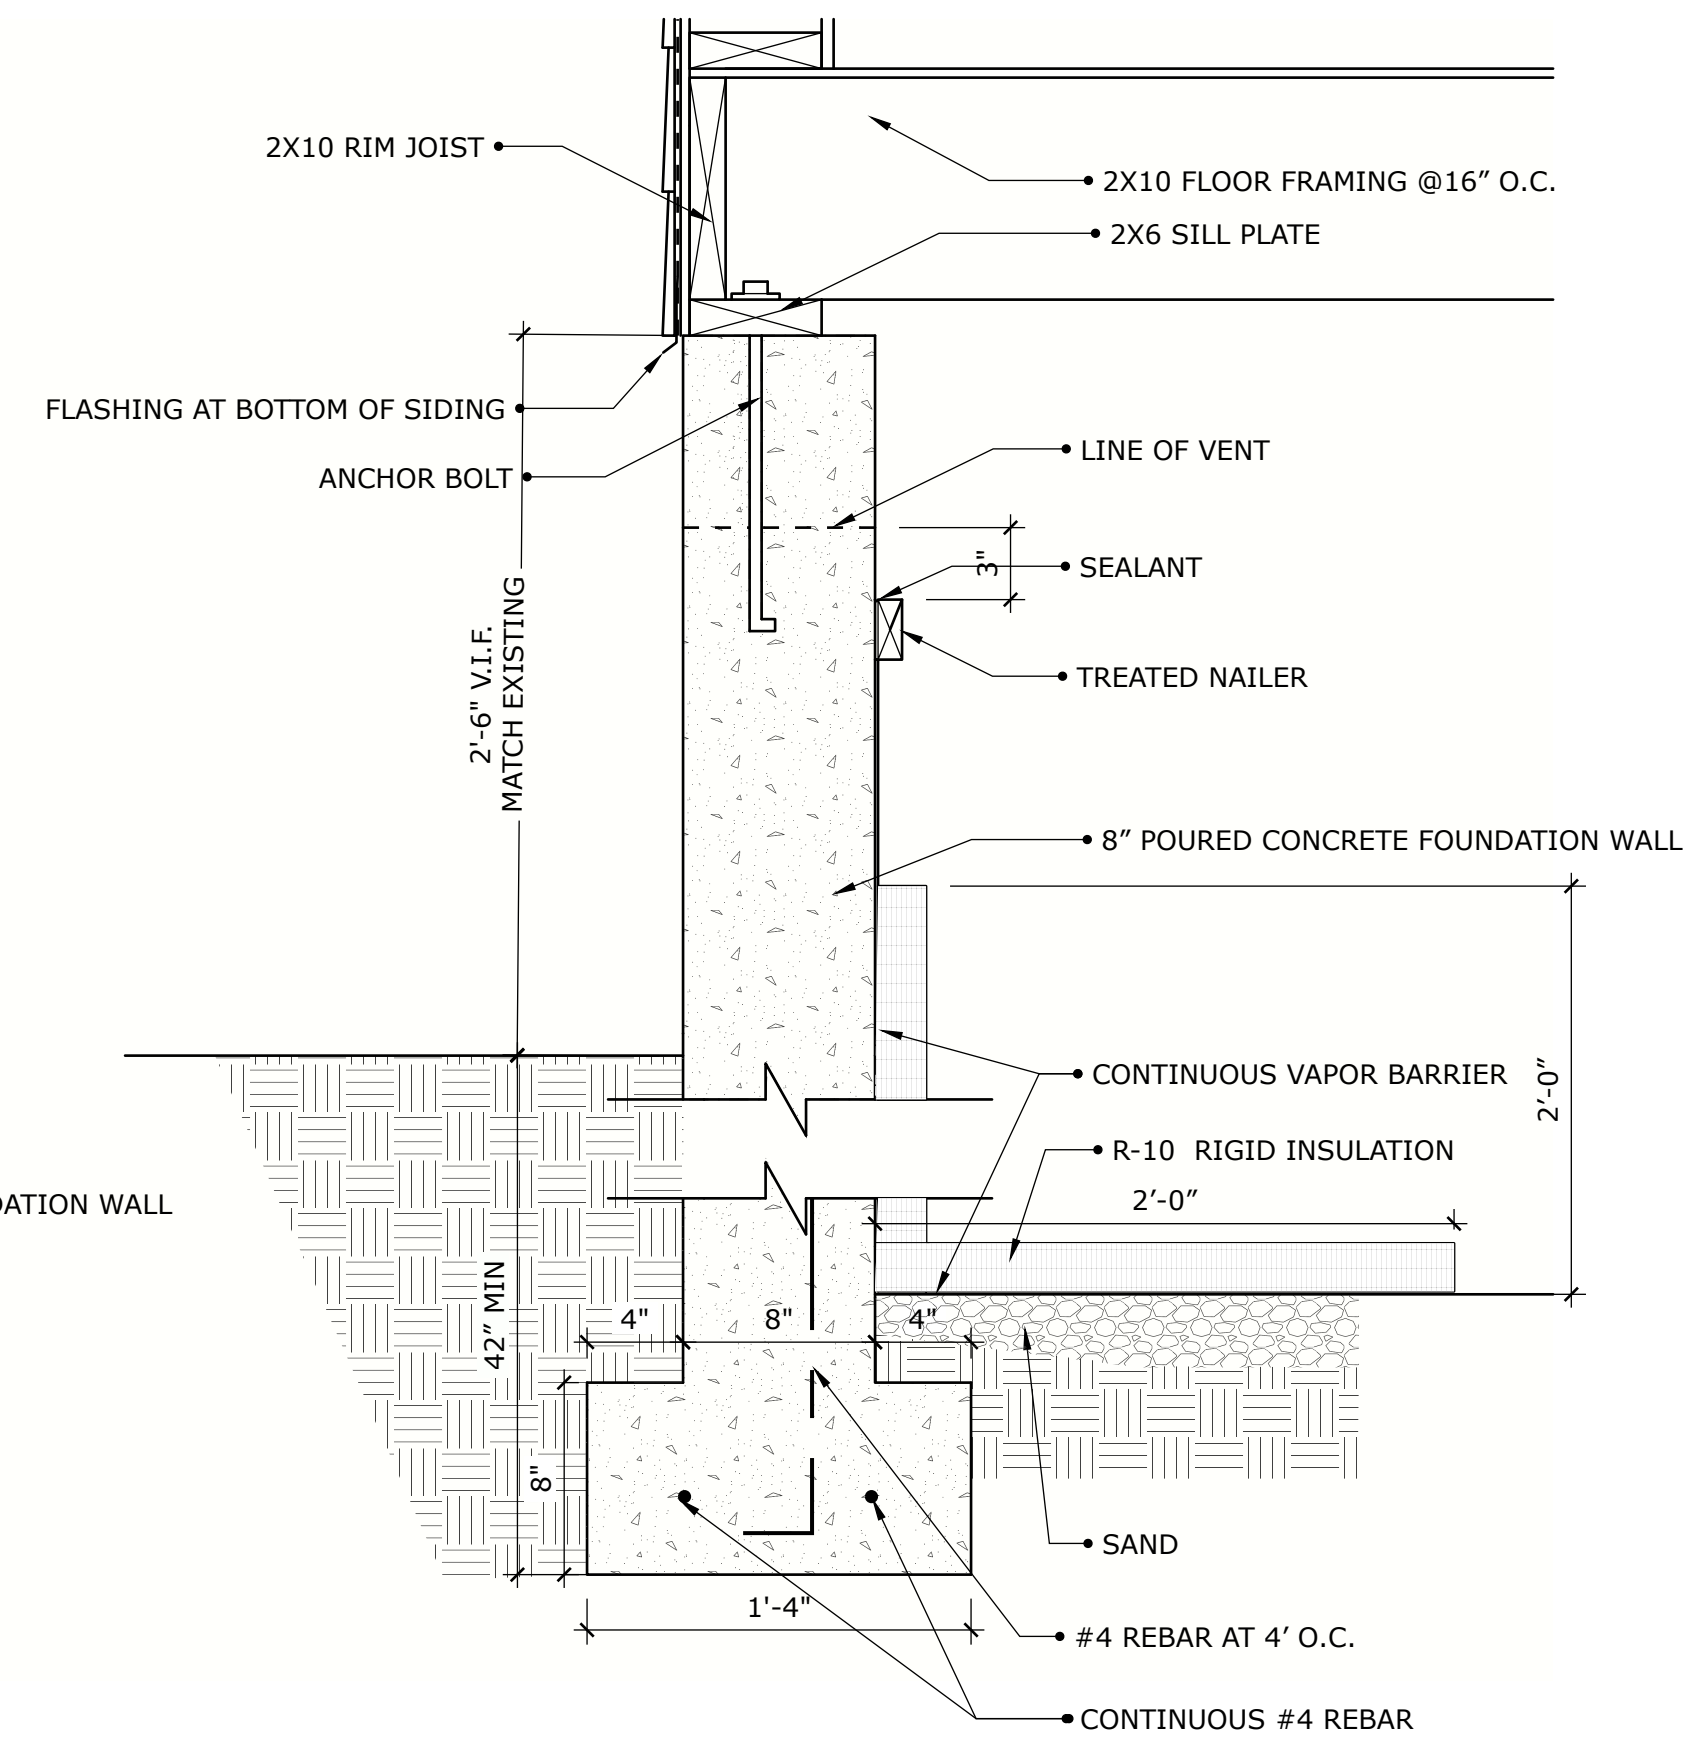


5 FOUNDATION DETAIL
A-00 SCALE: 1 1/2" = 1'-0"

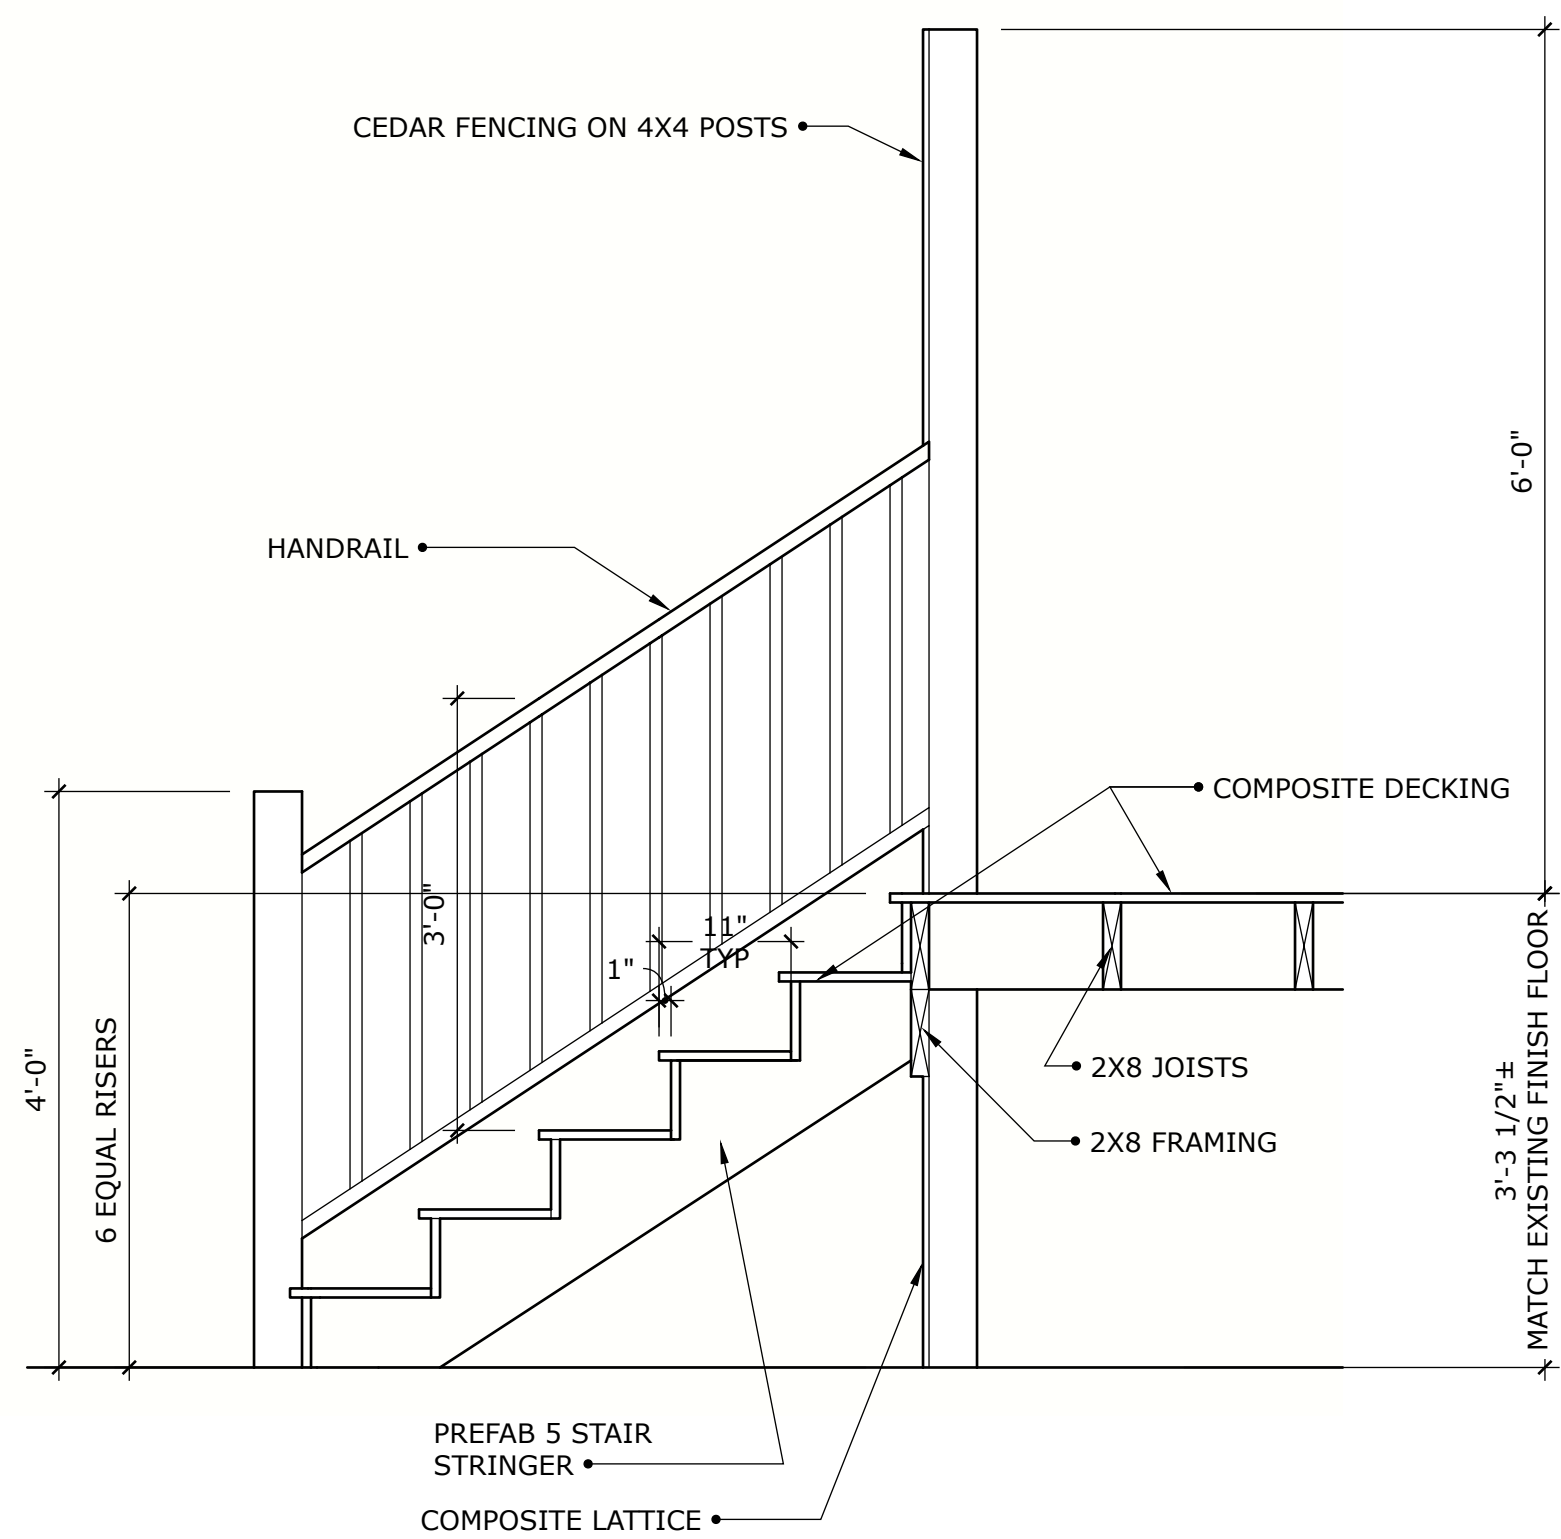


4 DECK STAIR SECTION
A-00 SCALE: 3/4" = 1'-0"

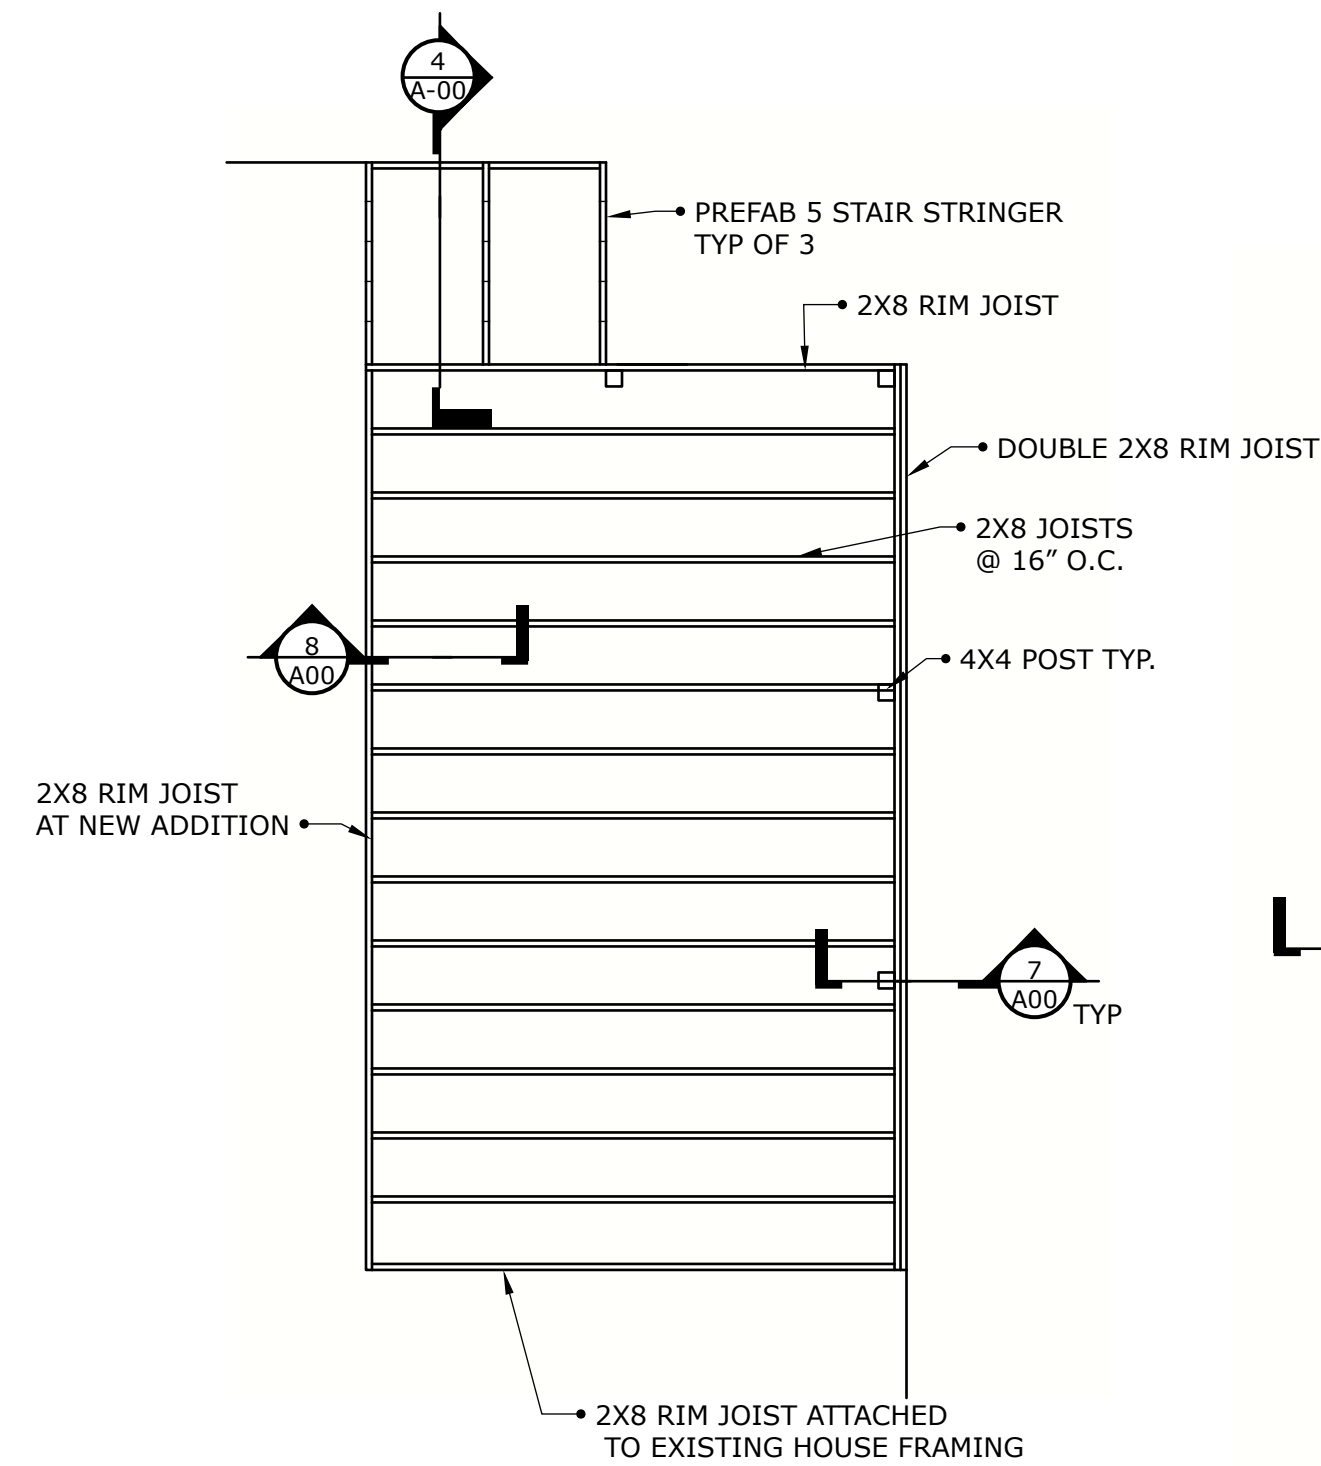


3 DECK FRAMING PLAN
A-00 SCALE: 1/4" = 1'-0"

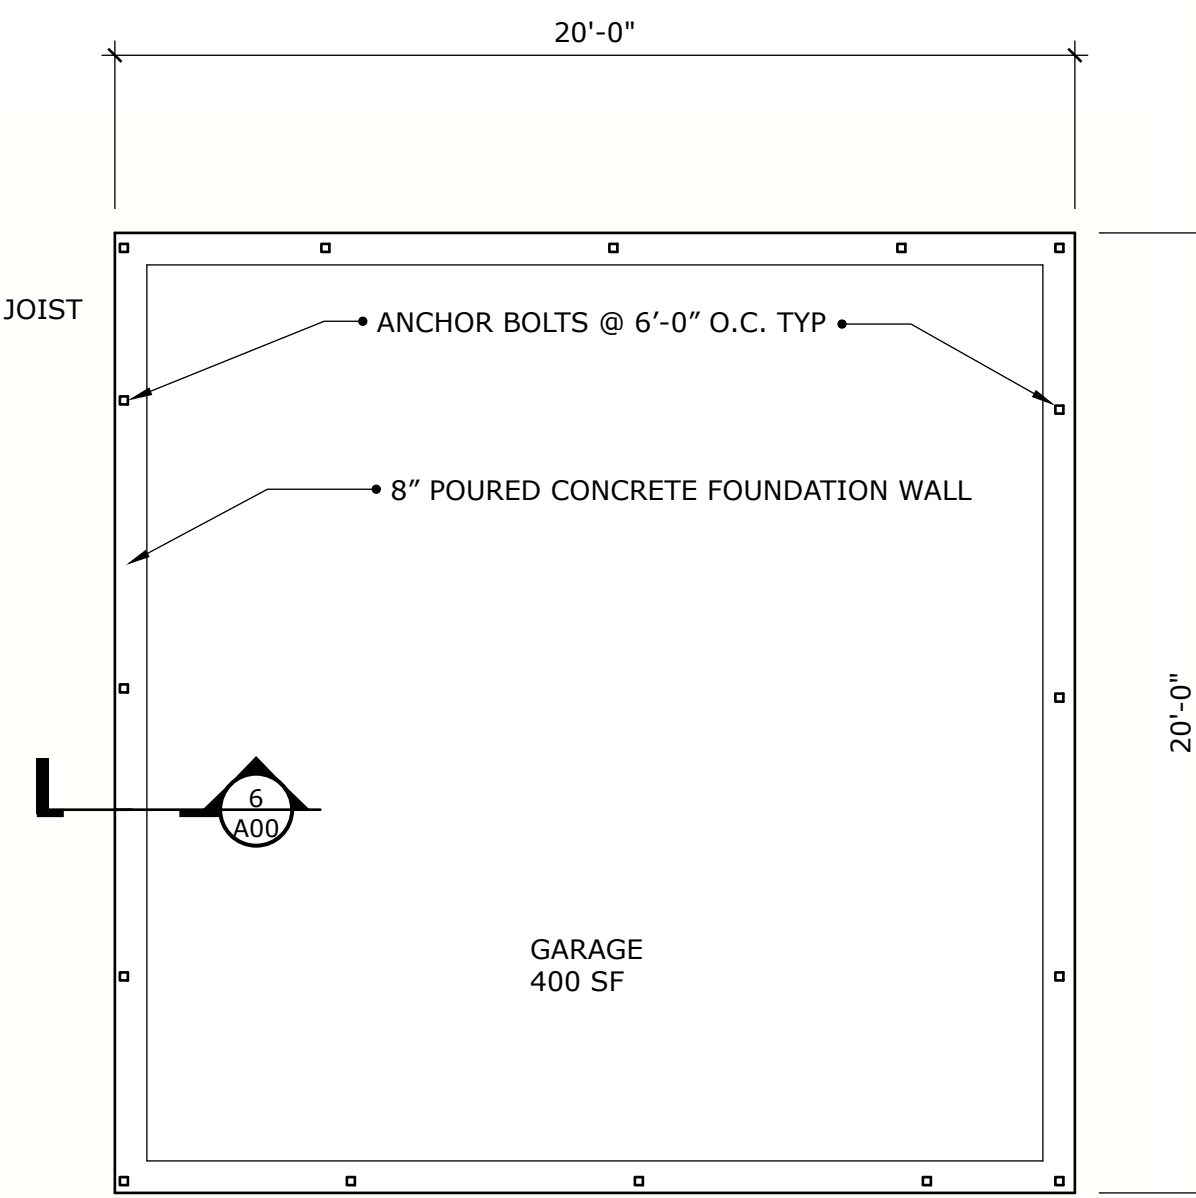


2 GARAGE FOUNDATION PLAN
A-00 SCALE: 1/4" = 1'-0"

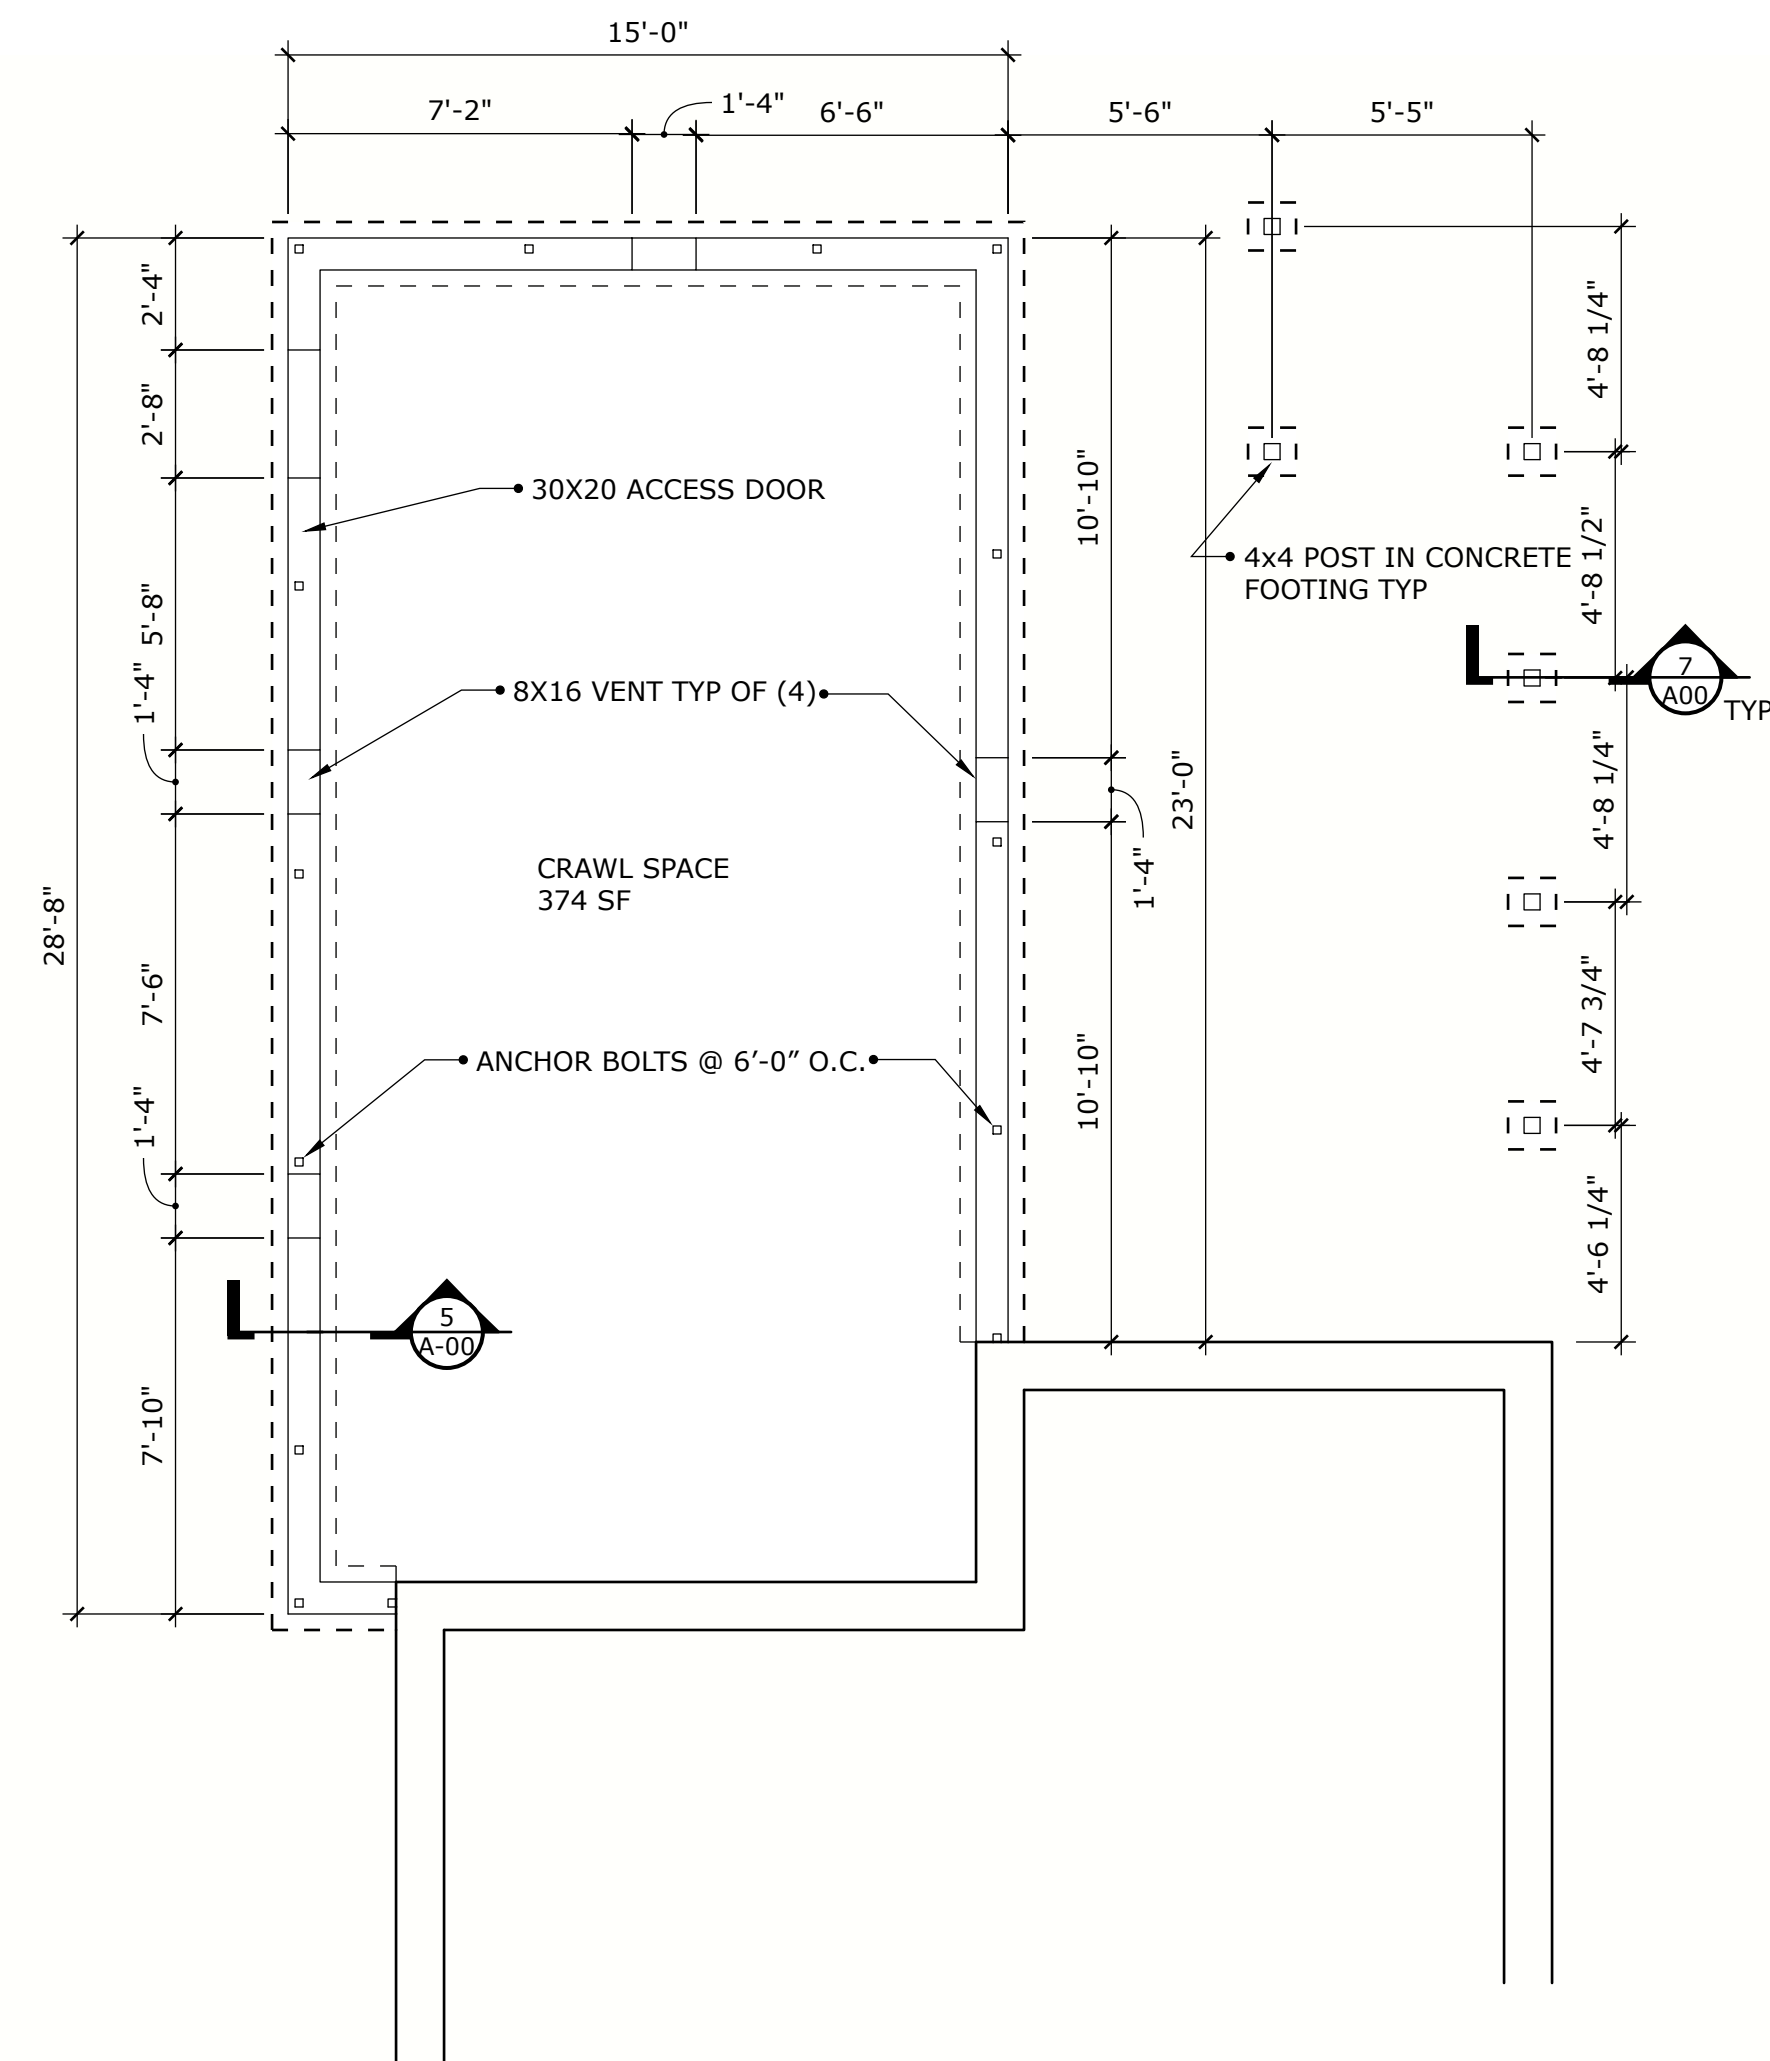


1 CRAWL SPACE FOUNDATION PLAN
A-00 SCALE: 1/4" = 1'-0"

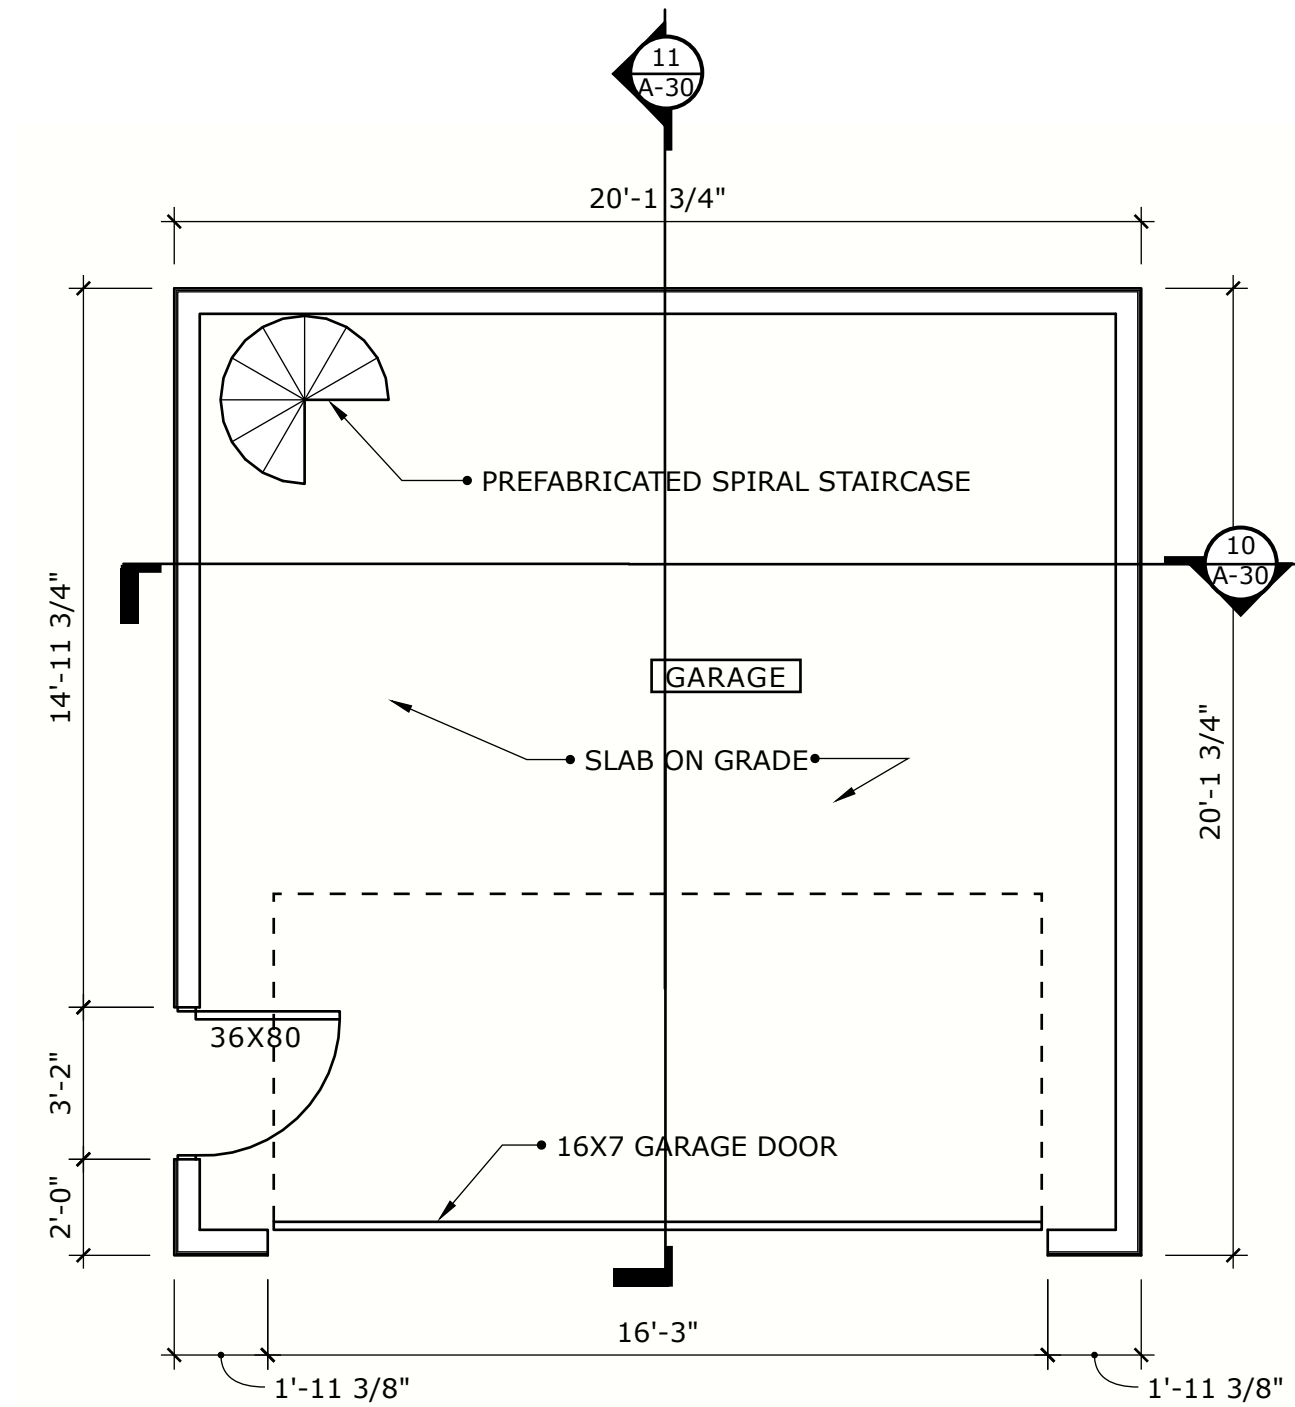


5 GARAGE PLAN
A-10 SCALE: 1/4" = 1'-0"

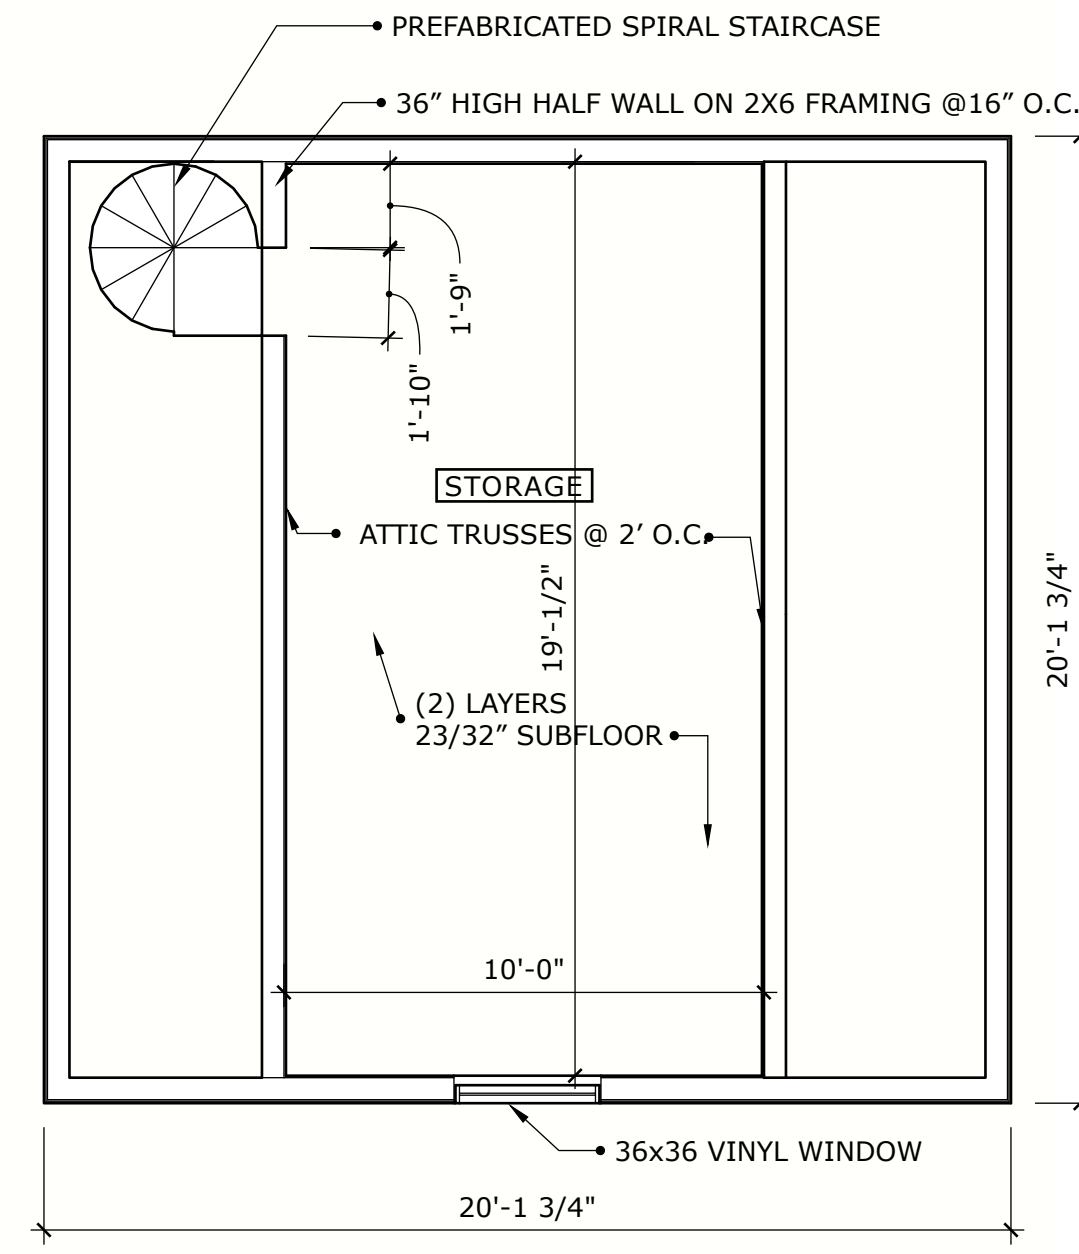


7 ADDITION ROOF EDGE DETAIL
A-10 SCALE: 1 1/2" = 1'-0"

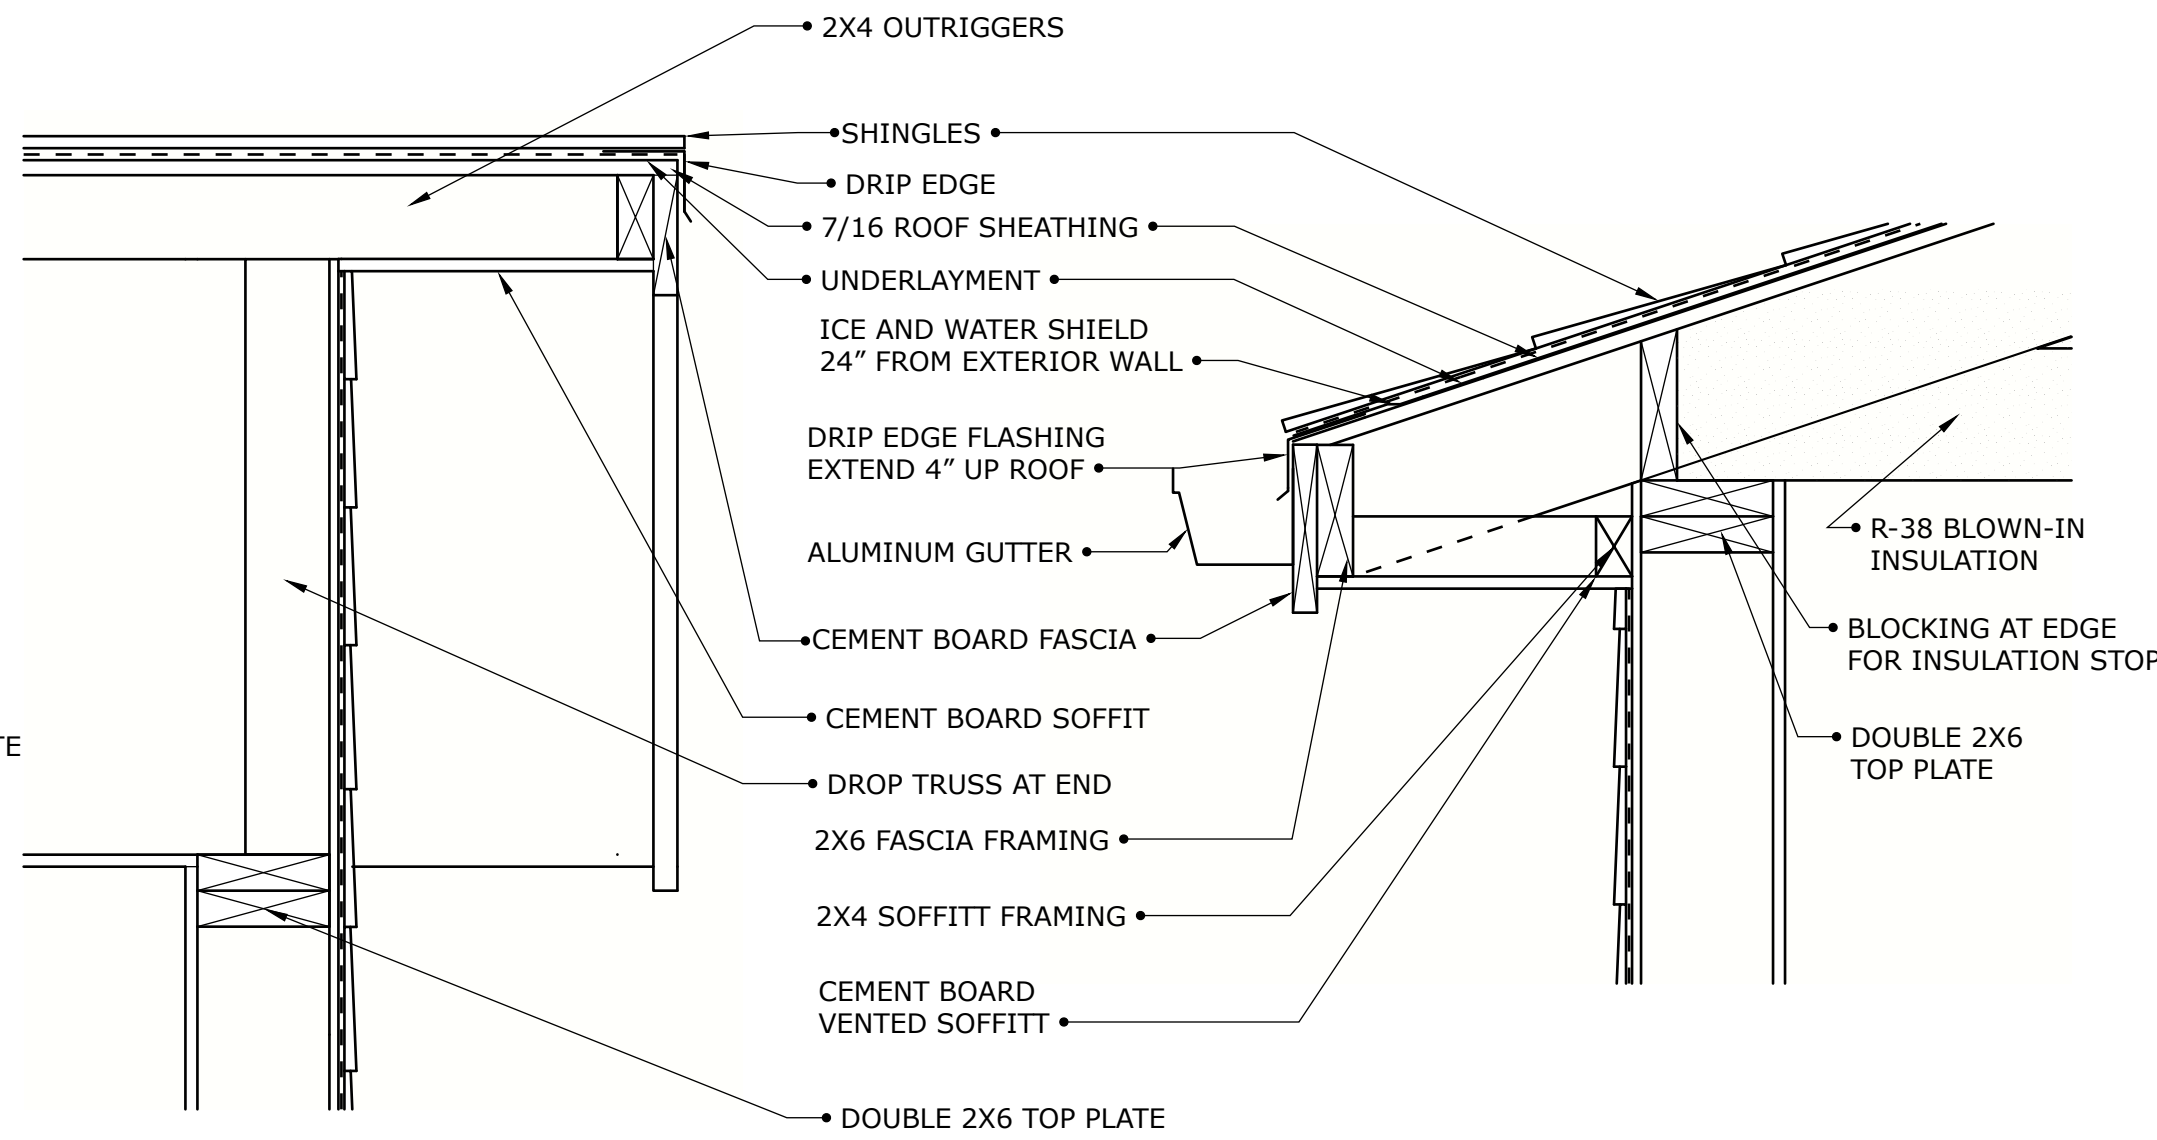


8 ADDITION ROOF EDGE DETAIL
A-10 SCALE: 1 1/2" = 1'-0"

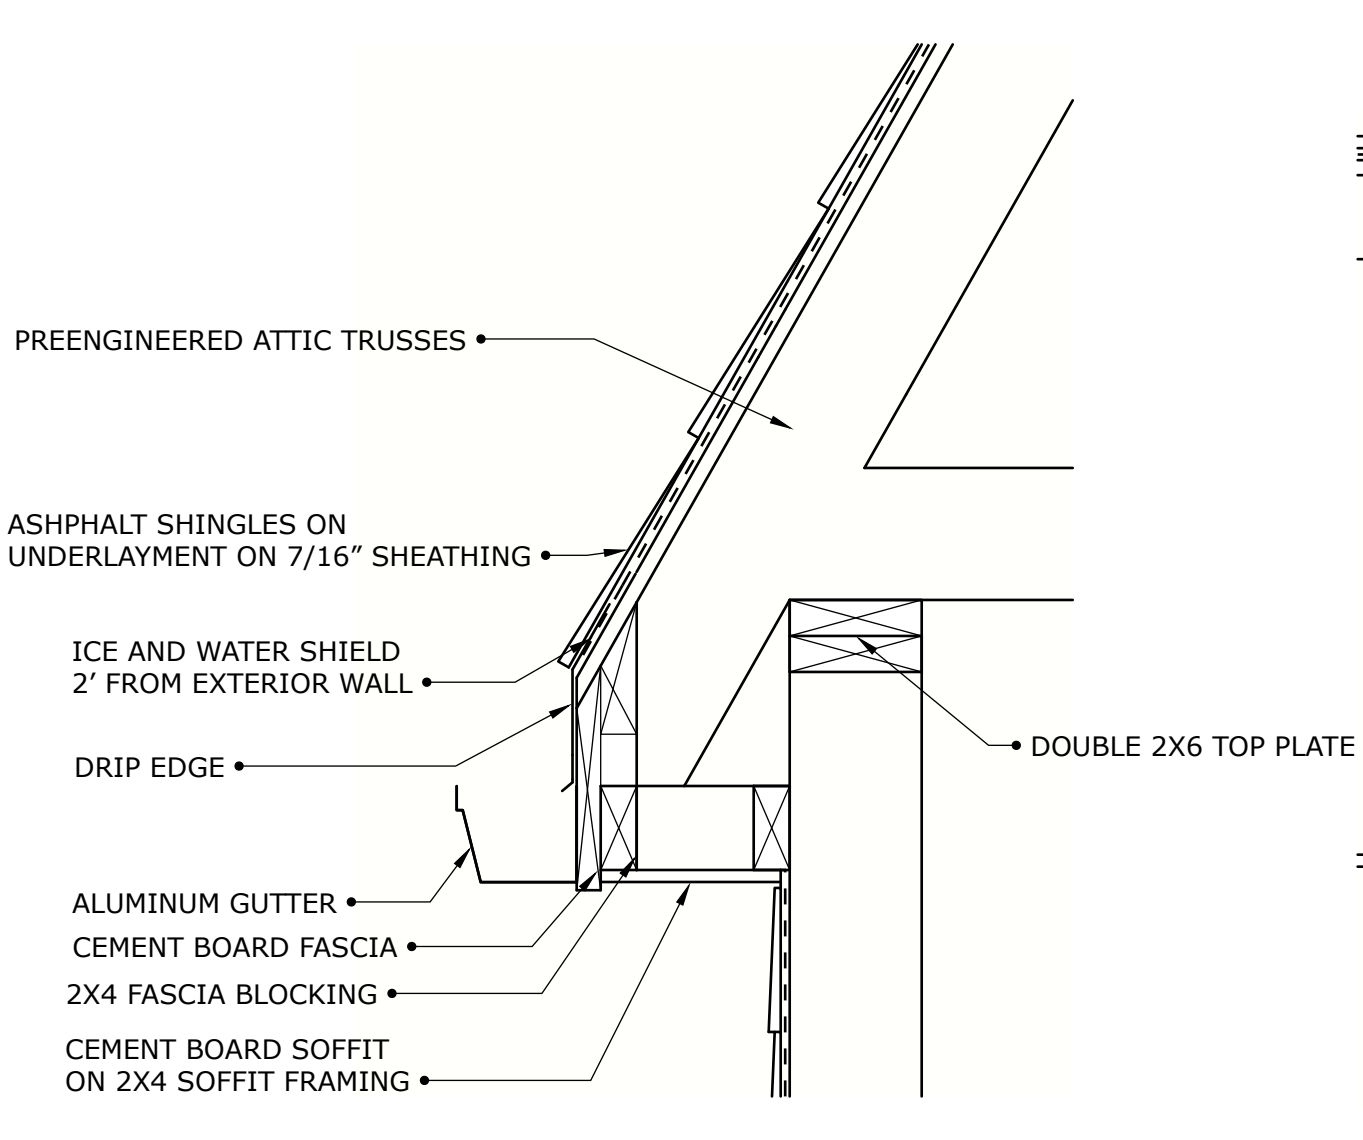


8 GARAGE ROOF EDGE DETAIL
A-10 SCALE: 1 1/2" = 1'-0"

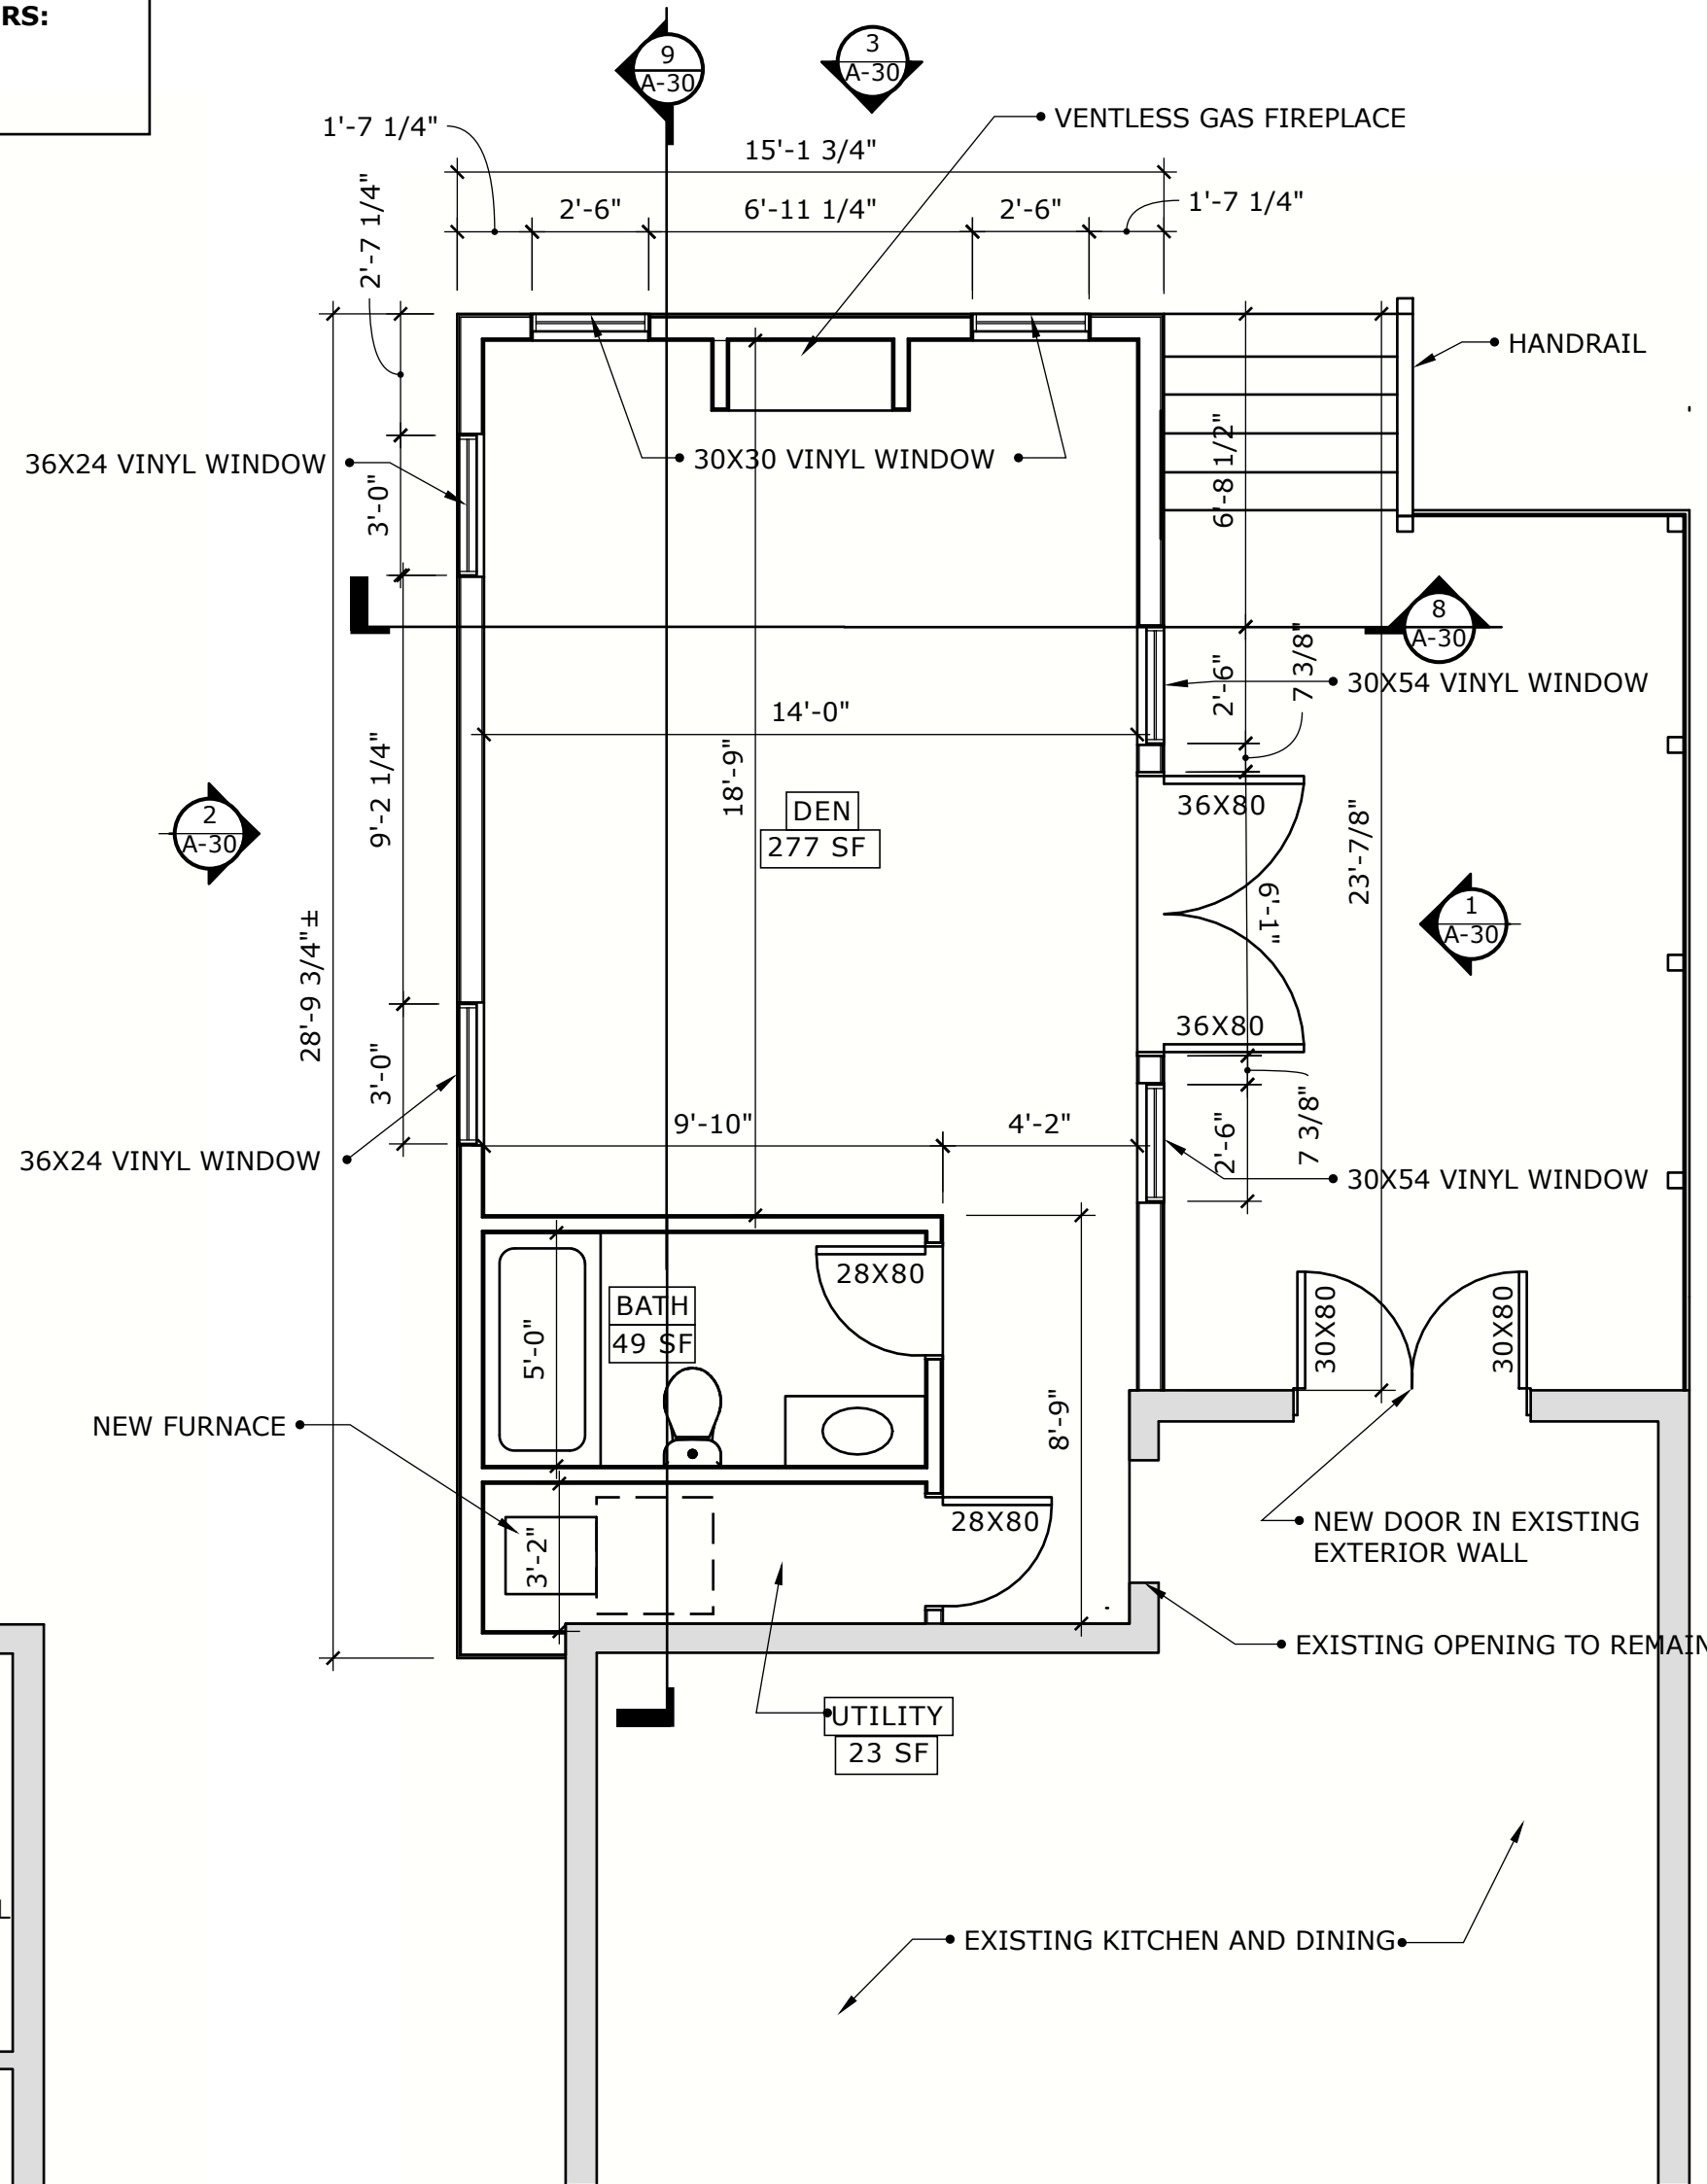


1 FIRST FLOOR PLAN
A-10 SCALE: 1/4" = 1'-0"

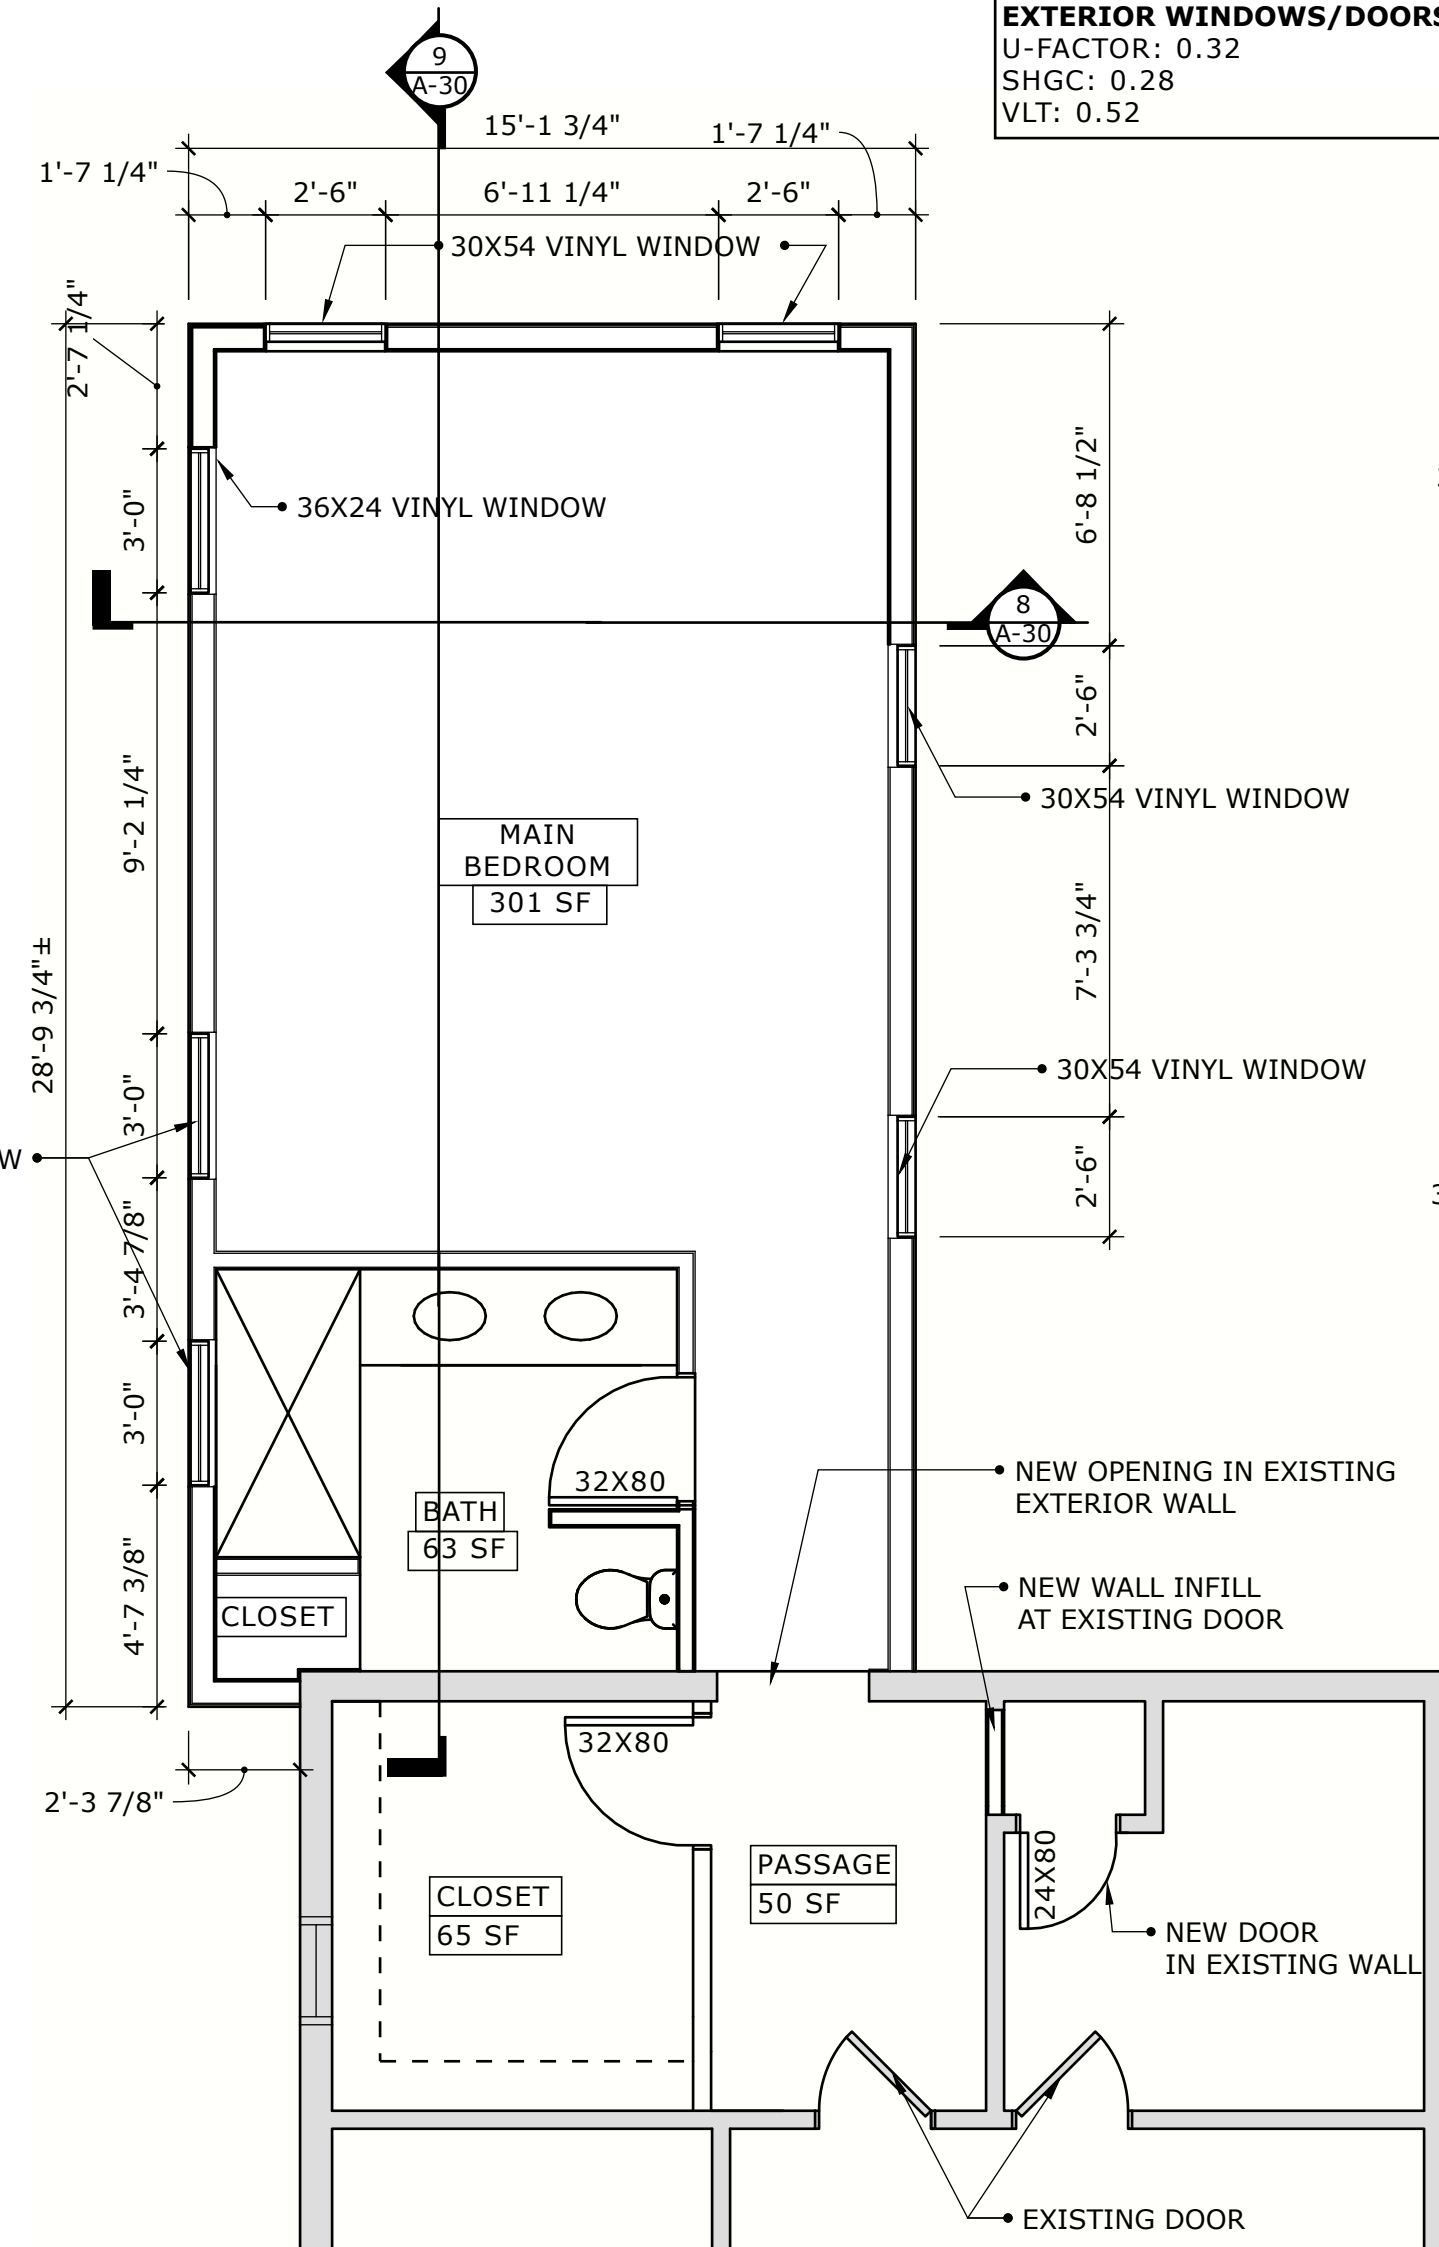


2 SECOND FLOOR PLAN
A-10 SCALE: 1/4" = 1'-0"





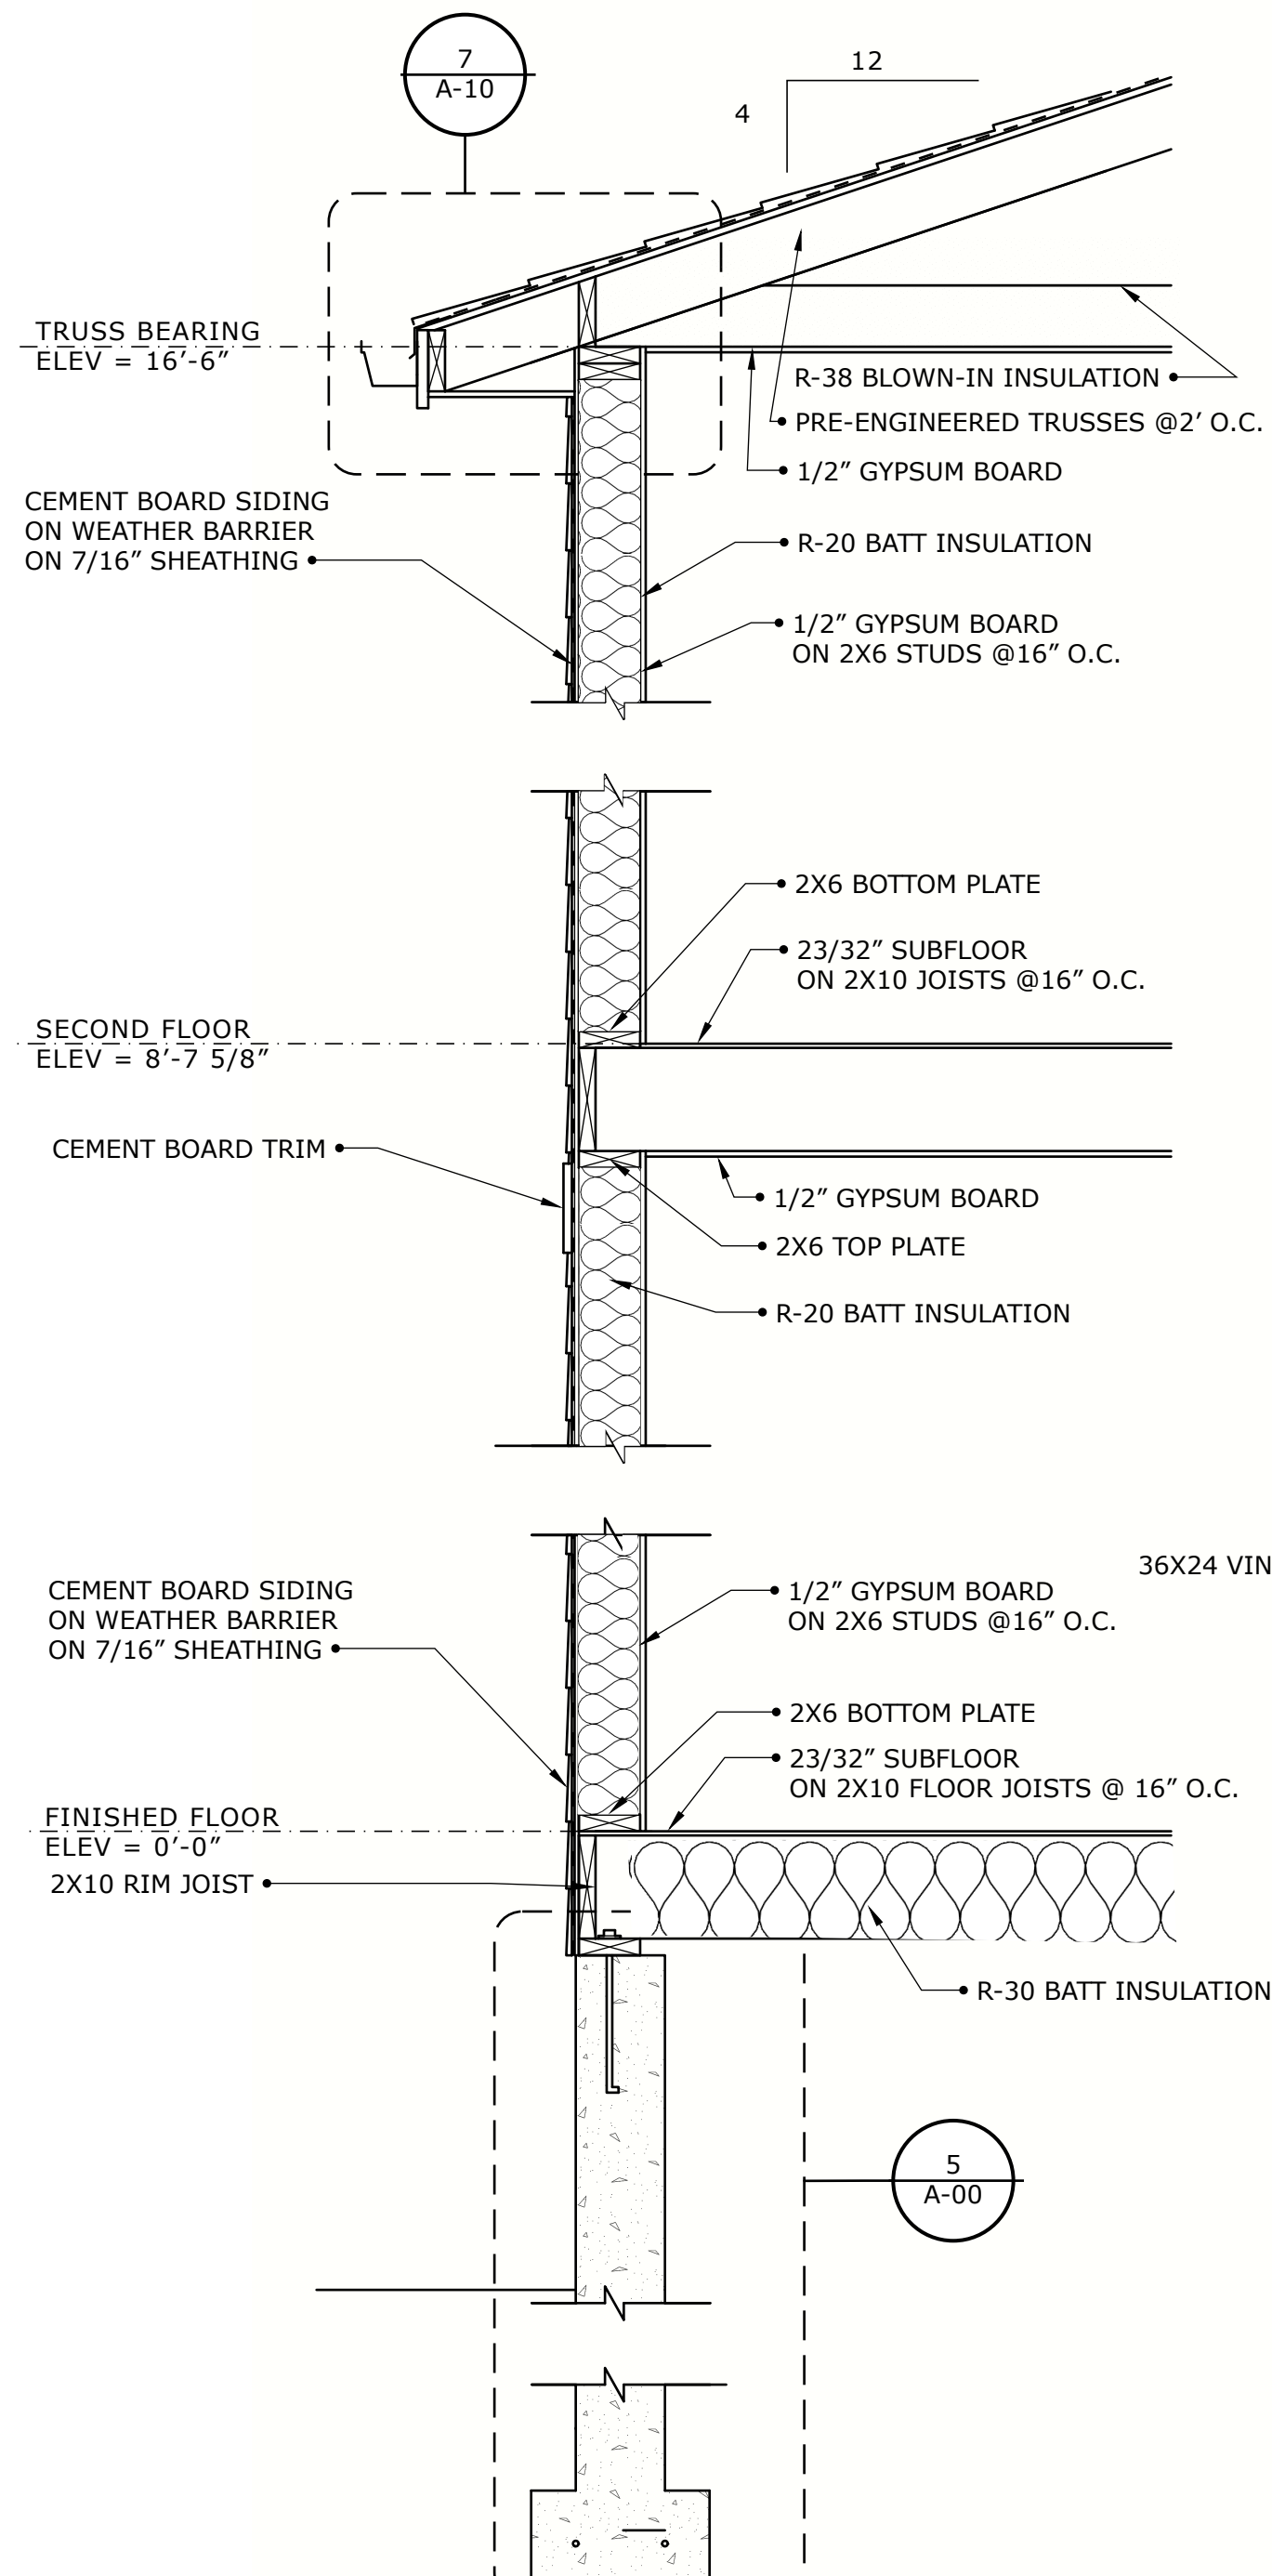



3 WALL SECTION
A-10 SCALE: 3/4" = 1'-0"

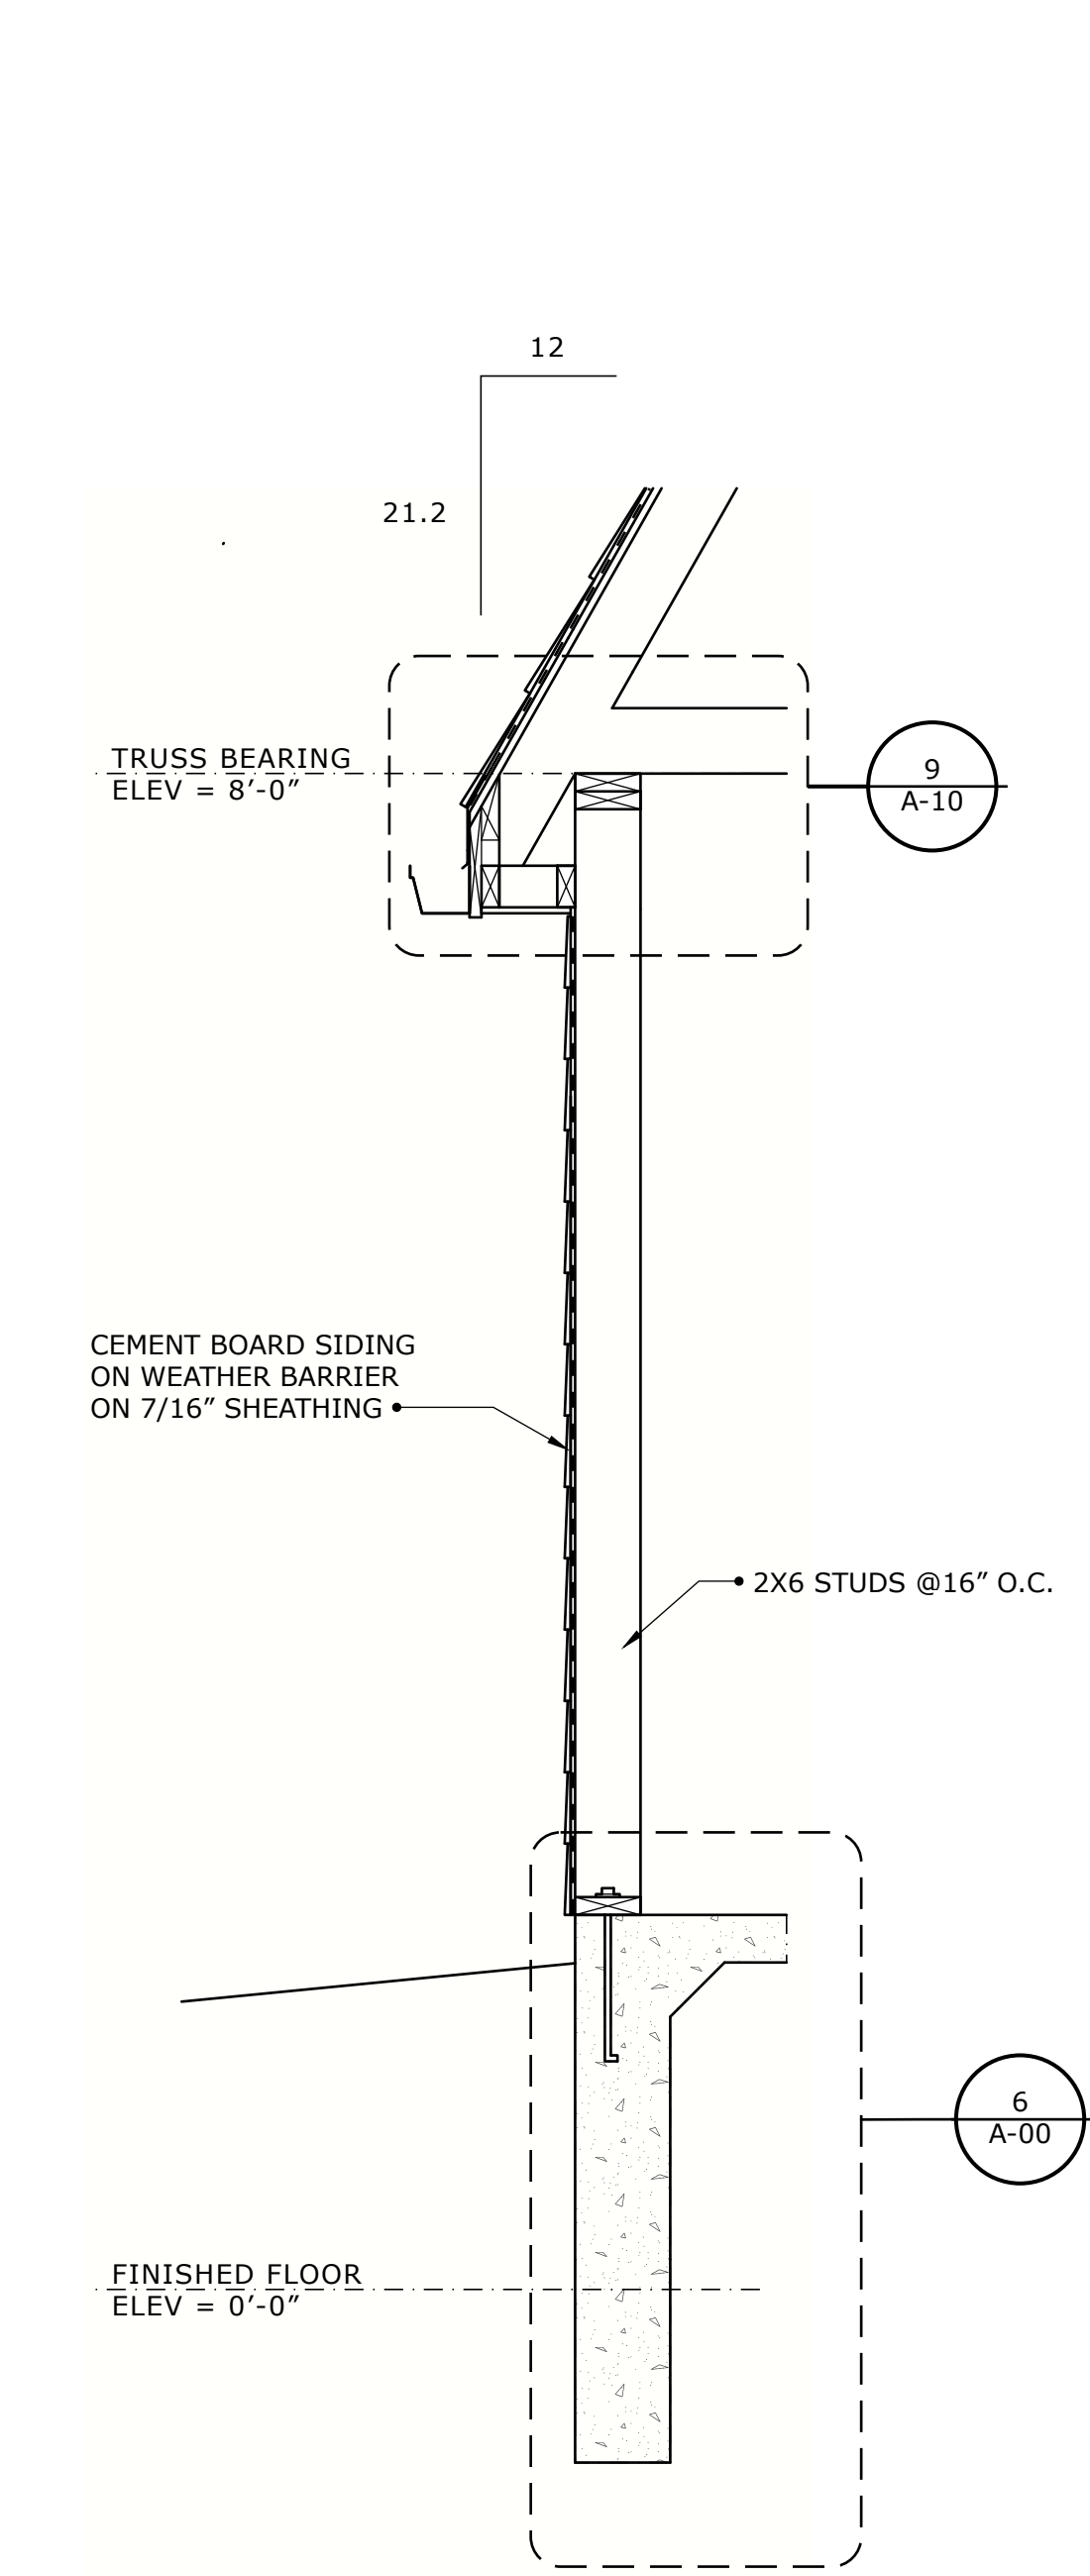


4 WALL SECTION
A-10 SCALE: 3/4" = 1'-0"

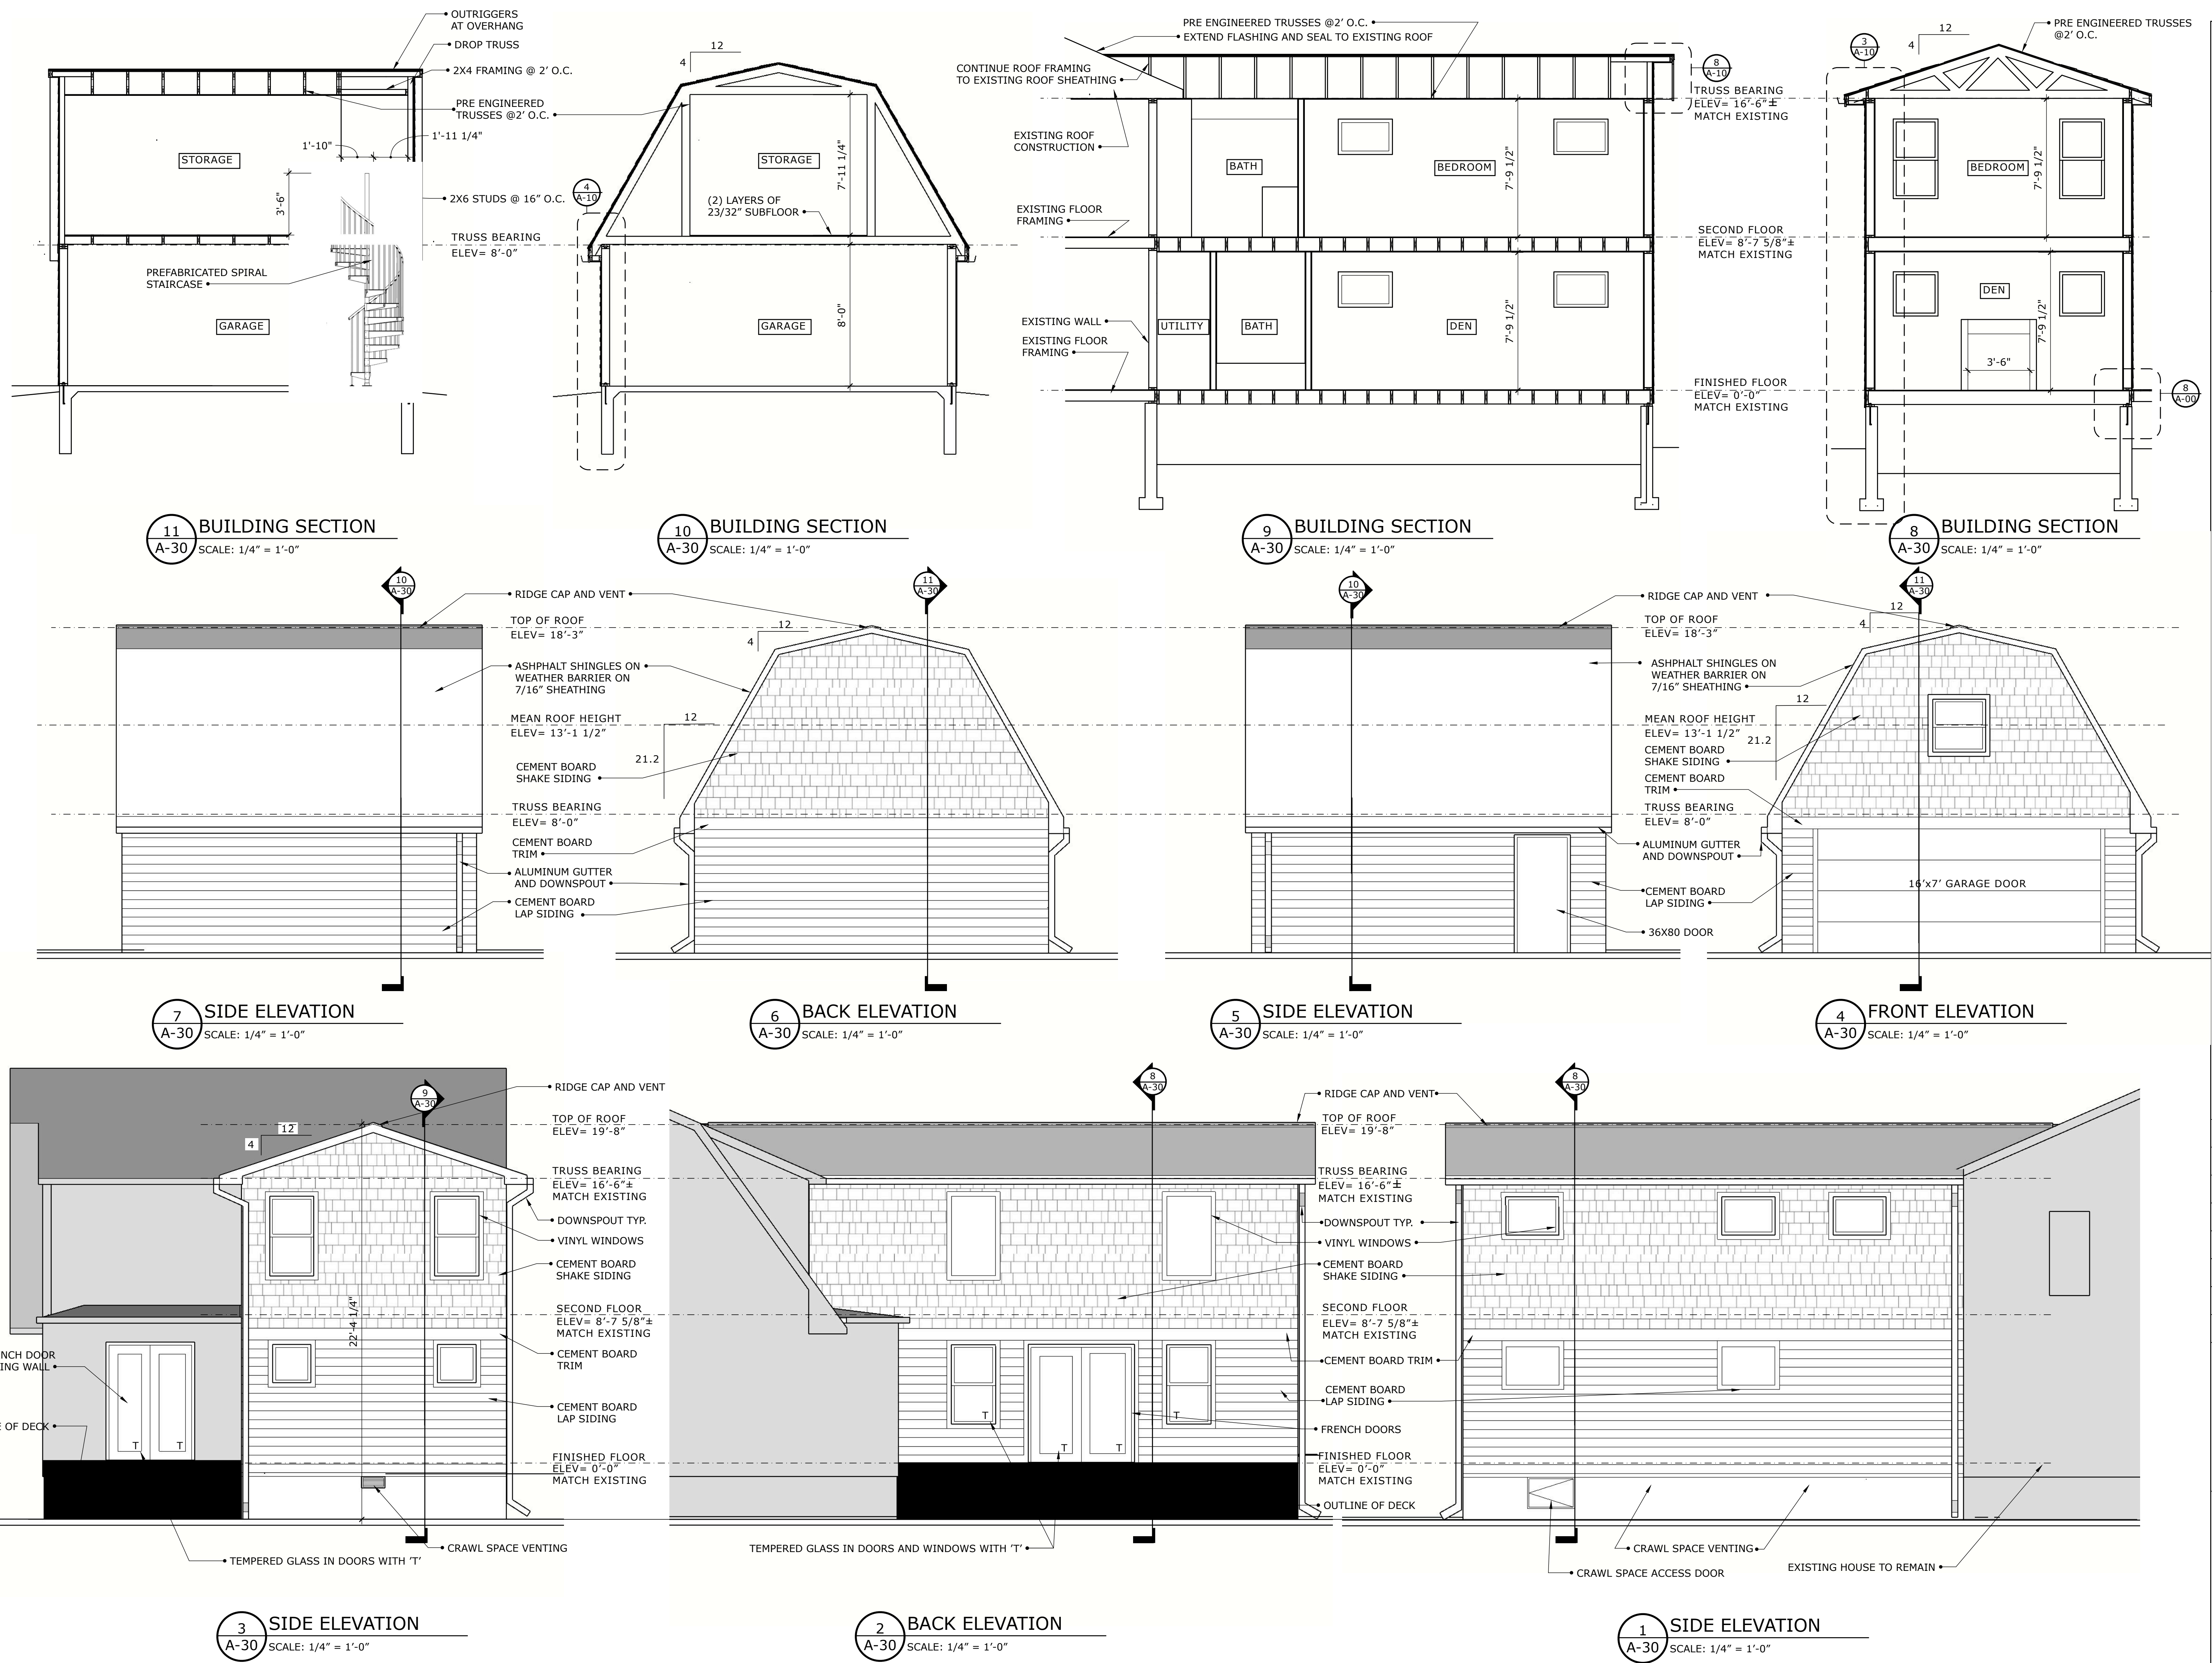

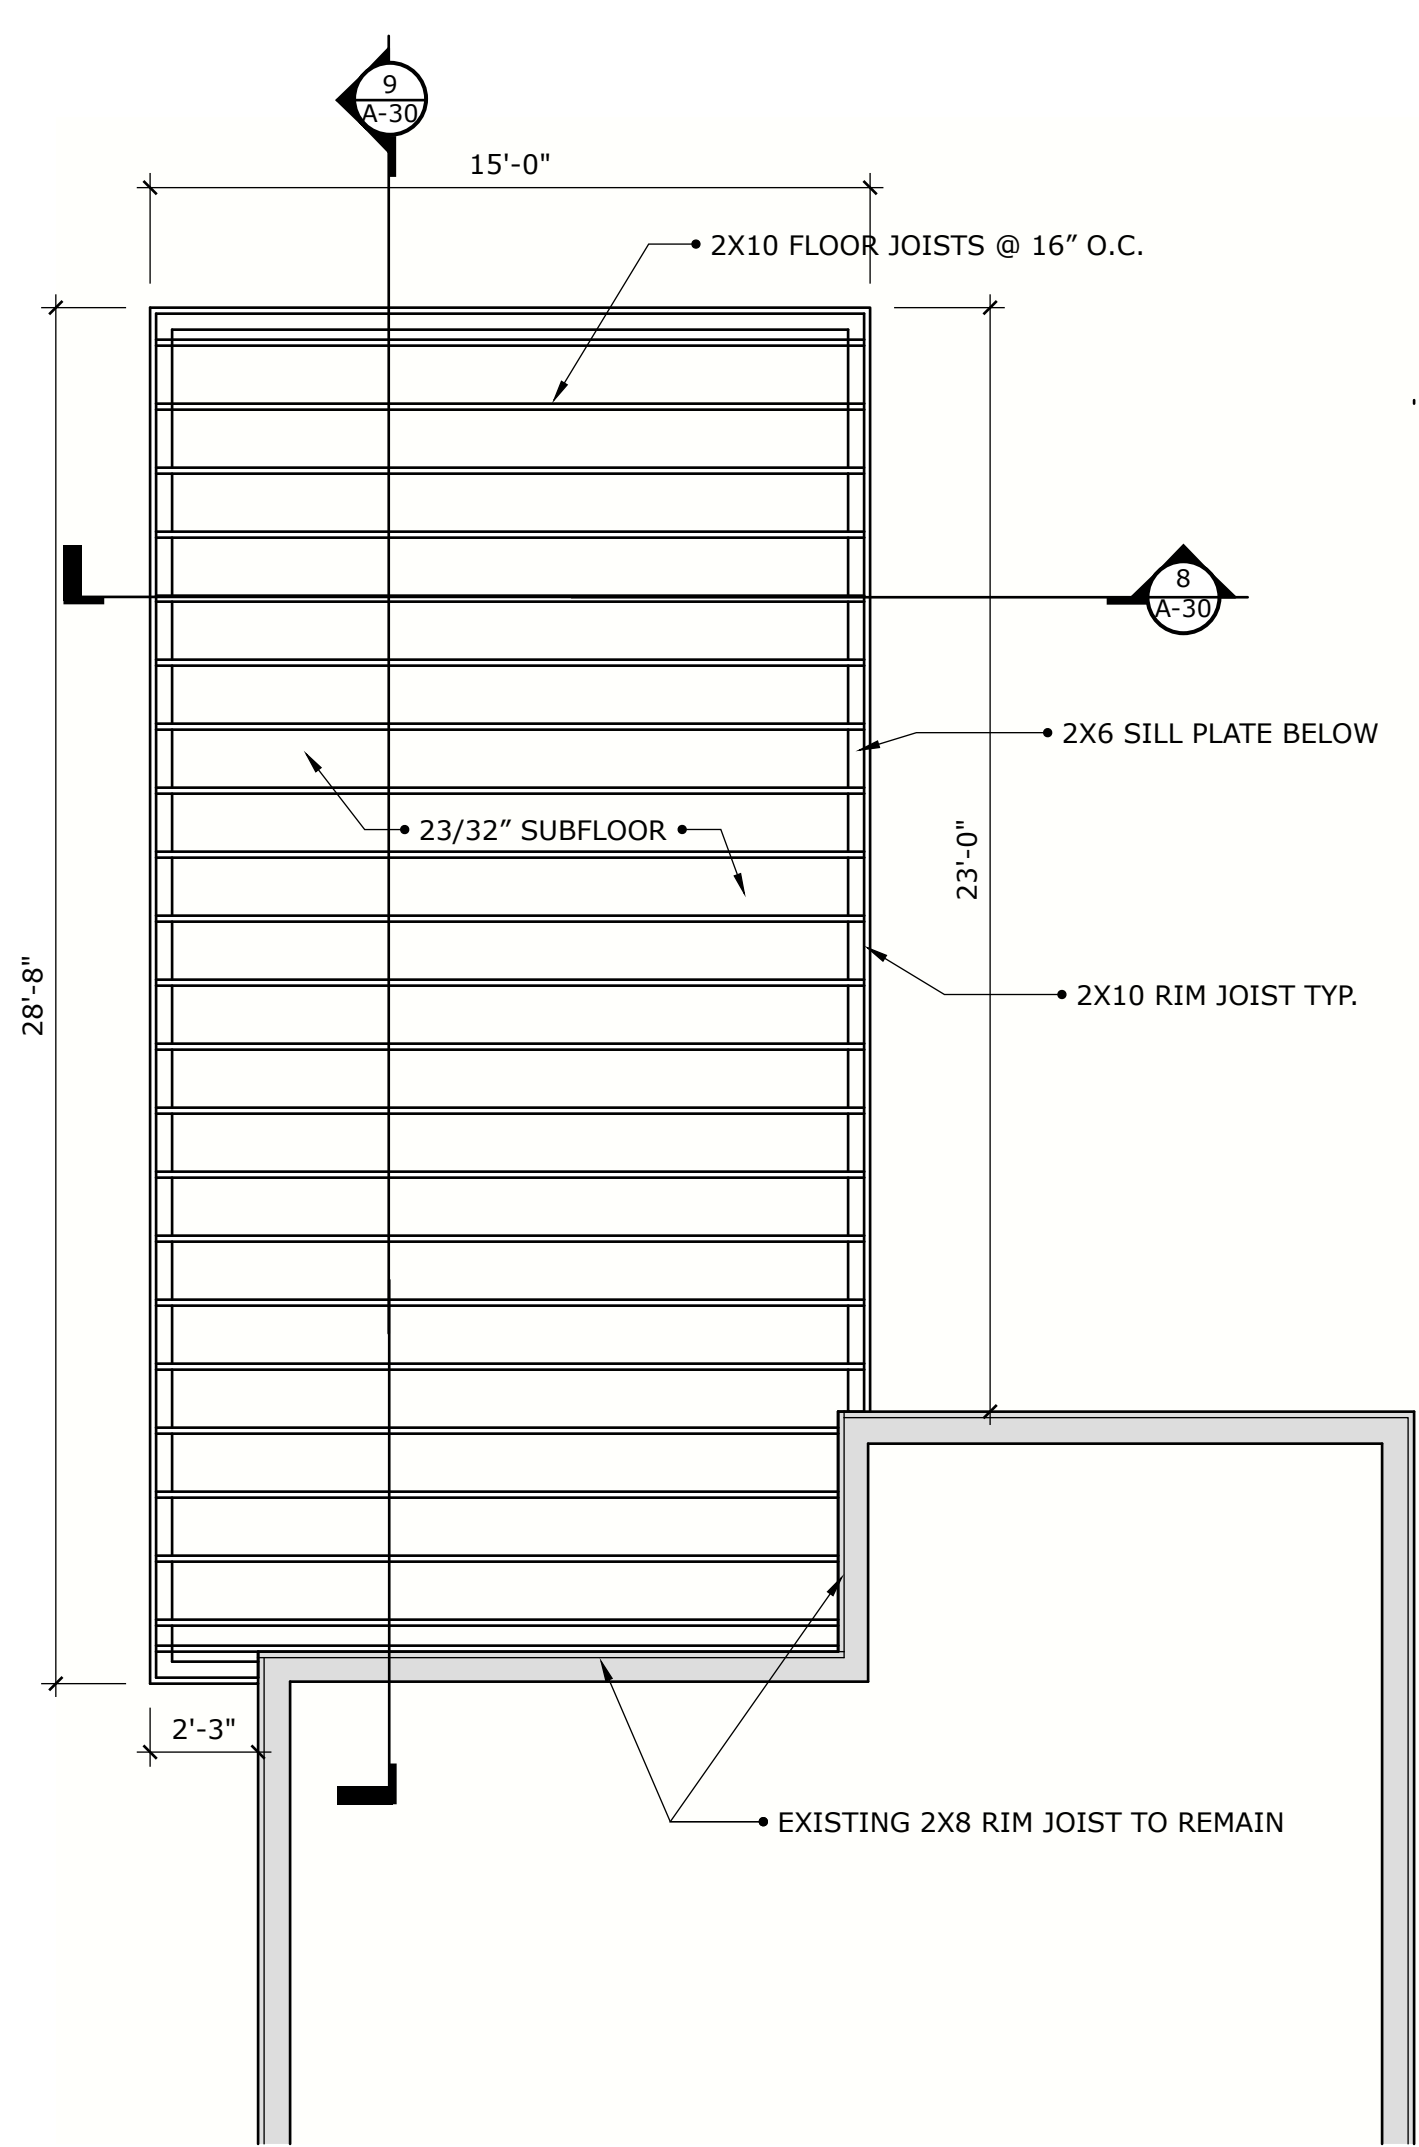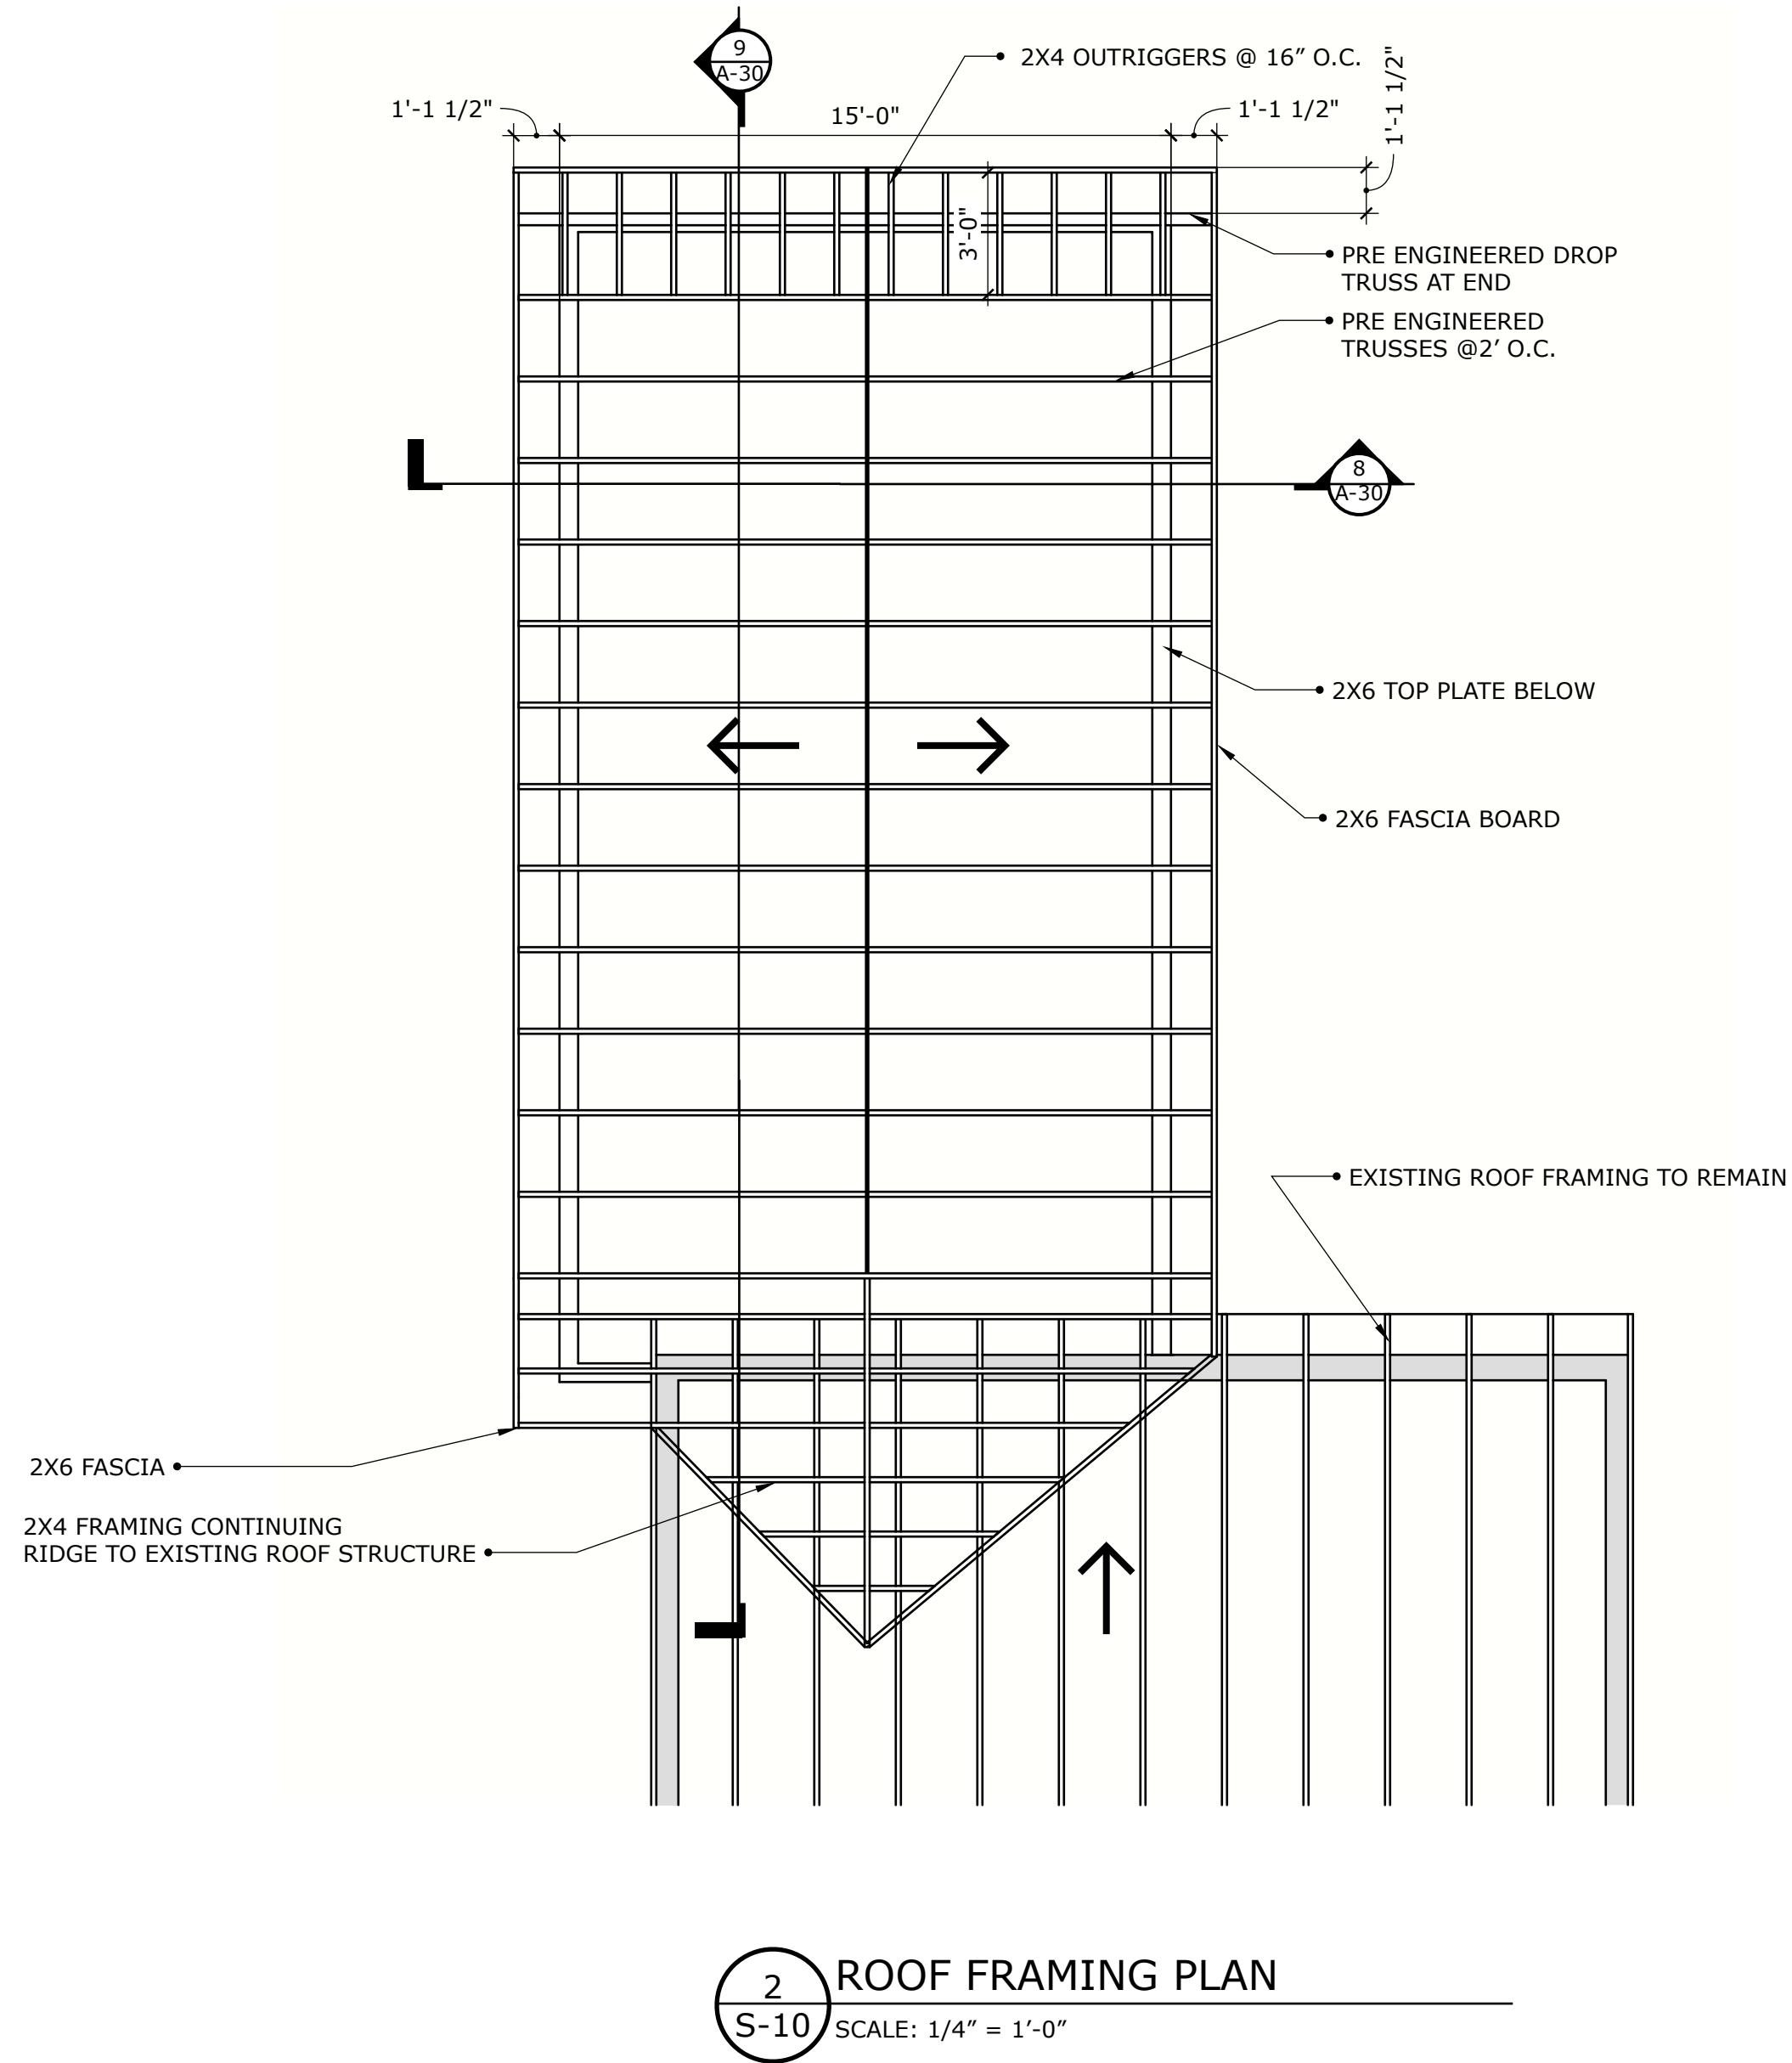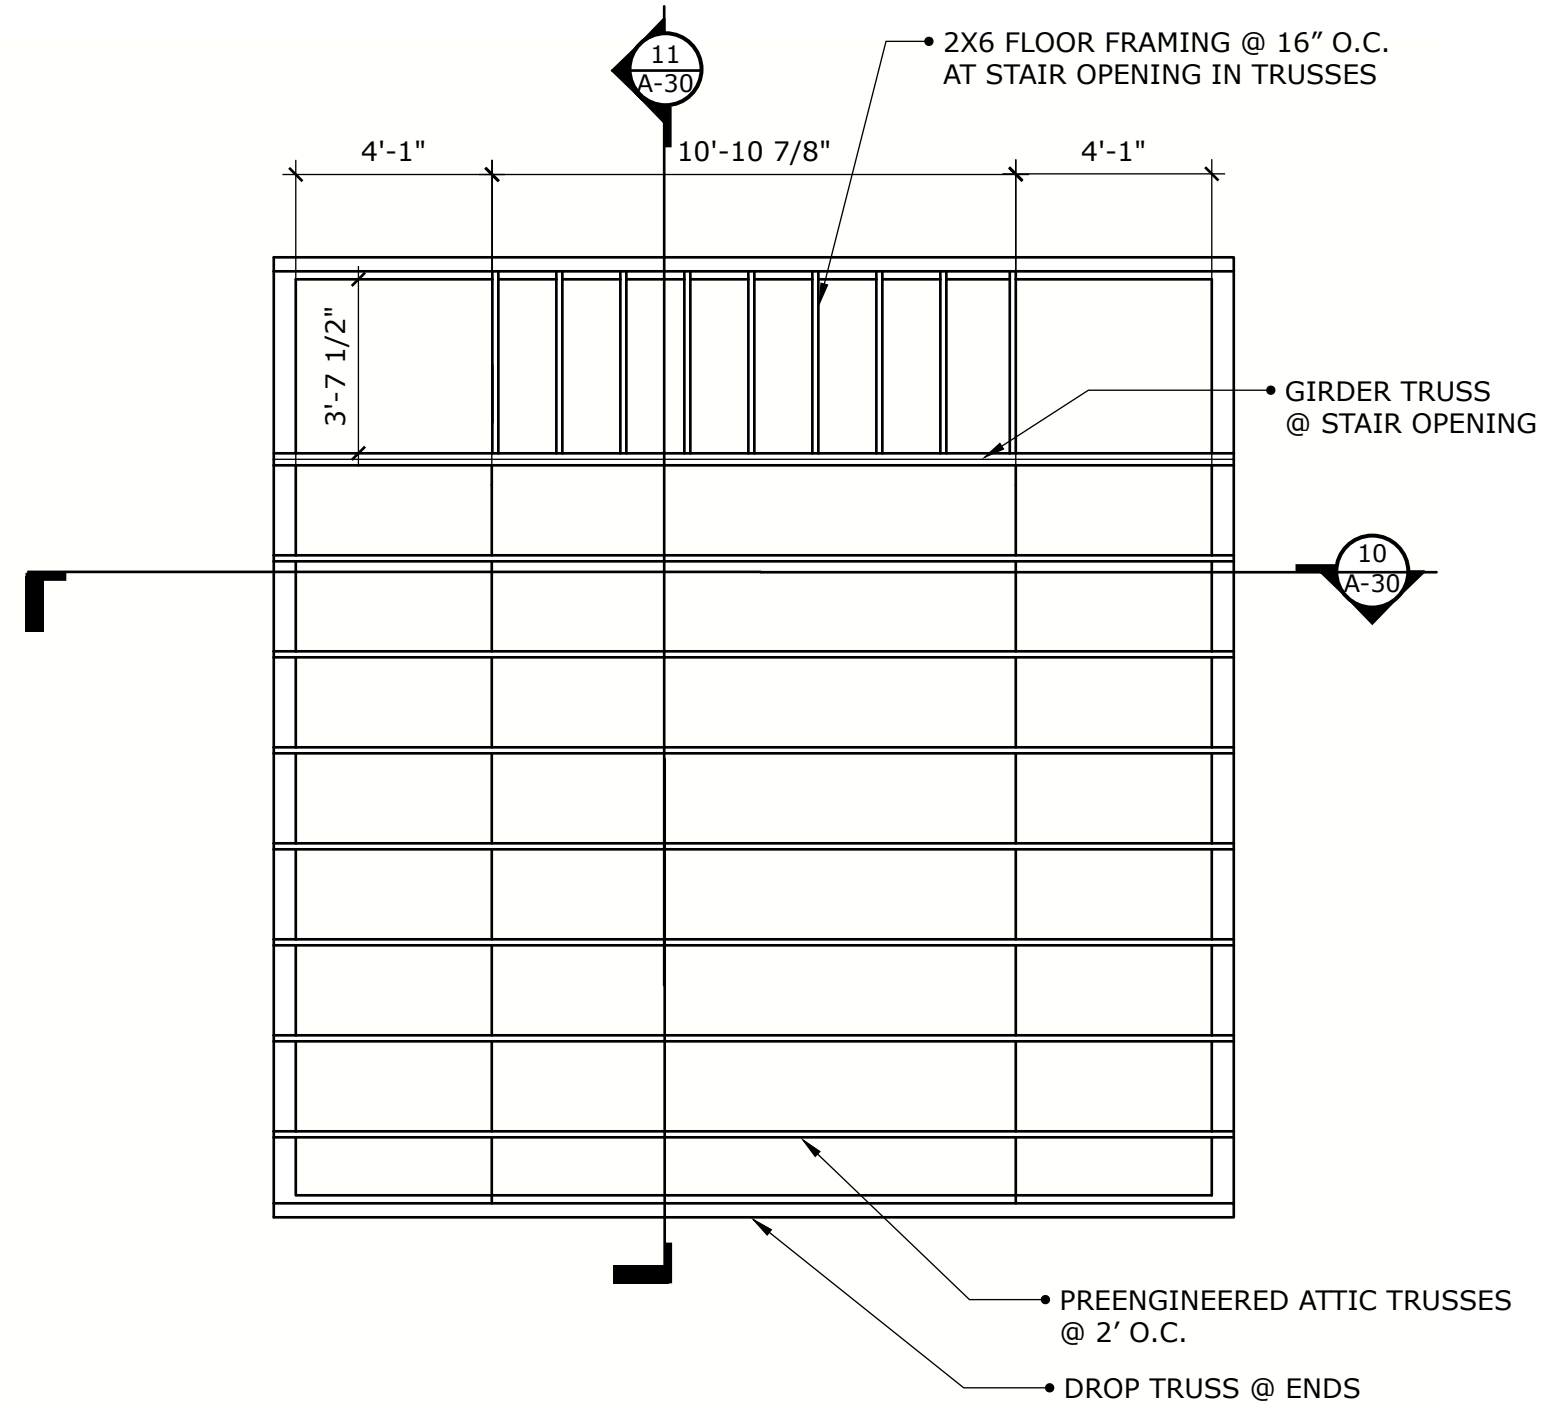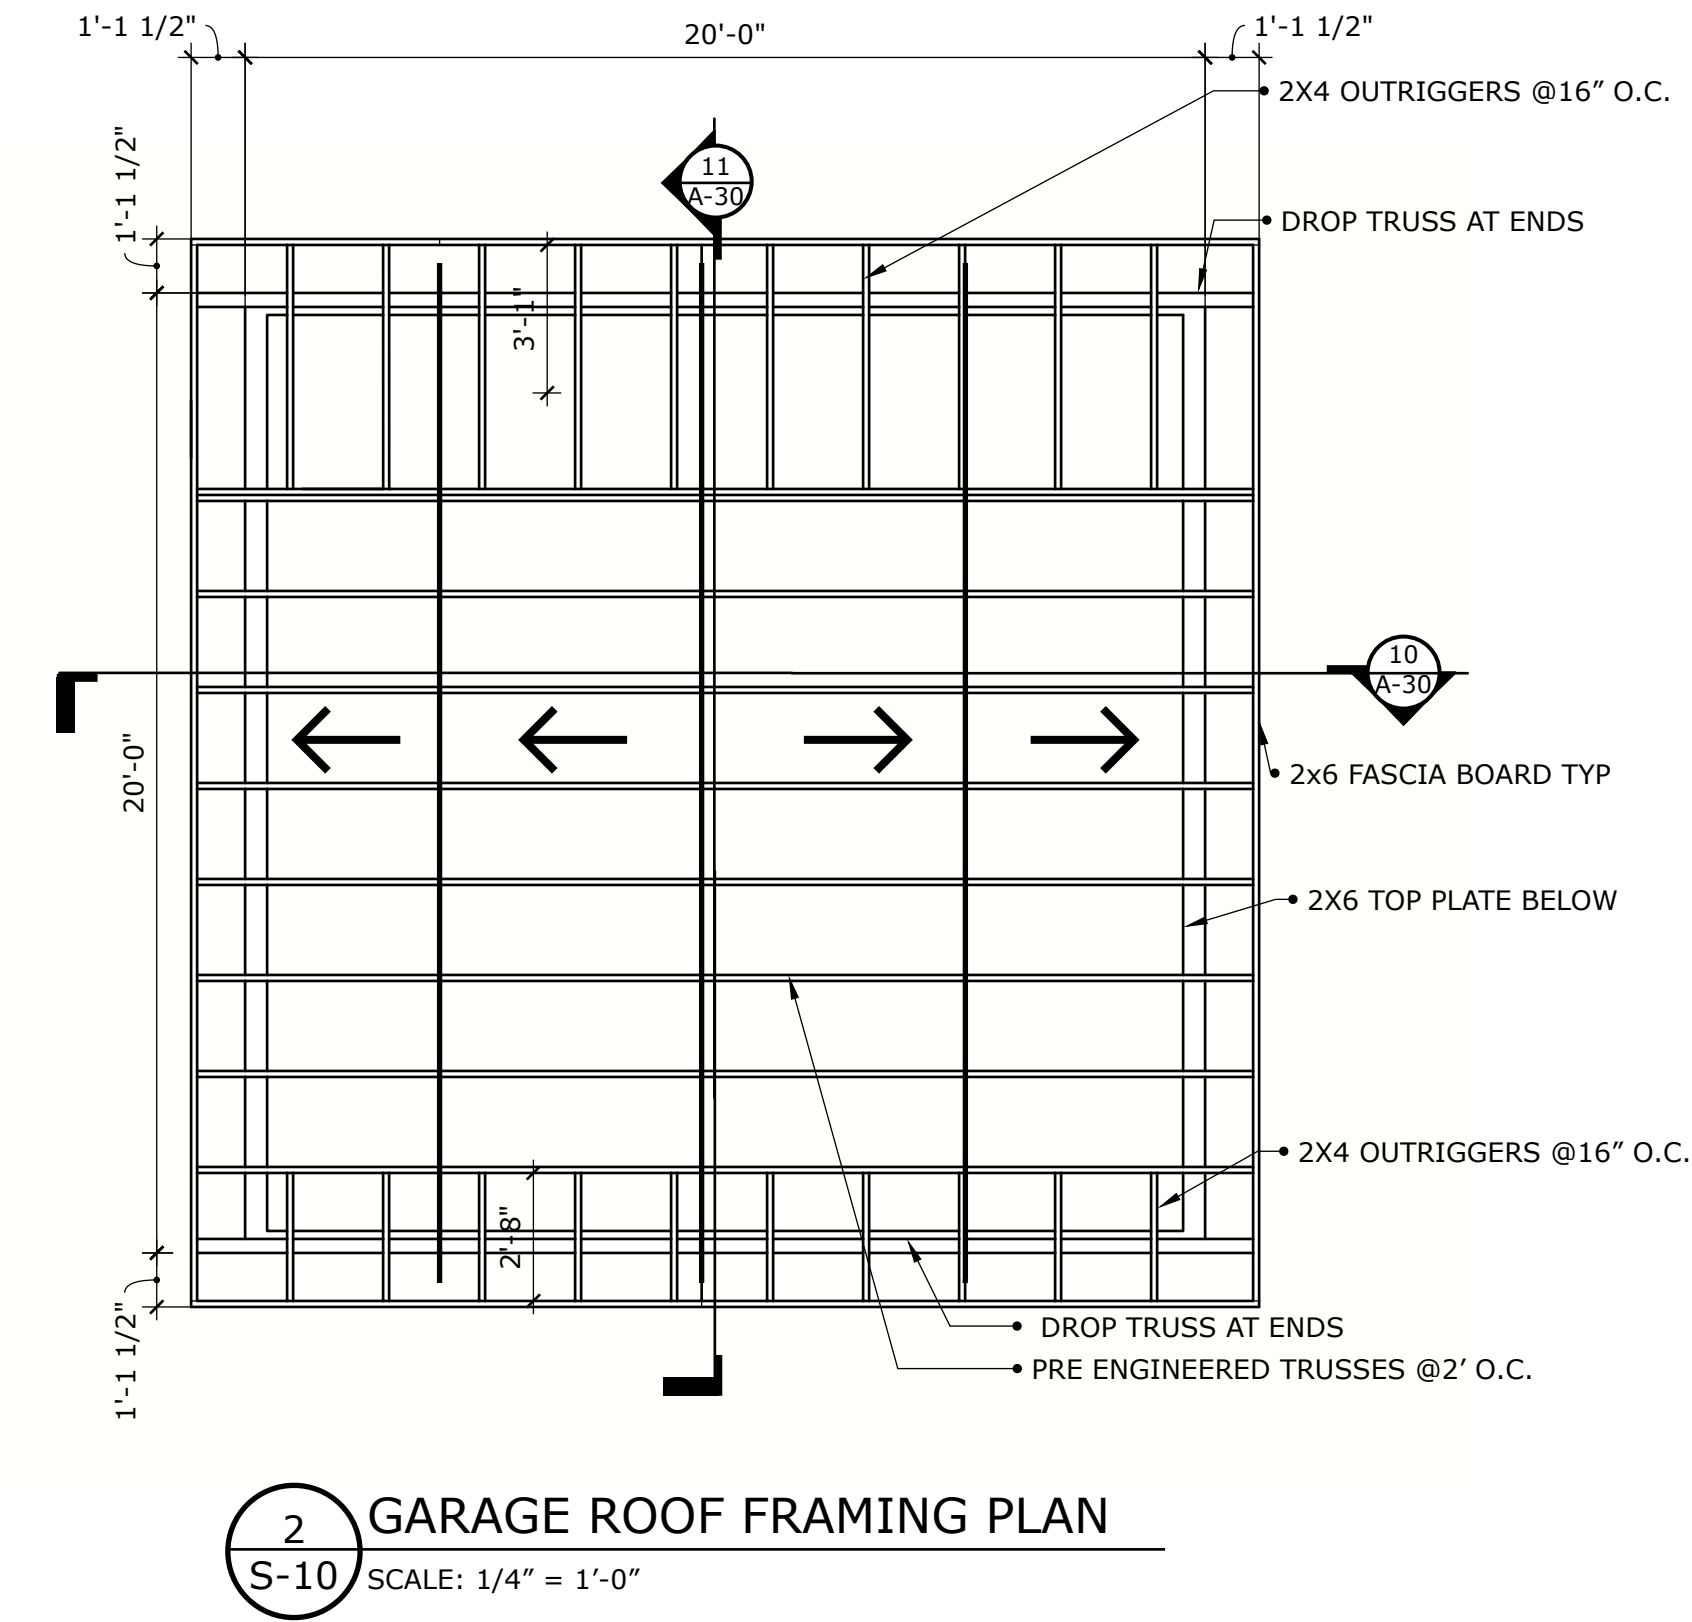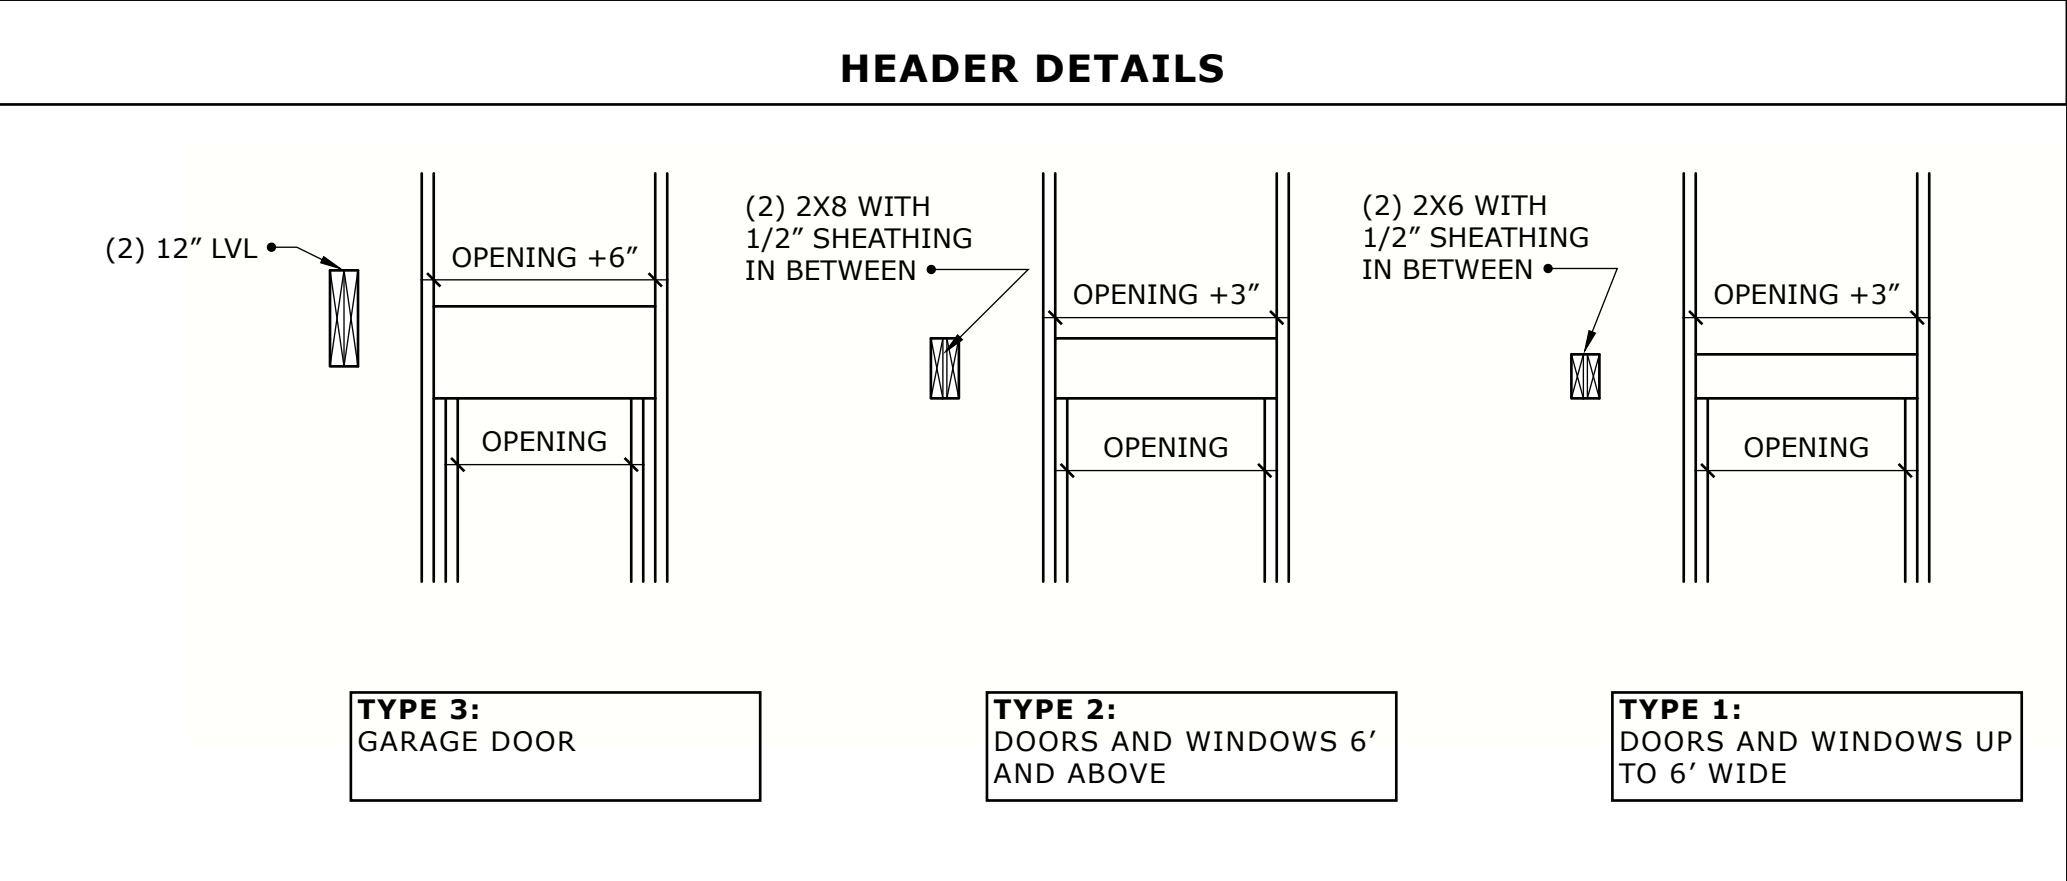


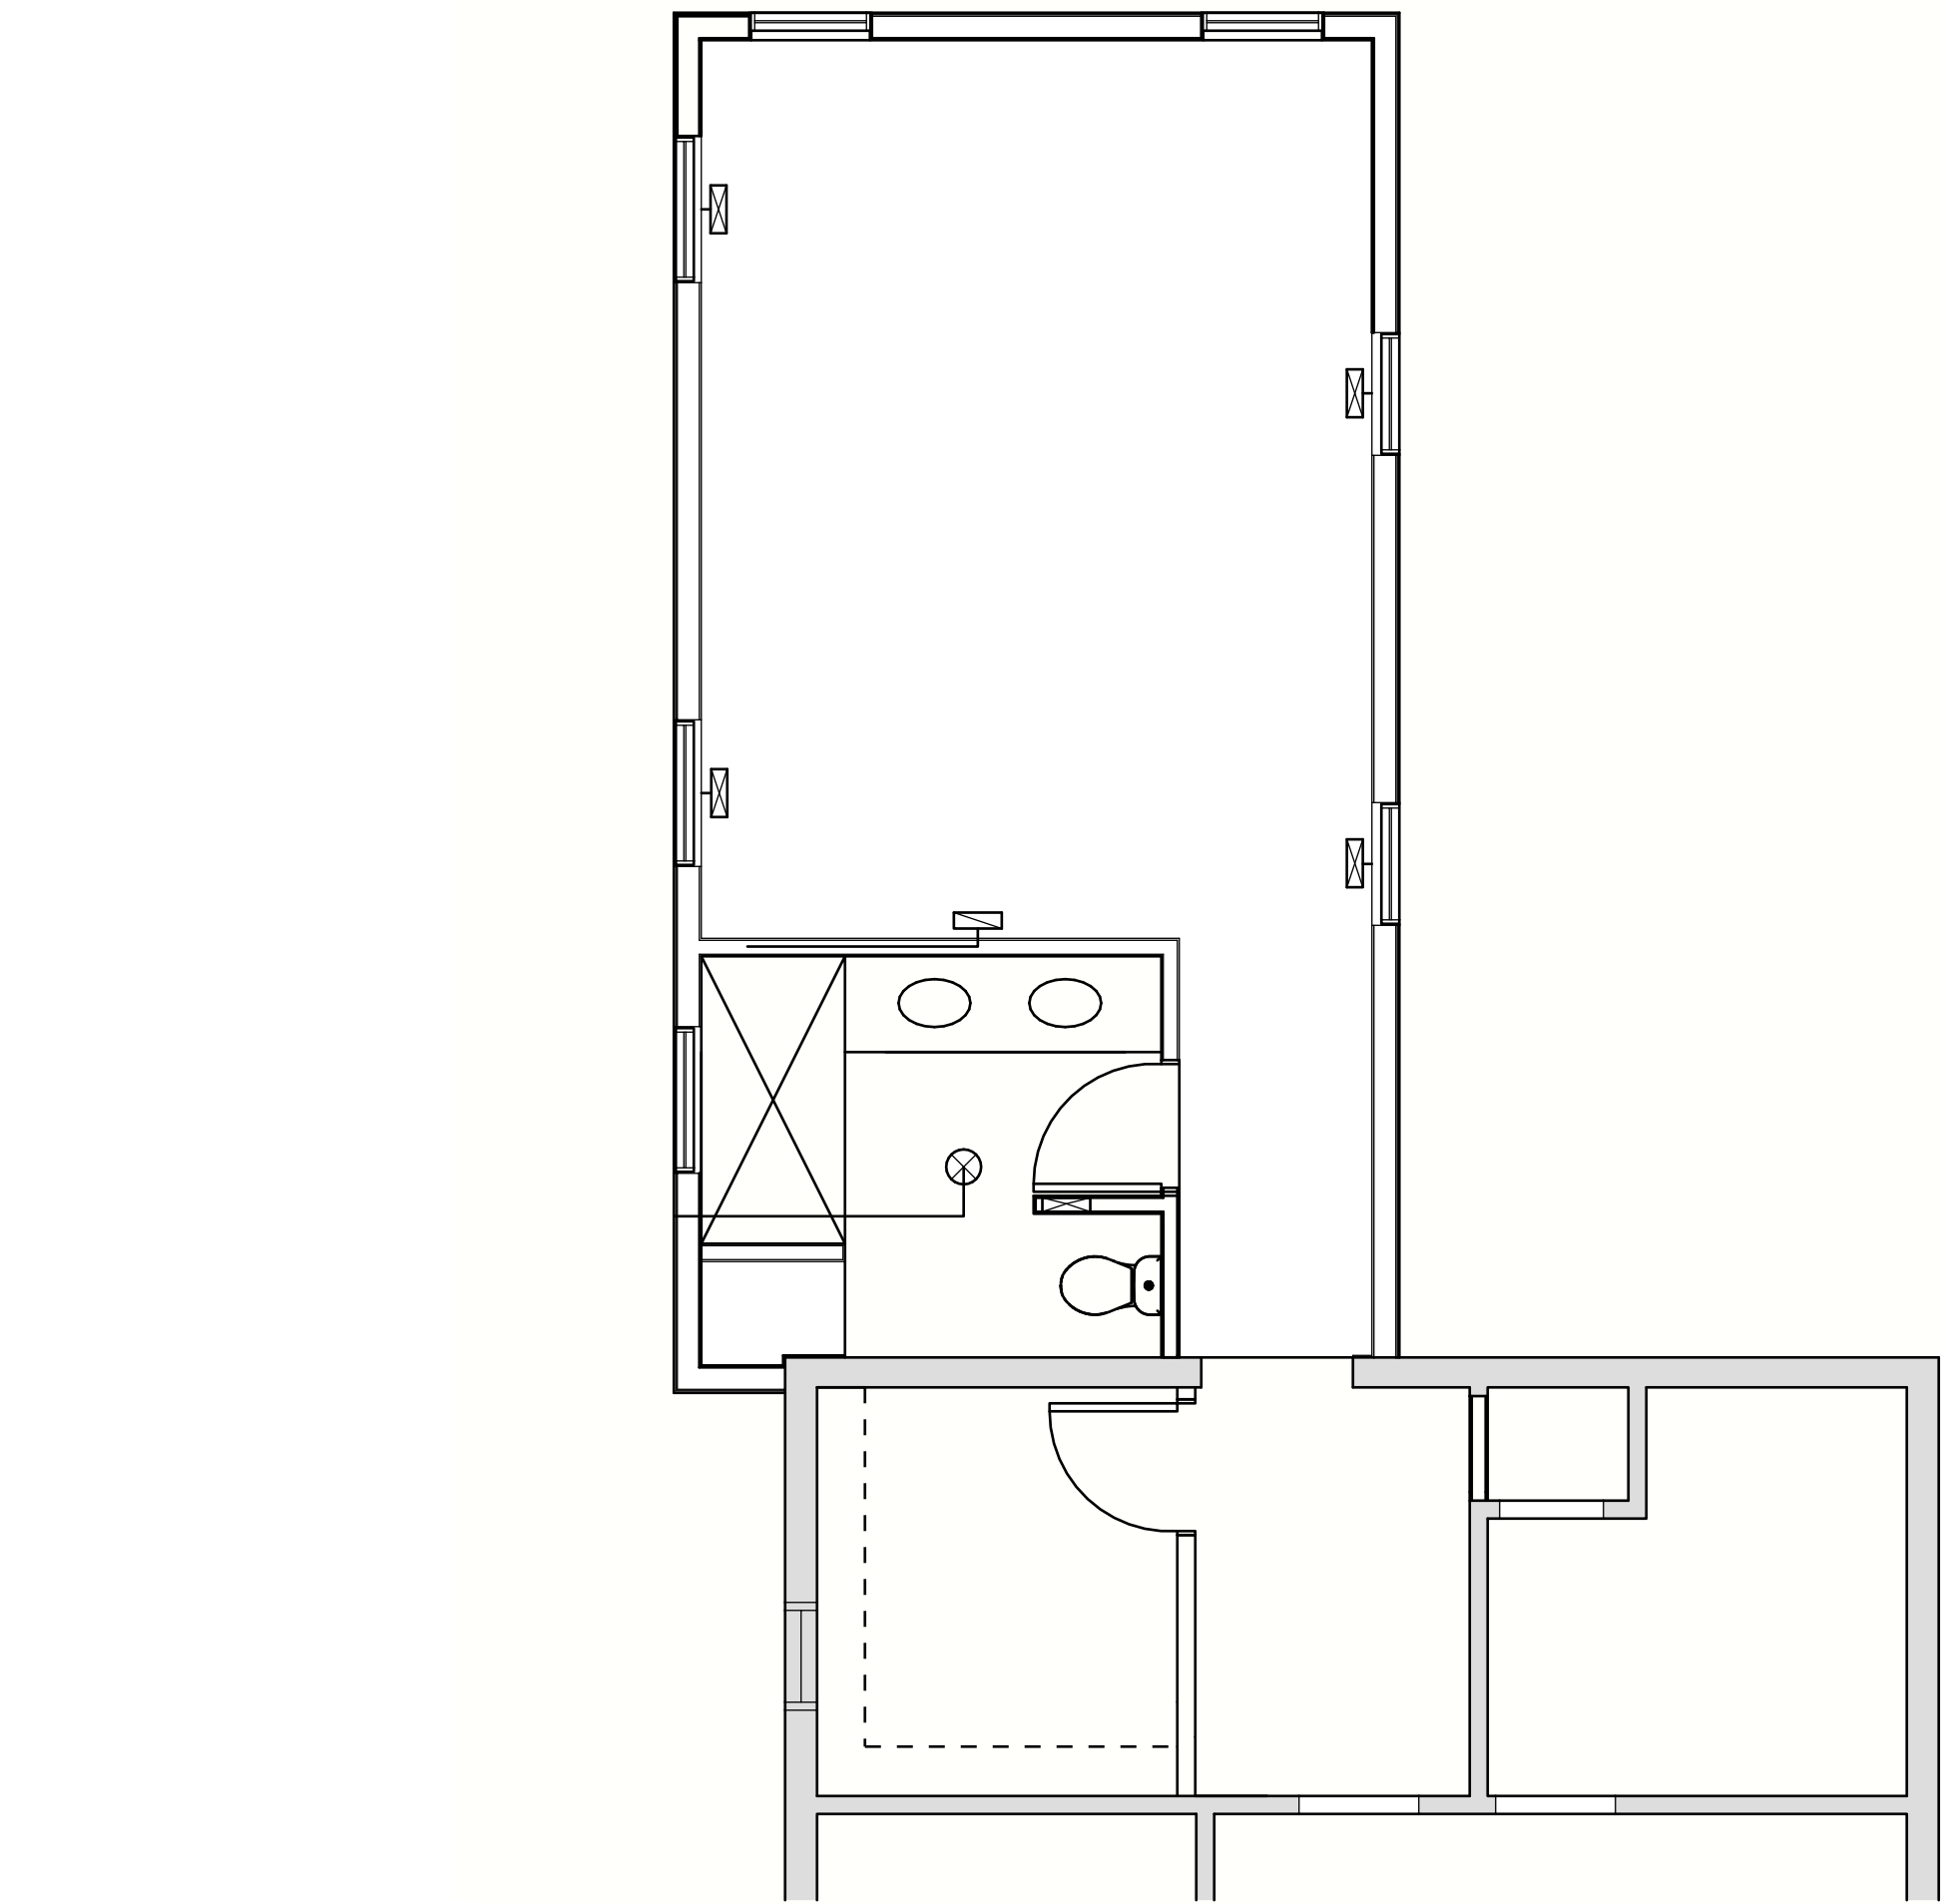


4 SECOND FLOOR MECHANICAL PLAN
EM-10 SCALE: 1/4" = 1'-0"

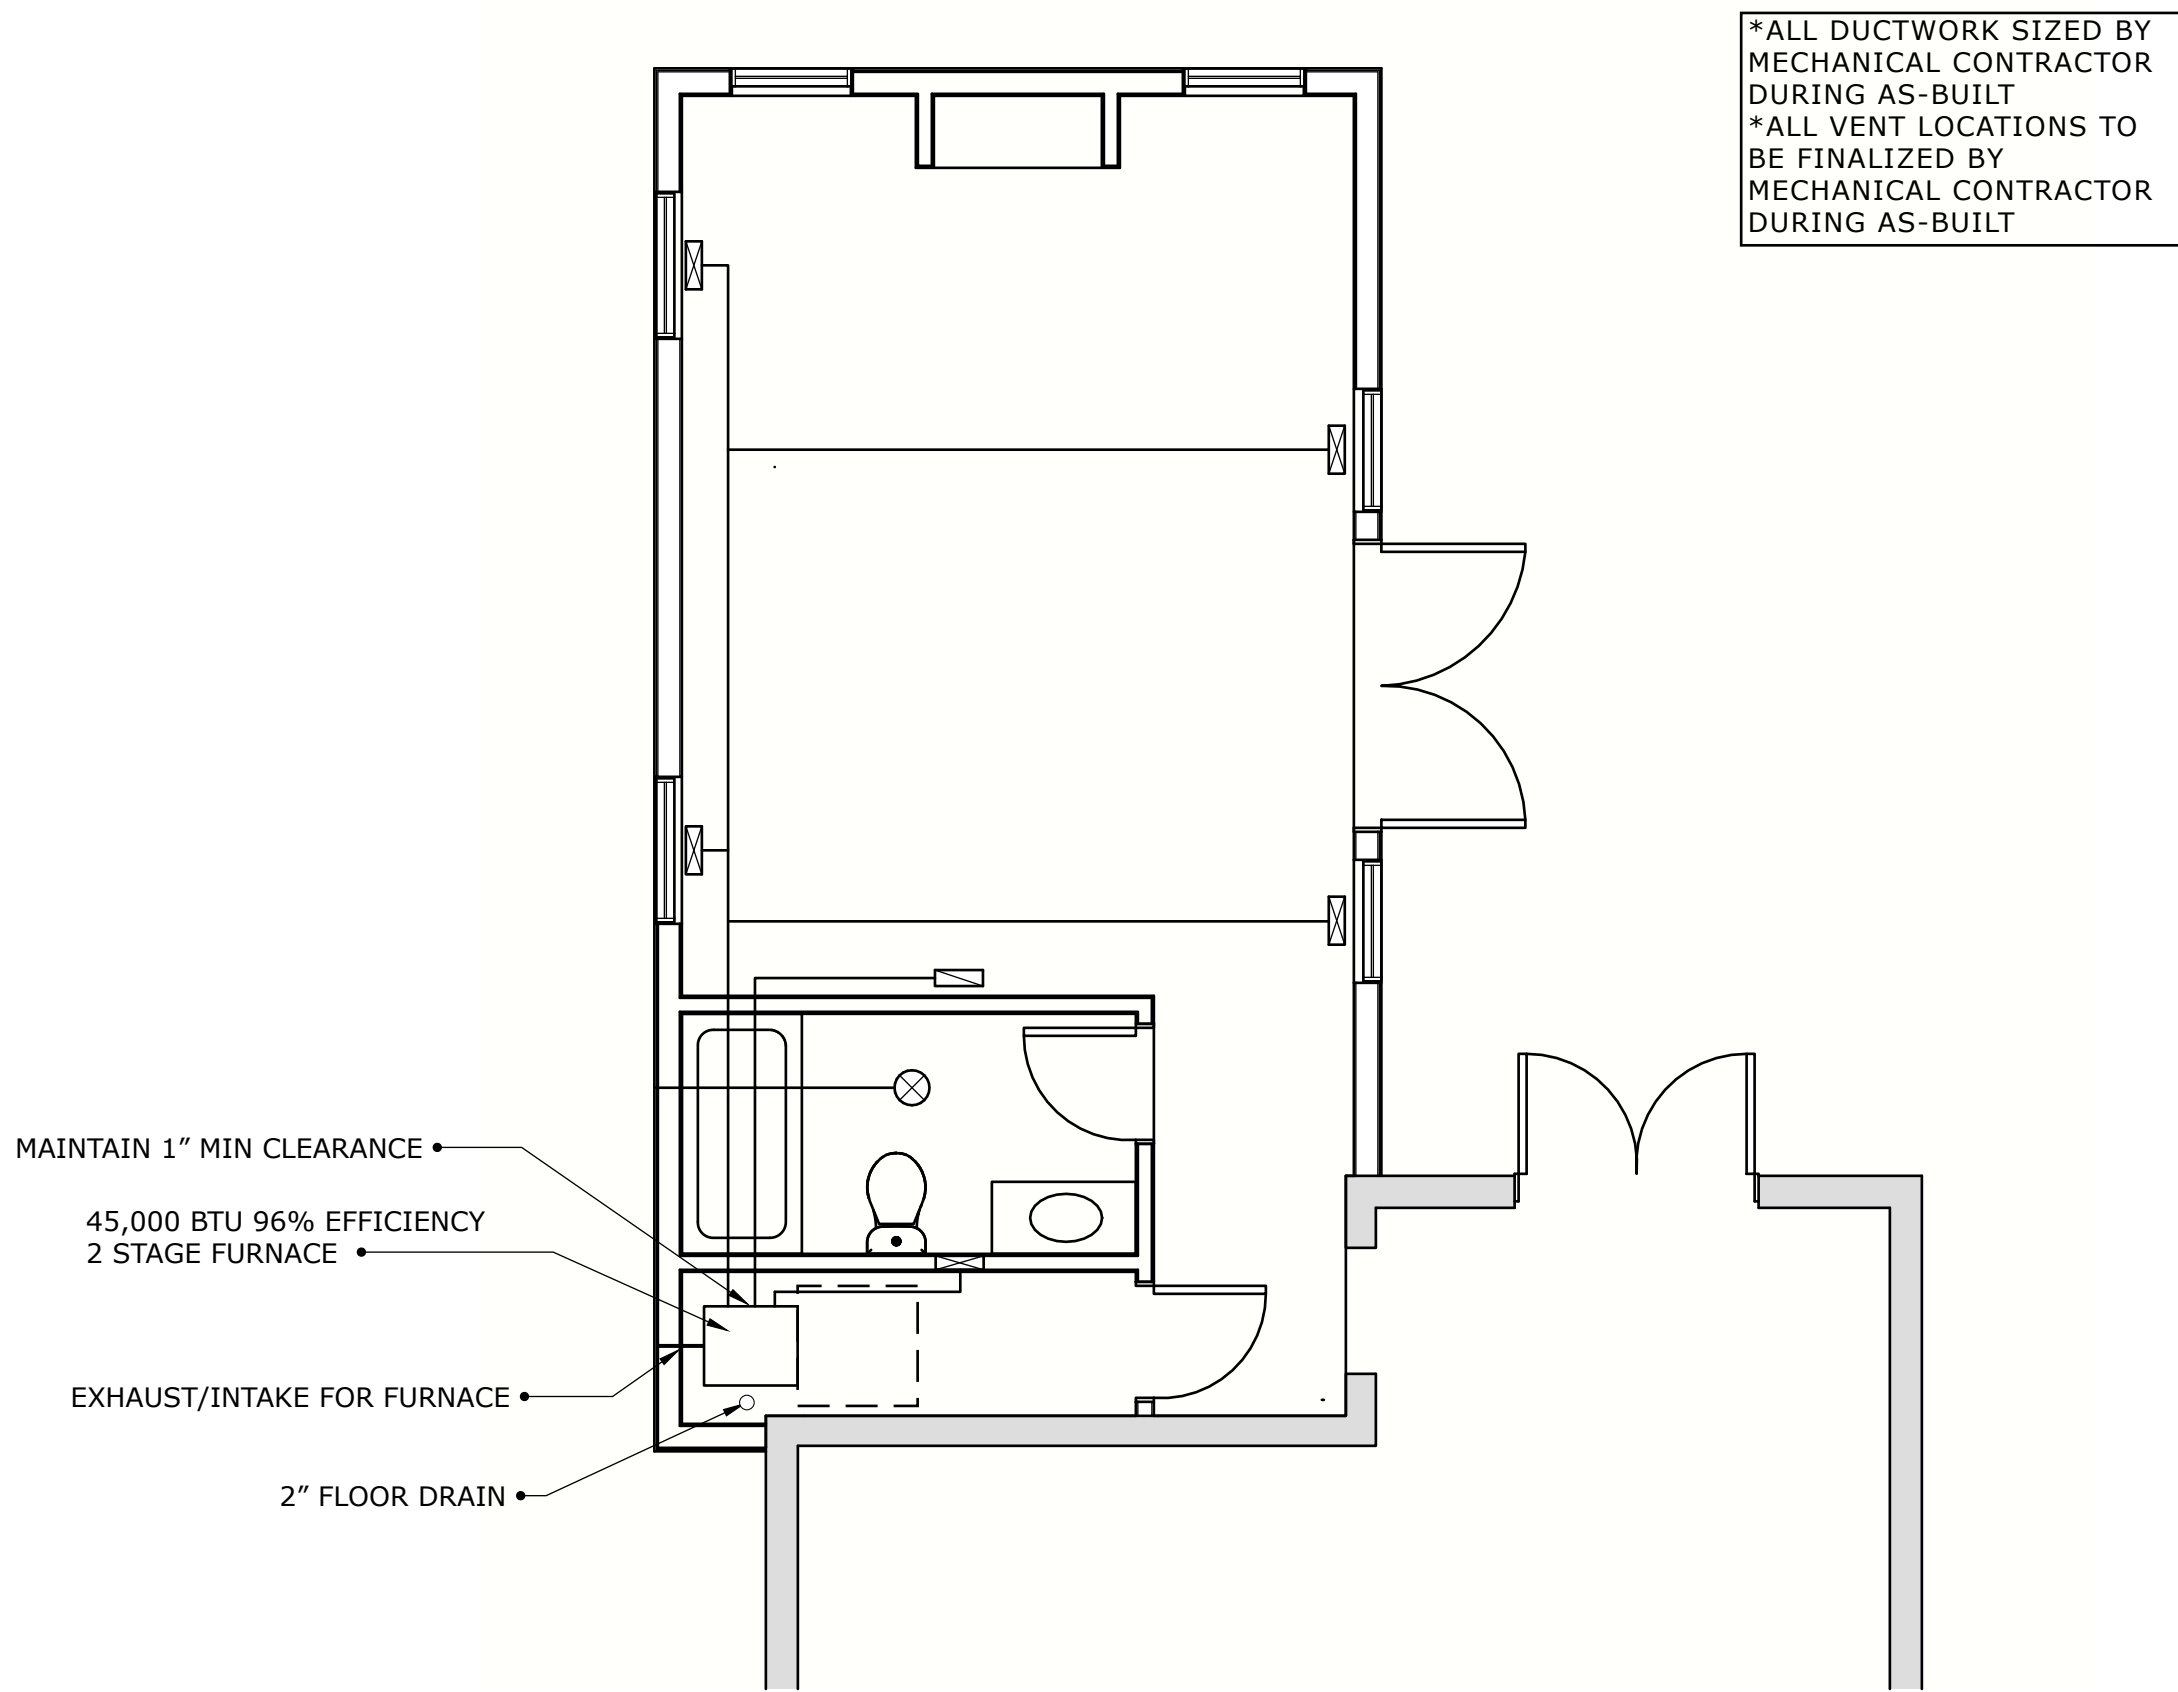

3 FIRST FLOOR MECHANICAL PLAN
EM-10 SCALE: 1/4" = 1'-0"

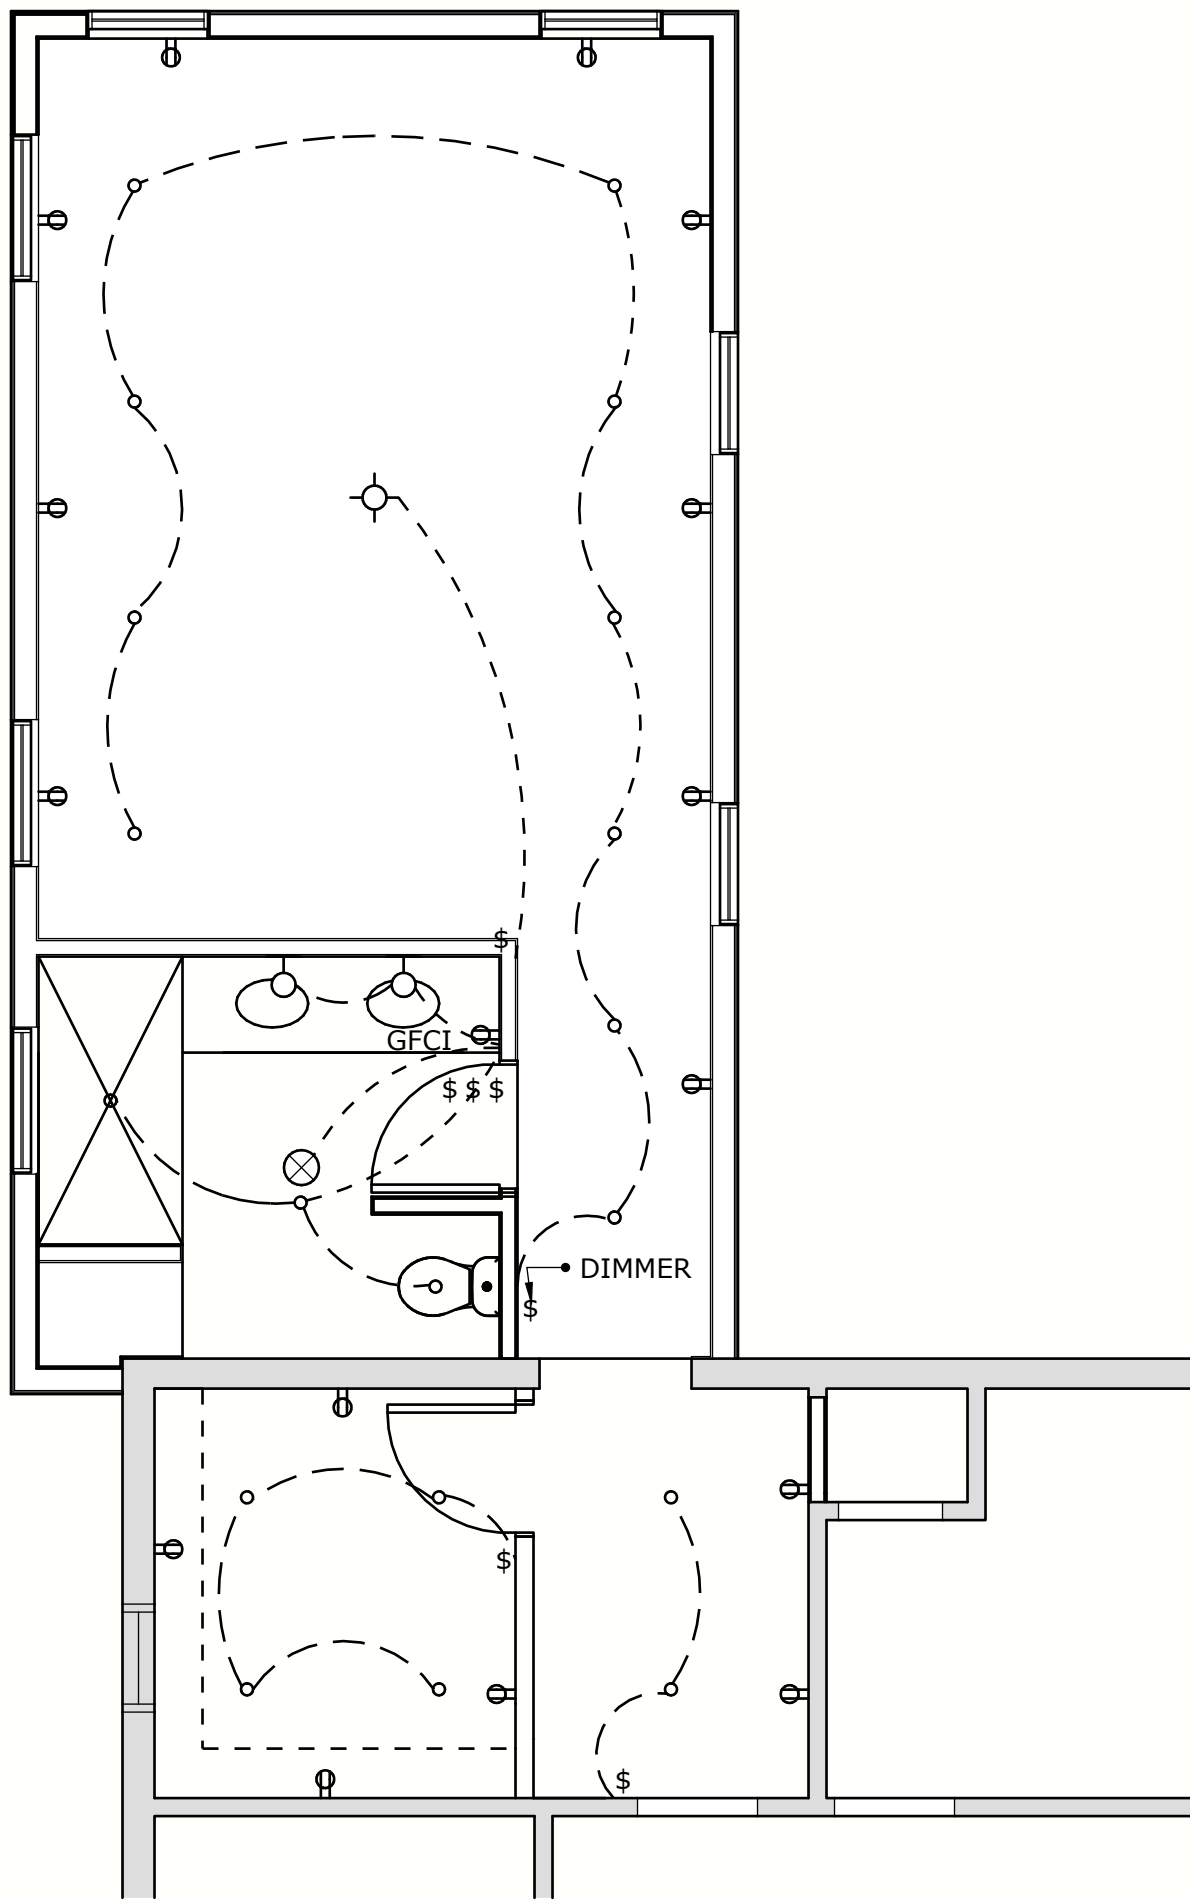

2 SECOND FLOOR ELECTRICAL PLAN
EM-10 SCALE: 1/4" = 1'-0"

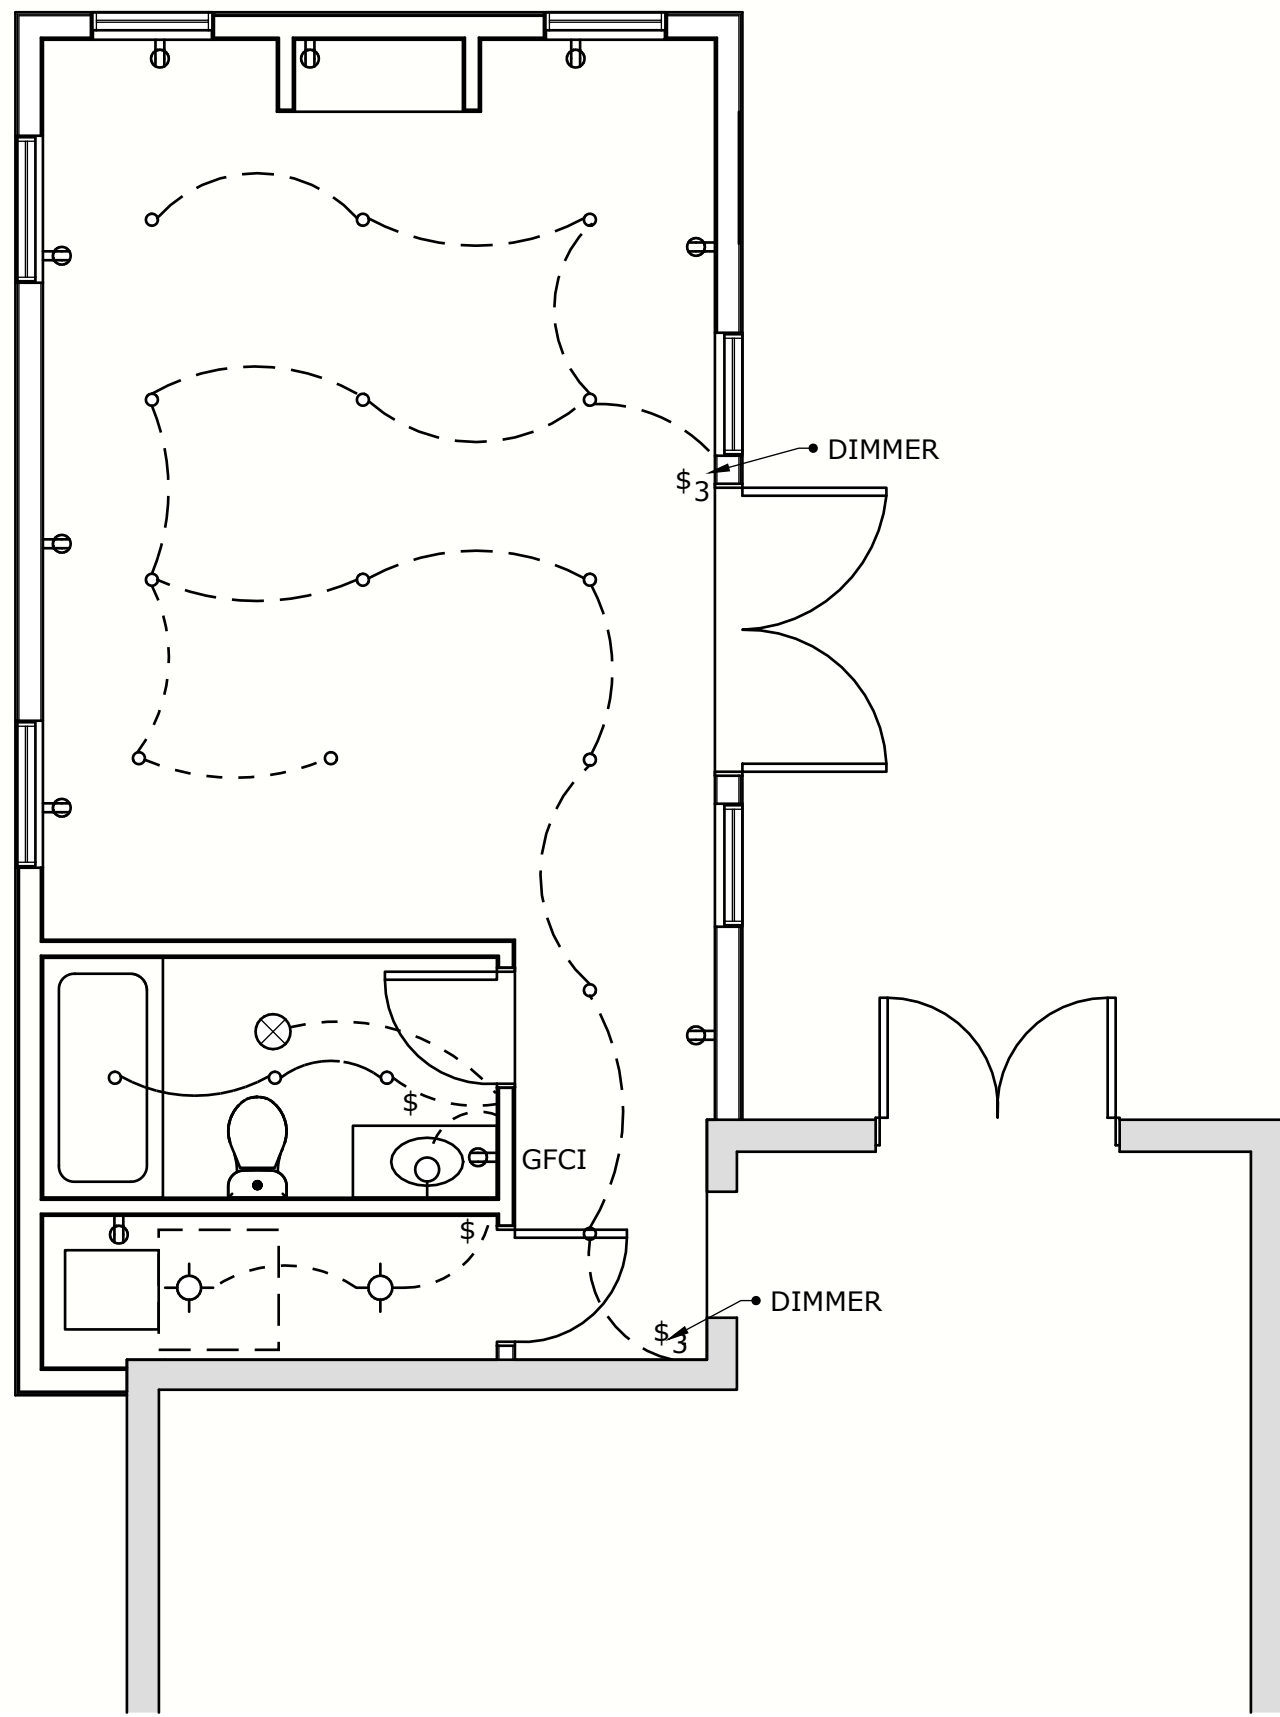

1 FIRST FLOOR ELECTRICAL PLAN
EM-10 SCALE: 1/4" = 1'-0"

MECHANICAL LEGEND		ELECTRICAL LEGEND	
	SUPPLY DIFFUSER		3" RECESSED DOWNLIGHT
	RETURN DIFFUSER		CEILING LIGHT
	EXHAUST FAN		WALL SCONCE
			SWITCH
			3-WAY SWITCH
			OULET
			EXHAUST FAN

ISSUE

ELECTRICAL AND
MECHANICAL
PLANS

EM-10