



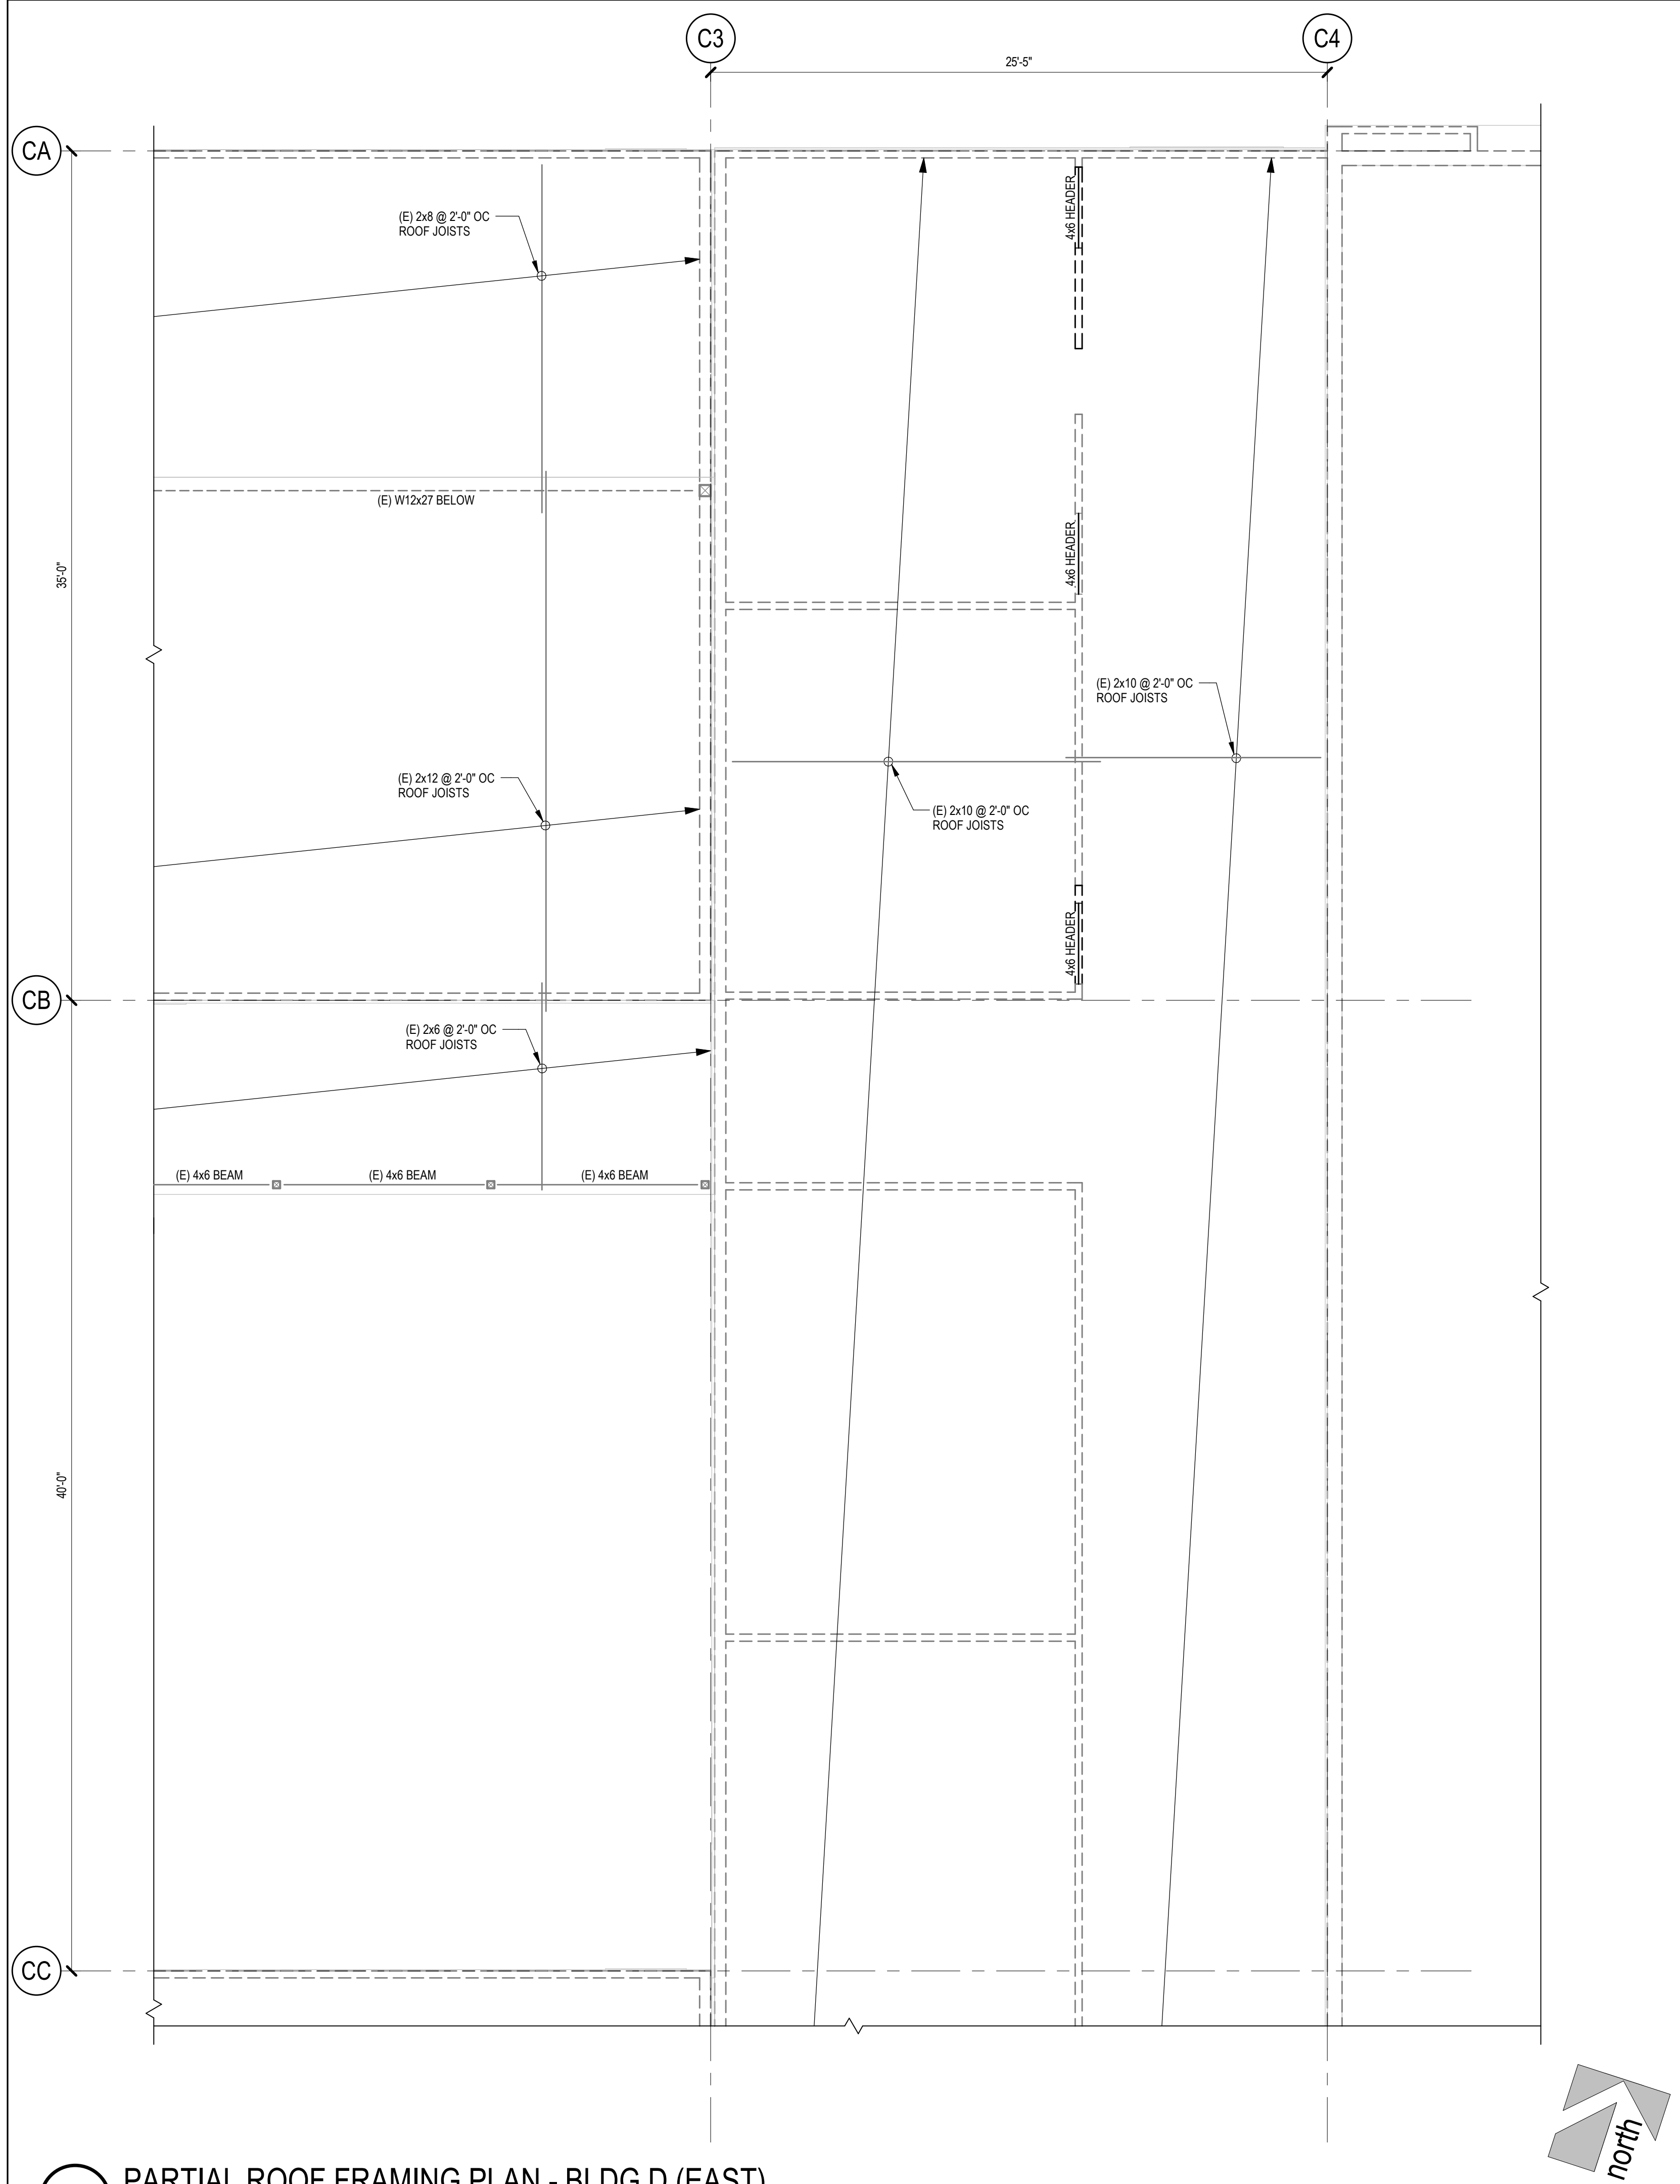

1 PARTIAL ROOF FRAMING PLAN - BLDG D (EAST)

1/4" = 1'-0"

- NOTES:
- SEE 'E' BUILDING DRAWINGS FOR TOP OF ROOF ELEVATIONS.
 - SEE ARCHITECTURAL, PLUMBING, MECHANICAL AND ELECTRICAL FOR LOCATION OF EQUIPMENT. CONTRACTOR TO VERIFY ALL UNIT LOCATIONS, SIZES AND OPENINGS.

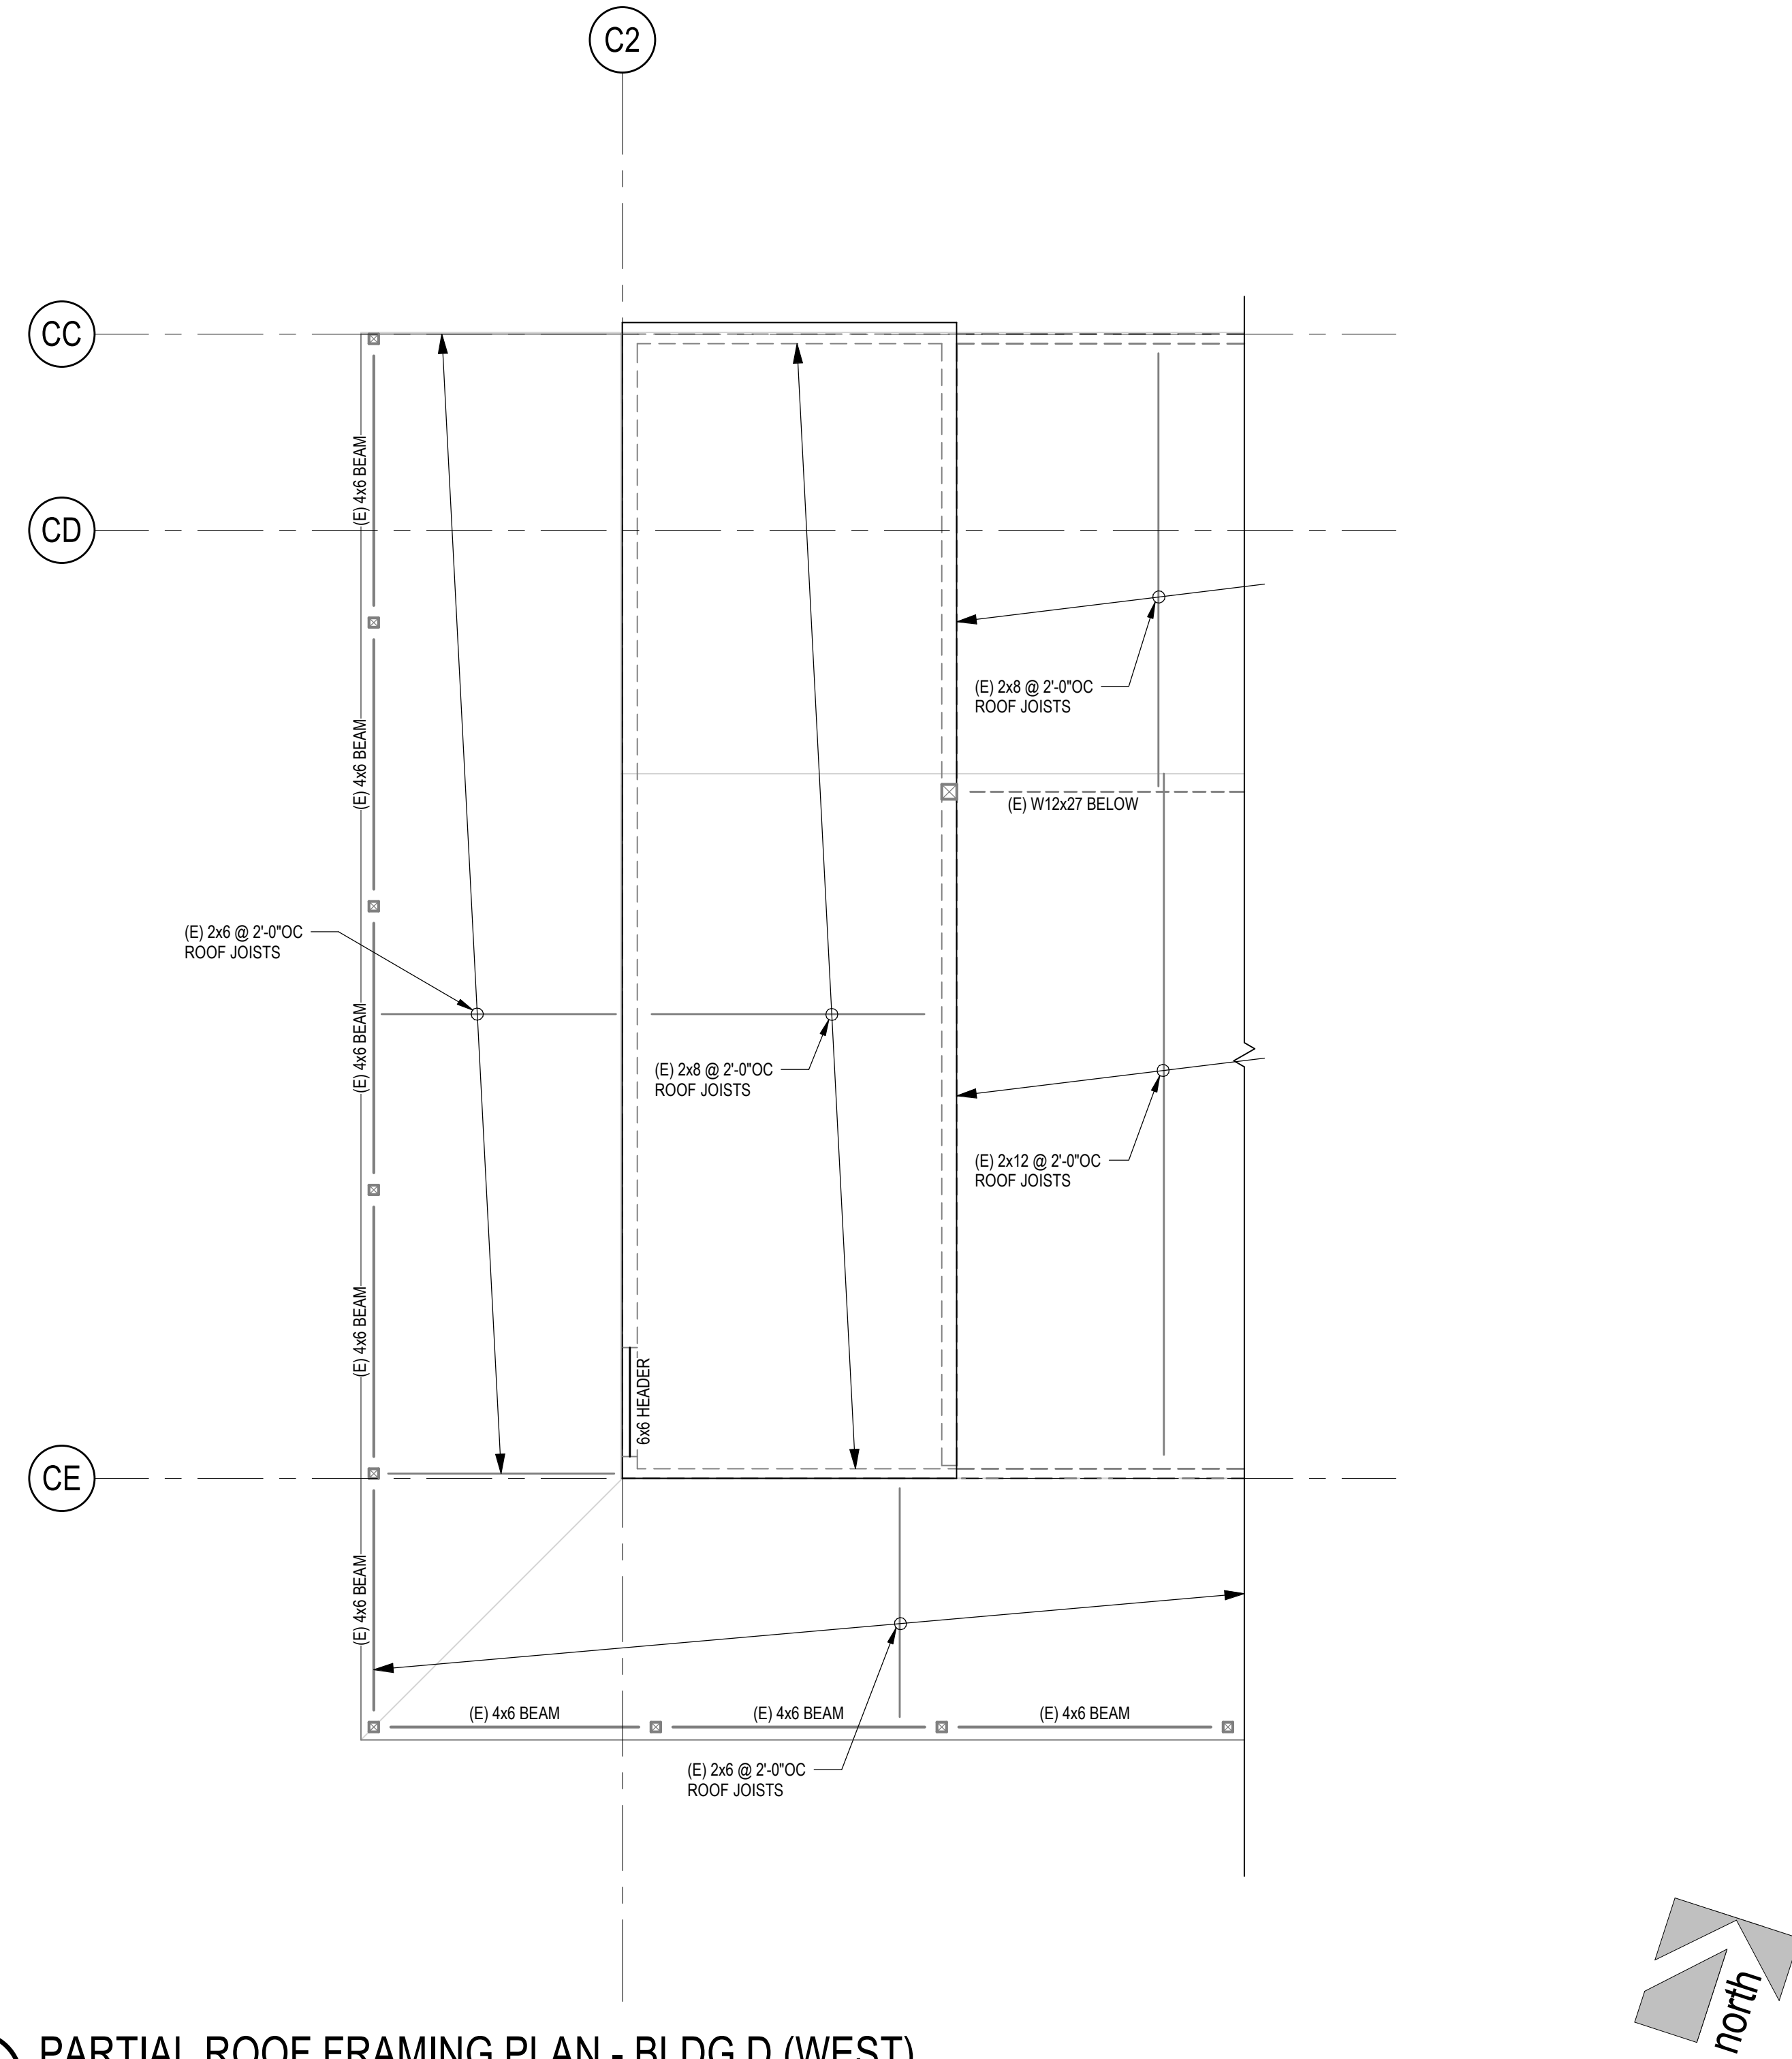

2 PARTIAL ROOF FRAMING PLAN - BLDG D (WEST)

1/4" = 1'-0"

Not for permitting or construction

IDENTIFICATION STAMP
DIV. OF THE STATE ARCHITECT
APP. 02-121896 INC.
REVIEWED FOR
SS ☐ FLS ☐ ACS ☐
DATE: 09/05/2024

PBK

ARCHITECT PBK Architects, Inc.
FOLSOM
1110 Iron Point Road, Suite 200
Folsom, CA 95630-8315
916-355-9922
PBK.com


STRUCTURAL ENGINEER
miyamoto.
1450 Harvard Drive, Suite One
West Sacramento, CA 95691
M2301016_R01
T: (916) 373-1969
miyamotointernational.com

NICHOLS ES MODERNIZATION
LODI UNIFIED SCHOOL DISTRICT
LEROY NICHOLS ELEMENTARY SCHOOL
1301 CRESCENT AVENUE
LODI, CA 95240
CONSTRUCTION DRAWINGS

LODI
UNIFIED SCHOOL DISTRICT

G	H	J
D	E	F
A	B	C

KEY PLAN

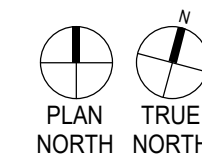

CLIENT		
LODI UNIFIED SCHOOL DISTRICT		
PROJECT NUMBER		
230170		
DATE	08/29/2024	
DRAWN BY: AJR	CHKD BY: RM	
REVISIONS		
#	DESCRIPTION	DATE

CONSTRUCTION DRAWINGS

PARTIAL ROOF
FRAMING PLANS

S1.02