



MYLES
NELSON
McKENZIE
DESIGN

Telephone: 949-683-6895
843-505-1031
Email: info@mylesmckenzie.com
Web: www.mylesmckenzie.com

These drawings documents and specifications are an instrument of service, copyright and the property of MYLES NELSON MCKENZIE DESIGN and shall not be used or reproduced in any part or whole, except by written agreement with the Architect or Designer of MYLES NELSON MCKENZIE DESIGN. Their use for publication shall be restricted to the original project in which they are designed for.

Written dimensions shall be verified on the job site. Any discrepancy shall be brought to notice of the Architect or Designer of MYLES NELSON MCKENZIE DESIGN prior to the commencement of any construction.

These plans have been reviewed and approved by:

GENERAL NOTES:


- A. THERMAL INSULATION:
- WALLS: R-13 MINIMUM
 - FLOORS: R-19 MINIMUM
 - ROOF: R-30 MINIMUM

KEYNOTES:


1. FINISHED GRADE.
2. CONCRETE FOOTING AND SLAB. REFER TO STRUCTURAL.
3. REFER TO GENERAL NOTES FOR THERMAL INSULATION MINIMUMS.
4. REFER TO STRUCTURAL FOR TYPICAL WALL CONSTRUCTION.
5. INSULATED WINDOW.
6. OVERHEAD GARAGE DOOR.
7. WOOD BEAM. REFER TO STRUCTURAL.
8. REFER TO STRUCTURAL FOR FLOOR AND ROOF FRAMING.
9. CAST-IN-PLACE CONCRETE STAIRS. REFER TO STRUCTURAL.
10. CONCRETE PATIO.
11. GAF TIMBERLINE HDZ SHINGLE ROOFING SYSTEM OVER ONE LAYER OF GAF TIGER PAW PREMIUM SYNTHETIC ROOFING UNDERLAYMENT OR EQUAL.
12. REFER TO MANUFACTURERS FLOOR TRUSSES FOR SPECIFICATIONS AND DETAILS.
13. REFER TO CABINET PLANS.




C BUILDING SECTION
SCALE : 1/4" = 1'-0"

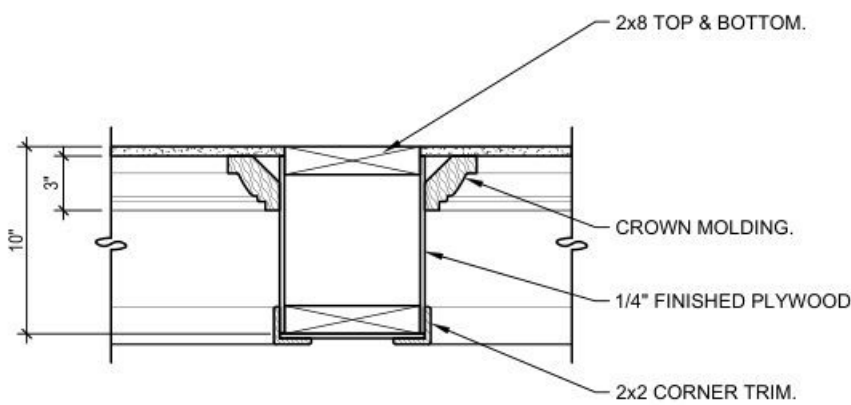

1 LIVING ROOM RECESSED TRIM
SCALE : 1 1/2" = 1'-0"

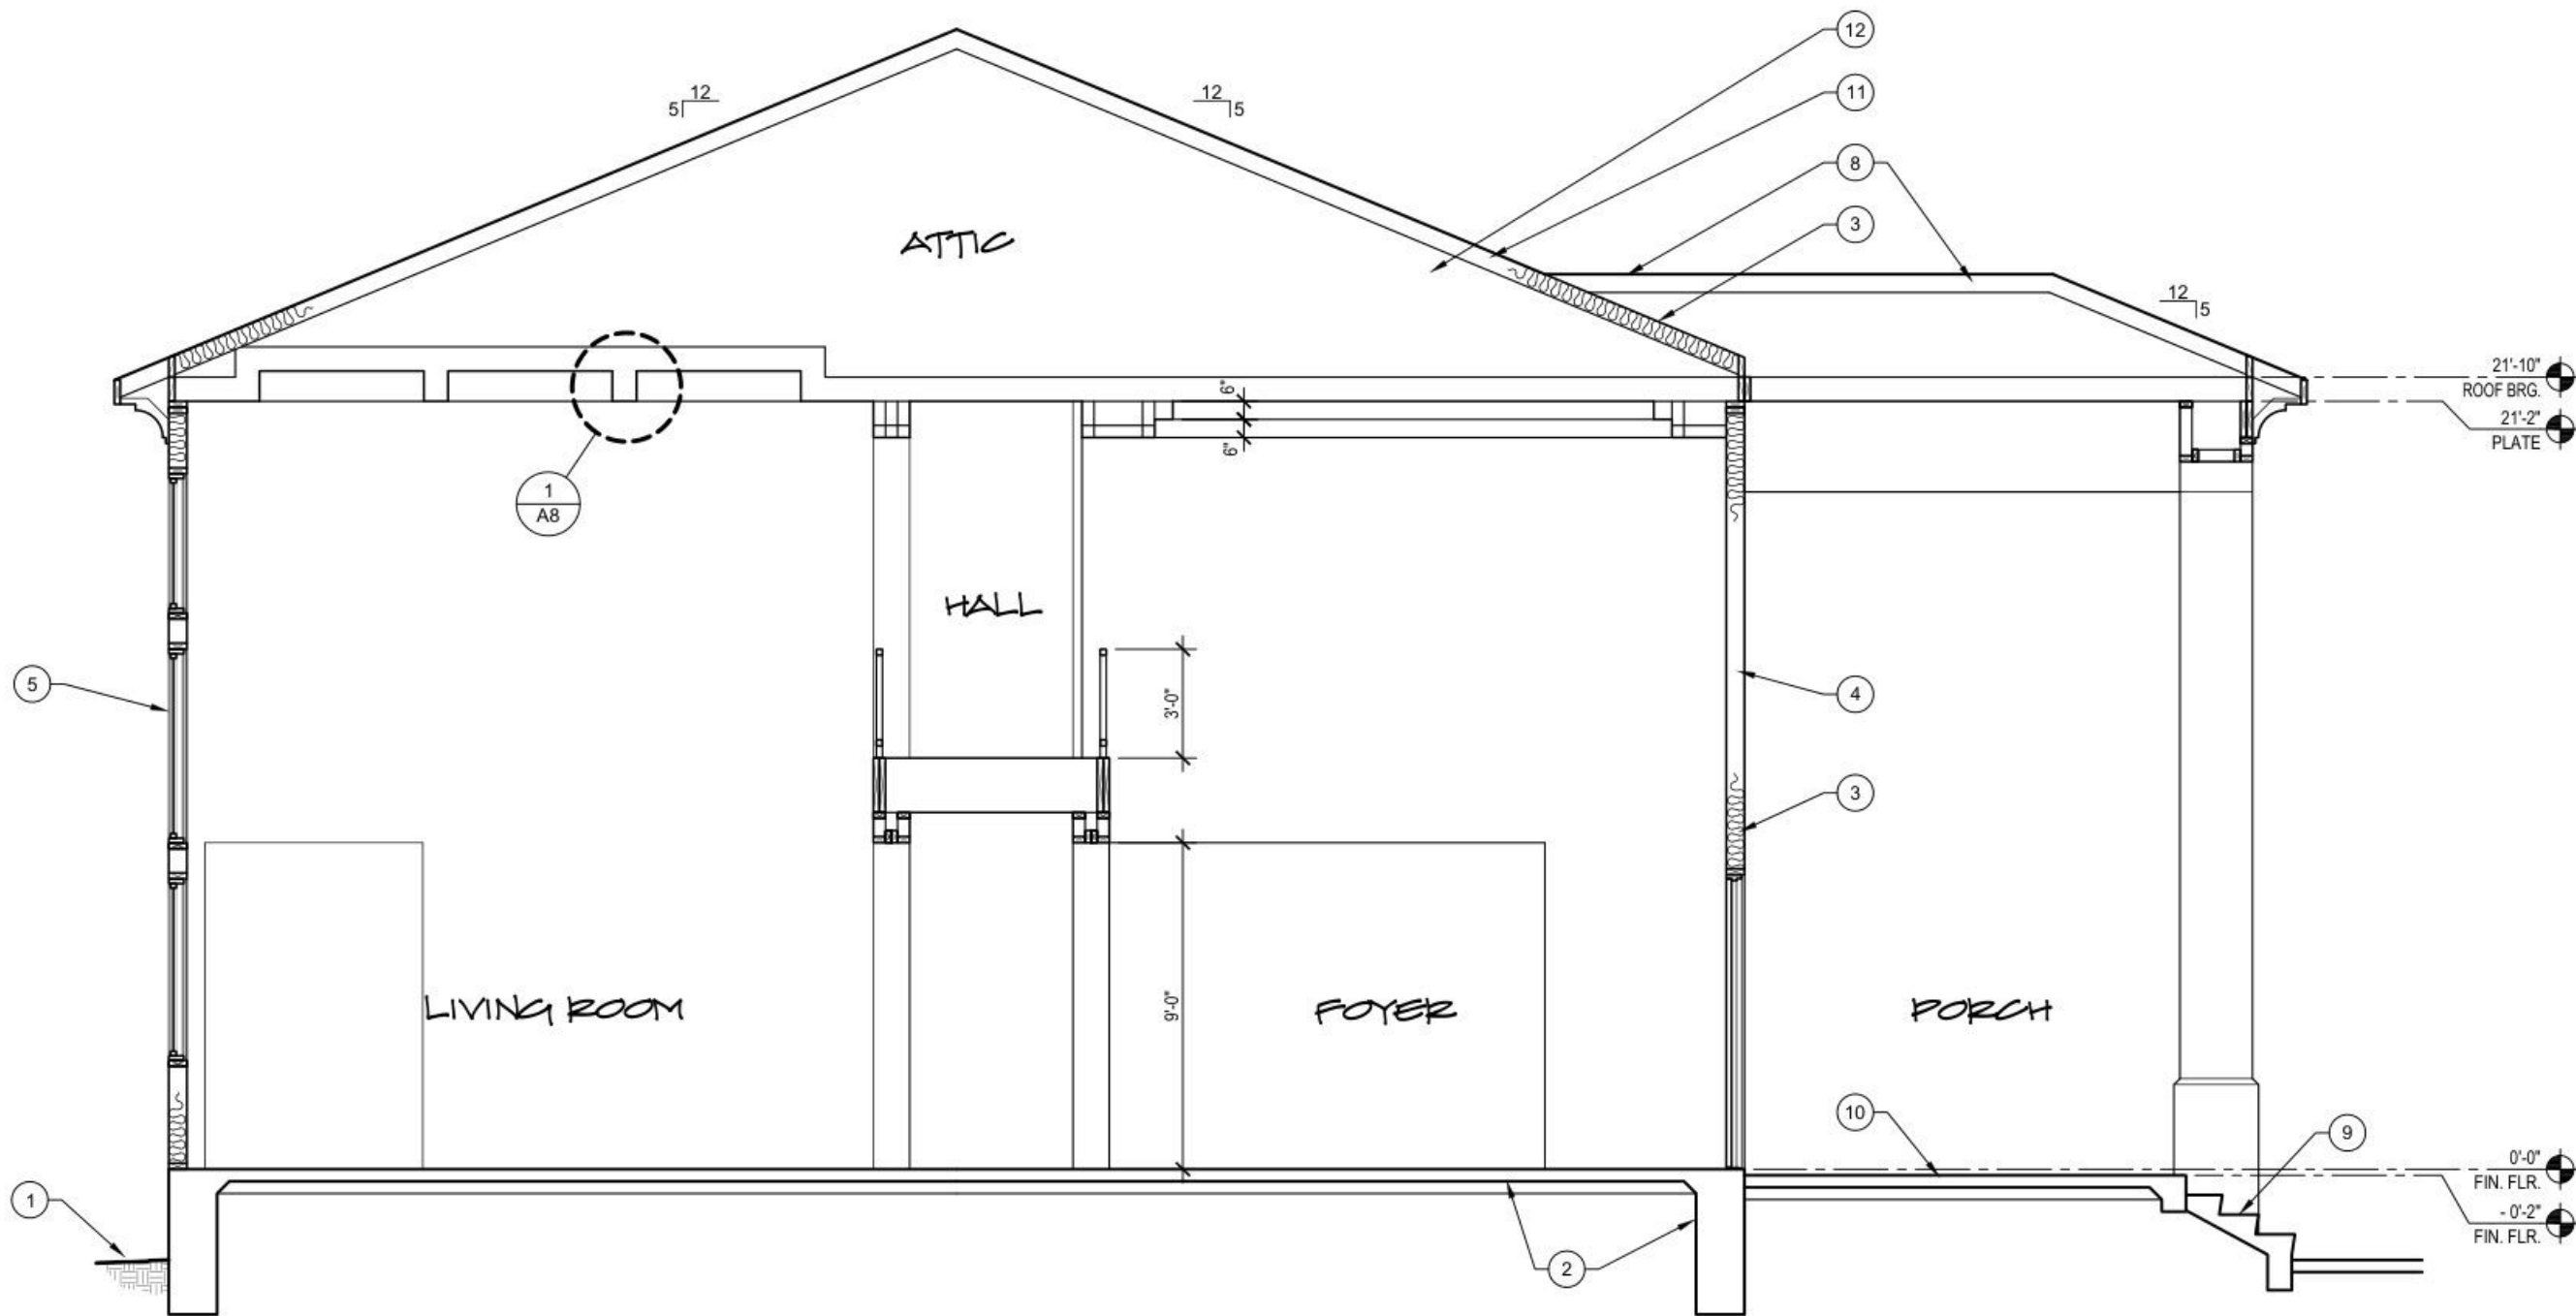

A BUILDING SECTION
SCALE : 1/4" = 1'-0"

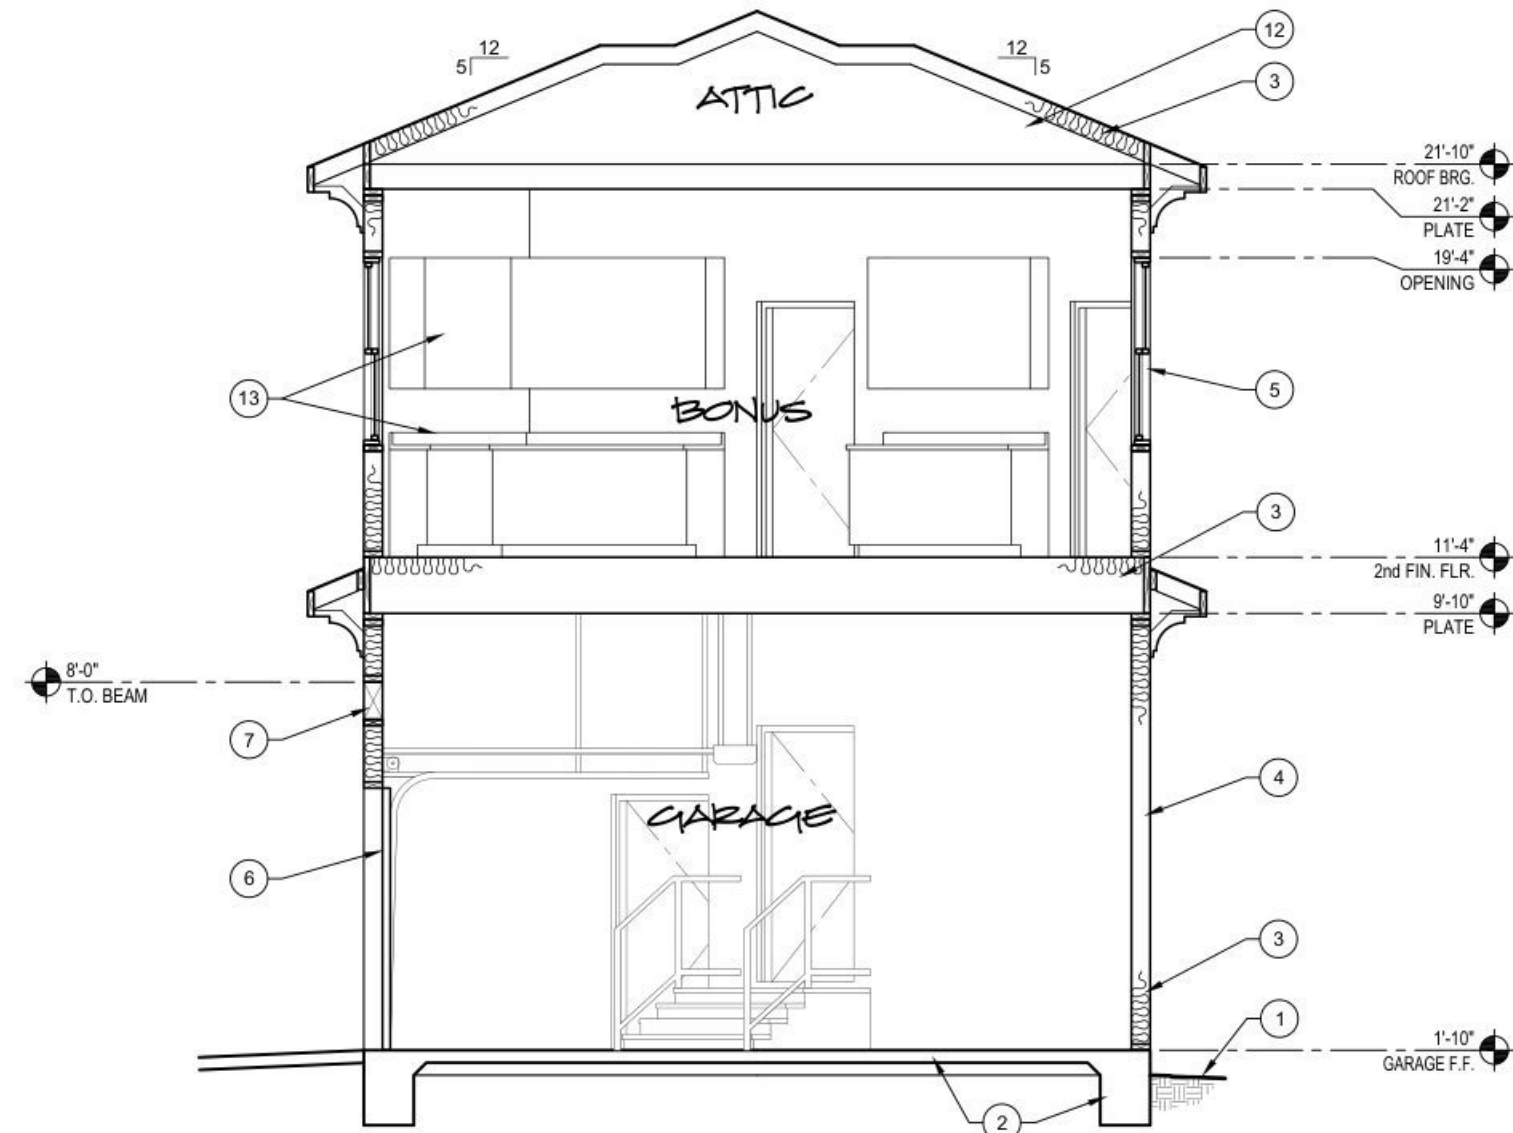

B BUILDING SECTION
SCALE : 1/4" = 1'-0"

A NEW CUSTOM HOME DESIGN FOR:
MESECHER - CLOUTREAU
RESIDENCE
LOT 2221, BLOCK 104, RIVERBEND
BLUFFTON TOWNSHIP, SC

Project

Number Date Description

Revisions

Issue Date 5/17/20

Plot Date 8/9/22

BUILDING SECTIONS

Sheet

AB