


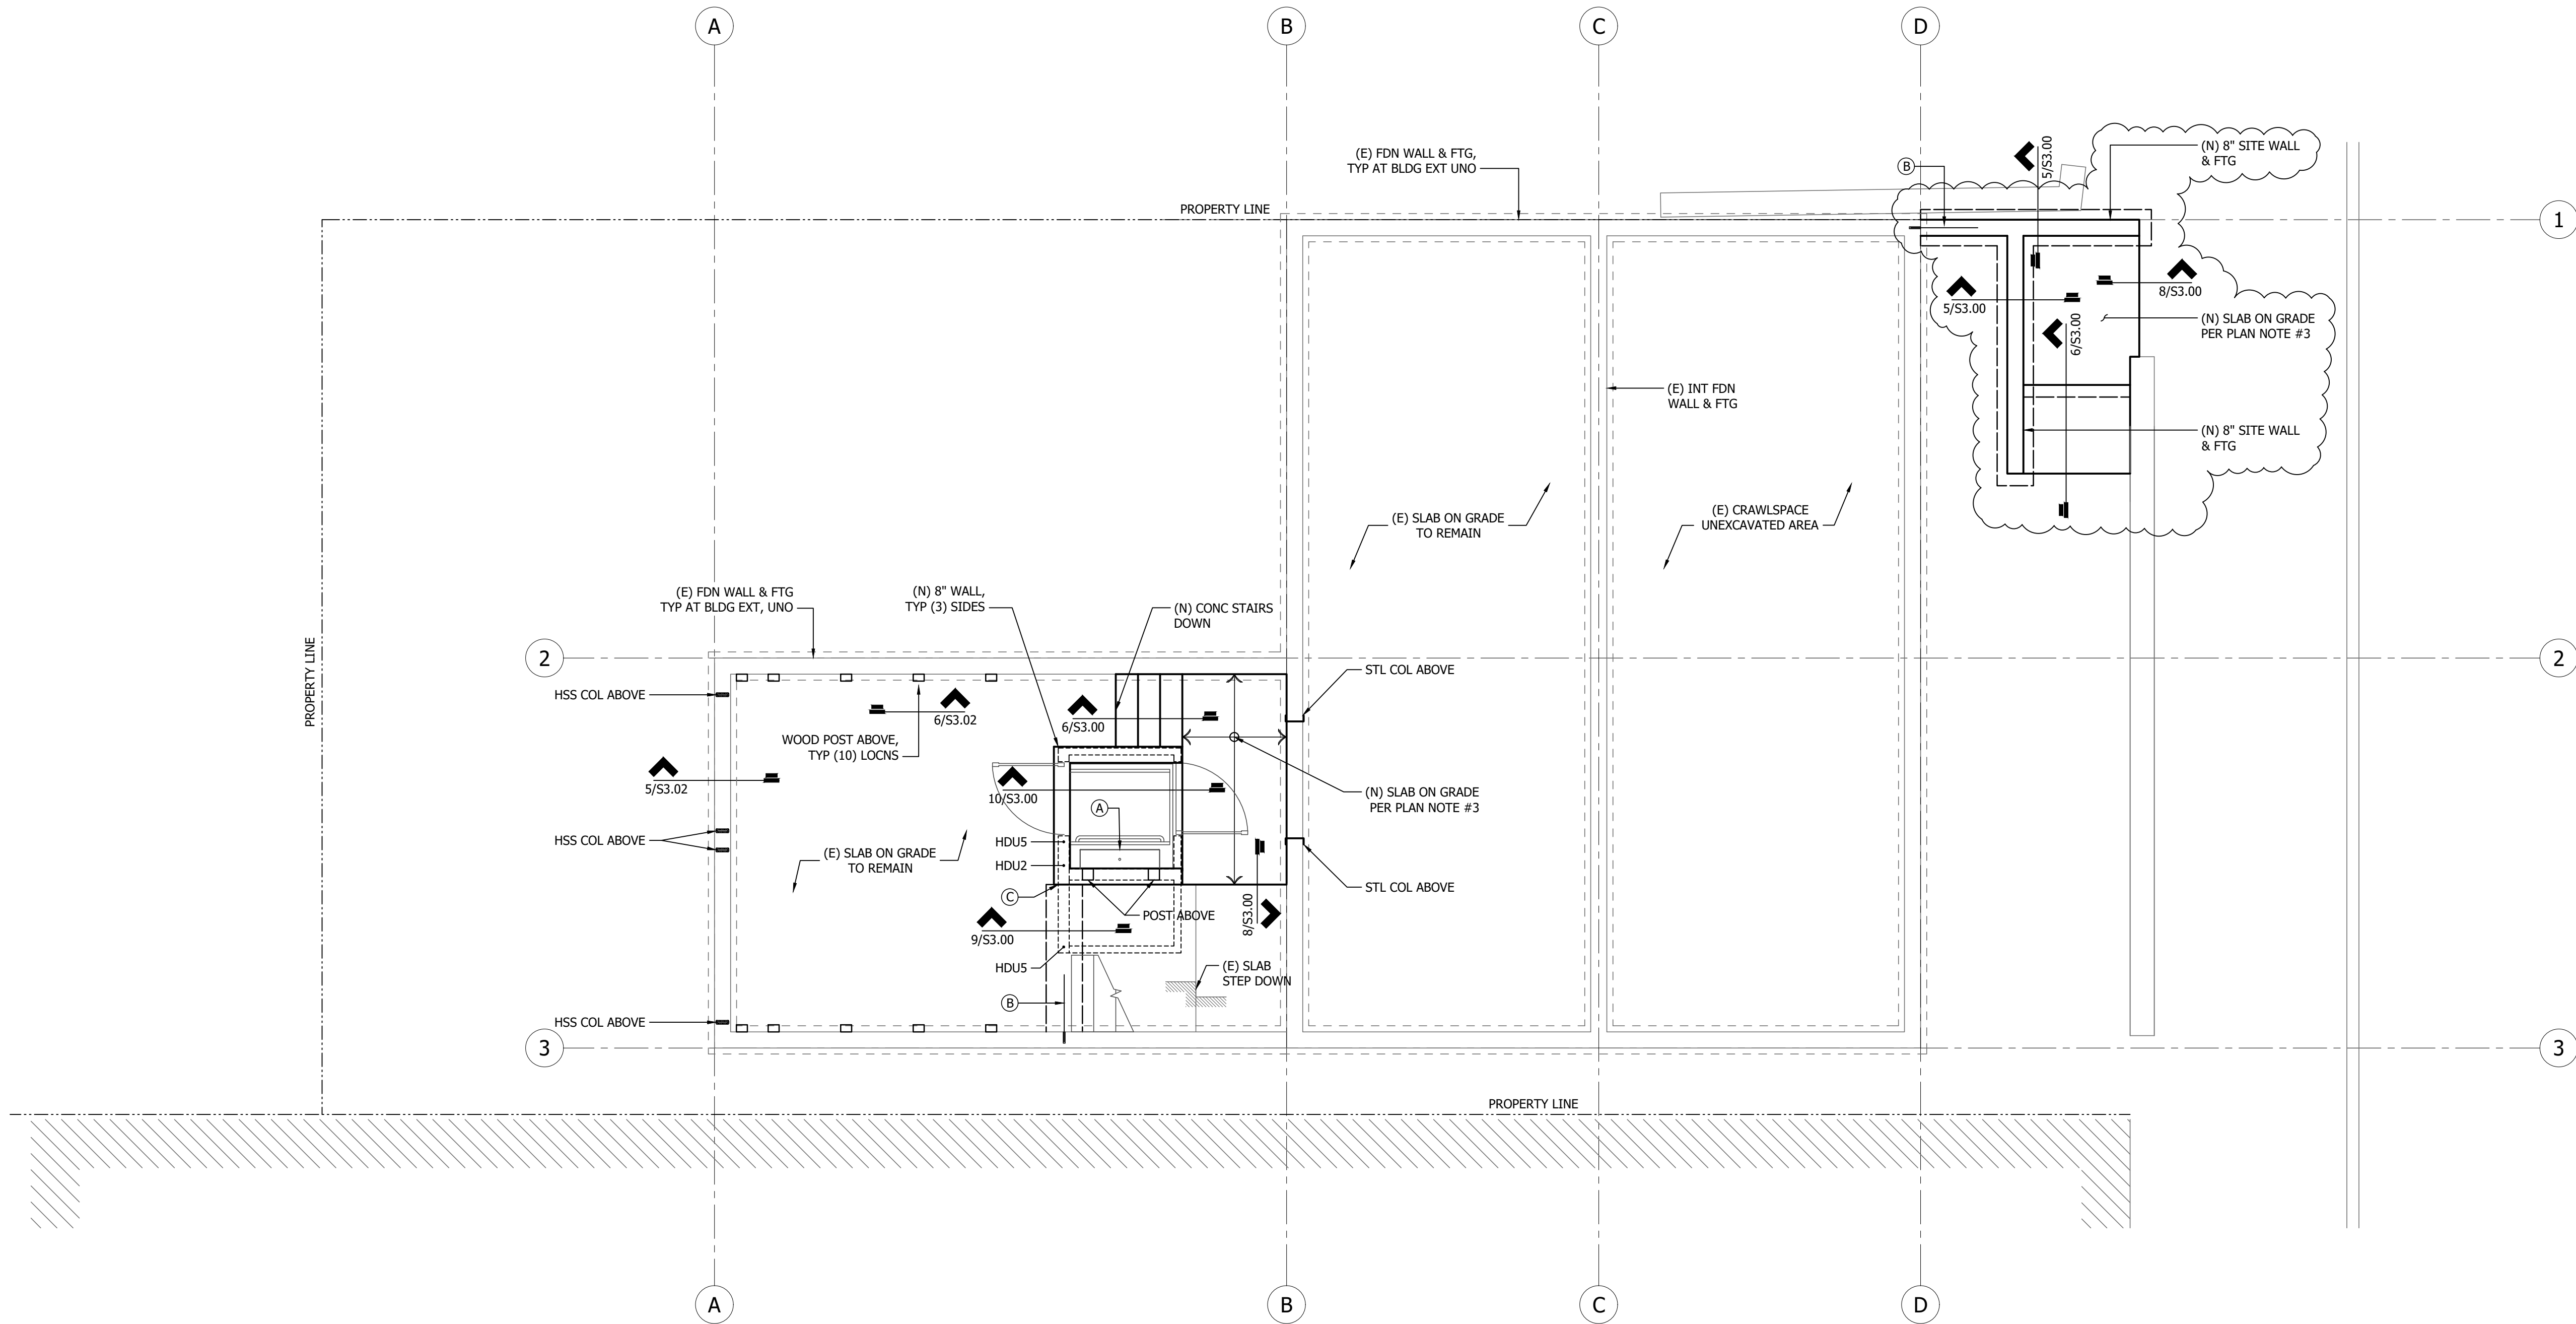

FOUNDATION PLAN

SCALE: 1/4" = 1'-0"

FOUNDATION PLAN NOTES

- REFER TO ARCHITECTURAL DRAWINGS FOR ALL DIMENSIONS, FINISH GRADES, AND TOP OF WALL ELEVATIONS.
- EXISTING CONDITIONS ARE ASSUMED AND SHOULD BE VERIFIED BY THE CONTRACTOR. WHERE DISCOVERED CONDITIONS VARY FROM THOSE SHOWN ON PLANS, CONTRACTOR SHALL CONTACT THE ENGINEER BEFORE PROCEEDING WITH CONSTRUCTION.
- TYPICAL SLAB ON GRADE SHALL BE 4" THICK, REINFORCE w/ #4 BARS @ 18"oc. PROVIDE RIGID INSULATION AT INTERIOR SPACES AND VAPOR BARRIER BELOW SLAB PER ARCHITECTURAL DRAWINGS OVER 4" MINIMUM FREE DRAINING GRAVEL OR CRUSHED ROCK OVER FIRM UNDISTURBED SOIL OR ENGINEERED COMPACTED BACK-FILL.
- ALL FOOTINGS MUST BE CENTERED ON LOADS ABOVE AND PLACED ON FIRM UNDISTURBED SOIL OR ENGINEERED COMPACTED BACKFILL. BOTTOM OF ALL NEW FOOTINGS SHALL BE 18" MINIMUM BELOW ADJACENT GRADE, UNO. REFER TO FOOTING SCHEDULE FOR SIZE AND REINFORCEMENT REQUIREMENTS AT ALL PAD FOOTINGS.
- HD___ INDICATES HOLD-DOWN AT END OF SHEAR WALL ABOVE.
- REFER TO GENERAL STRUCTURAL NOTES AND TYPICAL DETAILS FOR ADDITIONAL REQUIREMENTS.

LEGEND

- NEW CONCRETE WALL/SLAB
- NEW CONCRETE FOOTING (HIDDEN BELOW SLAB/GRADE)
- EXISTING CONCRETE WALL/SLAB
- EXISTING CONCRETE FOOTING (HIDDEN BELOW SLAB/GRADE)
- NEW WOOD WALL FRAMING ABOVE

FOOTNOTES

- (A) REFERENCE ARCH DWGS & LIFT MANUFACTURER SPECS FOR ALL DIMENSIONS, SOIL PLACEMENT/COMPACTION, AND INSTALLATION REQUIREMENTS. LIFT MANUFACTURER TO PROVIDE FINAL SITE SPECIFIC SHOP DRAWINGS FOR DESIGN COORDINATION AND APPROVAL PRIOR TO PROCEEDING WITH CONSTRUCTION.
- (B) PROVIDE NEW #4 x 2'-2" EPOXY DOWELS TO (E) CONC WALL TO MATCH NEW WALL FOOTING REINFORCING PER 7/S3.00.
- (C) STEPPED FOOTING w/ ADDITIONAL BENT DOWELS BETWEEN CONTINUOUS FOOTING AND LIFT WALL FOOTING PER DETAIL 11/S3.00.

SUNDBERG
KENNEDY
LY-AU YOUNG
ARCHITECTS

1501 E MADISON, SUITE 205
SEATTLE WA 98122-4465
206.322.1130



ROICH
STRUCTURAL

P.O. Box 38809 | Seattle, WA 98118
rol@roichstructural.com | 206.745.2967

Official
Stamps:

Eng Family Homestead Renovation
611 8th Ave South, Seattle, WA 98104

FOR CONSTRUCTION
PERMIT SET

9/22/2023

REVISIONS
NO. DESCRIPTION
1 Cycle 1 Revisions

DATE
2/18/24

FOUNDATION PLAN

S2.00

Scale

INTS