




@ NorthWind Architects, LLC, Project Number: NWA-2206

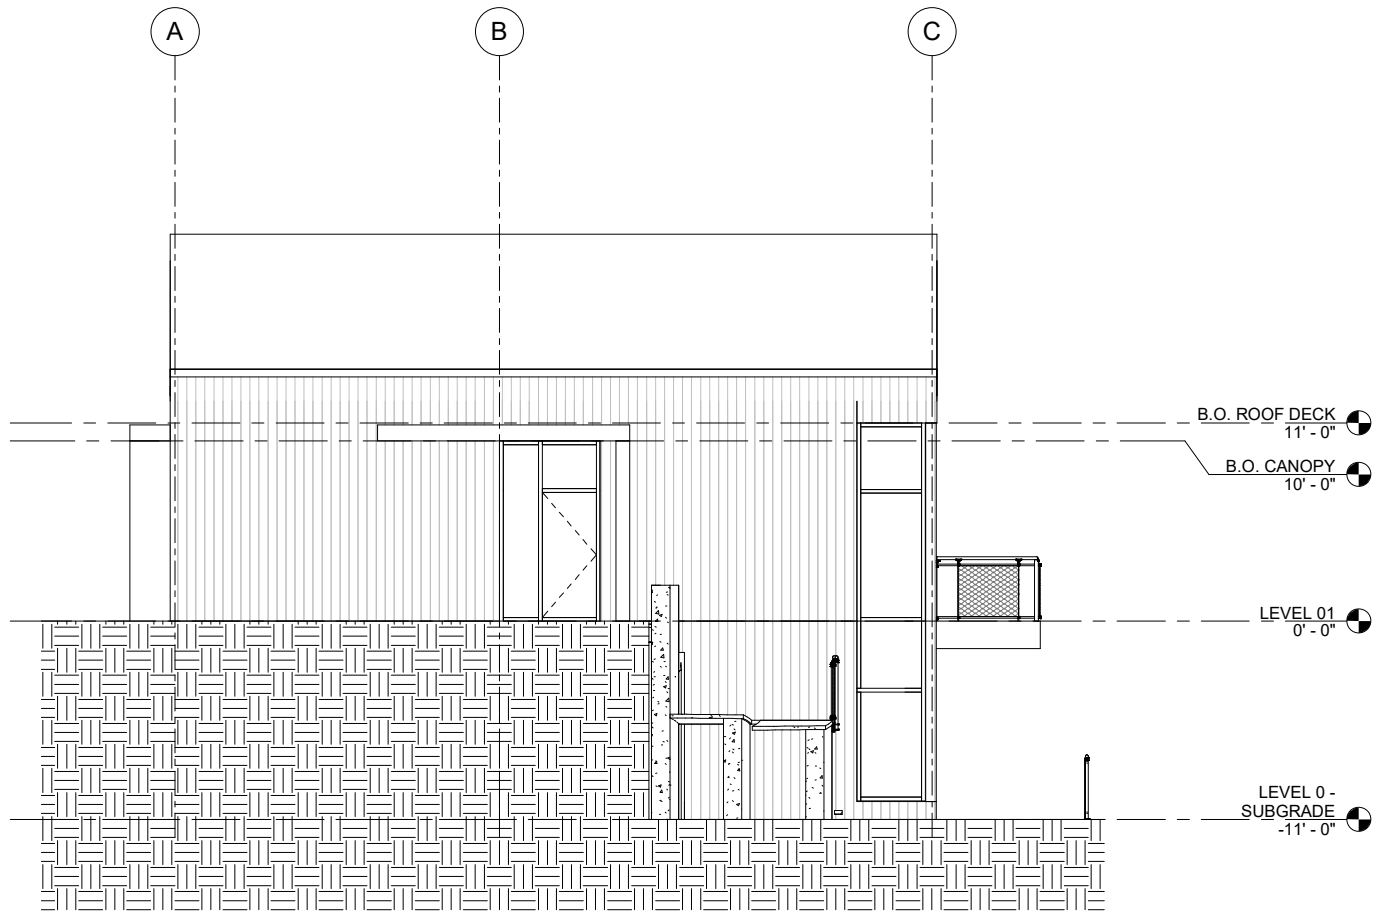


1 ELEVATION EAST
3/16" = 1'-0"

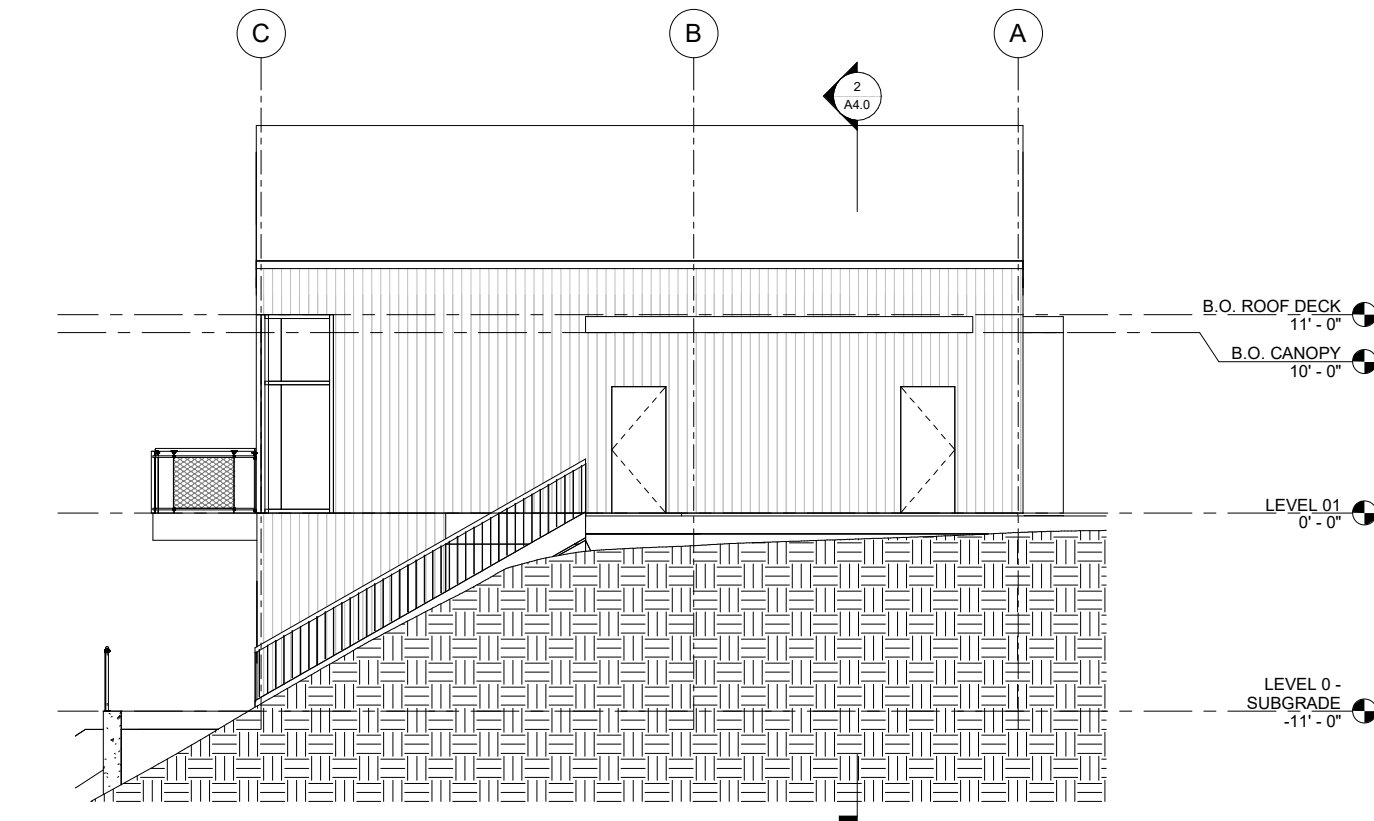


2 ELEVATION WEST
3/16" = 1'-0"

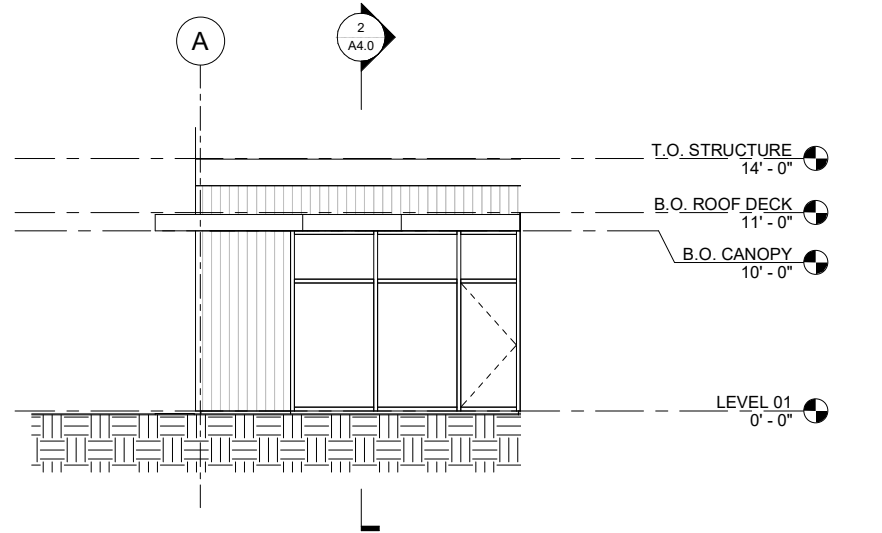

3 ELEVATION - EAST COURTYARD
3/16" = 1'-0"

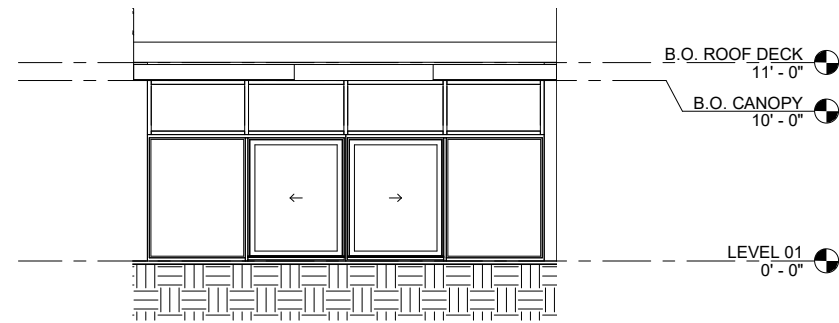

4 ELEVATION - SOUTH COURTYARD
3/16" = 1'-0"

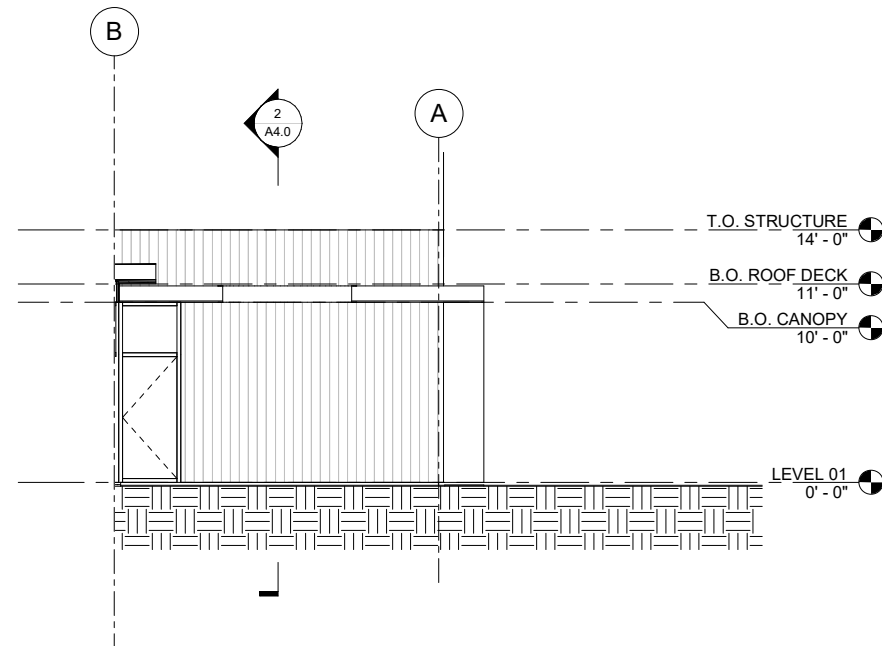

5 ELEVATION - WEST COURTYARD
3/16" = 1'-0"

GENERAL NOTES:

1. CONTRACTOR SHALL FIELD VERIFY ACTUAL BUILDING CONDITIONS AND DIMENSIONS. WHERE DISCREPANCIES OR CONFLICTS ARE FOUND, NOTIFY ARCHITECT PRIOR TO COMMENCING WORK.
2. DO NOT SCALE OFF OF DRAWINGS.
3. DIMENSIONS ARE TO GRIDLINE, FACE OR CENTER OF FRAMING UNO.
4. STRUCTURAL ELEMENTS SHOWN IN ARCHITECTURAL DRAWINGS FOR REFERENCE ONLY. SEE STRUCTURAL DRAWINGS FOR ALL STRUCTURAL INFORMATION.
5. SECTION DRAWINGS FOR REFERENCE ONLY IDENTIFY DATUM AND DETAILS. NOT FOR CONSTRUCTION.
6. TAPERED INSULATION SLOPES NOT SHOWN FOR CLARITY.

SHEET NOTES:

1. #SPEC DESCRIPTION



06/05/2023

NorthWind
Architects, LLC

126 Seward St
Juneau, AK 99801
Ph #907.586.6150
www.northwindarch.com

1" ACTUAL
IF THE ABOVE DIMENSION DOES NOT MEASURE ONE INCH (1") EXACTLY, THIS DRAWING WILL HAVE BEEN ENLARGED OR REDUCED, AFFECTING ALL LABEL SCALES.

AYAYD Cultural Center

DOUGLAS INDIAN ASSOCIATION AND TRIBAL GOVERNMENT

ST. ANNS AVENUE
DOUGLAS, ALASKA

SHEET TITLE:
EXTERIOR
ELEVATIONS

CHECKED Approver
DRAWN Author

issue date description

SHEET #

A3.1

ISSUE DATE

06/05/2023