

FILE PATH: I:\Users\modernhouse\Dropbox\000 ARCH\CAD FILES\Pangan Arch\CAD\PANGAN_BUILDING_Comments2_10082020.dwg • LAST SAVED BY: Modern House - Natsumi • PRINTED ON 4/27/21 @ 3:27 PM WITHOUT THE WRITTEN PERMISSION OF THE ARCHITECT. CURT CLINE • MODERN HOUSE ***PROJECT COMPANY*** • PANGAN RESIDENCE • **PROJECT NUMBER *** • A0.0



NEW RESIDENCE FOR ROY AND EVAN PANGAN

GENERAL NOTES

COORDINATION

- IF THESE DRAWINGS ARE NOT 24" x 36" THEY HAVE BEEN REDUCED OR ENLARGED
- THE STANDARD A.I.A. GENERAL CONDITIONS ARE HEREBY MADE A PART OF THESE DRAWINGS
- ALL WORK SHALL COMPLY WITH THE 2016 CALIFORNIA RESIDENTIAL CODE, CALIFORNIA MECHANICAL CODE, CALIFORNIA PLUMBING CODE, CALIFORNIA ELECTRICAL CODE, CALIFORNIA ENERGY CODE, CALIFORNIA GREEN BUILDING CODE AND CALIFORNIA FIRE CODE
- ALL DIMENSIONS ARE TO FACE OF STUD OR FACE OF CONCRETE UNLESS OTHERWISE NOTED
- DO NOT SCALE DRAWINGS FOR DIMENSIONS. WRITTEN DIMENSIONS SHALL TAKE PRECEDENCE OVER SCALED DIMENSIONS
- DISCREPANCIES BETWEEN THESE DRAWINGS AND ACTUAL SITE CONDITIONS SHALL BE BROUGHT TO THE ATTENTION OF THE ARCHITECT PRIOR TO COMMENCEMENT OF ANY WORK
- CONTRACTOR SHALL PROVIDE SHOP DRAWINGS AND OR SAMPLE BOARDS TO ARCHITECT PRIOR TO ORDERING AND OR INSTALLATION FOR:
 - ALL MILLWORK (CUSTOM OR FACTORY PRODUCED) WITH COUNTER MATERIAL
 - ALL EXTERIOR WINDOWS/DOORS WITH FIN. SAMPLES
 - ALL INTERIOR DOORS WITH FIN. SAMPLES
 - WOOD SIDING (CONNECTION AND CORNERS) WITH FIN. SAMPLES
 - ALL TILE WORK 12"x12" MOCKUP (INTERIOR AND EXTERIOR)
 - EXTERIOR STUCCO 24"x24" MOCKUP
 - EXPOSED FLASHING ELEMENTS (SAMPLE)
 - EXPOSED ROOFING (SAMPLE)

CONTRACTOR DUTIES

- THE CONTRACTOR SHALL:
 - FURNISH, PAY FOR, AND FILE ALL NECESSARY PERMITS, FEES, INSPECTIONS, ETC. EXCEPT FOR PLAN CHECK, ZONING, AND SCHOOL FEES WHICH WILL BE PAID FOR BY THE OWNER
 - GARANTEE ALL WORK FOR ONE YEAR AS EVIDENCED BY THE DATE OF THE FINAL CERTIFICATE OF PAYMENT
 - PROVIDE RELEASE OF ALL SUBCONTRACTOR AND SUPPLIER LIENS BEFORE FINAL PAYMENT IS MADE
 - FILE WORKMAN'S COMPENSATION
 - ARRANGE FOR ALL INSPECTIONS AS CALLED FOR IN SECTION 110 OF THE 2013 CBC

- CONTRACTOR SHALL INSTALL ALL MATERIALS AND EQUIPMENT IN ACCORDANCE WITH MANUFACTURER'S RECOMMENDATIONS AND ALL APPLICABLE CODES
- CONTRACTOR SHALL PROTECT EXISTING VEGETATION AND ADJACENT SITE IMPROVEMENTS FROM DAMAGE DURING THE COURSE OF THE WORK
- CONTRACTOR SHALL BRACE STRUCTURE AS REQUIRED DURING CONSTRUCTION
- CONTRACTOR SHALL PROVIDE STRICT CONTROL OF JOB CLEANUP TO REMOVE DUST AND DEBRIS FROM CONSTRUCTION AREA
- ALL SPECIAL INSPECTION AGENCIES, INDIVIDUALS, AND SHOP FABRICATORS SHALL BE APPROVED BY THE BUILDING DEPARTMENT PRIOR TO ANY WORK BEING PERFORMED. CONTRACTOR SHALL SUBMIT ALL DOCUMENTATION FOR APPROVAL
- CONTRACTOR SHALL PROVIDE PLANS OF GAS LINE SIZING TO THE BUILDING INSPECTION OFFICE PRIOR TO CALLING FOR INSPECTION

GENERAL

- ALL STAIRS WITH MORE THAN THREE RISERS SHALL HAVE ONE (1) 1-1/4" - 2" DIAMETER HANDRAIL w/ 1-1/2" CLEARANCE FROM THE WALL. ALL RAILS SHALL BE BETWEEN 34" AND 38" ABOVE NOSING OF THE TREAD AND BE CONTINUOUS FROM THE TOP RISER TO THE BOTTOM RISER -- 2016 CRC SEC.311
- GUARDRAILS SHALL BE A MINIMUM OF 42" IN HEIGHT AND DESIGNED SUCH THAT A 4" SPHERE CANNOT PASS THROUGH ANY OPENING -- 2016 CRC SEC. R311.7
- 16a. FIREBLOCKING AND DRAFTSTOPPING SHALL BE PROVIDED IN ALL LOCATIONS IN ACCORDANCE w/ 2016 CRC SEC. R302

16b. WHERE THE ROOF PROFILE ALLOWS A SPACE BETWEEN THE ROOF COVERING AND ROOF DECKING, THE SPACE SHALL BE CONSTRUCTED TO PREVENT THE INTRUSION OF FLAMES AND EMBERS. BE FIRESTOPPED WITH APPROVED MATERIALS OR HAVE ONE LAYER OF MINIMUM 72 POUNDS MINERAL-SURFACED NON-PERFORATED CAP SHEET INSTALLED OVER THE COMBUSTIBLE DECKING PER CRC R337.5.2

16c. WHERE VALLEY FLASHING IS INSTALLED, THE FLASHING SHALL NOT BE LESS THAN NO. 26 GAGE GALVANIZED SHEET CORROSION-RESISTANT METAL INSTALLED OVER NOT LESS THAN ON LAYER OF MINIMUM 72-POUND MINERAL-SURFACED NON-PERFORATED CAP SHEET, AT LEAST 36 INCH WIDE RUNNING THE FULL LENGTH OF THE VALLEY PER CRC R337.5.3
- HEARTH SHALL EXTEND 20" IN FRONT AND 12" BEYOND EACH SIDE OF FIREPLACE OPENING
- FIREPLACE SHALL HAVE TIGHT FITTING METAL OR GLASS DOOR AND OUTSIDE AIR INTAKE WITH DAMPER AND CONTROL
- ALL GLAZING SUBJECT TO HUMAN IMPACT SHALL BE TEMPERED -- 2016 CRC SECTIONS R308/R327.8

ENERGY

- THIS BUILDING MEETS THE ENERGY BUILDING DESIGN REQUIREMENTS OF TITLE 24 PART 6. SEE ATTACHED TITLE 24 FOR CERTIFICATE OF COMPLIANCE.
- ALL WINDOWS AND DOORS SHALL BE DOUBLE GLAZED U.O.N.
- FOR PROJECTS IN CALIFORNIA:
 - INSULATION SHALL MEET THE CALIFORNIA ENERGY COMMISSION (C.E.C.) QUALITY STANDARDS AND BE CERTIFIED BY THE MANUFACTURER.
 - ALL FREEZERS, REFRIGERATORS, AND FLUORESCENT LAMP BALLASTS SHALL BE CERTIFIED BY THE C.E.C.
 - ALL HVAC EQUIPMENT, WATER HEATERS, FAUCETS, AND SHOWER HEADS SHALL BE CERTIFIED BY THE C.E.C.
- ALL TOILETS ARE TO BE ULTRA LOW FLOW 1.28 GALLONS MAXIMUM FLUSH CAPACITY PER 2016 CPC 402.2
- THERMOSTATS SHALL BE OF A PROGRAMMABLE DUAL SET BACK TYPE.
- WATER HEATER SHALL BE INSULATED WITH R-12 BLANKET AND PIPES WITHIN FIRST FIVE FEET OF TANK WITH R-4
- GENERAL LIGHTING IN KITCHENS AND BATHS SHALL BE HIGH EFFICACY & COMPLY w/ TITLE 24 CALCULATIONS

LIFE SAFETY

- WHERE REQUIRED BY LOCAL JURISDICTIONS, BUILDINGS TO BE FULLY SPRINKLERED IN ACCORDANCE w/ 2016 CRC SEC. R313/R309.8 AND 2013 NFPA. DRAWINGS TO BE SUBMITTED FOR PERMIT BY DESIGN/BUILD SUBCONTRACTOR
- SMOKE DETECTORS SHALL BE HARD-WIRED IN CEILINGS AND EQUIPPED w/ A BATTERY BACKUP. SEE REFLECTED CEILING AND MECHANICAL PLANS FOR EXACT LOCATIONS -- 2016 CRC SEC.314
- ALL SMOKE DETECTORS TO BE WIRED FOR 24 HOUR MONITORING BY REMOTE ANSWERING STATION PER NFPA 72

MEP

- ALL GAS APPLIANCES SHALL HAVE GAS IGNITER TYPE PILOTS AND INTERMITTENT IGNITION DEVICES
- CLOTHES DRYERS SHALL BE VENTED TO THE OUTSIDE. PROVIDE BACKDRAFT DAMPER
- WATER HEATERS SHALL BE SECURELY FASTENED TO PREVENT OVERTURNING AS DETAILED ON DRAWING 2/A8.4 -- 2016 CRC R301.2.2.3.7
- ALL HOT WATER FAUCETS WITH 10 FEET OR MORE OF PIPE BETWEEN FAUCET AND WATER HEATER ARE TO BE EQUIPPED WITH HOT WATER RECIRCULATING SYSTEM
- ALL SHOWERS AND TUB-SHOWER COMBINATIONS SHALL BE PROVIDED WITH INDIVIDUAL CONTROL VALVES OF THE PRESSURE BALANCE OR THE THERMOSTATIC MIXING VALVE TYPE
- ALL HOSE BIBBS SHALL HAVE APPROVED NON-REMOVABLE BACKFLOW PREVENTION DEVICES -- 2016 CRC AP103.3
- DUCTS SHALL BE CONSTRUCTED, INSTALLED AND INSULATED PER 2010 CMC
- EXHAUST SYSTEMS SHALL HAVE DAMPER CONTROLS
- ALL ELECTRICAL OUTLETS IN EXTERNAL WALLS SHALL HAVE INSULATING GASKETS
- NO LIGHT FIXTURES IN CLOTHES CLOSETS SHALL BE CLOSER THAN 12" TO COMBUSTIBLE STORAGE ITEMS -- 2016 CRC
- ALL 120V / 1-PH / 15- & 20- AMP BRANCH CIRCUITS IN BEDROOMS SHALL BE PROTECTED BY A LISTED ARC-FAULT CIRCUIT INTERRUPTER -- 2016 CEC ARTICLE 210.12
- HYRO RADIANT. CONTRACTOR SHALL DOCUMENT AND PROVIDE DIMENSIONED DRAWING/ WITH PICTURES OR VIDEO FOR THE OWNER SHOWING LOCATIONS OF ALL IN FLOOR HYRO- RADIANT TUBING.

FRAMING PLANS AND LIGHTING COORDINATION

- CONTRACTOR SHALL REVIEW ALL RCP/LIGHTING PLANS PRIOR TO SETTING FLOOR/ROOF JOIST MEMBERS TO ALLOW FOR LIGHTING PLACEMENT AS SHOWN. CONTRACTOR SHALL SPOT LOCATE (PAINT OR OTHER MEANS) ALL RECESSED FIXTURES AND NOTIFY THE ARCHITECT FOR A WALK THRU PRIOR TO SETTING OF CANS IN PERMANENT LOCATION.

ARCHITECT SHALL HAVE ACCESS TO THE SITE AT ALL TIMES

- PRIOR TO BUILDING PERMIT FINAL APPROVAL, THE PROPERTY SHALL BE IN A COMPLIANCE WITH THE VEGETATION MANAGEMENT REQUIREMENTS PRESCRIBED IN CALIFORNIA FIRE CODE (SECTION 4906, INCLUDING CALIFORNIA PUBLIC RESOURCES CODE 4291 OR CALIFORNIA GOVERNMENT CODE SECTION 51182 PER CRC R337.1.5.

SYMBOLS

- GRID LINE - F.O.S. UNLESS OTHERWISE NOTED
- DIMENSION TO FACE OF FRAMING
- DIMENSION TO CENTERLINE
- DIMENSION TO FACE OF FINISH
- DETAIL REFERENCE SHEET LOCATION
- INTERIOR ELEVATION KEY AND SHEET LOCATION
- DOOR NUMBER, SEE DOOR SCHEDULE
- WINDOW NUMBER, SEE WINDOW SCHEDULE
- ELEVATION DATUM POINT
- CROSS SECTION SHEET LOCATION
- EXTERIOR ELEVATION
- SPOT ELEVATION
- DRAWING KEYNOTE
- MATCH LINE
- DRAWING REVISION

PROJECT DATA


LOCATION:	AUGUSTA CT MILPITAS, CA 95035
APN:	029-35-005
ZONING:	HS-d2
LOT SIZE:	1,688,821.20 SQ. FT. (38.77 ACRES)
BLDG USE:	SINGLE FAMILY
OCCUPANCY GROUP:	R-3U
CONSTRUCTION TYPE:	TYPE VB
CLIMATE ZONE:	NA
BLDG. CODE:	2016 CALIFORNIA BUILDING, RESIDENTIAL, PLUMBING, ELECTRICAL, ENERGY, GREEN BUILDING STANDARDS, FIRE AND MECHANICAL CODES
ITEMS TO BE UNDER SEPARATE PERMIT(S):	AUTOMATED FIRE SPRINKLER, SOLAR WATER HEATING SYSTEM
PROJECT SCOPE:	NEW SINGLE FAMILY

SEE SITE PLAN SHEET A1.0 FOR FLOOR AREA CALCULATIONS

DIRECTORY

OWNER:	ROY AND EVAN PANGAN 2767 BELMONT TR FREMONT CALIFORNIA 94539 Tel: 503.641.8311 EMAIL: CHRIS@SFADG.COM
ARCHITECT:	MODERN HOUSE ARCHITECTS 1265 INDIANA STREET SAN FRANCISCO CALIFORNIA 94107 TEL: (415) 596-7281 EMAIL: MODERNHOUSE@MAC.COM
GENERAL CONTRACTOR:	TBD
STRUCTURAL ENGINEER:	SFA DESIGN GROUP 1813 RUTAN DR, SUITE C LIVERMORE, CALIFORNIA 94551 TEL: 503.641.8311 WWW.SFADG.COM
LANDSCAPE ARCHITECT:	FIELD LANDSCAPE DESIGN 1265 INDIANA STREET SAN FRANCISCO, CA 94107 TEL: (415) 928-5775 EMAIL: chris@fielddesign@gmail.com
CIVIL/SURVEY:	WESTFALL ENGINEERS, INC. 14583 BIG BASIN WAY SARATOGA, CA 95070 TEL: (408) 867-0244 EMAIL: jtk@westf.com
GEOTECHNICAL ENGINEER:	EARTH SYSTEMS 48511 WARM SPRING BLVD., SUITE 210 FREMONT, CA 94539 (510) 353-3833 WWW.EARTHSYSTEMS.COM

VICINITY MAP

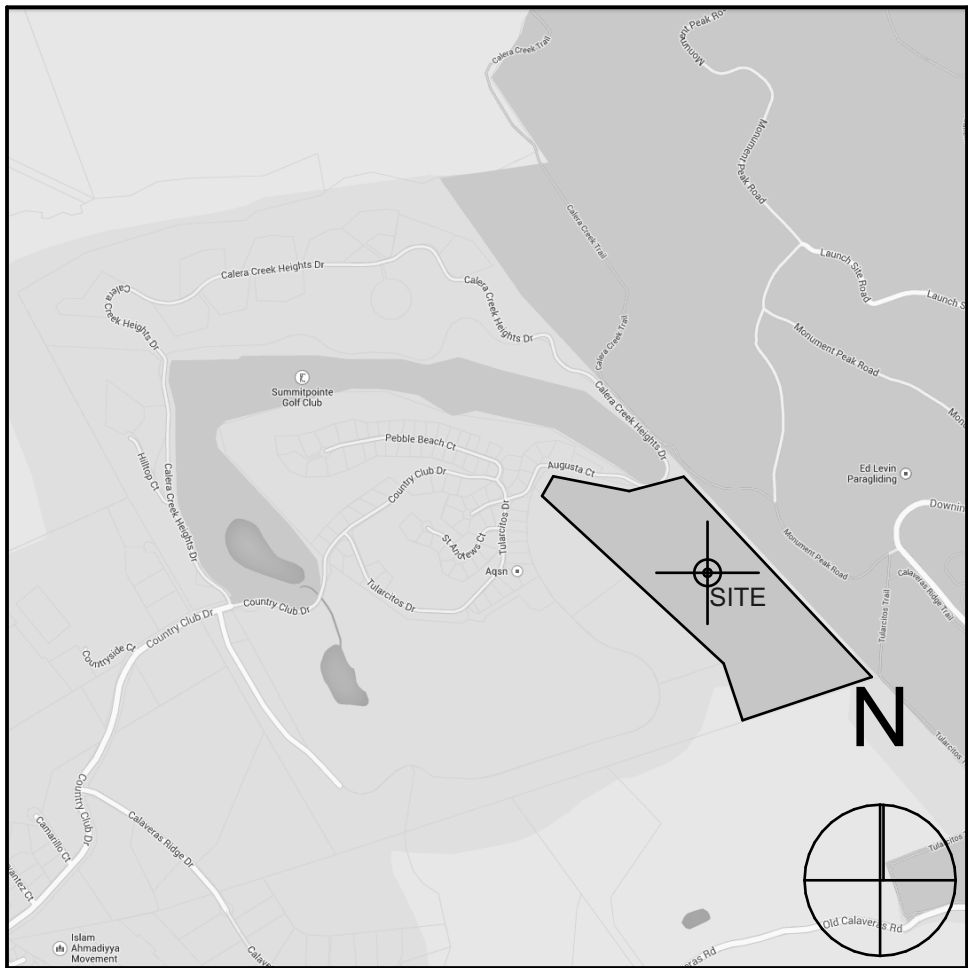

DRAWING INDEX

CIVIL DRAWINGS

BMP-1	BEST MANAGEMENT PRACTICES
BMP-2	BEST MANAGEMENT PRACTICES
C1	CIVIL COVER SHEET
C2	IMPROVEMENT PLAN
C3	IMPROVEMENT PLAN
C4	IMPROVEMENT PLAN
C5	IMPROVEMENT PLAN
C6	GRADING AND DRAINAGE PLAN
C7	SECTIONS
C8	SECTIONS
C9	EROSION CONTROL PLAN
C10	DETAILS
C11	SEPTIC SYSTEM DESIGN
C12	ACCESS DRIVEWAY
C13	ACCESS DRIVEWAY
C14	EXTERIOR RETAINING WALLS

IRRIGATION PLAN

I-1	IRRIGATION PLAN
I-2	IRRIGATION LEGEND AND NOTES
I-3	IRRIGATION DETAILS 1
I-4	IRRIGATION DETAILS 2
I-5	IRRIGATION WATER CALCULATIONS
L1	LANDSCAPE PLAN

ARCHITECTURAL

A0.0	COVERSHEET
A0.1	CALGREEN RESIDENTIAL MANDATORY MEASURES
A0.2A	2016 CALGREEN RESIDENTIAL CHECKLIST
A0.2B	2016 CALGREEN RESIDENTIAL CHECKLIST (CONT'D)
A0.3	INSTRUCTIONS FOR BIDDERS
A0.4	SITE SURVEY
A0.5	SPECIFICATIONS
A0.6	SPECIFICATIONS SUPPLEMENTAL
A0.7	FLOOR AREA CALCULATION
A1.0	SITE PLAN
A1.2	LAND DISTURBANCE SITE PLAN
A2.0	GROUND FLOOR PLAN
A2.1	MAIN FLOOR PLAN
A2.2	ROOF PLAN
A3.1	NORTH & WEST ELEVATIONS (PROPOSED)
A3.2	SOUTH & EAST ELEVATIONS (PROPOSED)
A4.1	BUILDING SECTIONS
A5.1	RCP/LIGHTING PLAN GROUND FLOOR
A5.2	RCP/LIGHTING PLAN MAIN FLOOR
A5.3	LIGHTING SPECIFICATIONS (Interior)
A5.4	LIGHTING SPECIFICATIONS (Interior)
A6.1	DOOR SCHEDULE
A6.2	DOOR SCHEDULE (CONT'D)
A6.3	WINDOW SCHEDULE
A7.1	INTERIOR ELEVATIONS
A7.2	INTERIOR ELEVATIONS
A7.3	INTERIOR SPECIFICATIONS
A8.1	DETAILS
A8.2	DOOR DETAILS
A8.3	WINDOW DETAILS
A8.4	ROOF DETAILS
A9.1	STAIR SECTIONS/ DETAILS
T-1	TITLE 24 REPORT
T-2	TITLE 24 REPORT

STRUCTURAL DRAWINGS

S1.1	GENERAL NOTES
S1.2	GENERAL NOTES
S2.1	FOUNDATION PLAN
S2.2	2ND FLOOR FRAMING PLAN
S2.3	ROOF FRAMING PLAN
S4.1	FOUNDATION DETAILS
S5.1	FRAMING DETAILS
S5.2	FRAMING DETAILS
S5.3	FRAMING DETAILS
S5.4	FRAMING DETAILS
S5.5	FRAMING DETAILS

FOR COUNTY APPROVAL STAMP

MODERN HOUSE

ARCHITECTURE

& DESIGN

1265 Indiana Street
San Francisco Ca. 94107
P. 415.800.8520
C. 415.596.7281
modernhouse@mac.com
www.modernhousearchitects.com



Curt Cline Architect

BUILDING PERMIT REVIEW
029-35-005
PANGAN RESIDENCE
AUGUSTA CT
MILPITAS, CA

REVISIONS:

1	BUILDING COMMENTS 11/29/2018
2	BUILDING COMMENTS 9/16/2020

COVERSHEET

SCALE : AS NOTED

07.26.2018

SHEET : A0.0

THESE DRAWINGS ARE THE ORIGINAL UNPUBLISHED WORK OF THE ARCHITECT. NO PART OF THESE DRAWINGS MAY BE REPRODUCED OR TRANSMITTED IN ANY FORM OR BY ANY MEANS, WITHOUT THE WRITTEN PERMISSION OF THE ARCHITECT. CURT CLINE • MODERN HOUSE