




ALL RIGHTS RESERVED. NO USE OR
REPRODUCTION OF THIS MATERIAL IS PERMITTED
WITHOUT WRITTEN CONSENT.

DO NOT SCALE THE DRAWINGS. USE ALL
DIMENSIONS SHOWN. VERIFY ALL DIMENSIONS ON
SITE & NOTIFY ARCHITECT OF ANY
DISCREPANCIES.

[illegible]

PROJECT NAME:

11 SILVER HILL RD
WESTON, MA

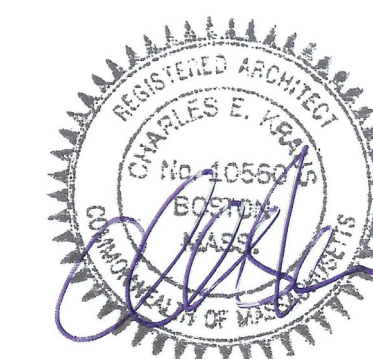

DRAWING NAME:


FIRST FLOOR FRAMING PLAN

DATE:	03.16.2023
PROJECT NO:	21031
SCALE:	1/4" = 1'-0"
DRAWN & CHECKED BY:	JJ/CK

DRAWING NO:

A3.2

2023.03.16 - PROGRESS SET

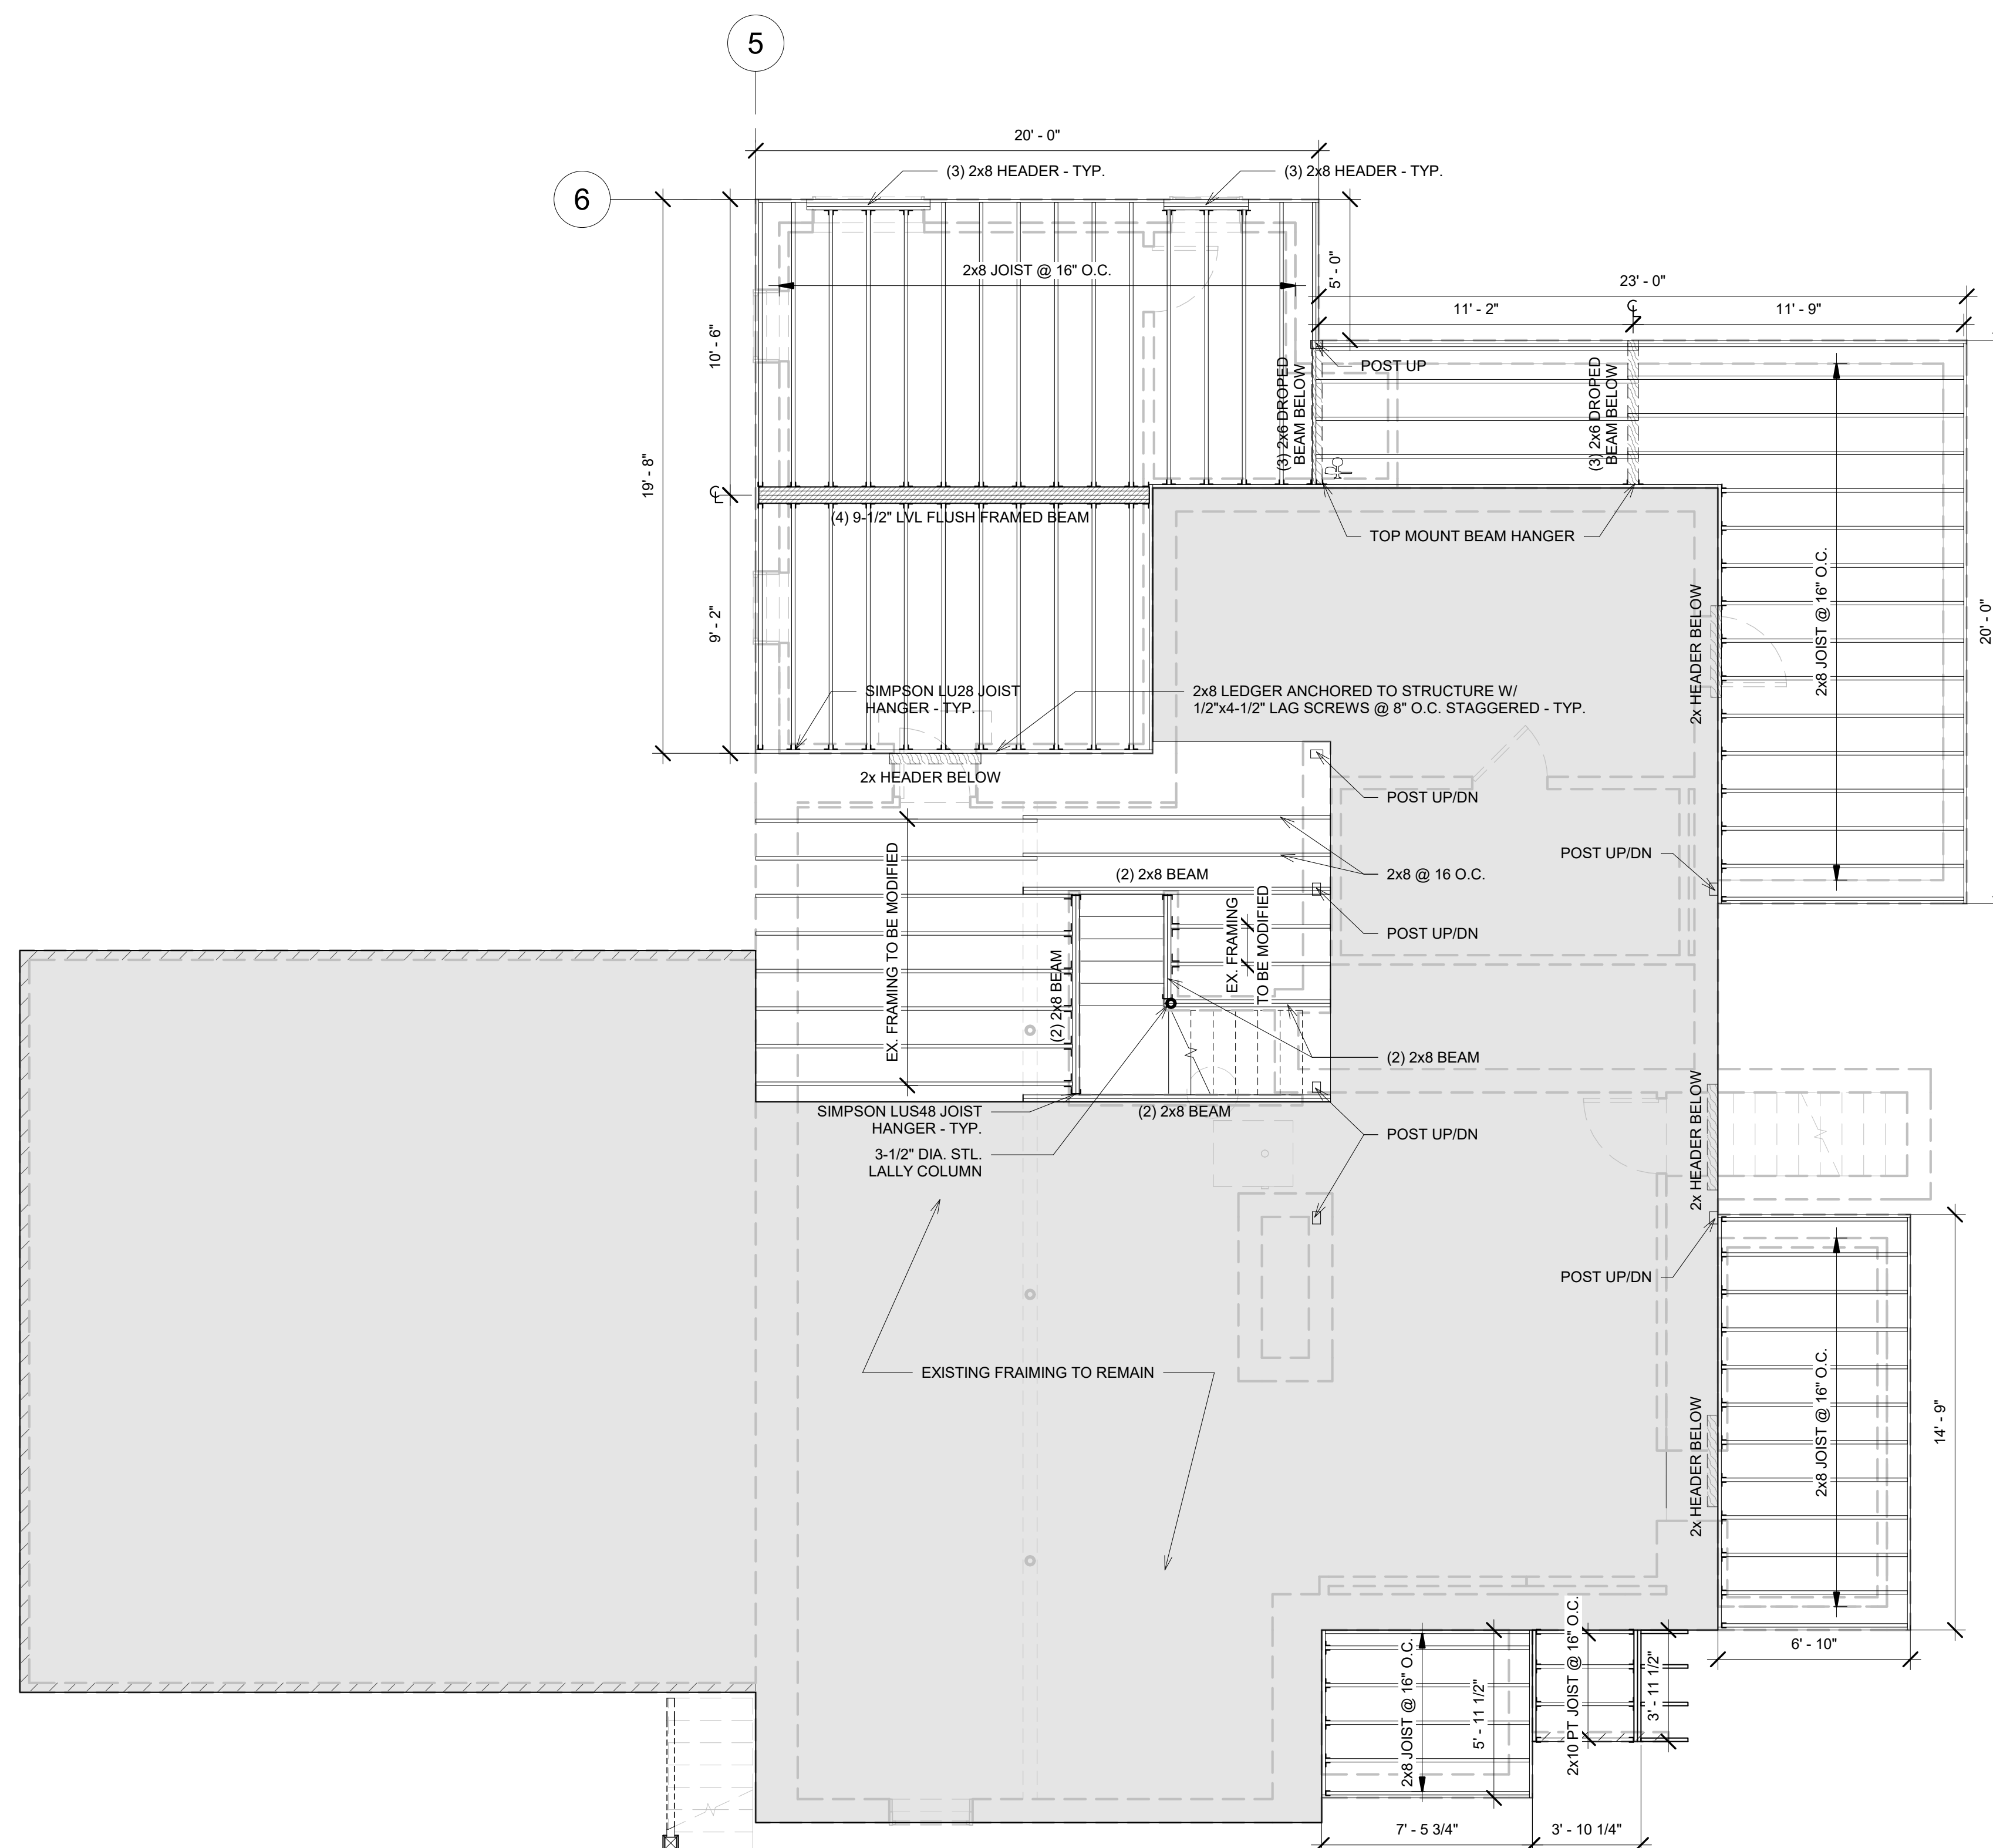

1 FIRST FLOOR FRAMING PLAN
1/4" = 1'-0"

