


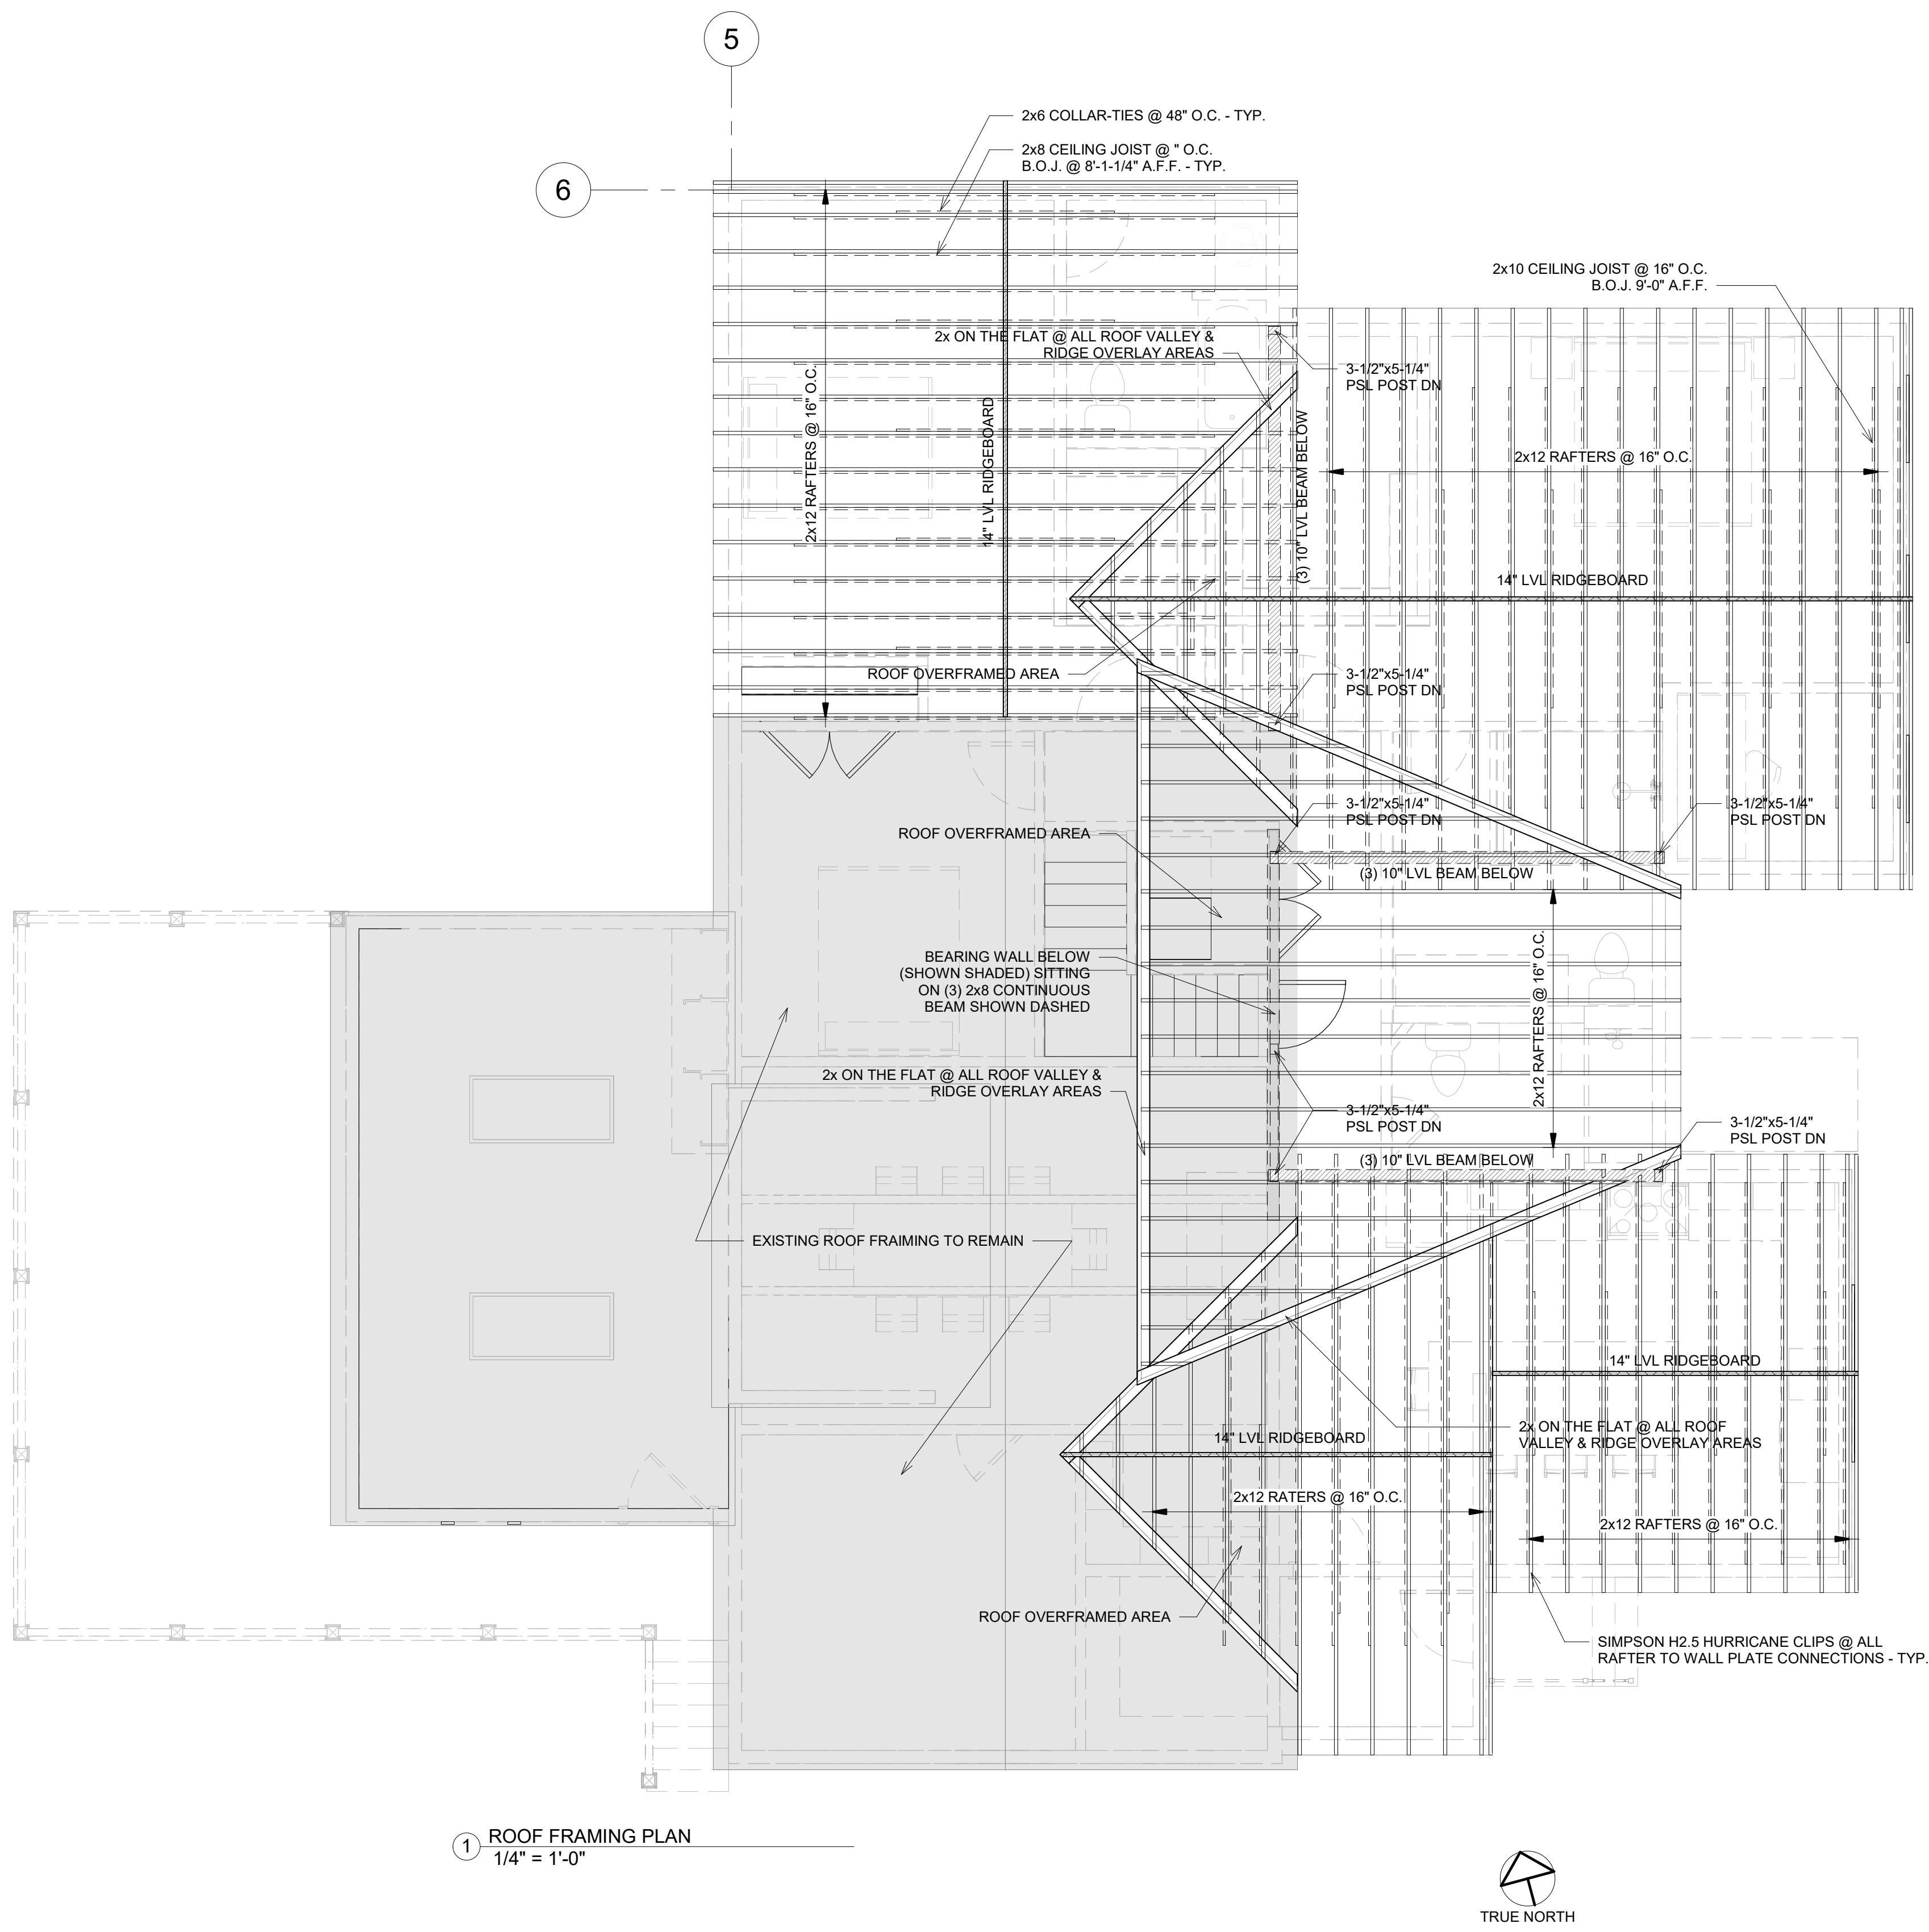

1 ROOF FRAMING PLAN
1/4" = 1'-0"



KRAUS ASSOCIATES

66 CENTRAL STREET STE. 2
WELLESLEY, MA 02482
(781) 431-7400
WWW.KRAUSAB.COM


ALL RIGHTS RESERVED. NO USE OR REPRODUCTION OF THIS MATERIAL IS PERMITTED WITHOUT WRITTEN CONSENT.

DO NOT SCALE THE DRAWINGS. USE ALL DIMENSIONS SHOWN. VERIFY ALL DIMENSIONS ON SITE & NOTIFY ARCHITECT OF ANY DISCREPANCIES.

No.	Date	Description

PROJECT NAME:
PIGNATELLI RESIDENCE


**11 SILVER HILL RD
WESTON, MA**

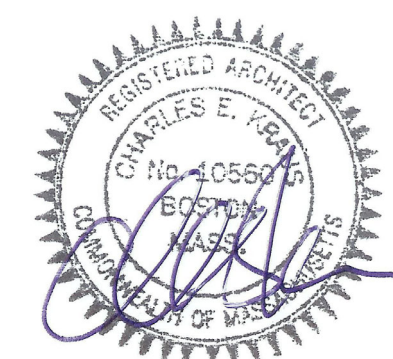

DRAWING NAME:
ROOF FRAMING PLAN

DATE:	03.16.2023
PROJECT NO:	21031
SCALE:	1/4" = 1'-0"
DRAWN & CHECKED BY:	JJ/CK
DRAWING NO:	

A3.3

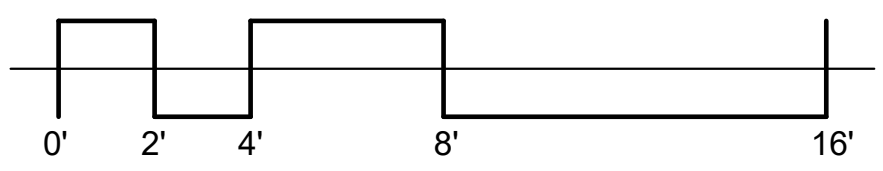

2023.03.16 - PROGRESS SET