



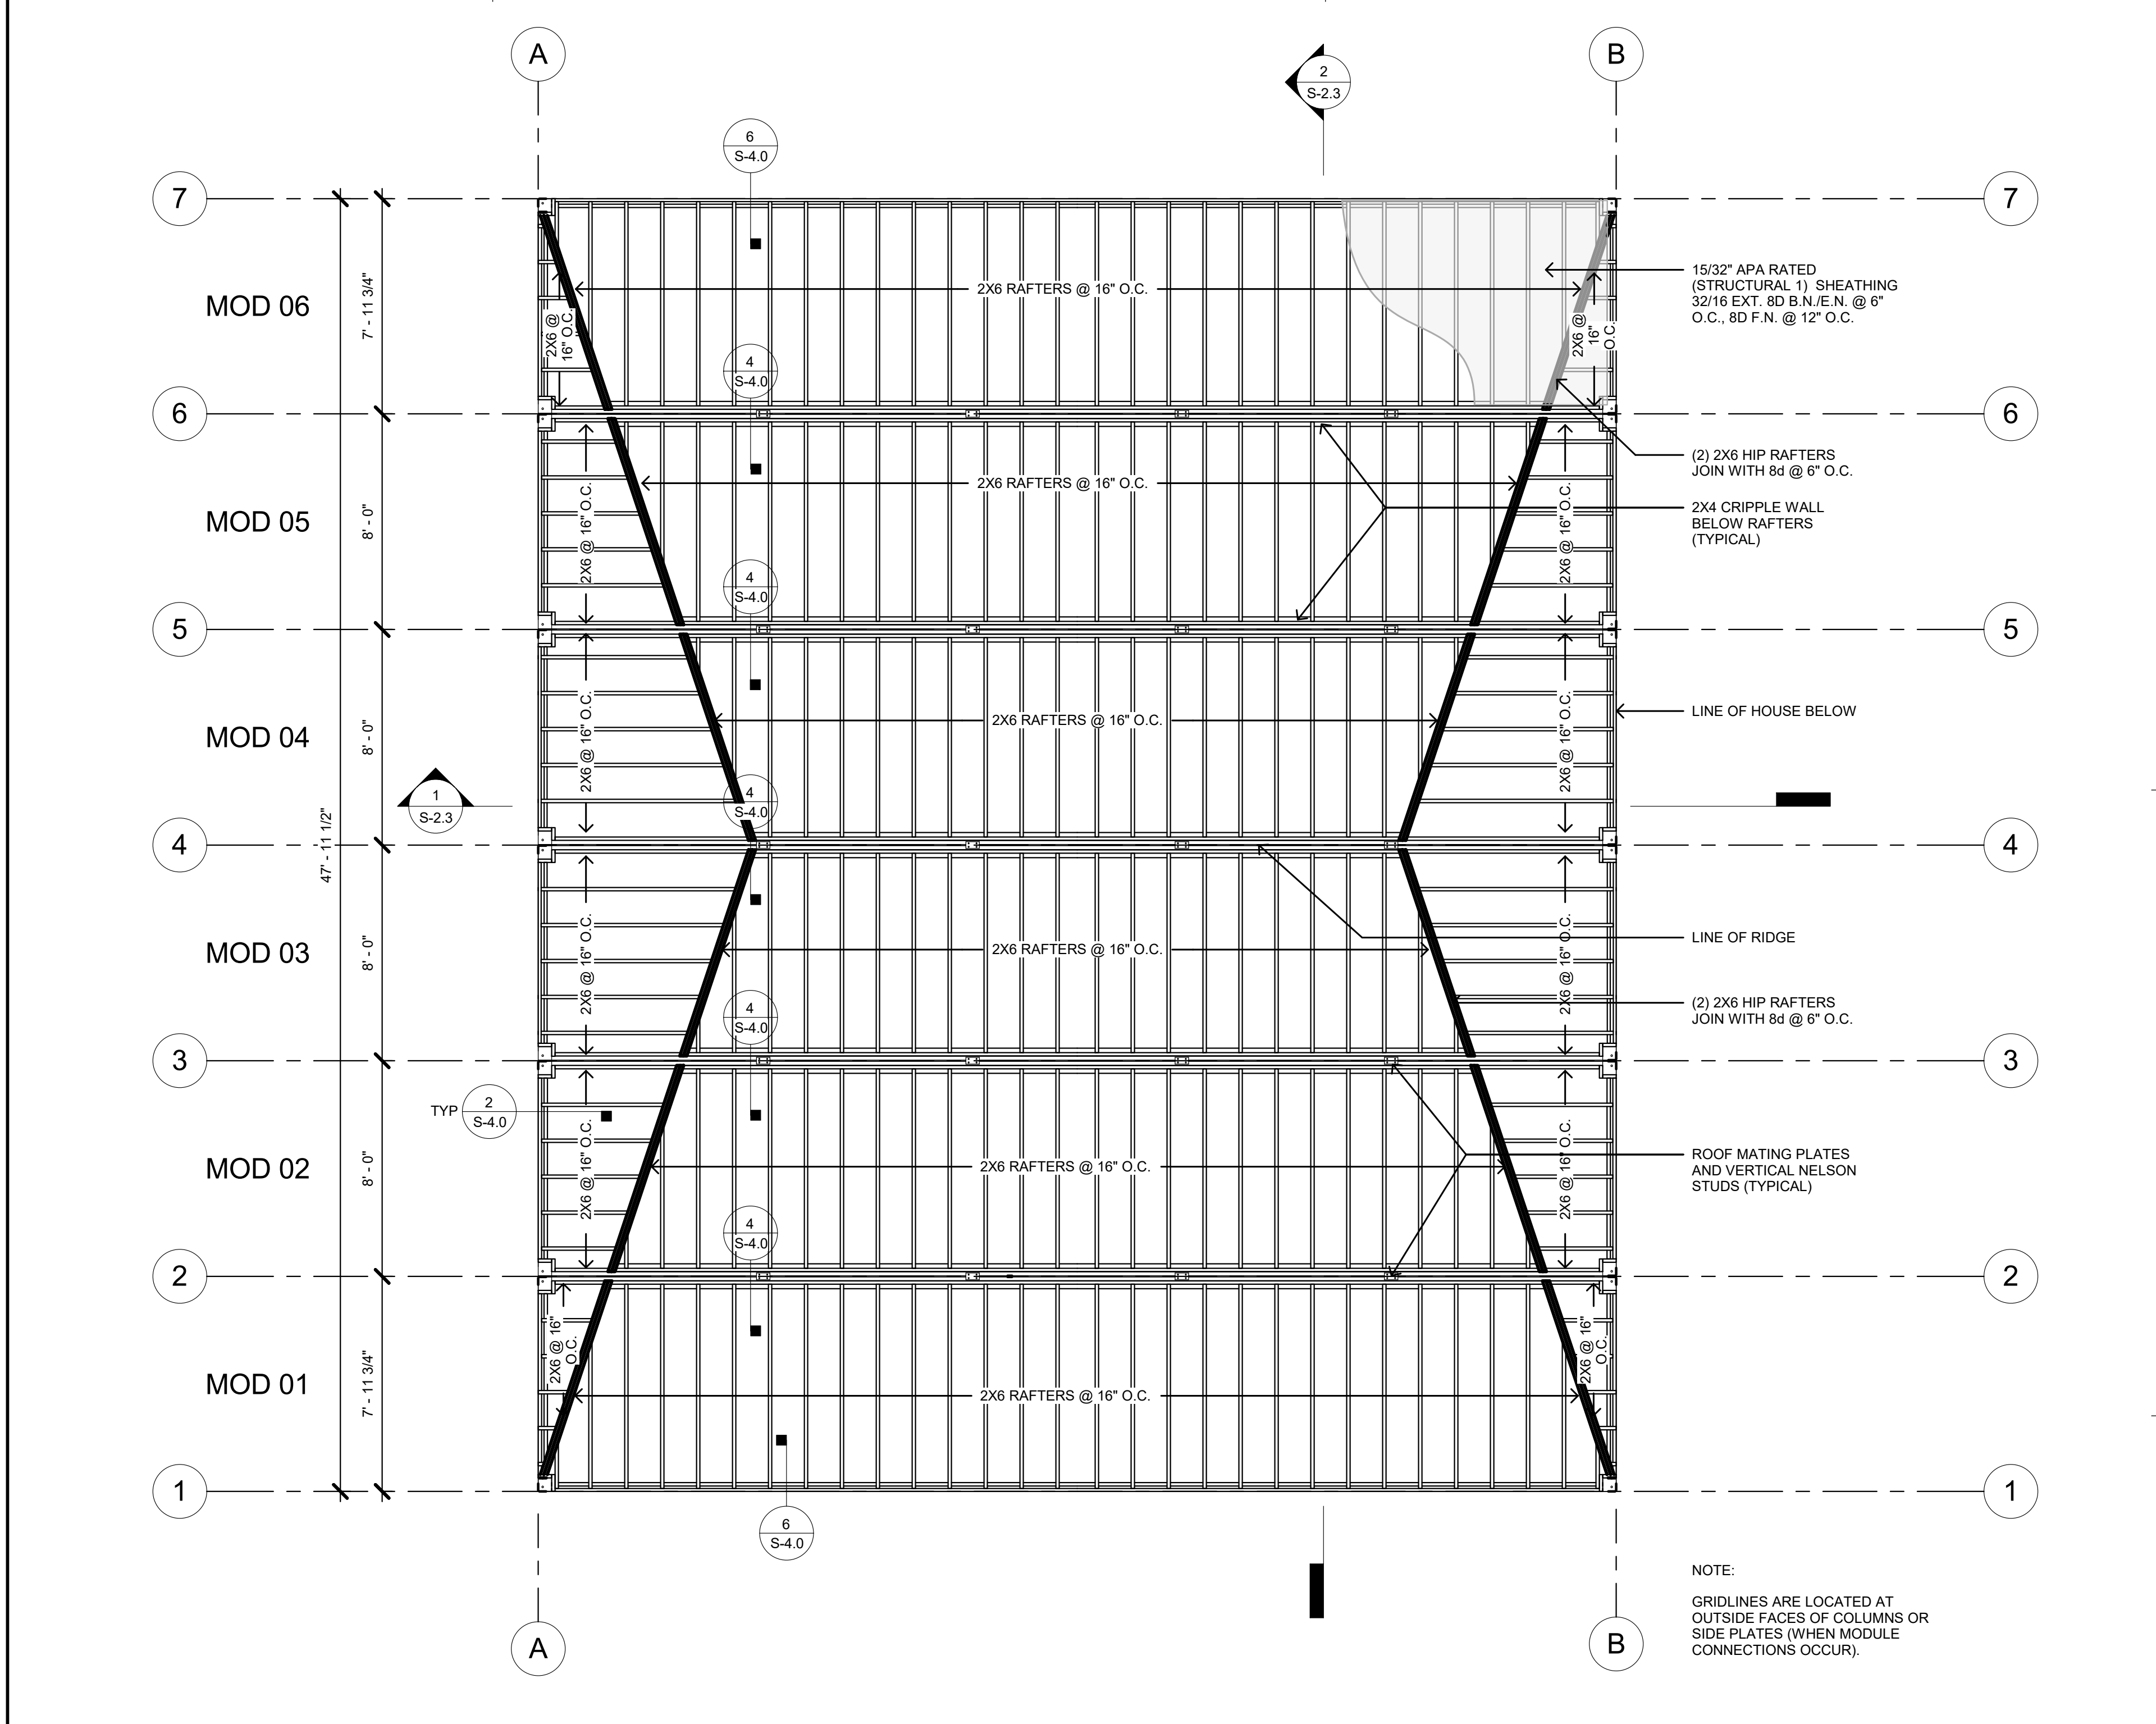


S - STRUCTURAL ROOF FRAMING PLAN - FACTORY BUILT
1/4" = 1'-0"

3

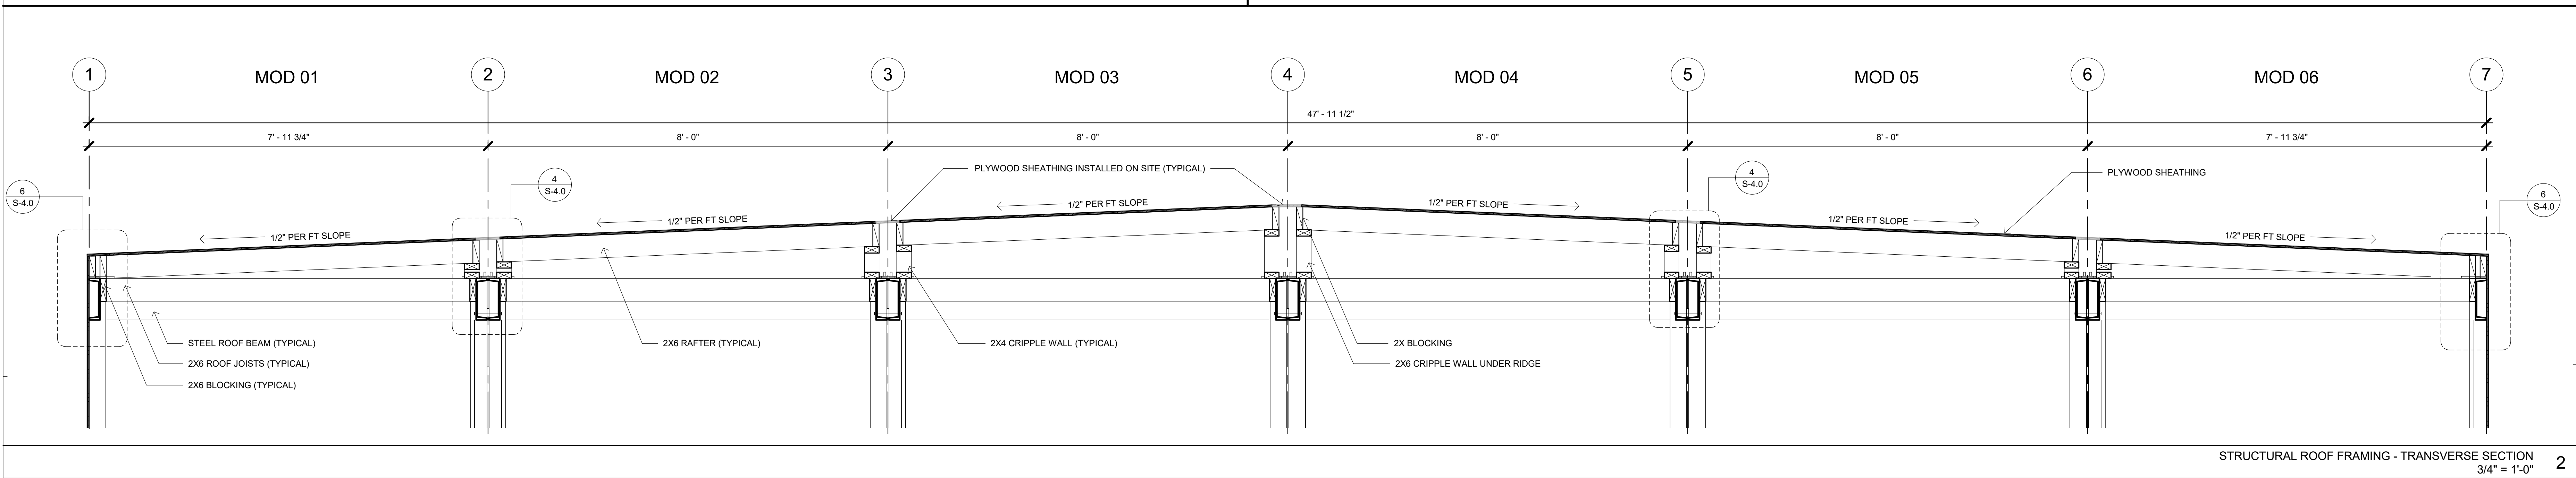

STRUCTURAL ROOF FRAMING - TRANSVERSE SECTION
3/4" = 1'-0"

2

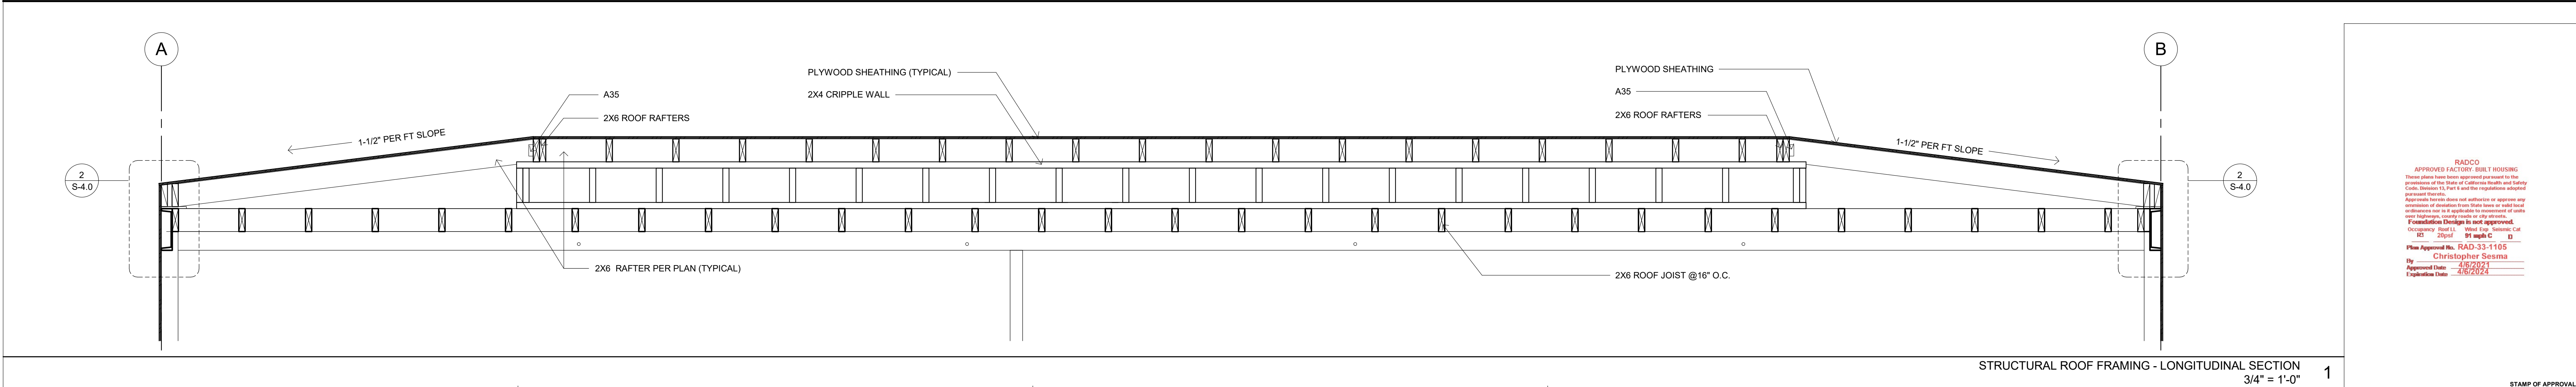

STRUCTURAL ROOF FRAMING - LONGITUDINAL SECTION
3/4" = 1'-0"

1