


BUILDING ENVELOPE SCHEDULE	
WALL INSULATION (ABOVE GRADE)	R-23 INTERMEDIATE
WALL INSULATION (BELOW GRADE)	N/A
FLAT CEILINGS	R-49
VAULTED CEILINGS	R-49
UNDER FLOOR (CRAWL SPACE)	R-38
SLAB EDGE PERIMETER	N/A
HEATED SLAB INTERIOR	N/A
WINDOWS	U-0.25
SKYLIGHTS	N/A
EXTERIOR DOORS	U-0.20

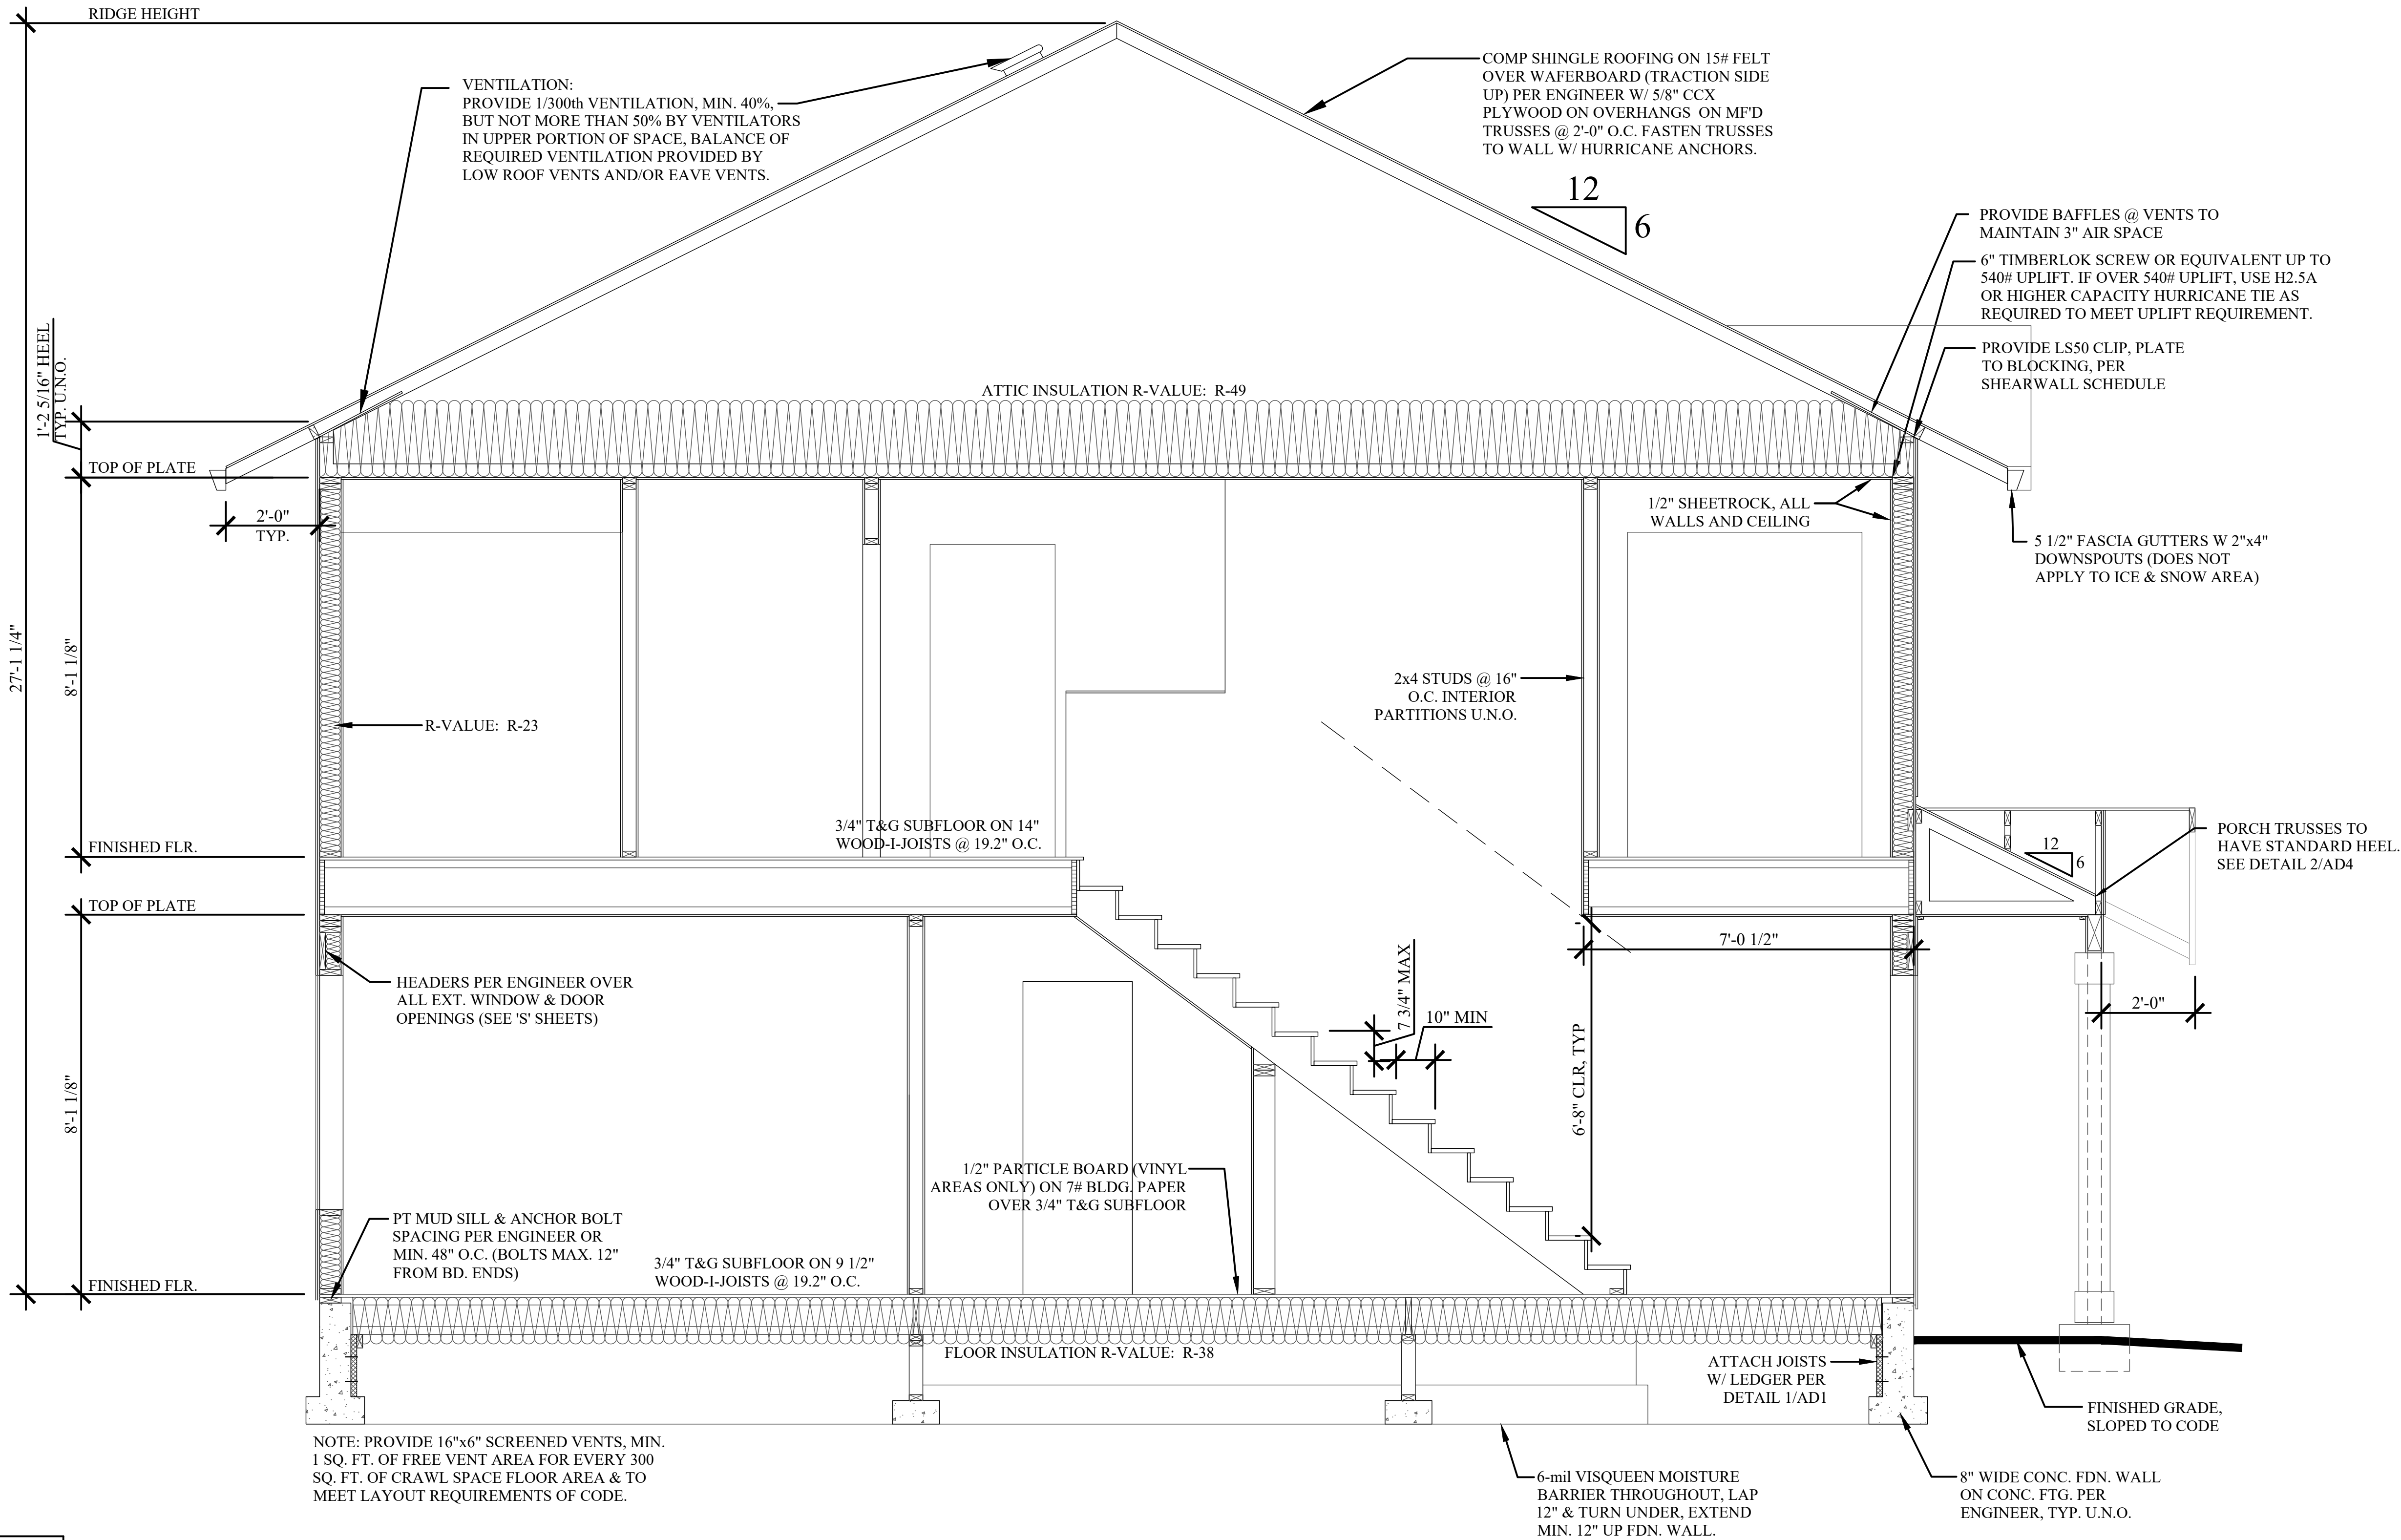

BUILDING SECTION A

1/2" = 1'-0"



ADAIR HOMES, INC
4400 NE 77TH AVE
SUITE 100
VANCOUVER, WA 98662

HODSON #1 - 2386

PLAN ORIENTATION:
STANDARD

COMMUNITY CODE / LOT#:
MEME-122

BUILDING SECTION A

2023 ORSC

SCALE: 3/8" = 1'-0"
DATE: 08/26/2025
DRAFTED BY: ES
REV:

PAGE:
A6