
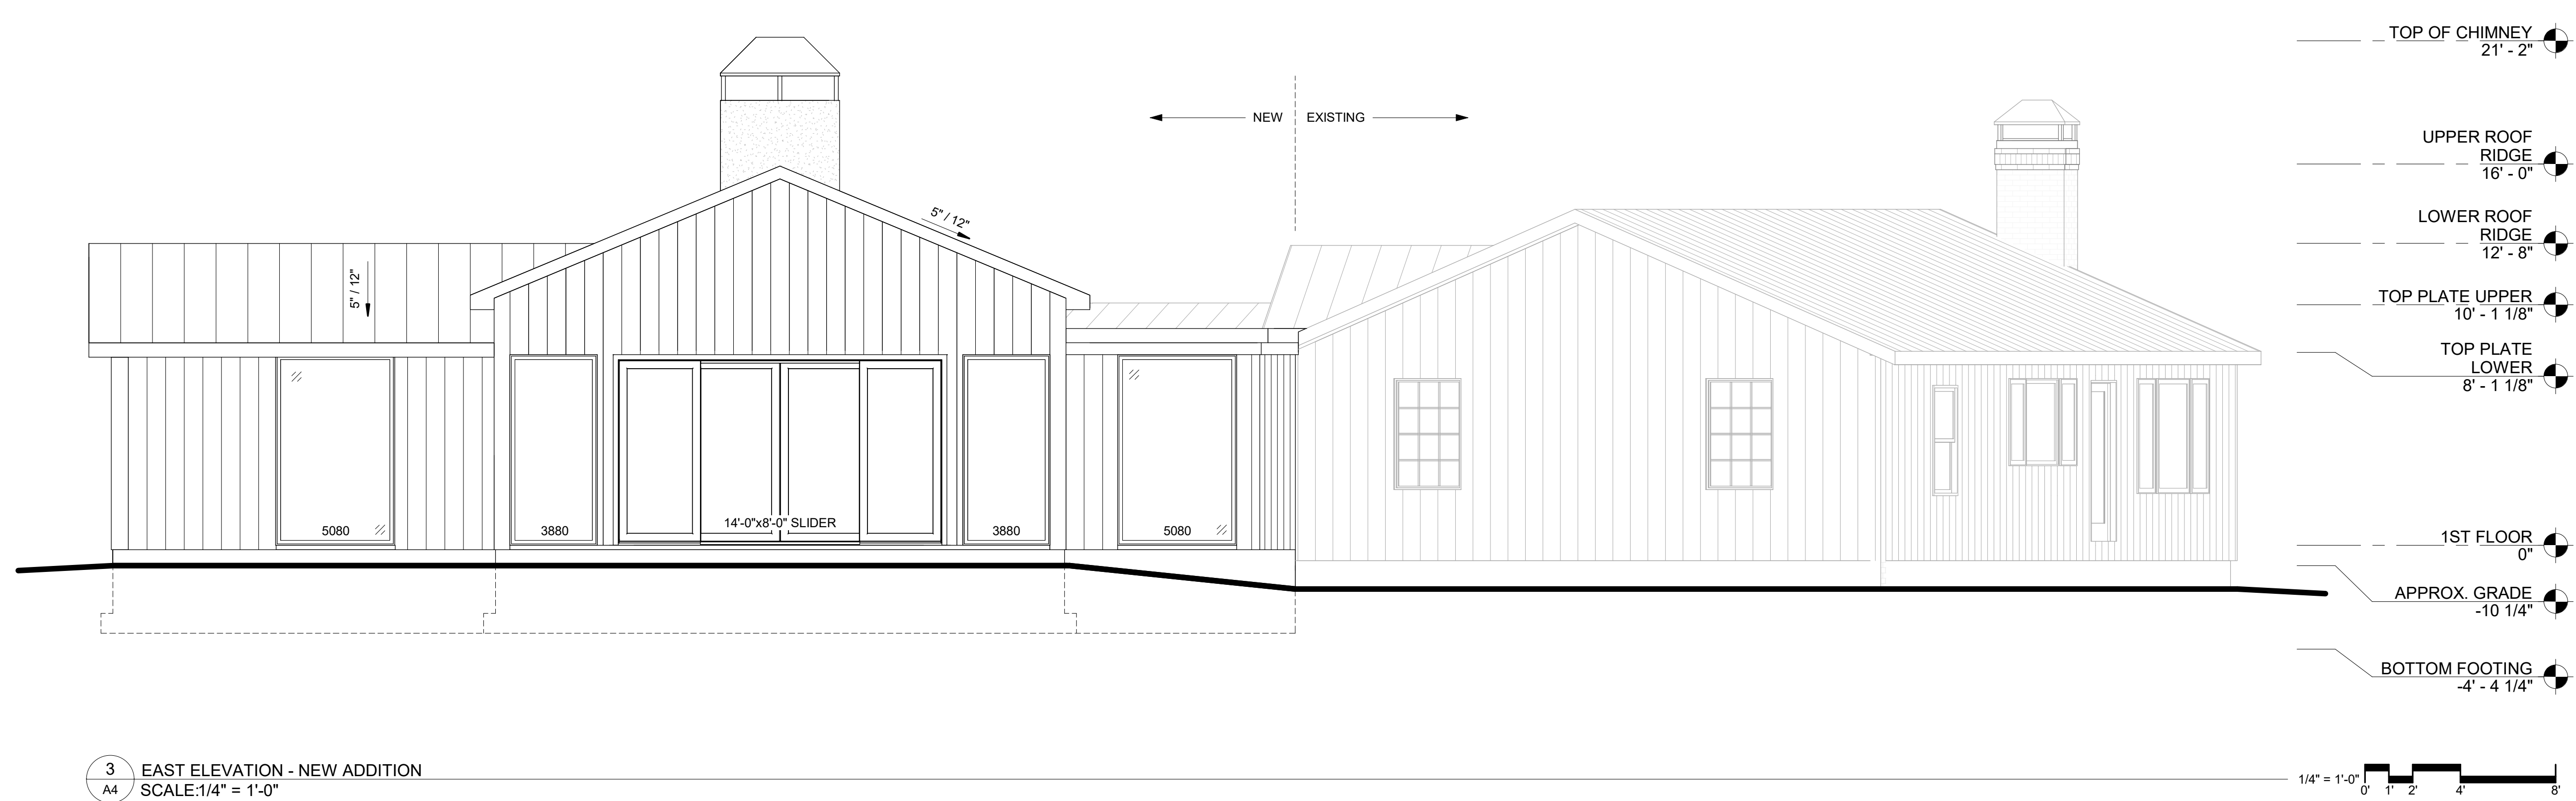
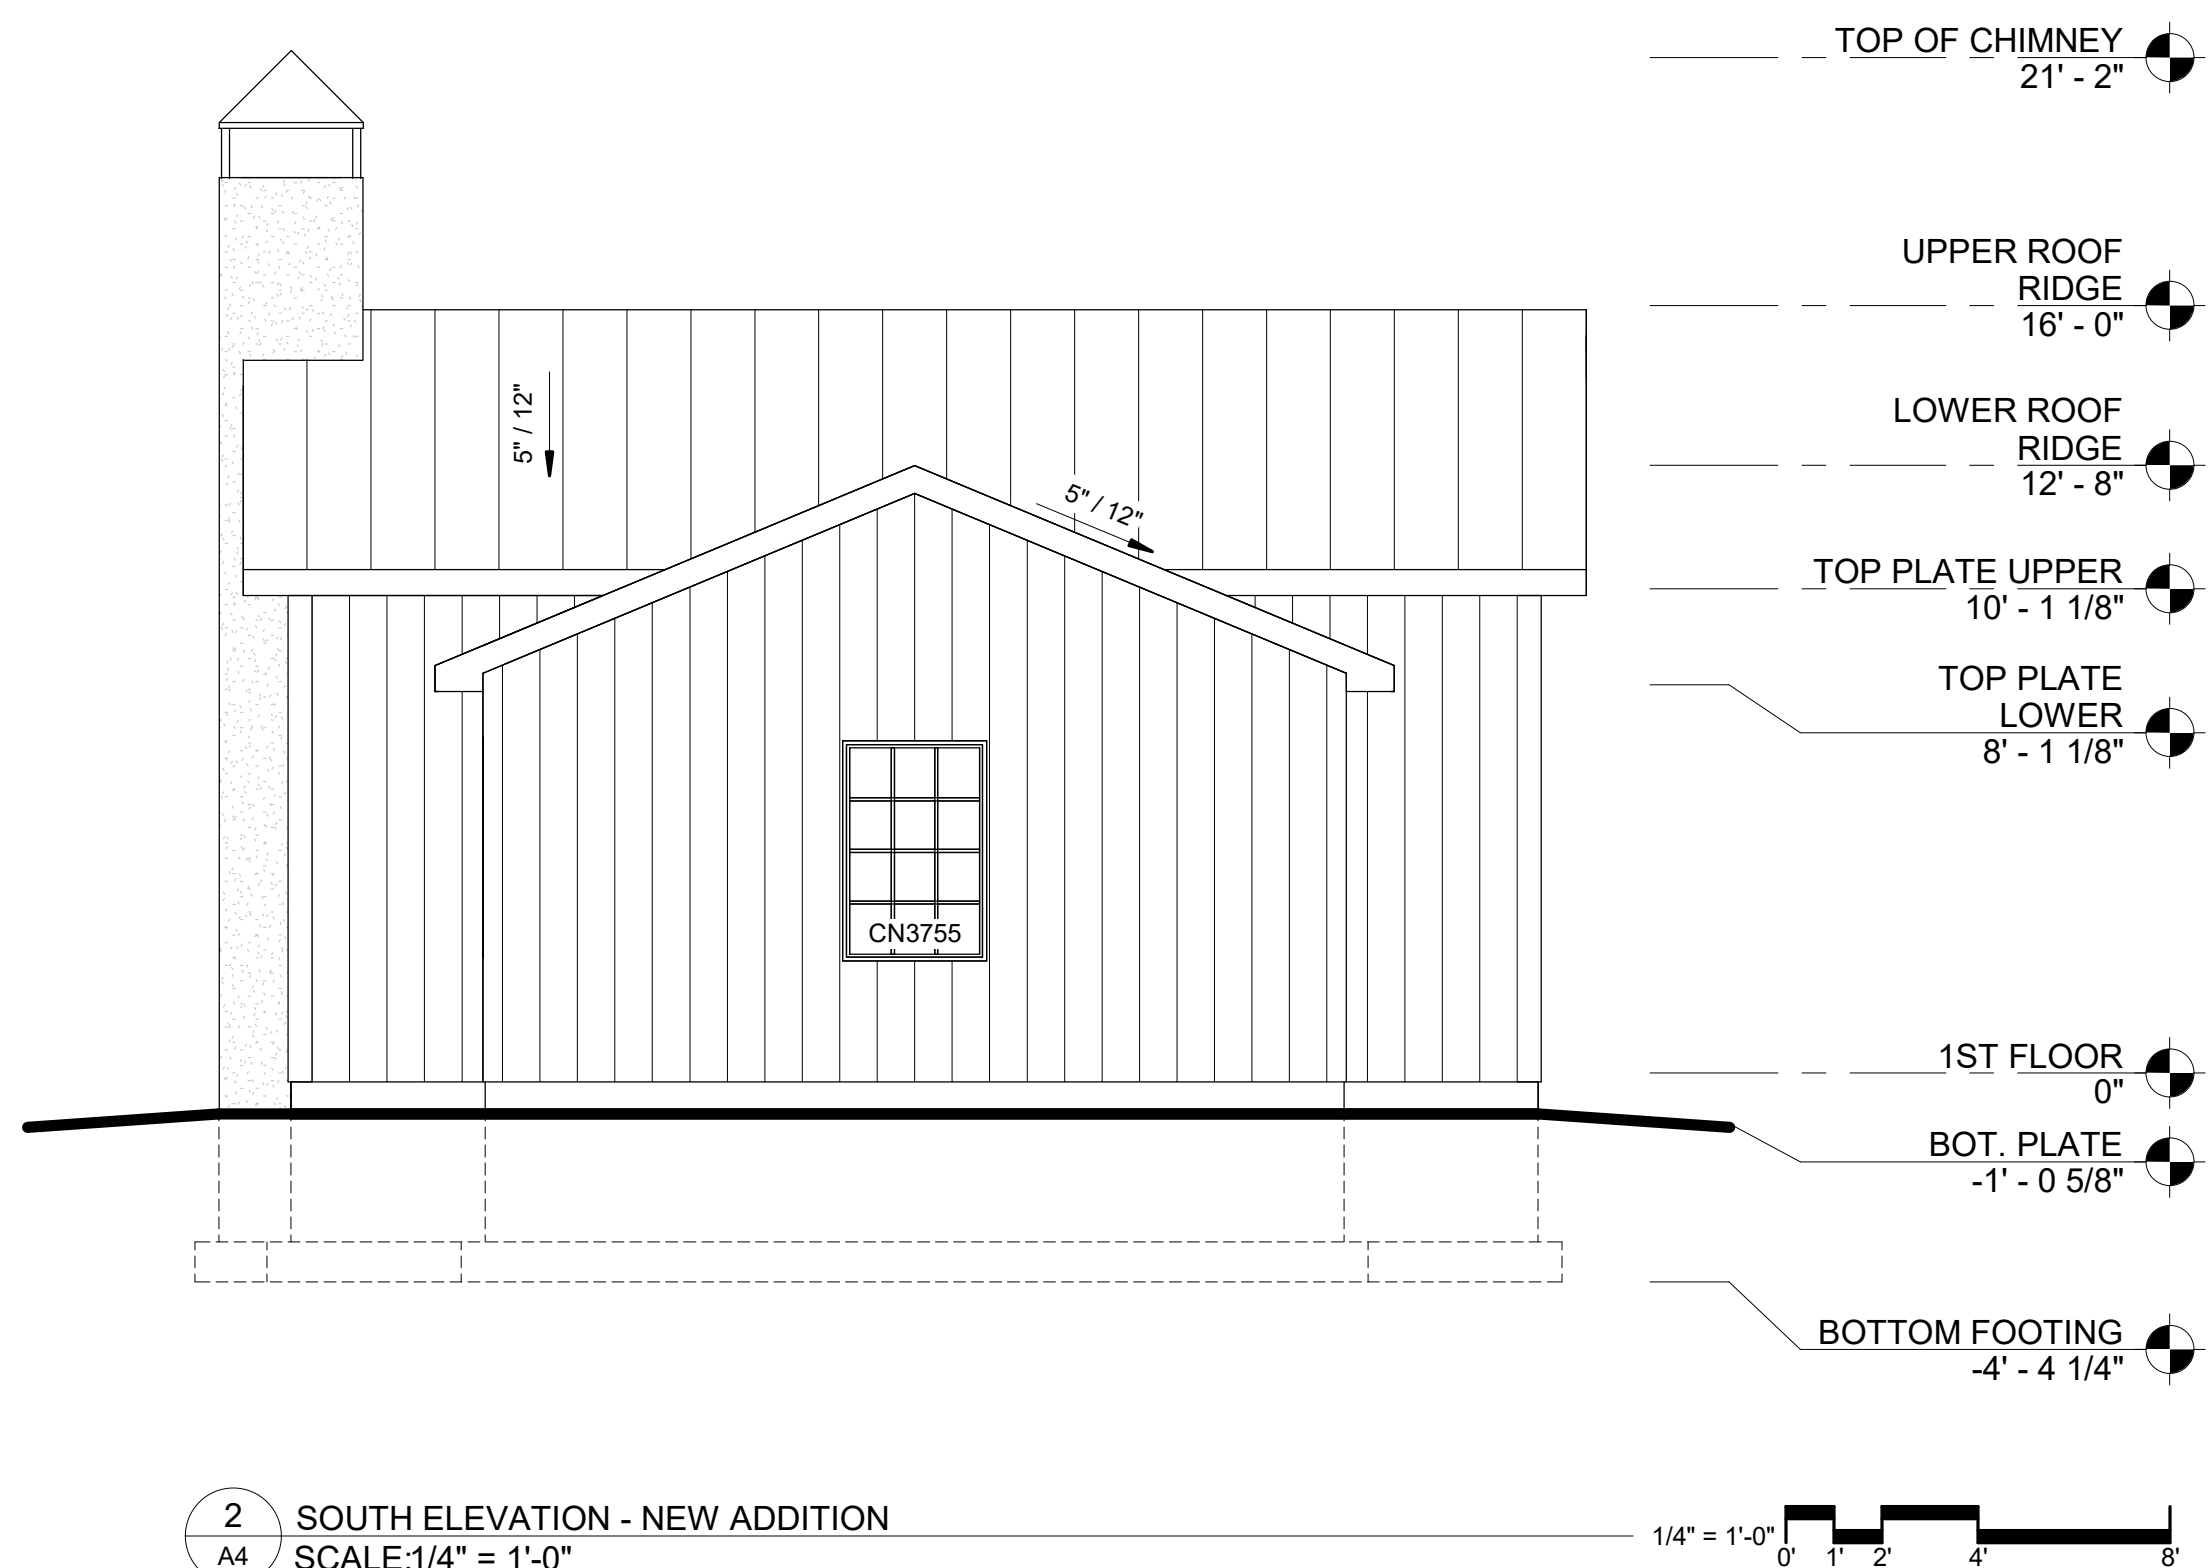


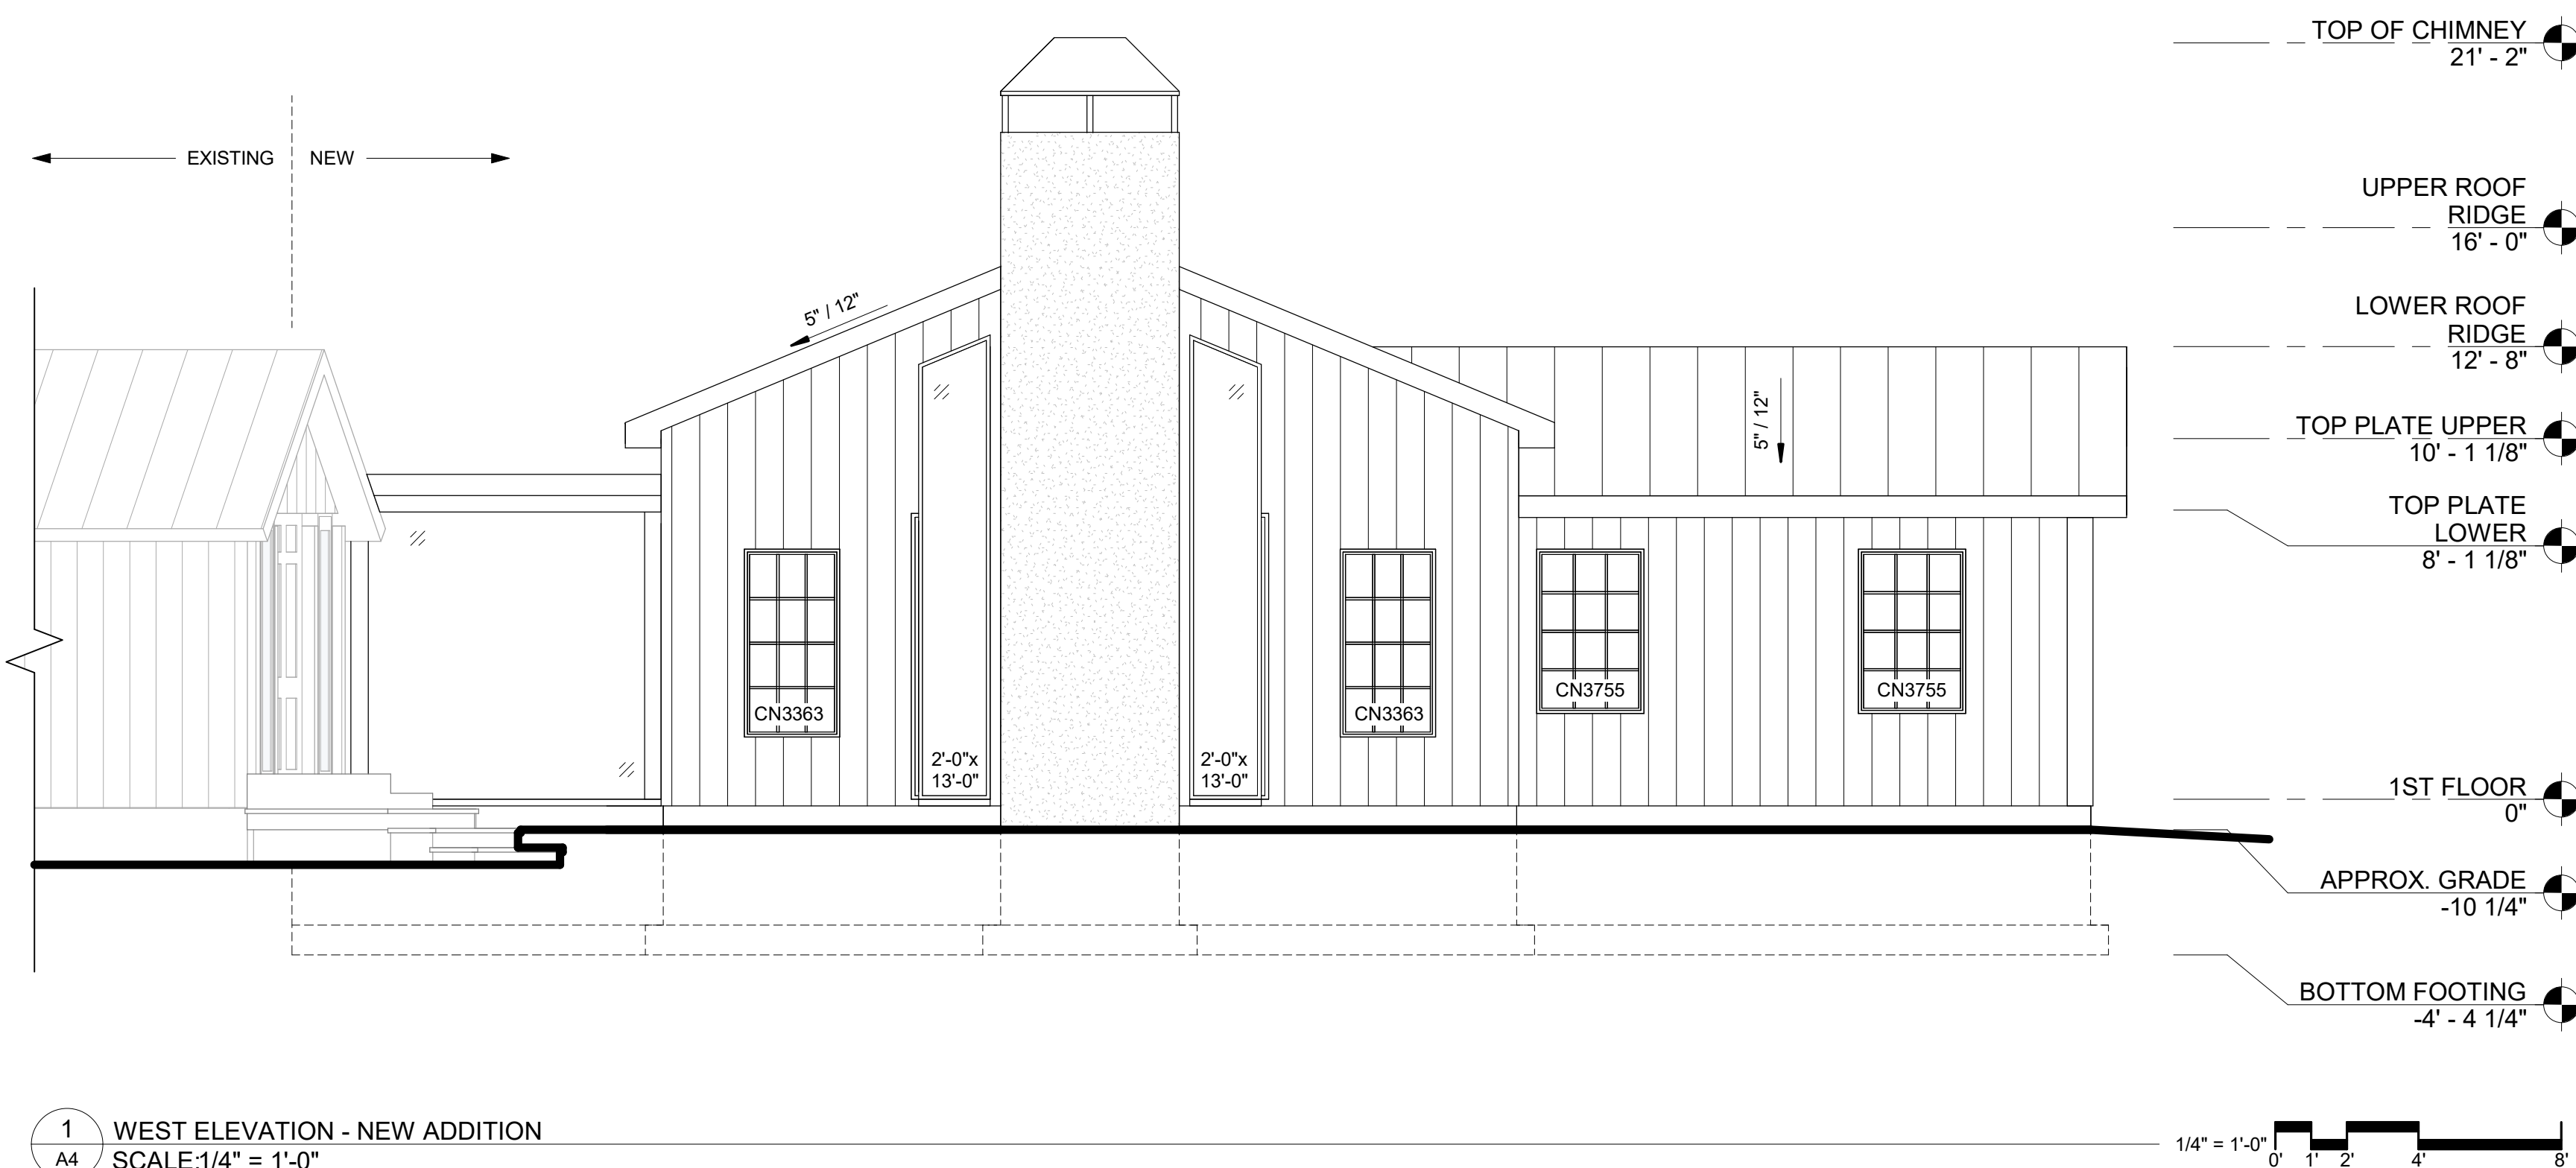

**kezlo group**  
PO Box 1086 844.495.3956  
Brookhaven, PA 19015 www.kezlo.com

THE INFORMATION CONTAINED HEREIN MAY NOT  
BE USED OR REPRODUCED WITHOUT THE  
WRITTEN PERMISSION OF KEZLO GROUP, LLC.

SEAL

CONSULTANTS:

| ISSUE | DATE | NUMBER |
|-------|------|--------|
|-------|------|--------|

CLIENT:

MARY-ANNE SCHOEB  
RICHARD SCHOEB

DATE: 02.28.2025

KEZLO GROUP PROJECT NUMBER: 24-083

PROJECT TITLE:

**STAGHILL  
COTTAGE -  
ADDITION**

SHEET TITLE:

**EXTERIOR  
ELEVATIONS,  
NOTES &  
DETAILS**

SHEET NUMBER:

**A4**