




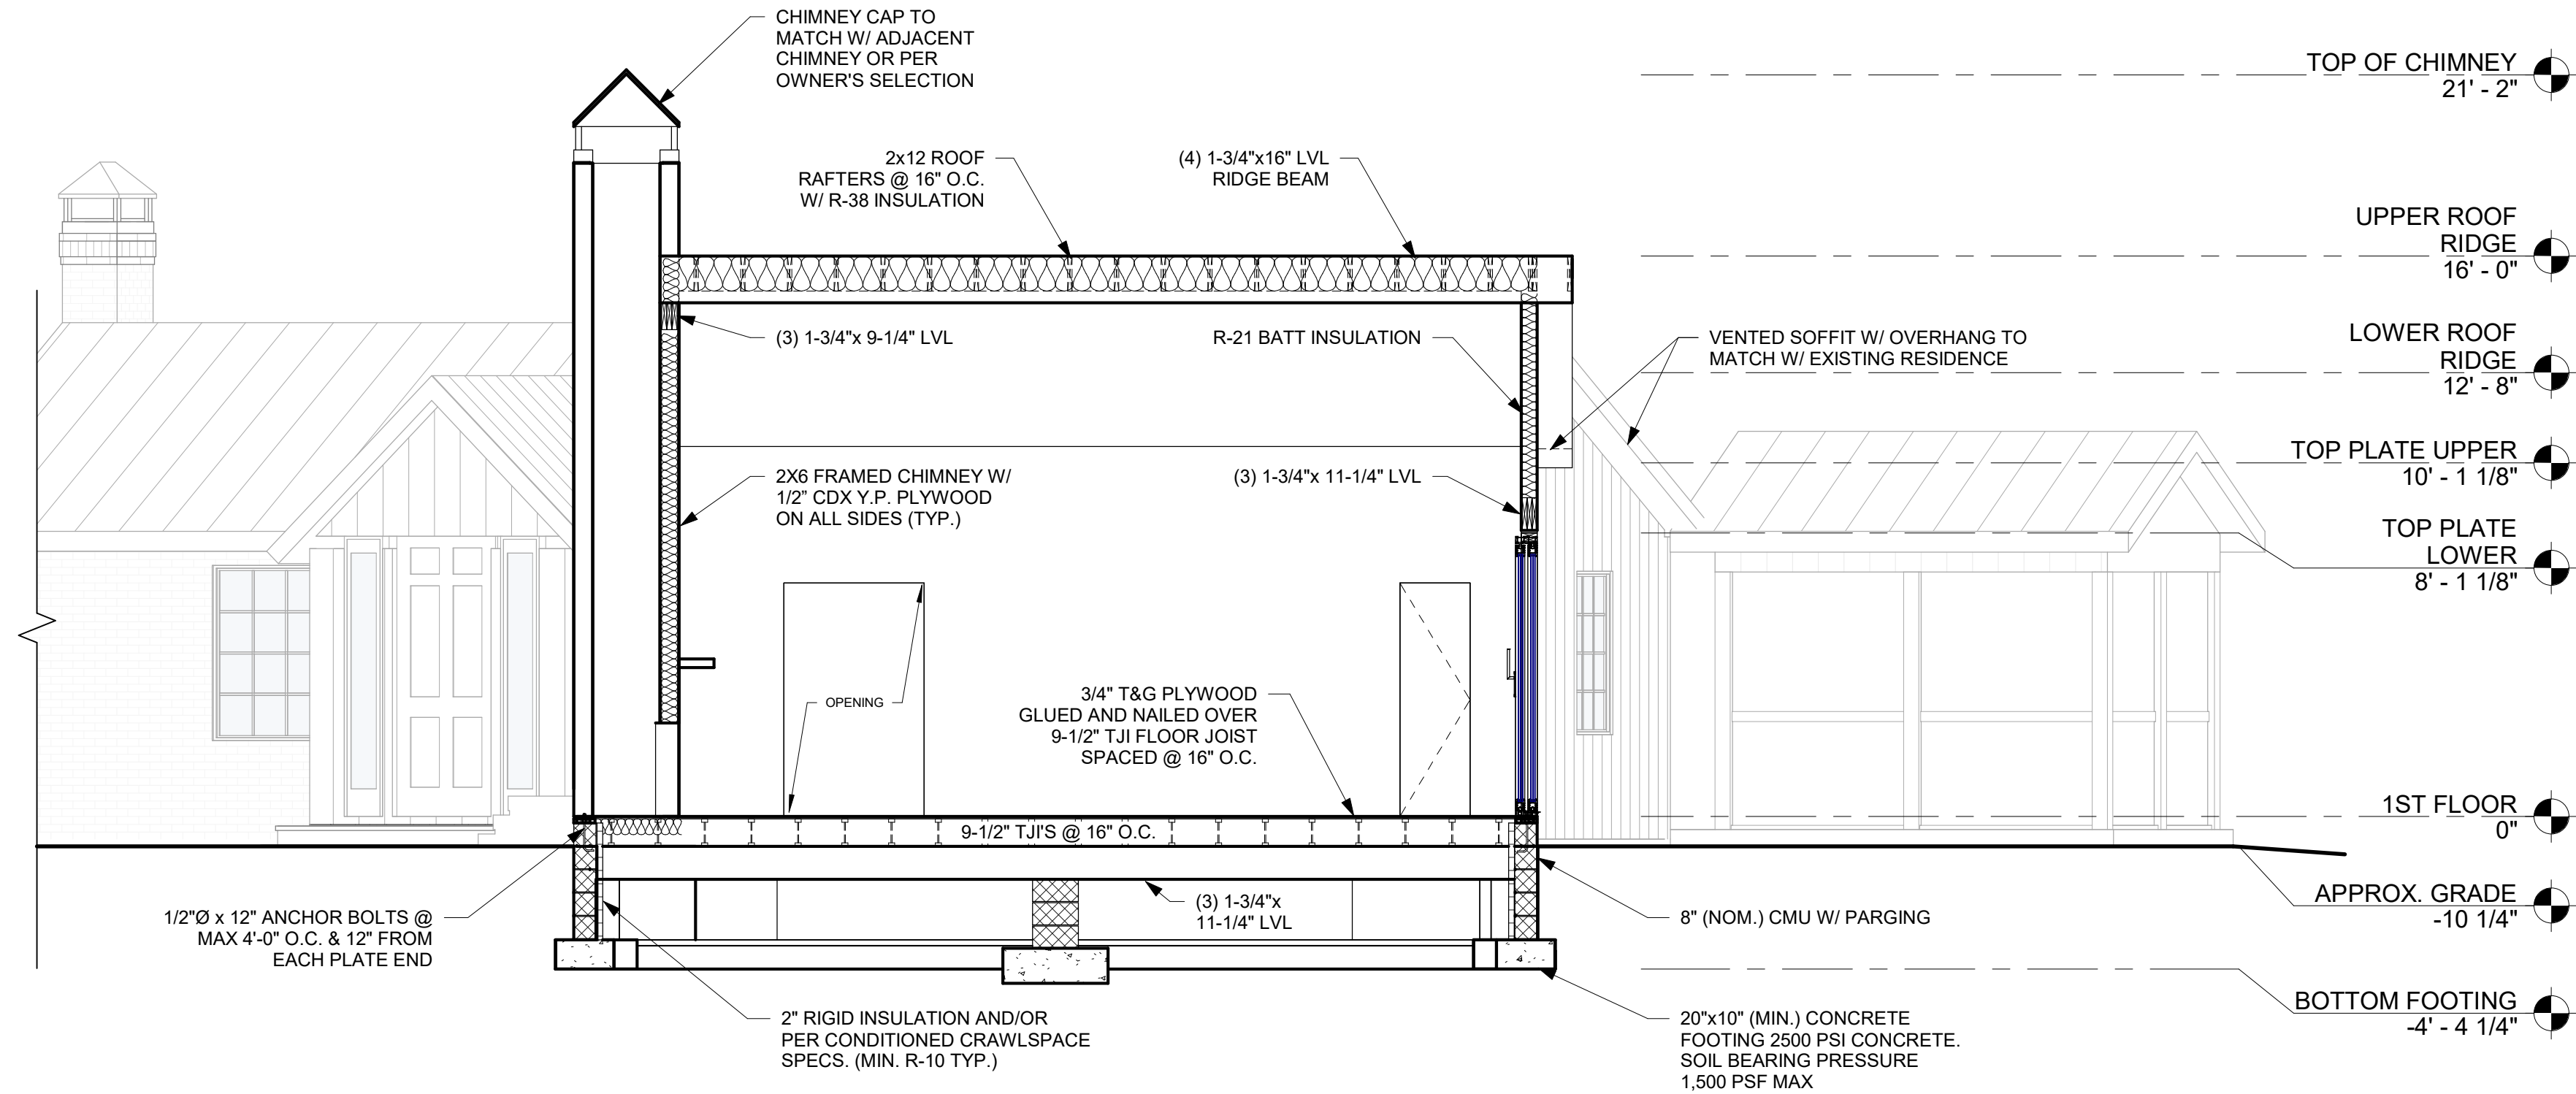

1 TRANVERSE SECTION @ GREAT ROOM ADDITION
A5 SCALE:1/4" = 1'-0"

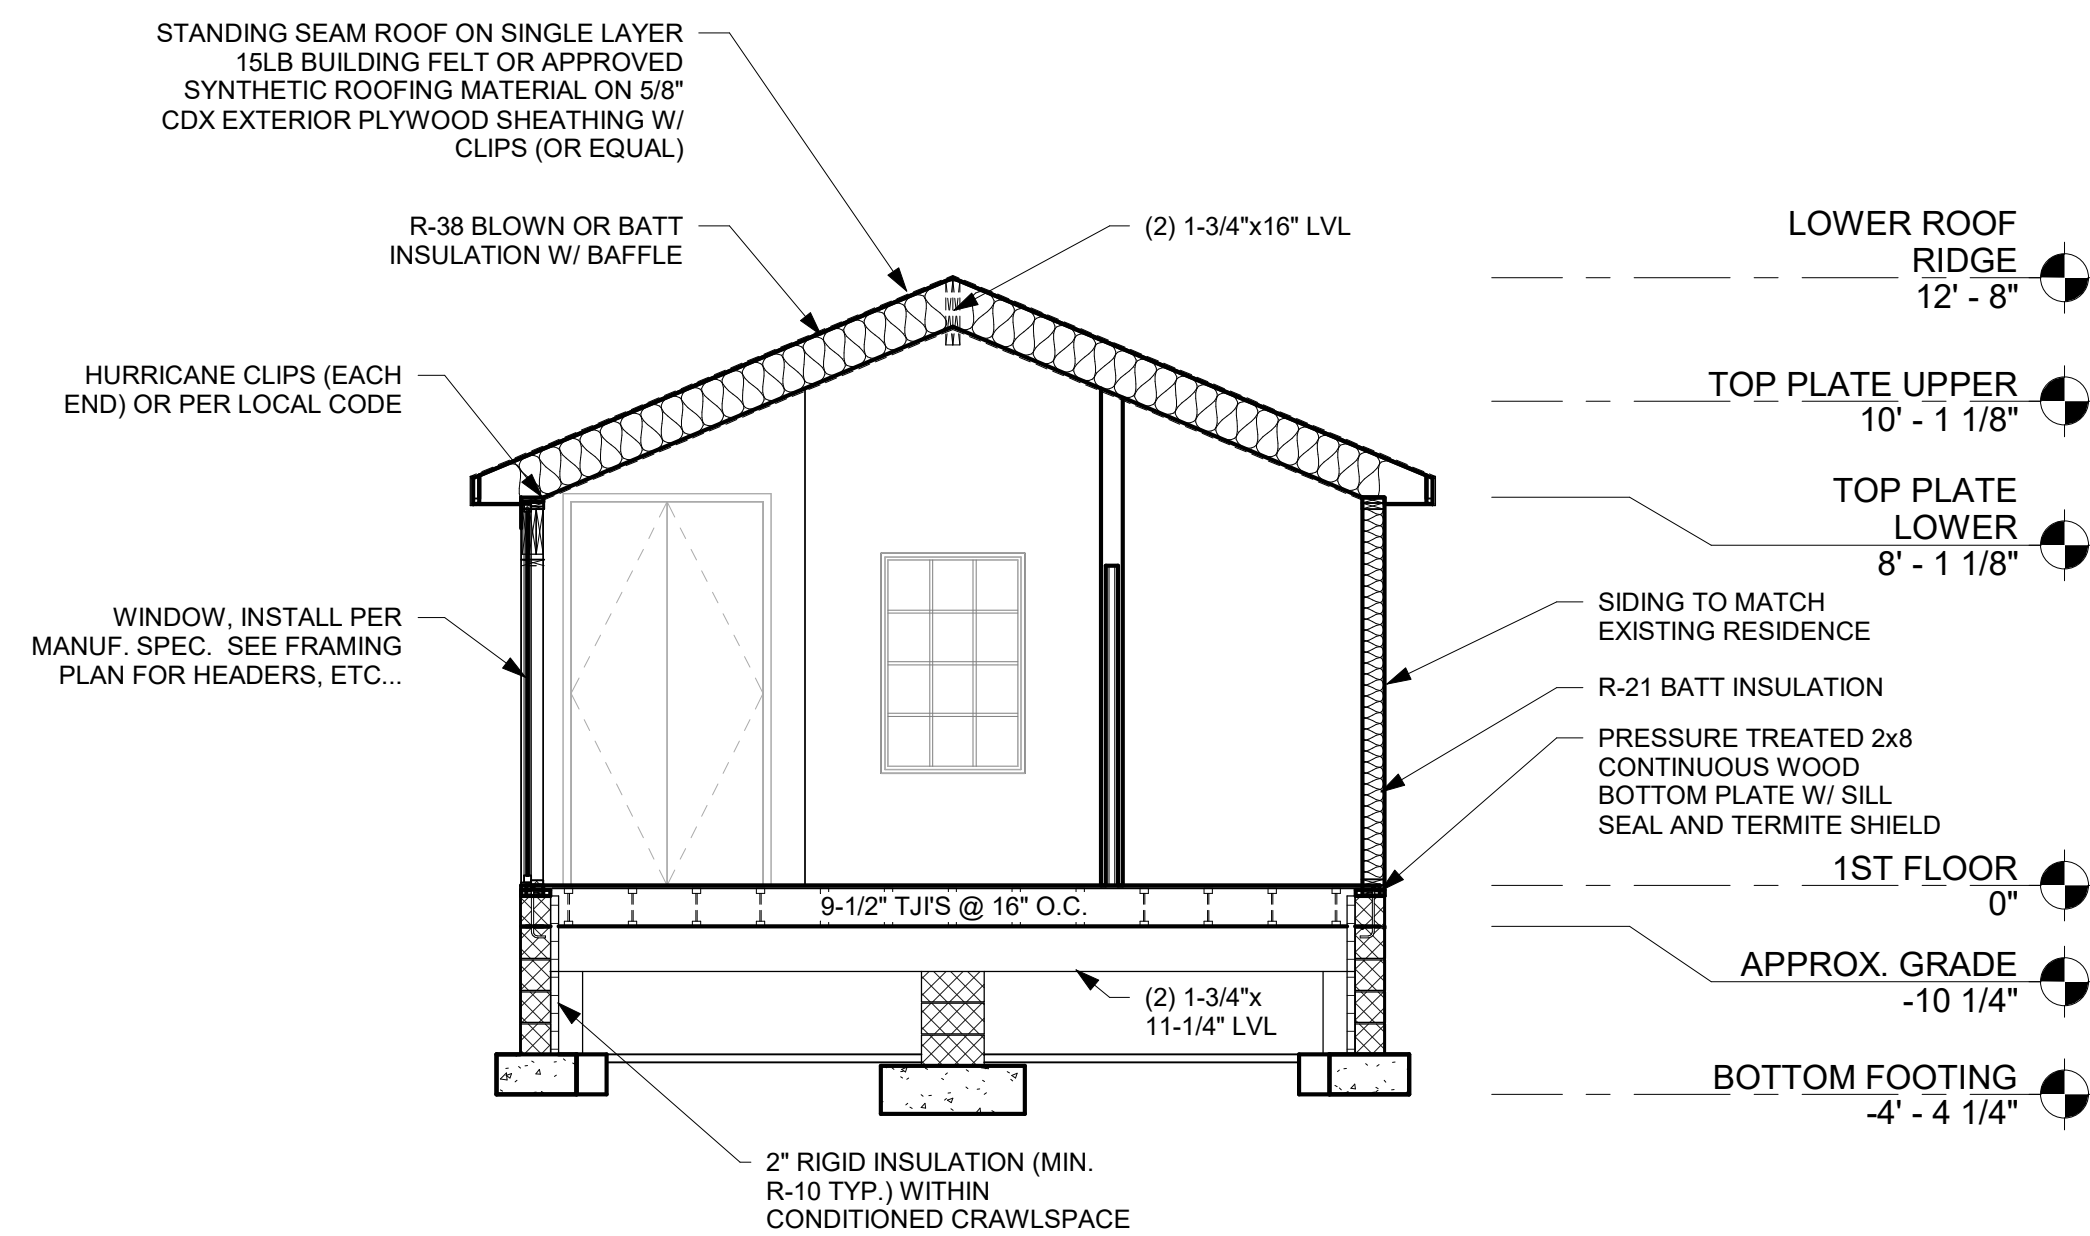

2 TRANVERSE SECTION @ BEDROOM ADDITION
A5 SCALE:1/4" = 1'-0"

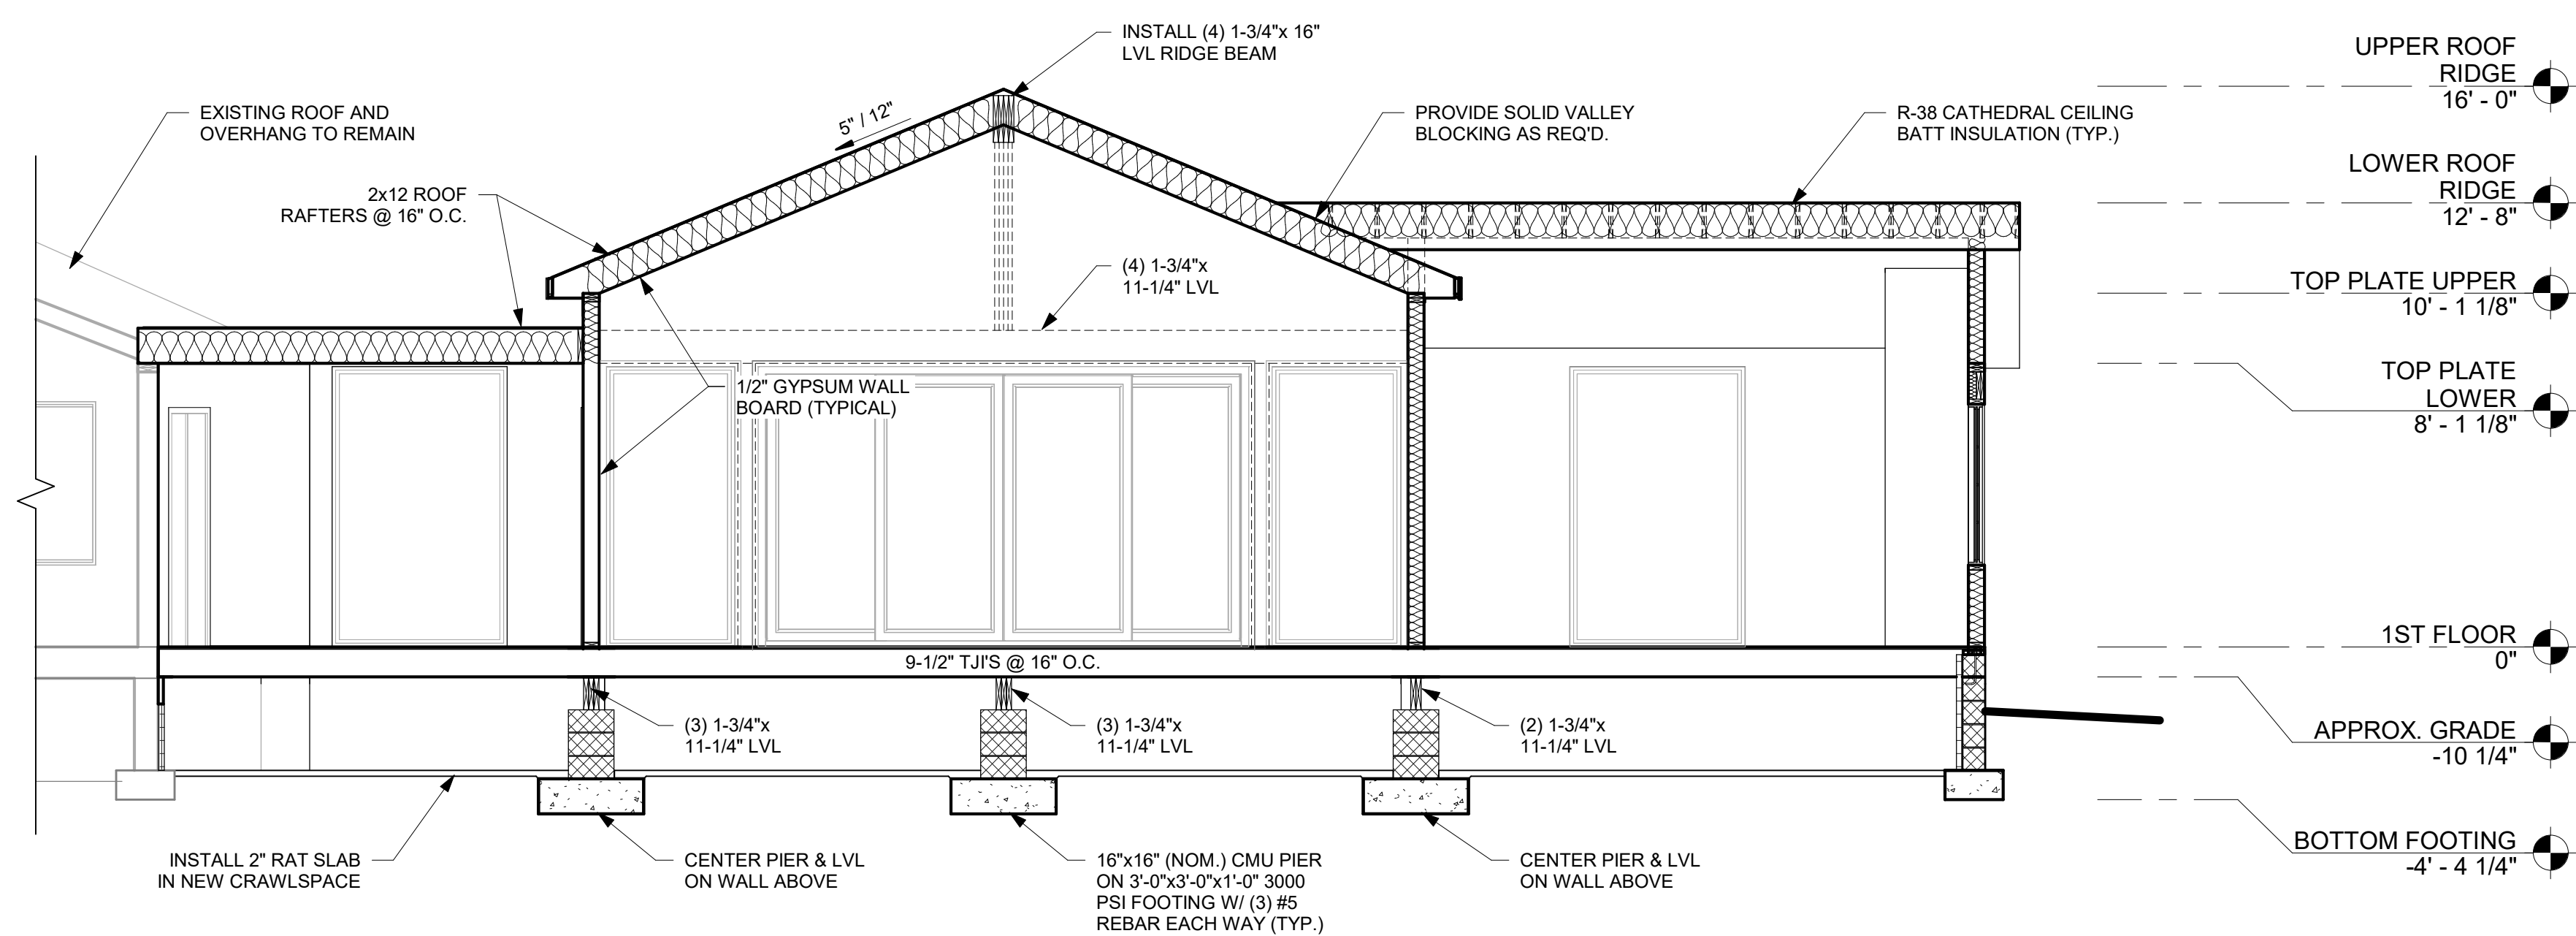

3 LONGITUDINAL SECTION @ ADDITION
A5 SCALE:1/4" = 1'-0"